

A

B

C


D

E

F


G

H

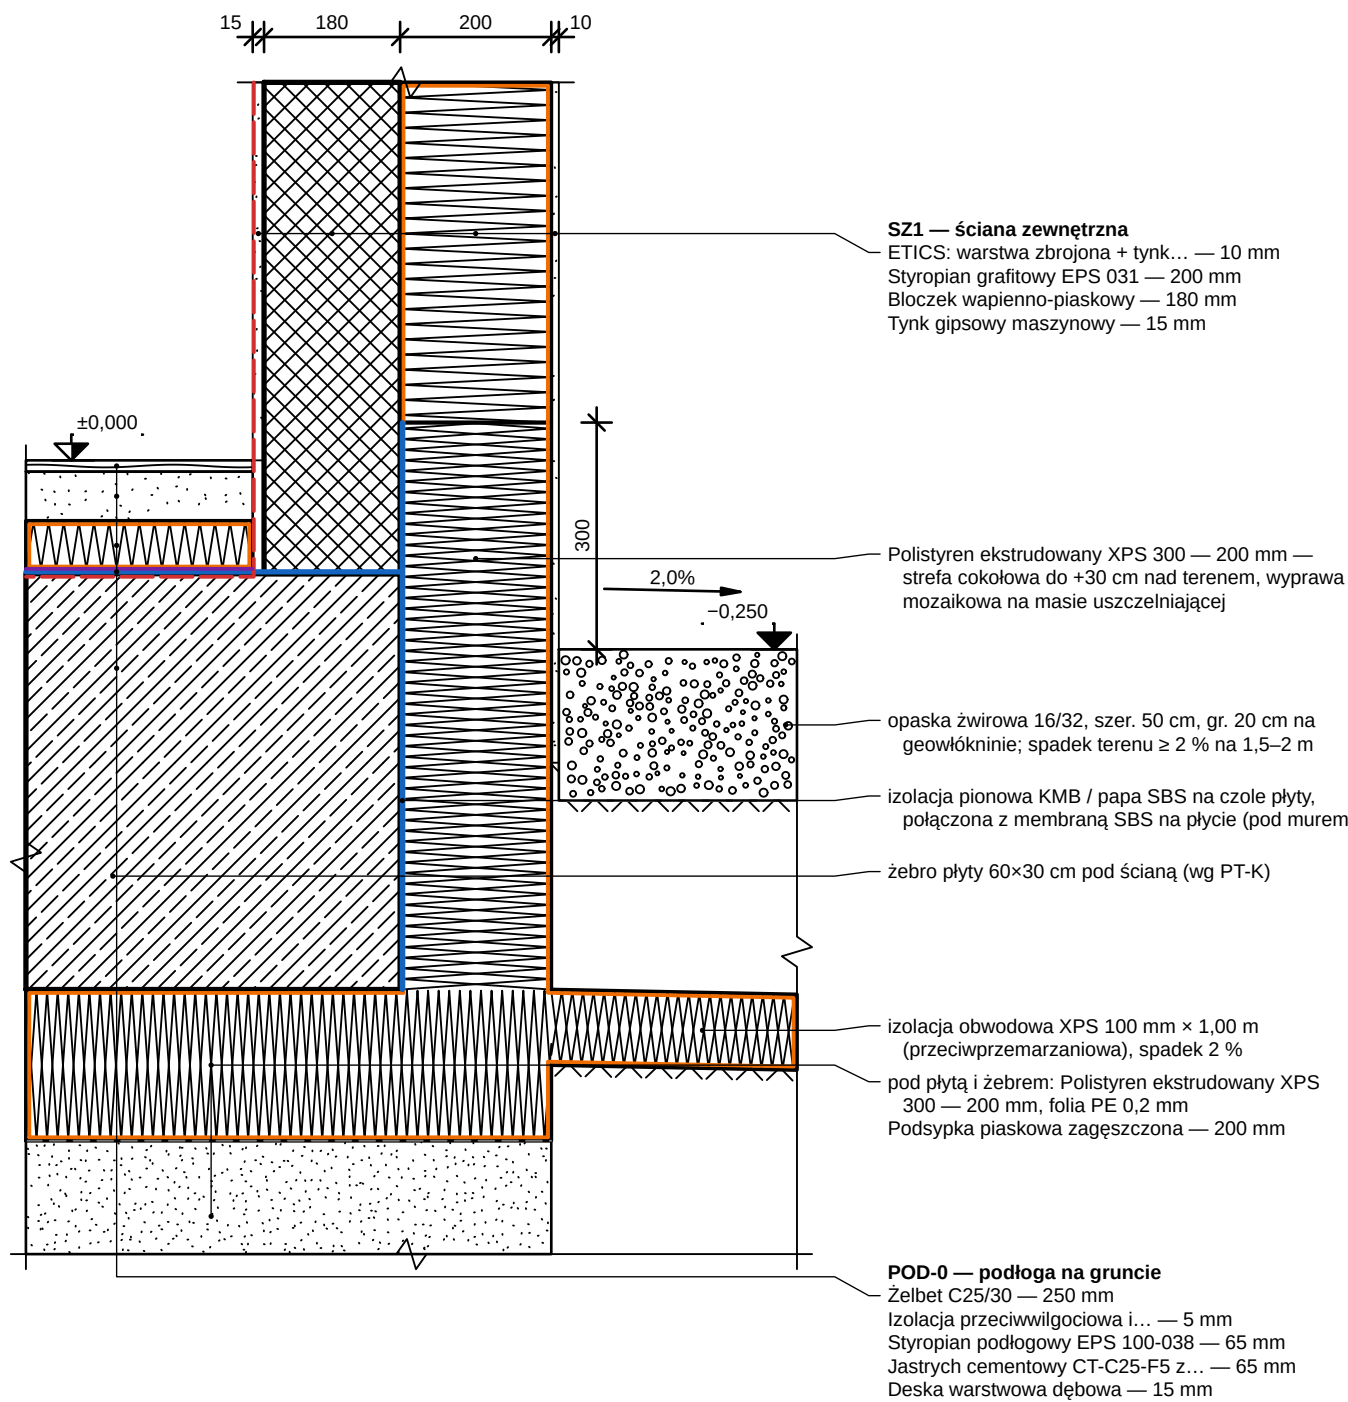


WZ-08: $\psi_e = 0,058$, $\psi_{oi} = 0,100$ W/(m·K); f, Rsi = 0,903 ± 0,72 — DOBRY
4 linie: H OK, S OK, P OK, I OK — ciągłość zachowana

DETAL D-01 — COKÓŁ — ŚCIANA NA PŁYCE FUNDAMENTOWEJ 1:10

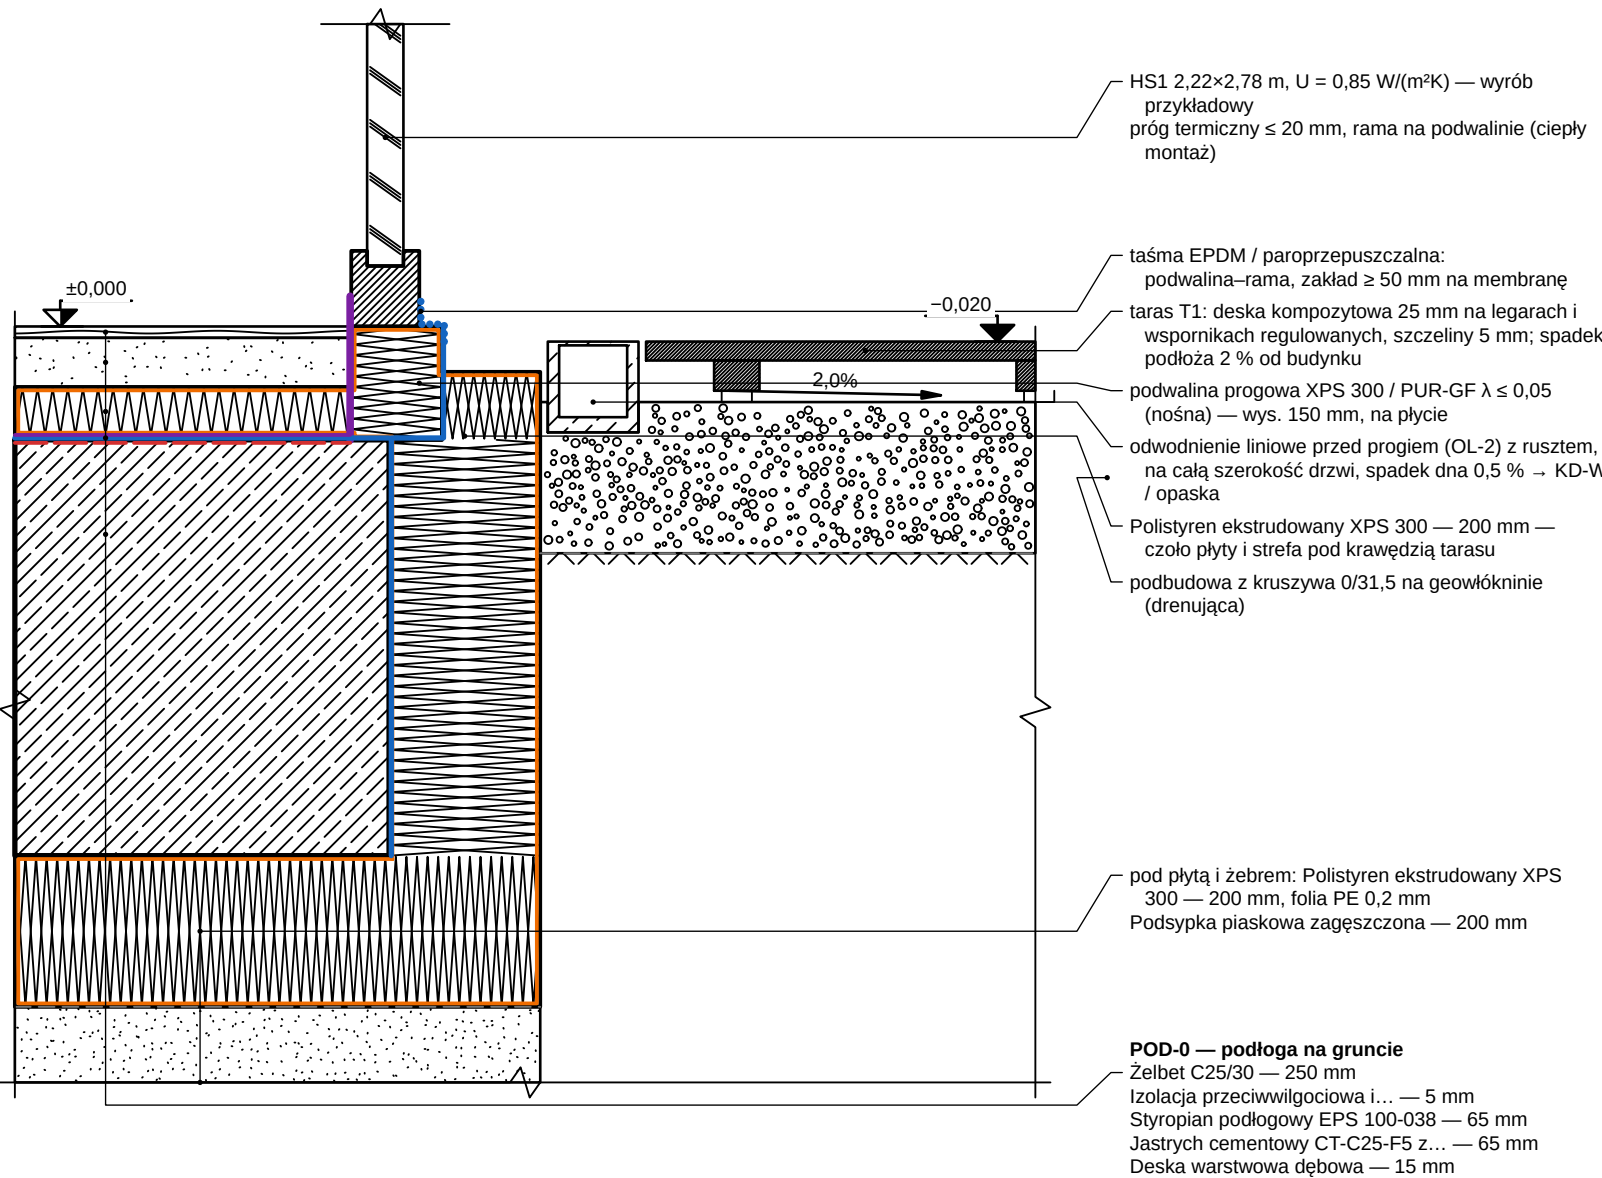

WZ-11T: $\psi_e = 0,076$, $\psi_{oi} = 0,118$ W/(m·K); f, Rsi = 0,845 ± 0,72 — DOBRY
4 linie: H OK, S OK, P OK, I OK — ciągłość zachowana

DETAL D-03 — PRÓG DRZWI HS BEZPROGOWY Z ODWODNIENIEM LINIOWYM 1:10

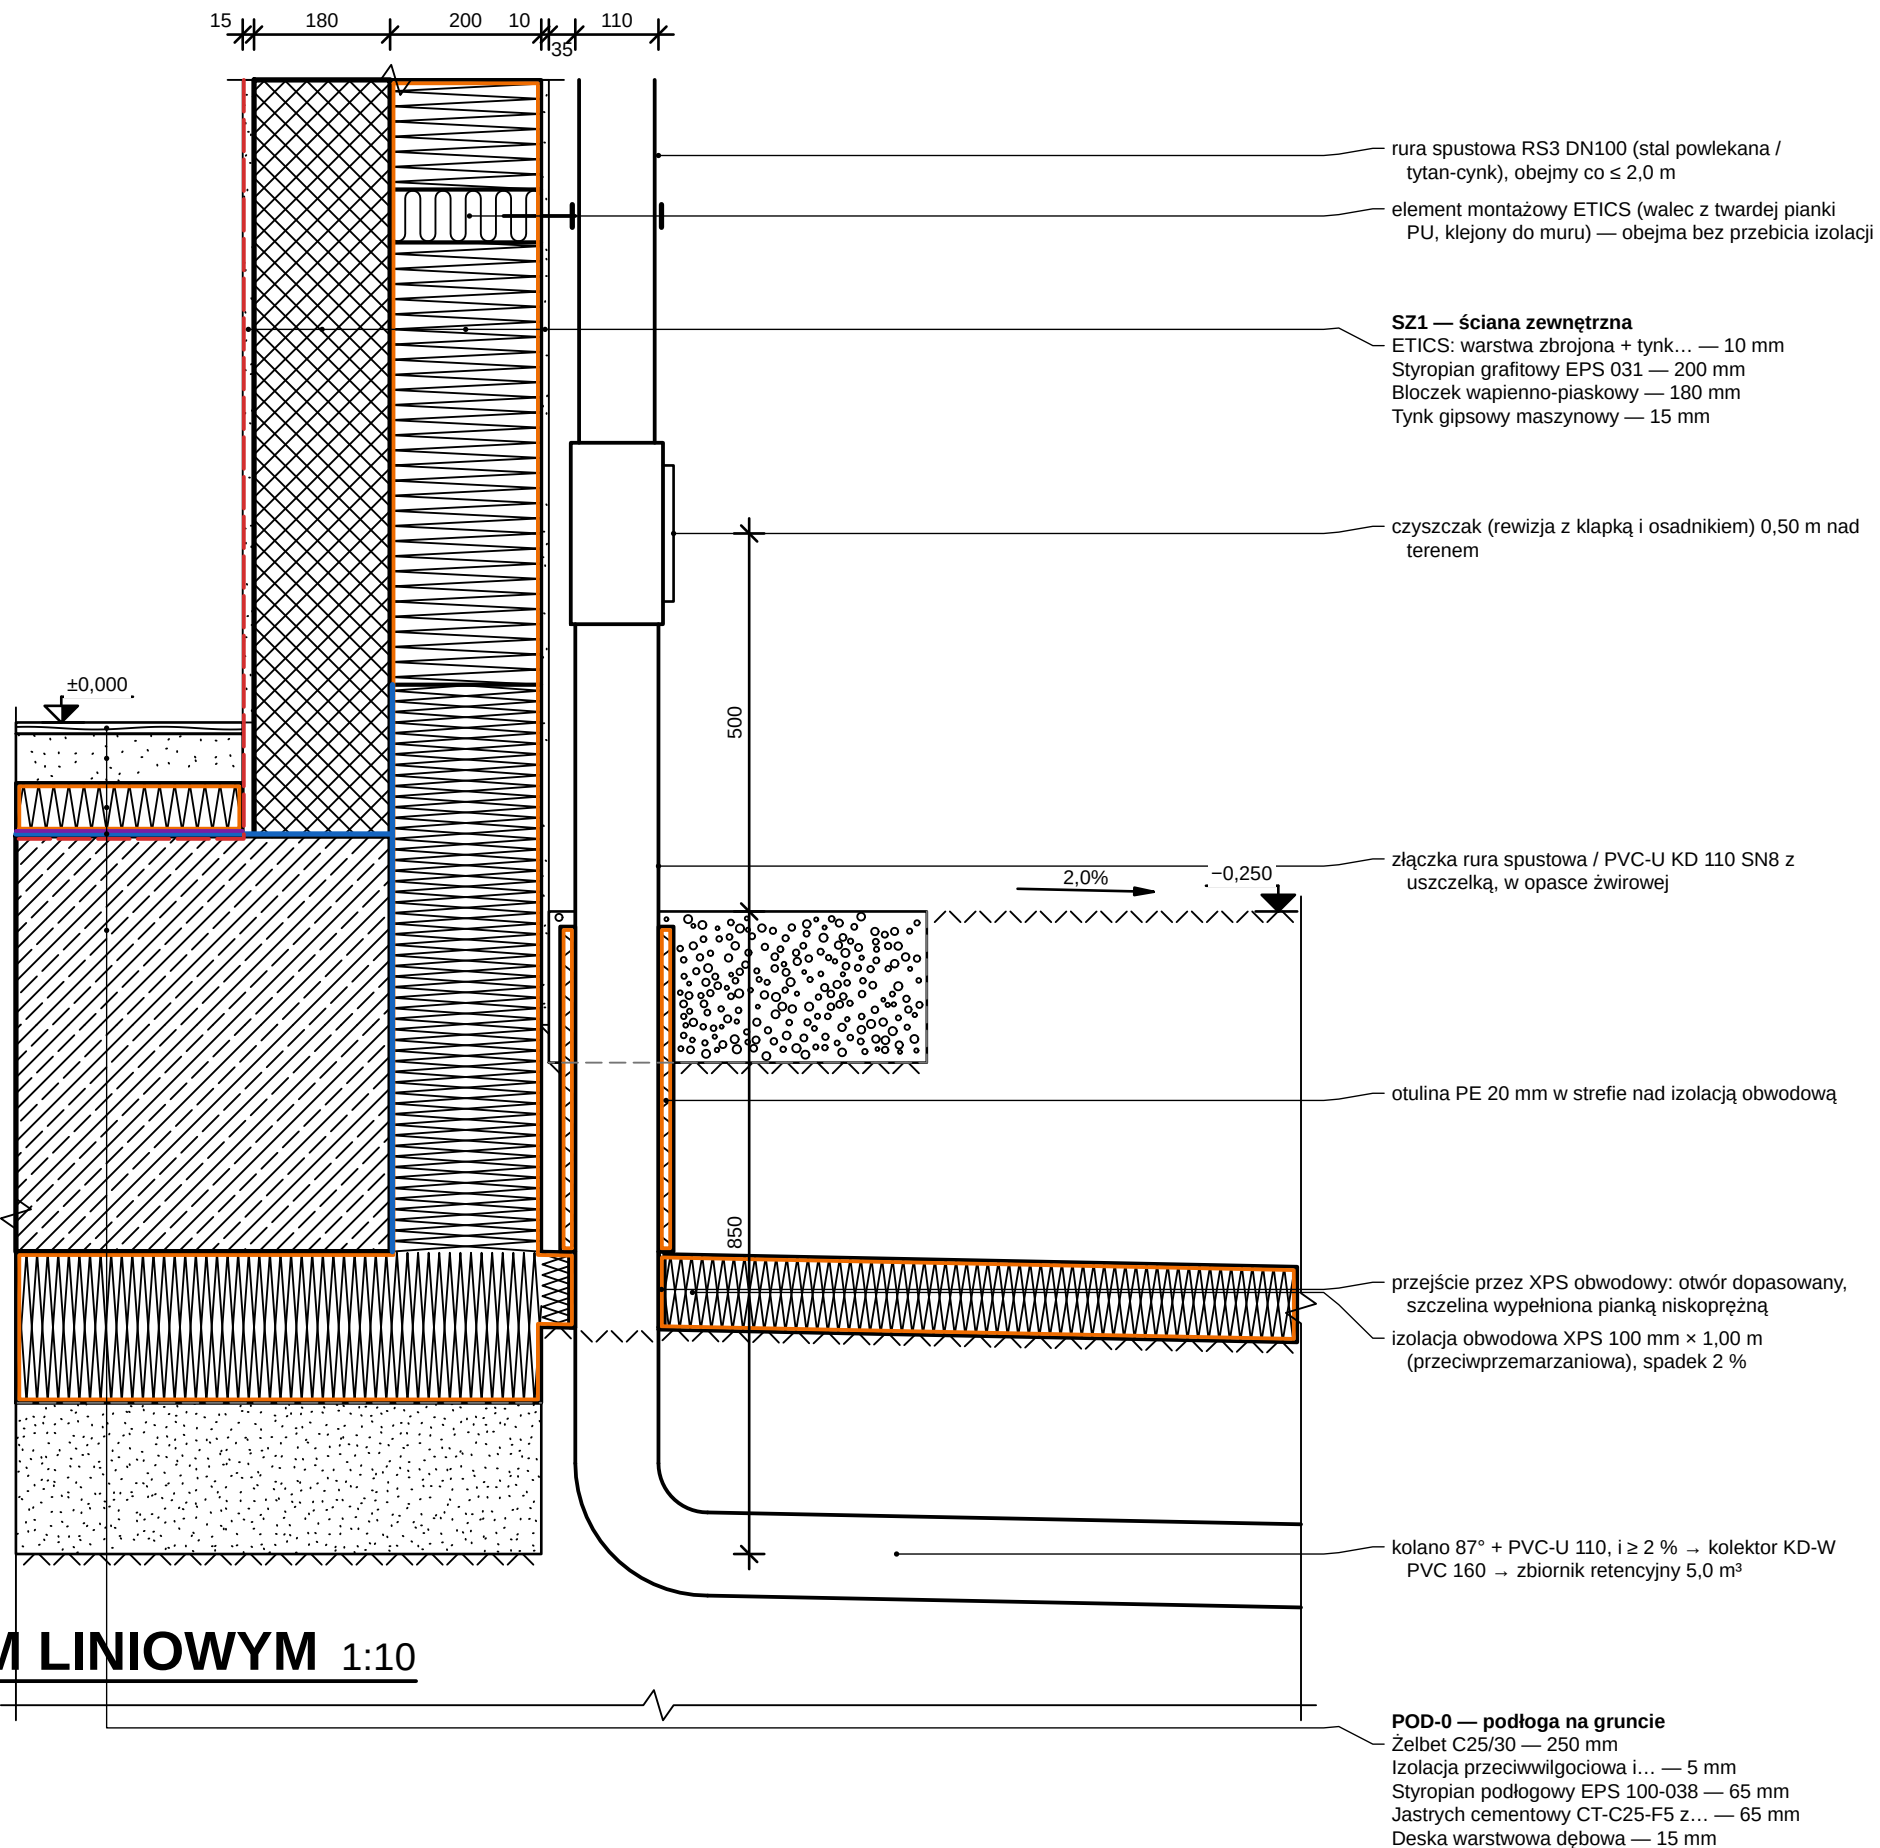

WZ-08: $\psi_e = 0,058$, $\psi_{oi} = 0,100$ W/(m·K); f, Rsi = 0,903 ± 0,72 — DOBRY
4 linie: H OK, S OK, P OK, I OK — ciągłość zachowana

DETAL D-07 — RURA SPUSTOWA RS3 PRZY COKOLE — CZYSZCZAK I ODPŁYW DO KD 1:10

OZNACZENIA MATERIAŁÓW (PN-B-01030 + przyjęte)

	Odwodnienie liniowe — korytko z polimerobetonu z rusztem (klasa A15/B125) — 45° przerywane		Podsyпка piaskowa zagęszczona (l, s ≥ 0,98)
	Deska warstwowa dębowa 15 mm, klejona — przekrój wzdłuż włókien		Solarka — profile aluminiowe, antracyt — zaczernienie
	grunt rodzimy		Pakiet szybowy 3-szybowy (ciepła ramka)
	Opulina izolacyjna 20 mm (kauczuk / PE), akustyczna; Pianka PUR niskopropna (wypełnienie szczeliny) — meander, UUU		Deska tarasowa kompozytowa 25 mm na legarach; Legar aluminiowy / kompozytowy na wspornikach regulowanych
	Styropian grafitowy EPS 031 (ETICS, NRO w systemie); Styropian podłogowy EPS 100-038 (pod jastychem) — zygzak „VVV”		Tynk gipsowy maszynowy 1,5 cm; ETICS: warstwa zbrojona + tynk silikonowy 1,5 mm (biały / jasnoszary NCS S 1500-N) — kropki nieregularne
	Polistyren ekstrudowany XPS 300 (pod płytą fundamentową, cokół, izolacja obwodowa); Podwalnia progowa / profil nosiny z XPS 300 lub PUR-GF, λ ≤ 0,05 — zygzak podwójny		Zelbet C25/30, B500SP (stropy, płyta fundamentowa, ściany) — 45° na przemienną cięgieł przerywane
	Jastyż cementowy CT-C25-F5 z wężownicą ogrzewania podłogowego — kropki		Zwir plukany 16/32 mm (balast dachu P1, opaska przy alicy); Podbudowa z kruszywa łamanego 0/31,5 zagęszczona
	Błoczek wapienno-piaskowy (silikat) 18 cm, kl. 20, gr. 1, na zaprawie cienkowarstwowej — kratka ukośna 45°/135°		

ZASADA „4 LINII” I OZNACZENIA DETALI

- hydroizolacja / izolacja przeciwwodna i przeciwwilgociowa (ochrona przed wodą)
- warstwa szczelności powietrznej (tynk wewn., płyta ZB, OSB, membrana, taśmy)
- paroizolacja / kontrola pary (folia, papa z Al, membrana sd ≥ 10 m)
- izolacja cieplna — obrys ciągłej warstwy izolacji (test „dławką”)
- taśma paroszczelna (od wewnątrz — ciepły montaż)
- taśma paroprzepuszczalna / uszczelnienie zewnętrzne (ciepły montaż, próg)
- membrana wiatroizolacyjna paroprzepuszczalna
- geowłóknina, bariera przeciwwodna, mata drenażowa
- obróbka blacharska z okapniem (kapinosem), rynna ukryta

WYNIKI MOSTKÓW (PN-EN ISO 10211) I OCENA 4 LINII


D-01: WZ-08: $\psi_e = 0,058$, $\psi_{oi} = 0,100$ W/(m·K); f, Rsi = 0,903 ± 0,72 — DOBRY
4 linie: H OK, S OK, P OK, I OK — ciągłość zachowana

D-03: WZ-11T: $\psi_e = 0,076$, $\psi_{oi} = 0,118$ W/(m·K); f, Rsi = 0,845 ± 0,72 — DOBRY
4 linie: H OK, S OK, P OK, I OK — ciągłość zachowana

D-07: WZ-08: $\psi_e = 0,058$, $\psi_{oi} = 0,100$ W/(m·K); f, Rsi = 0,903 ± 0,72 — DOBRY
4 linie: H OK, S OK, P OK, I OK — ciągłość zachowana

OBJAŚNIENIA I UWAGI

- Wymiary w mm, rzędne w m względem ±0,000 = 101,650 m n.p.m. (PL-EVRF2007-NH).
- Kreskowania materiałów wg PN-B-01030:2000 (aktualna) i PN-EN ISO 128-3:2023-02 (zastąpiła wycofane PN-ISO 128-50:2006); oznaczenia spoza normy — w legendzie arkusza.
- Opisy warstw od zewnątrz do wewnątrz (kolejność kropek na linii odnośnika = kolejność wierszy), grubości w mm wg przegrod modelu (kontrola zgodności — raport modułu detali).
- Zasada „4 linii” (brief 99.1): hydroizolacja — niebieska, szczelność powietrzna — czerwona przerywana, paroizolacja — fioletowa, izolacja cieplna — obrys pomarańczowy; każda linia ciągła wokół kubatury ogrzewanej.
- Wyniesienia hydroizolacji ≥ 15 cm ponad warstwę wierzchnią (zwir, substrat, nawierzchnia) — Wytyczne DAFA dla dachów płaskich; DIN 18531 (pomocniczo); PN-EN 1991 wysokości wyniesień nie określa. Cokół uszczelnienie ≥ 30 cm nad terenem (brief 99.4; DIN 18533-1 — pomocniczo) albo odwodnienie liniowe przy drzwiach bezprogowych.
- Wyroby (łączniki termoizolacyjne, taśmy, profile progowe, wpusty, konsole) — dane przykładowe „lub równoważne”; parametry (ETA/DWU) do potwierdzenia przed realizacją.
- Detal D-01: drenażu opaskowego nie projektuje się — decyzja w modelu działki (DR-0, W-285); płaski średnie, ZWG = 3,8 m p.p.t. (uzasadnienie: REKOMENDACJE mostków, rozdz. C).
- Detal D-01: zebro płyty licowane z czołem płyty (lico konstrukcji muru — audyt A2 K-1); w modelu zebro osiowe 0,60 m — do ujednolicenia w PT-K.
- Detal D-03: próg bezbarierowy; wyniesienie hydroizolacji 15 cm ponad płytę (pod próg), przed drzwiami odwodnienie liniowe na całą szerokość — DIN 18531-5 / wytyczne DAFA (redukcja wysokości progu przy zapewnionym odpływie); spadek podłoża tarasu 2 % od budynku.
- Detal D-07: drenażu opaskowego nie projektuje się — decyzja w modelu działki (DR-0, W-285); płaski średnie, ZWG = 3,8 m p.p.t. (uzasadnienie: REKOMENDACJE mostków, rozdz. C).
- Detal D-07: zebro płyty licowane z czołem płyty (lico konstrukcji muru — audyt A2 K-1); w modelu zebro osiowe 0,60 m — do ujednolicenia w PT-K.
- Detal D-07: RS3: zewnętrzna na elewacji pn., czyszczak 0,5 m nad terenem, kolektor KD-W, odpływ do zbiornika — sieć KD wg PZT / PT-IS (zagłębienie ≥ h, z 0,8 m lub w strefie izolacji obwodowej).
- Rysunek wygenerowany automatycznie z modelu modelbudynk.yam1 (wersja 1.0, 2026-09-25) — generatory lamela.wiews.

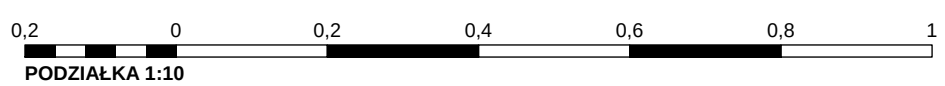

REW.	OPIS ZMIANY	DATA
0	Wydanie — rysunek wygenerowany z modelu	2026-09-25
PRACOWNIA PROJEKTOWA	STADIUM	BRANŻA
PRACOWNIA PROJEKTOWA — nazwa do uzupełnienia	PT	ARCHITEKTURA (AR)
adres pracowni do uzupełnienia		
INWESTOR		
(do uzupełnienia)		
OBIEKT / NAZWA ZAMIERZENIA BUDOWLANEGO		
Budynek mieszkalny jednorodzinny wolnostojący „Dom LAMELA”		
ADRES / LOKALIZACJA (NR DZIAŁKI, OBRĘB, JEDN. EWIDENCYJNA)		KAT. OBIEKTU
ul. Lipowa (fikcyjna), dz. nr ewid. 123/4, obręb 0005 Przykładowo, gm. Przykładowo (fikcyjna)		I
FUNKCJA	IMIĘ I NAZWISKO	SPECJALNOŚĆ, NR UPRAWNIEN
Projektant		DATA
Projektant (wsp.)		PODPIS
Sprawdzający		
Opracował		
TYTUŁ RYSUNKU		
DETALE — COKÓŁ, PRÓG HS, RURA SPUSTOWA		
SKALA	FORMAT	DATA WYDANIA
1:10	A3×4	2026-09-25
RODZAJ DOK.	NR RYSUNKU	ARKUSZ
detal	PT-AR-D-01	1/6
REW.		
0		