



A
B
C
D
E
F
G
H

odcinek kontrolny 100 mm (wydruk 1:1)

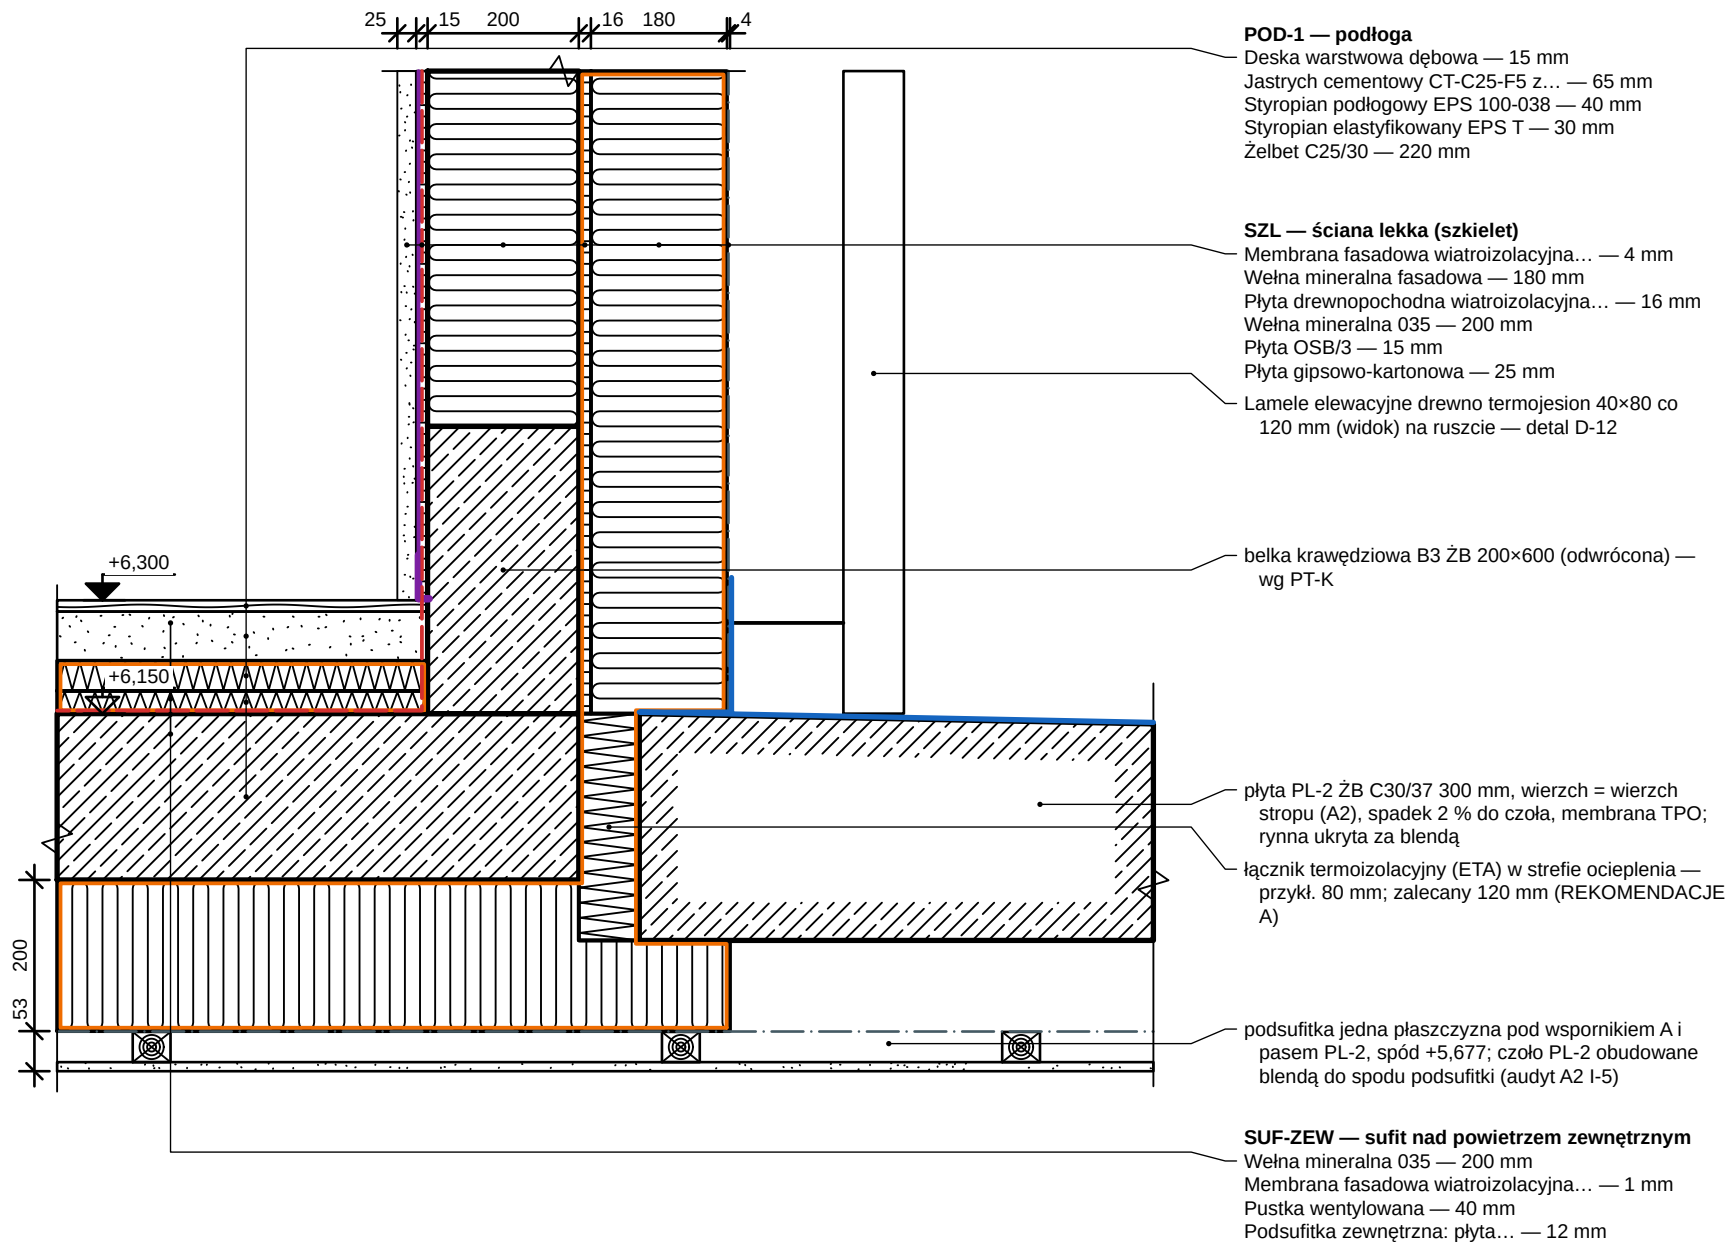

WZ-07a: $\psi_e = 0,058$, $\psi_{oi} = 0,182$ W/(m·K); f_Rsi = 0,837 ≥ 0,72 — DO POPRAWY
WZ-16a: $\psi_e = 0,057$, $\psi_{oi} = 0,236$ W/(m·K); f_Rsi = 0,840 ≥ 0,72 — DO POPRAWY
4 linie: H OK, S OK, P OK, I OK — ciągłość zachowana


DETAL D-08 — WSPORNIK BRYŁY A — KRAWĘDŹ ST2Z Z PŁYTĄ PL-2 1:10

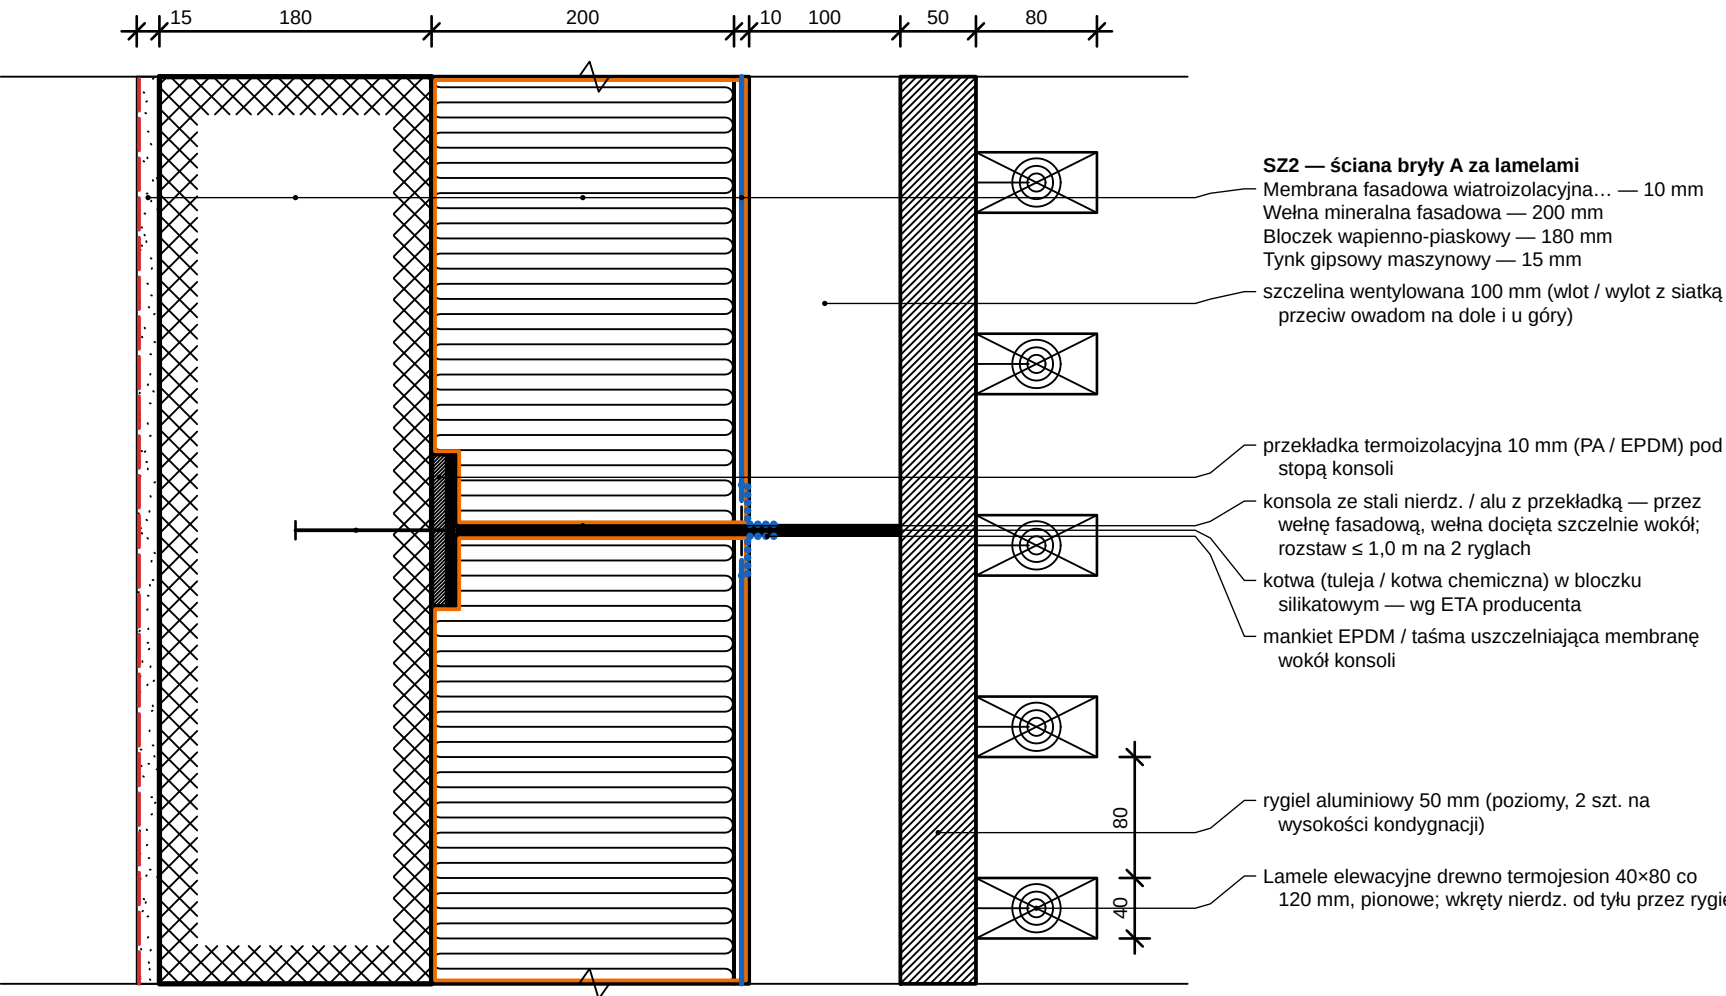

WZ-13 — mostek punktowy: $\chi = 0,010$ W/K × 51 szt. = 0,51 W/K ([DANE PRZYKŁADOWE – FIKCYJNE] dane przykładowe z deklaracji)
4 linie: H OK, S OK, P OK, I OK — ciągłość zachowana

DETAL D-12 — LAMELE ELEWACYJNE SZ2 — KONSOLA RUSZTU (RZUT) 1:5

OZNACZENIA MATERIAŁÓW (PN-B-01030 + przyjęte)

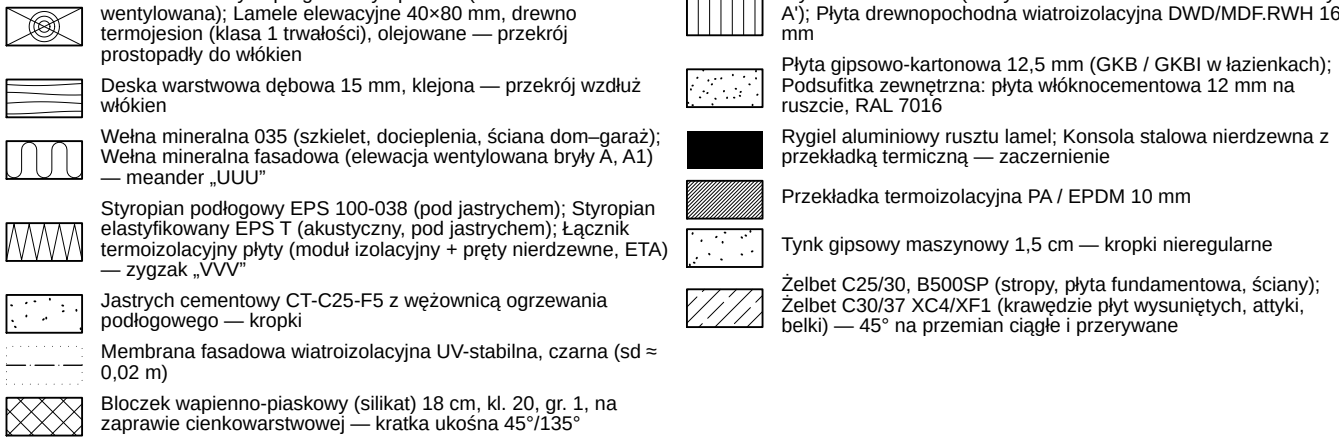

ZASADA „4 LINII” I OZNACZENIA DETALI

- hydroizolacja / izolacja przeciwwodna i przeciwwilgociowa (ochrona przed wodą)
- warstwa szczelności powietrznej (tynk wewn., płyta ŻB, OSB, membrana, taśmy)
- paroizolacja / kontrola pary (folia, papa z Al, membrana sd ≥ 10 m)
- izolacja cieplna — obrys ciąglej warstwy izolacji (test „ołówka”)
- taśma paroszczelna (od wewnątrz — ciepły montaż)
- taśma paroprzepuszczalna / uszczelnienie zewnętrzne (ciepły montaż, próg)
- membrana wiatroizolacyjna paroprzepuszczalna
- geowłóknina, bariera przeciwwkorzeniowa, mata drenażowa
- obróbka blacharska z okapnikiem (kapinosem), rynna ukryta

WYNIKI MOSTKÓW (PN-EN ISO 10211) I OCENA 4 LINII

D-08: WZ-07a: $\psi_e = 0,058$, $\psi_{oi} = 0,182$ W/(m·K); f_Rsi = 0,837 ≥ 0,72 — DO POPRAWY
WZ-16a: $\psi_e = 0,057$, $\psi_{oi} = 0,236$ W/(m·K); f_Rsi = 0,840 ≥ 0,72 — DO POPRAWY
4 linie: H OK, S OK, P OK, I OK — ciągłość zachowana

D-12: WZ-13 — mostek punktowy: $\chi = 0,010$ W/K × 51 szt. = 0,51 W/K ([DANE PRZYKŁADOWE – FIKCYJNE] dane przykładowe z deklaracji)
4 linie: H OK, S OK, P OK, I OK — ciągłość zachowana

OBJAŚNIENIA I UWAGI

- Wymiary w mm, rzędne w m względem ±0,000 = 101,650 m n.p.m. (PL-EVRF2007-NH).
- Kreskowania materiałów wg PN-B-01030:2000 (aktualna) i PN-EN ISO 128-3:2023-02 (zastąpiła wycofane PN-ISO 128-50:2006); oznaczenia spoza normy — w legendzie arkusza.
- Opisy warstw od zewnątrz do wewnątrz (kolejność kropek na linii odnośnika = kolejność wierszy), grubości w mm wg przegród modelu (kontrola zgodności — raport modułu detali).
- Zasada „4 linii” (brief §9.1): hydroizolacja — niebieska, szczelność powietrzna — czerwona przerywana, paroizolacja — fioletowa, izolacja cieplna — obrys pomarańczowy; każda linia ciągła wokół kubatury ogrzewanej.
- Wywiniecia hydroizolacji ≥ 15 cm ponad warstwę wierzchnią (zwir, substrat, nawierzchnia) — Wytyczne DAFA dla dachów płaskich; DIN 18531 (pomocniczo); PN-EN 1991 wysokości wywinieć nie określa. Cokół: uszczelnienie ≥ 30 cm nad terenem (brief §9.4; DIN 18533-1 — pomocniczo) albo odwodnienie liniowe przy drzwiach bezprogowych.
- Wyroby (łączniki termoizolacyjne, taśmy, profile progowe, wpusty, konsole) — dane przykładowe „lub równoważne”; parametry (ETA/DWU) do potwierdzenia przed realizacją.
- Detal D-08: wspornik bryły A: ocieplenie spodu stropu ST2Z ciągle od ETICS ściany P1 do lica ocieplenia ściany lekkiej, podsuflita wentylowana (szczelina 40 mm, kratki na obwodzie)
- Detal D-12: mostek punktowy konsoli: χ wg deklaracji producenta (wartość w zestawieniu H_TB — dane przykładowe do potwierdzenia wyrobem); liczba konsol z długości linii lamel × 2 rygle / 1,0 m
- Detal D-12: rzut na wysokości konsoli — rozstaw konsol i rygli wg obliczeń statycznych rusztu (PT-K / dostawca systemu)
- Rysunek wygenerowany automatycznie z modelu model/budynek.yaml (wersja 1.0, 2026-09-25) — generatory lamela.views.

0,2 0 0,2 0,4 0,6 0,8 1 m
PODZIAŁKA 1:10

REW.	OPIS ZMIANY			DATA
0	Wydanie — rysunek wygenerowany z modelu			2026-09-25
PRACOWNIA PROJEKTOWA PRACOWNIA PROJEKTOWA — nazwa do uzupełnienia adres pracowni do uzupełnienia		STADIUM PT	BRANŻA ARCHITEKTURA (AR)	
INWESTOR (do uzupełnienia)				
OBIEKT / NAZWA ZAMIERZENIA BUDOWLANEGO Budynek mieszkalny jednorodzinny wolnostojący „Dom LAMELA”				
ADRES / LOKALIZACJA (NR DZIAŁKI, OBRĘB, JEDN. EWIDENCYJNA) ul. Lipowa (fikcyjna), dz. nr ewid. 123/4, obręb 0005 Przykładowo, gm. Przykładowo (fikcyjna)				KAT. OBIEKTU I
FUNKCJA	IMIĘ I NAZWISKO	SPECJALNOŚĆ, NR UPRAWNIENI	DATA	PODPIS
Projektant				
Projektant (wsp.)				
Sprawdzający				
Opracował				
TYTUŁ RYSUNKU DETALE — WSPORNIK BRYŁY A, LAMELE ELEWACYJNE				
SKALA 1:5 / 1:10	FORMAT A2	DATA WYDANIA 2026-09-25	RODZAJ DOK. detal	NR RYSUNKU PT-AR-D-04
			ARKUSZ 4/6	REW. 0