


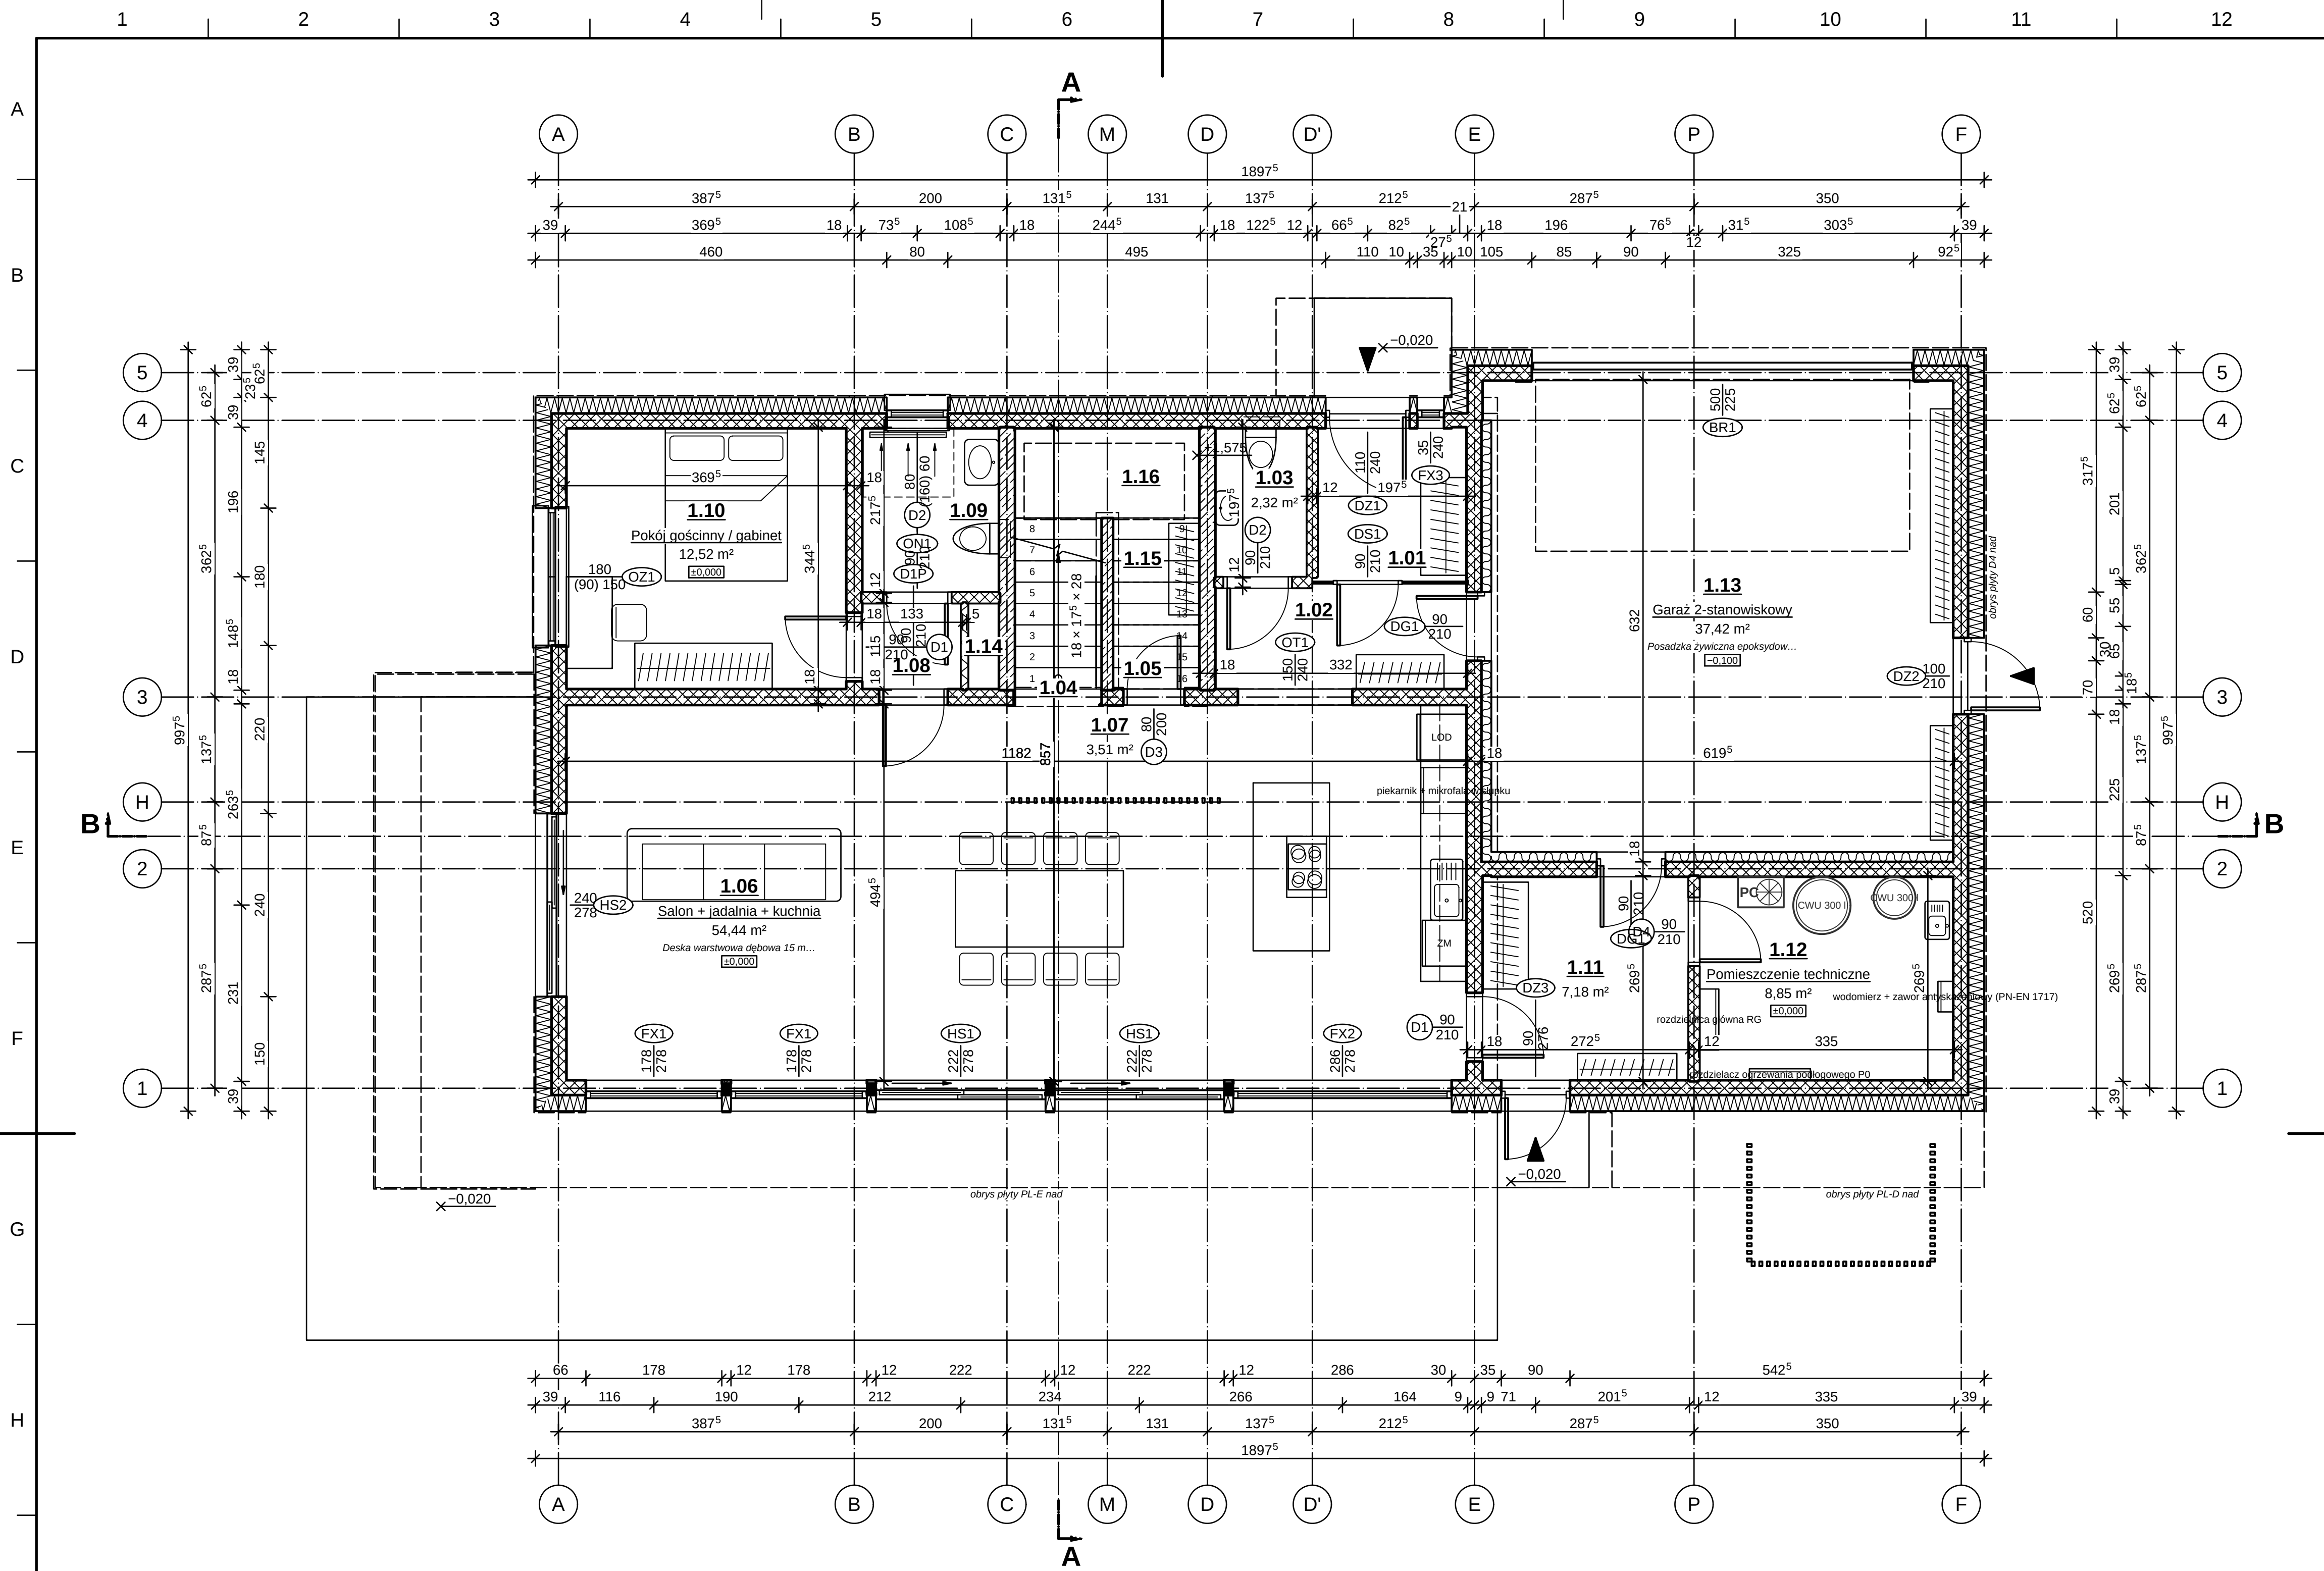

RZUT PARTERU 1:50

ZESTAWIENIE POMIESZCZEŃ

| Nr                            | Nazwa pomieszczenia                | Posadzka                                                | Kat.   | Wys. [m] | Pow. [m²] |
|-------------------------------|------------------------------------|---------------------------------------------------------|--------|----------|-----------|
| 1.06                          | Salon + jadalnia + kuchnia         | Deska warstwowa dębowa 15 mm, klejona                   | podst. | 2,77     | 54,44     |
| 1.13                          | Garaż 2-stanowiskowy               | Posadzka żywiczna epoksydowa antypoślizgowa R11 (garaż) | pomoc. | 2,76     | 37,42     |
| 1.10                          | Pokój gościnny / gabinet           | Deska warstwowa dębowa 15 mm, klejona                   | podst. | 2,77     | 12,52     |
| 1.12                          | Pomieszczenie techniczne           | Płytki gresowe 60×120 na kleju C2TE S1                  | techn. | 2,76     | 8,85      |
| 1.11                          | Przedsiónek gospodarczy            | Płytki gresowe 60×120 na kleju C2TE S1                  | ruchu  | 2,76     | 7,18      |
| 1.02                          | Hoł                                | Płytki gresowe 60×120 na kleju C2TE S1                  | ruchu  | 2,77     | 4,44      |
| 1.01                          | Wiatrołap                          | Płytki gresowe 60×120 na kleju C2TE S1                  | ruchu  | 2,77     | 3,89      |
| 1.09                          | Łazienka gościnna (natrysk)        | Płytki gresowe 60×120 na kleju C2TE S1                  | pomoc. | 2,77     | 3,84      |
| 1.07                          | Pas komunikacyjny przy schodach    | Deska warstwowa dębowa 15 mm, klejona                   | ruchu  | 2,77     | 3,51      |
| 1.16                          | Schówek pod spocznikiem (h < 1,40) | Płytki gresowe 60×120 na kleju C2TE S1                  | pomoc. | 1,37     | 2,91      |
| 1.04                          | Klatka schodowa                    | Deska warstwowa dębowa 15 mm, klejona                   | ruchu  | 2,77     | 2,78      |
| 1.03                          | WC gościnne                        | Płytki gresowe 60×120 na kleju C2TE S1                  | pomoc. | 2,77     | 2,32      |
| 1.15                          | Schówek pod schodami (h 1,40-2,20) | Płytki gresowe 60×120 na kleju C2TE S1                  | pomoc. | 1,80     | 1,45      |
| 1.08                          | Przedpokój gościnny                | Deska warstwowa dębowa 15 mm, klejona                   | ruchu  | 2,77     | 1,44      |
| 1.05                          | Spizarnia                          | Płytki gresowe 60×120 na kleju C2TE S1                  | pomoc. | 2,77     | 1,02      |
| 1.14                          | Szacht instalacyjny SI             |                                                         | techn. | 2,77     | 0,45      |
| RAZEM powierzchnia netto      |                                    |                                                         |        |          | 148,45    |
| w tym podstawowa + pomocnicza |                                    |                                                         |        |          | 115,91    |

OZNACZENIA MATERIAŁÓW (PN-B-01030 + przyjęte)



|  |   |  |   |
|--|---|--|---|
|  | Włna mineralna 035 (szkielet, docieplenia, ściana dom-garaż)   |  | Stal konstrukcyjna S355 (słupy RK, rama boksu C), cynkowana ogniowo + malowana proszkowo RAL 7016 — zaczernienie                                                    |
|  | Styropian grafitowy EPS 031 (ETICS, NRO w systemie) — zrygawk „VVV”   |  | Ścianka szklana VSG 2 x 8 mm w ramie aluminiowej (wiatrołap / hol)                                                                                                  |
|  | Błoczek wapienno-piaskowy 12 cm, kl. 15 (ścianki działowe, lico w klatce); Błoczek wapienno-piaskowy (silikat) 18 cm, kl. 20, gr. 1, na zaprawie cienkowarstwowej — klatka ukośna 45°/135° |  | Żelbet C25/30, B500SP (stropy, płyta fundamentowa, ściany); Żelbet C30/37 XC4/XF1 (krawędzie płyt wysuniętych, attyki, belki) — 45° na przemian ciagle i przerywane |

OZNACZENIA LINII

|  |                                                                                      |
|--|--------------------------------------------------------------------------------------|
|  | elementy nad płaszczyzną cięcia (obrysy płyt, wsporników, brył wyższych kondygnacji) |
|  | elementy poniżej płaszczyzny cięcia (widok z góry)                                   |
|  | osie konstrukcyjne; linia punktowa z pogrubionymi końcami — ślad przekroju           |

OBJAŚNIENIA I UWAGI

- Wymiary w cm (mm w indeksie górnym, np. 24<sup>5</sup> = 24,5 cm), rzędne w m względem ±0,000 = 101,650 m n.p.m. (PL-EVRF2007-NH).
- Rzuty: płaszczyzna cięcia +1,10 m nad posadzką kondygnacji. Linia kreskową — elementy nad płaszczyzną cięcia (obrysy płyt i wsporników, brył wyższych kondygnacji, otwory w stropie nad, belki); linią ciekłą — elementy poniżej (widok).
- Otwory: licznik — szerokość, mianownik — wysokość w świetle muru, w nawiasie wysokość parapetu; symbol stolarki wg zestawienia stolarki.
- Numeracja pomieszczeń wg PN-B-01025 / PN-EN ISO 4157-2: <nr kondygnacji (partier = 1)> <nr> <identyfikator w modelu: <kond> <nr> (partier = 0)>.
- Drzwi: strona otwierania (lewe/prawe) wg modelu — patrząc od strony, w którą otwiera się skrzydło.
- Rysunek wygenerowany automatycznie z modelu model/budynek-yaml (wersja 1.0, 2026-09-25) — generatory lamela.views.

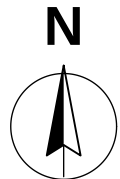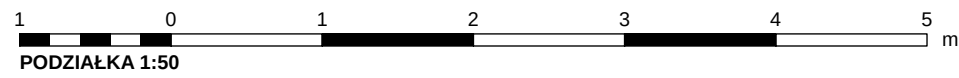

|   |                                         |                             |
|---|-----------------------------------------|-----------------------------|
| REW.   | OPIS ZMIANY                             | DATA                        |
| 0   | Wydanie — rysunek wygenerowany z modelu | 2026-09-25                  |
| PRACOWNIA PROJEKTOWA<br>PRACOWNIA PROJEKTOWA — nazwa do uzupełnienia                                                                                        |                                         | STADIUM<br>PB               |
| adres pracowni do uzupełnienia   |                                         | BRANŻA<br>ARCHITEKTURA (AR) |
| INWESTOR<br>(do uzupełnienia)   |                                         |                             |
| OBIEKT / NAZWA ZAMIERZENIA BUDOWLANEGO<br>Budynek mieszkalny jednorodzinny wolnostojący „Dom LAMELA”                                                        |                                         |                             |
| ADRES / LOKALIZACJA (NR DZIAŁKI, OBRĘB, JEDN. EWIDENCYJNA)<br>ul. Lipowa (fikcyjna), dz. nr ewid. 123/4, obręb 0005 Przykładowo, gm. Przykładowo (fikcyjna) |                                         | KAT. OBIEKTU<br>I           |
| FUNKCJA   | IMIĘ I NAZWISKO                         | SPECJALNOŚĆ, NR UPRAWNIENI  |
| Projektant   | [DO UZUPEŁNIENIA]                       | [DO UZUPEŁNIENIA]           |
| Projektant (wsp.)   | [DO UZUPEŁNIENIA]                       | [DO UZUPEŁNIENIA]           |
| Sprawdzający   | nie dotyczy (art. 20 ust. 3 pkt 2 PB)   | —                           |
| Opracował   | [DO UZUPEŁNIENIA]                       | [DO UZUPEŁNIENIA]           |
| TYTUŁ RYSUNKU<br>RZUT PARTERU   |                                         |                             |
| SKALA<br>1:50   | FORMAT<br>630×594                       | DATA WYDANIA<br>2026-09-25  |
| RODZAJ DOK.<br>rzut   | NR RYSUNKU<br>PB-AR-01                  | ARKUSZ<br>1/5               |
| REW.<br>0   |                                         |                             |