

RZUT II PIĘTRA 1:50



OZNACZENIA LINII

- elementy nad płaszczyzną cięcia (obrysy płyt, wsporników, brył wyższych kondygnacji)
--- elementy poniżej płaszczyzny cięcia (widok z góry)
--- osie konstrukcyjne; linia punktowa z pogrubionymi końcami — ślad przebiegu

RZUT DACHU 1:50

OBJAŚNIENIA I UWAGI

- Wymiary w cm (mm w indeksie górnym, np. 24° = 24,5 cm), rzędne w m względem ±0,000 = 101,650 m n.p.m. (PL-EVRF2007-NH).
- Rzuty: płaszczyzna cięcia +1,10 m nad posadzką kondygnacji. Linia kreskowa — elementy nad płaszczyzną cięcia (obrysy płyt i wsporników, brył wyższych kondygnacji), otwory w stropie nad, belki), linia cienka — elementy poniżej (widok).
- Otwory: licznik — szerokość; mianownik — wysokość w świetle muru, w nawiasie wysokość parapetu; symbol stolarki wg zestawienia stolarki.
- Numeracja pomieszczeń wg PN-B-01025 / PN-EN ISO 4157-2: <nr kondygnacji (parter = 1)> <nr> <identyfikator w modelu: <kond> <nr> (parter = 0).
- Drzwi: strona otwierania (lewe/prawe) wg modelu — patrzeć od strony, w którą otwiera się skrzydło.
- Rysunek wygenerowany automatycznie z modelu model/budynki.yamli (wersja 1.0, 2026-09-25) — generatory lamela.views.

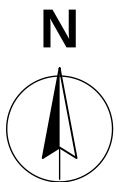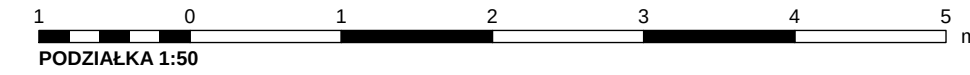

ZESTAWIENIE POMIESZCZEŃ

Nr	Nazwa pomieszczenia	Posadzka	Kat.	Wys. [m]	Pow. [m²]
3.02	Sypialnia rodziców	Deska warstwowa dębowa 15 mm, klejona	podst.	2,77	21,43
3.05	Gabinet / pokój gościnny okazjonalny	Deska warstwowa dębowa 15 mm, klejona	podst.	2,77	16,25
3.03	Garderoba (przedpokój apartamentu)	Deska warstwowa dębowa 15 mm, klejona	pomoc.	2,77	10,49
3.07	Pom. techniczne (centrala rekuperacyjna, wyłaz na dach)	Płytki gresowe 60×120 na kleju C2TE S1	techn.	2,77	5,90
3.01	Hol	Deska warstwowa dębowa 15 mm, klejona	ruchu	2,77	5,74
3.04	Łazienka rodziców	Płytki gresowe 60×120 na kleju C2TE S1	pomoc.	2,77	5,51
3.08	Szacht instalacyjny SI		techn.	2,77	0,45
3.06	Klatka schodowa (wyjście z biegu 2, pustka)	Deska warstwowa dębowa 15 mm, klejona	ruchu	2,77	0,24
RAZEM powierzchnia netto					66,01
w tym podstawowa + pomocnicza					53,67

OZNACZENIA MATERIAŁÓW (PN-B-01030 + przyjęte)

	Włna mineralna 035 (szkielet, docieplenia, ściana dom-garaz); Włna mineralna fasadowa (elewacja wentylowana bryły A, A1) — meander „UUU”		Błoczek wapienno-piaskowy 12 cm, kl. 15 (ściana działkowa, łączowy w klatce); Błoczek wapienno-piaskowy (silikat) 18 cm, kl. 20, gr. 1, na zaprawie cienkowarstwowej — kratka ukośna 45/7,135°
	Styropian grafitowy EPS 031 (ETICS, NRO w systemie) — zygzrak „VVV”		Żelbet C25/30, B500SP (stropy, płyta fundamentowa, ściany); Żelbet C30/37 XC4/XF1 (krawędzie płyt wysuniętych, atyki, belki) — 45° na przemian cienie i przerywane
	Membrana fasadowa wiatroizolacyjna UV-stabilna, czarna (sd = 0,02 m)		

REW.	OPIS ZMIANY	DATA
0	Wydanie — rysunek wygenerowany z modelu	2026-09-25
PRACOWNIA PROJEKTOWA PRACOWNIA PROJEKTOWA — nazwa do uzupełnienia		STADIUM PB
adres pracowni do uzupełnienia		BRANŻA ARCHITEKTURA (AR)
INWESTOR (do uzupełnienia)		
OBJEKT / NAZWA ZAMIERZENIA BUDOWLANEGO Budynek mieszkalny jednorodzinny wolnostojący „Dom LAMELA”		
ADRES / LOKALIZACJA (NR DZIAŁKI, OBRĘB, JEDN. EWIDENCYJNA) ul. Lipowa (fikcyjna), dz. nr ewid. 123/4, obręb 0005 Przykładowo, gm. Przykładowo (fikcyjna)		KAT. OBJEKTU I
FUNKCJA	IMIĘ I NAZWISKO	SPECJALNOŚĆ, NR UPRAWNIENI
Projektant	[DO UZUPEŁNIENIA]	[DO UZUPEŁNIENIA]
Projektant (wsp.)	[DO UZUPEŁNIENIA]	[DO UZUPEŁNIENIA]
Sprawdzający	nie dotyczy (art. 20 ust. 3 pkt 2 PB)	—
Opracował	[DO UZUPEŁNIENIA]	[DO UZUPEŁNIENIA]
TYTUŁ RYSUNKU RZUT II PIĘTRA I RZUT DACHU		
SKALA 1:50	FORMAT 590×891	DATA WYDANIA 2026-09-25
RODZAJ DOK. Rzut	NR RYSUNKU PB-AR-03	ARKUSZ 3/5
REW. 0		