


PRZEKRÓJ A-A 1:50

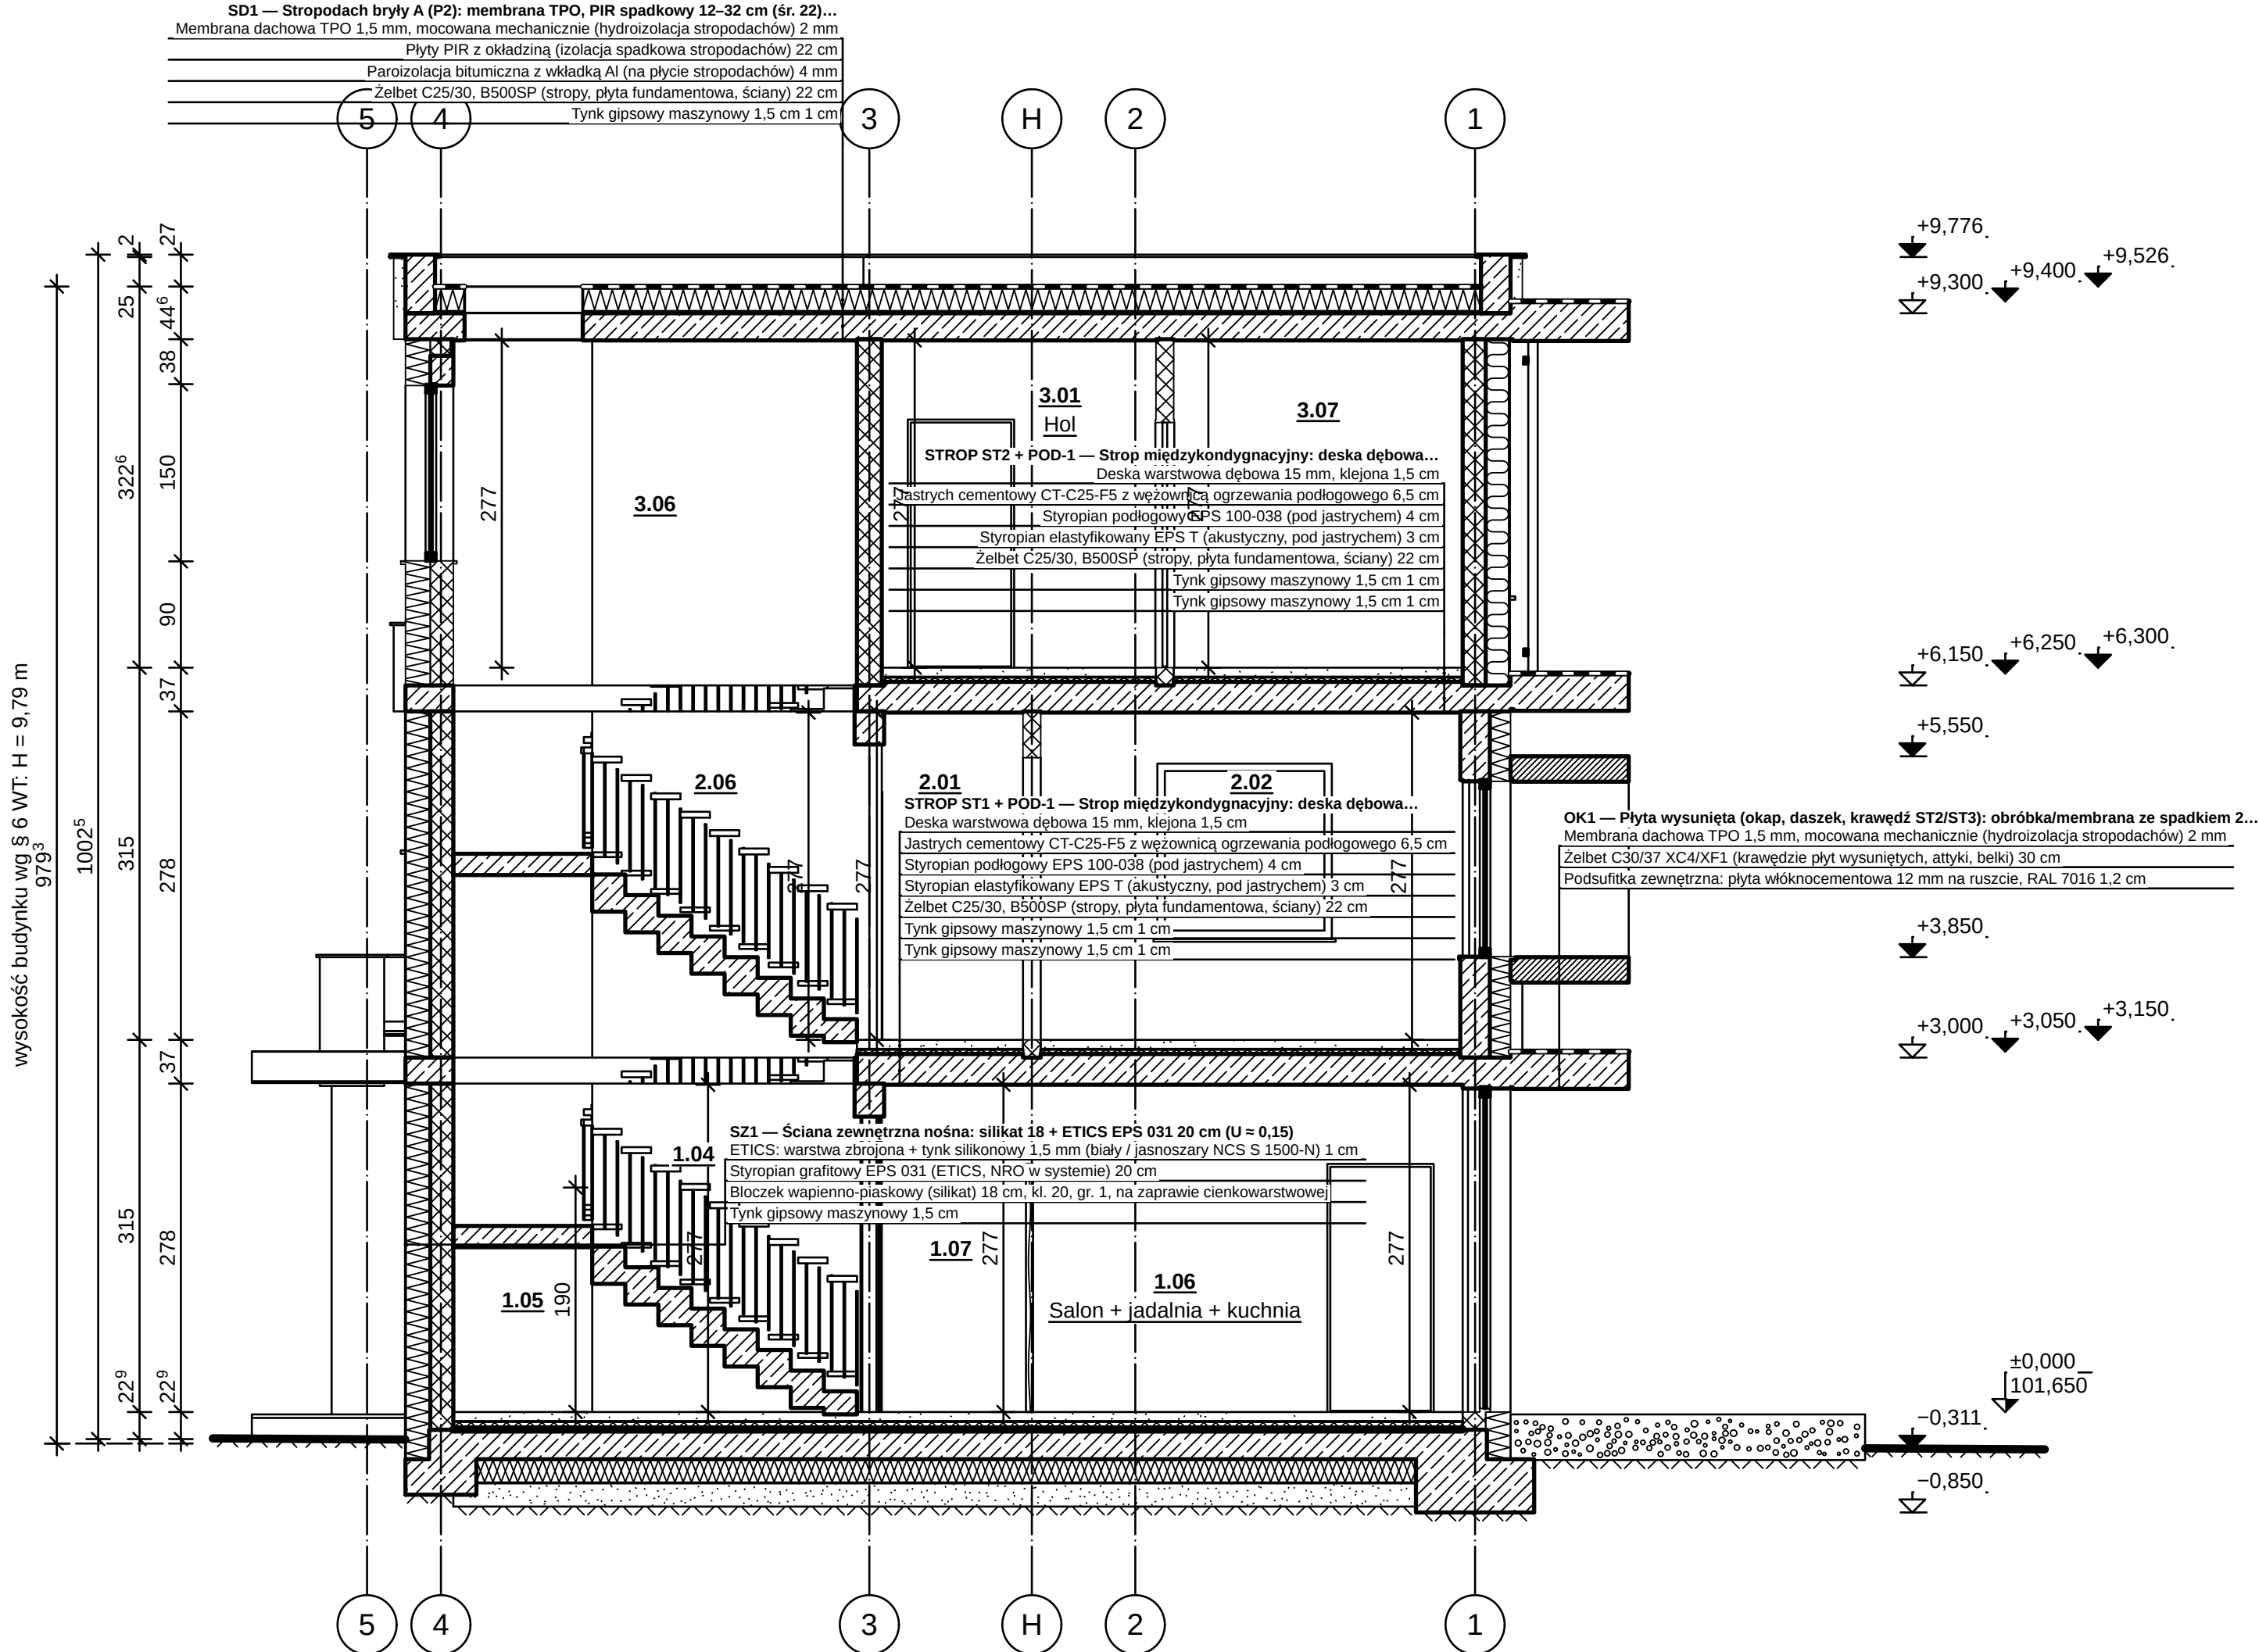


OZNACZENIA MATERIAŁÓW (PN-B-01030 + przyjęte)

	Lamele dębowe 30×60 mm (ekran komunikacji P0, h 2,10 m); Deska warstwowa dębowa 15 mm, klejona — przekrój wzdłuż włókien		Membrana fasadowa wiatroizolacyjna UV-stabilna, czarna (sd = 0,02 m)
	grunt rodzimy		Błoczek wapienno-piaskowy 12 cm, kl. 15 (ścianki działowe, licowy w klatce); Błoczek wapienno-piaskowy (silikat) 18 cm, kl. 20, gr. 1, na zaprawie cienkowarstwowej — krata ukośna 45°/135°
	Wetna mineralna fasadowa (elewacja wentylowana bryły A, A1) — meander „UUU”		Folia PE 0,2 mm (warstwa rozdzielająca); Parioizolacja bitumiczna z wkładką Al (na płycie stropodachów) — linia kropkowa cienka 3/1 po ciepłej stronie
	Płyty PIR z okładziną (izolacja spadkowa stropodachów) — zygzak z okładziną		Podsypka piaskowa zagęszczona (l_s ≥ 0,98)
	Izolacja przeciwwilgociowa i przeciwdrońowa: membrana SBS 4 mm na płycie fundamentowej — linia bardzo gruba		Obróbki blacharskie (blacha powlekana); Stoiarka — profile aluminiowe, antracyt; Rama boksu C; ruszt stalowy ocynkowany w okładzinie z blachy aluminiowej RAL 7016 (pusia w środku); Stal malowana proszkowo (balustrady, rygle) — zacierzenie
	Membrana dachowa TPO 1,5 mm, mocowana mechanicznie (hydroizolacja stropodachów) — pas czarno-biały		Tynk gipsowy maszynowy 1,5 cm; ETICS: warstwa zbrojona + tynk silikonowy 1,5 mm (biały / jasnoszary NCS S 1500-N) — kropki nieregularne
	Styropian grafitowy EPS 031 (ETICS, NRO w systemie); Styropian podłogowy EPS 100-038 (pod jastrychem); Styropian elastyfikowany EPS T (akustyczny, pod jastrychem) — zygzak „VVV”		Żelbet C25/30, B500SP (stropy, płyta fundamentowa, ściany); Żelbet C30/37 XC4/XF1 (krawędzie płyt wysuniętych, atyki, belki) — 45° na przemian ciągłe i przerywane
	Polistyren ekstrudowany XPS 300 (pod płytą fundamentową, cokół, izolacja obwodowa) — zygzak podwójny		Podbudowa nawierzchni (kruzywo)
	Jastrych cementowy CT-C25-F5 z węzownicą ogrzewania podłogowego — zygzak		

OBJAŚNIENIA I UWAGI

- Wymiary w cm (mm w indeksie górnym, np. 24⁶ = 24,5 cm), rzędne w m względem ±0,000 = 101,650 m n.p.m. (PL-EVRF2007-NH).
- Rzędne: trójkąt zacierzony — poziom wykończenia, niezacierzony — konstrukcji, w połowie zacierzony — poziom ±0,000 z rzędną bezwzględną (PN-B-01025).
- Wysokość budynku wg § 6 WT: od terenu przy najniższej położonym wejściu (−0,267) do wierzchu stropodachu D1 (+9,526) — H = 9,79 m (bez atyki).
- Opisy warstw: kod i nazwa przegrody z modelu, materiały i grubości wg modelu (od góry / od lewej).
- Opisy warstw pominięte na rysunku (brak miejsca w podziale 1:50): POD-0 — układ warstw wg zestawienia przegród w części opisowej / przekroju 1:50.
- Rysunek wygenerowany automatycznie z modelu /home/user/aihouse/model/budynek.yaml (wersja 1.0, 2026-09-25) — generatory lamele.views.

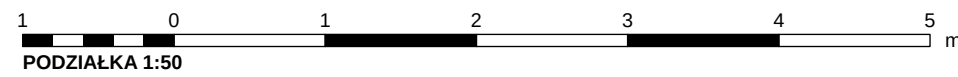

REW.		OPIS ZMIANY		DATA	
0		Wydanie — rysunek wygenerowany z modelu		2026-09-25	
PRACOWNIA PROJEKTOWA				STADIUM	BRANZA
PRACOWNIA PROJEKTOWA — nazwa do uzupełnienia				PB	ARCHITEKTURA (AR)
adres pracowni do uzupełnienia					
INWESTOR					
(do uzupełnienia)					
OBIEKT / NAZWA ZAMIERZENIA BUDOWLANEGO					
Budynek mieszkalny jednorodzinny wolnostojący „Dom LAMELA”					
ADRES / LOKALIZACJA (NR DZIAŁKI, OBRĘB, JEDN. EWIDENCYJNA)					KAT. OBIEKTU
ul. Lipowa (fikcyjna), dz. nr ewid. 123/4, obręb 0005 Przykładowo, gm. Przykładowo (fikcyjna)					I
FUNKCJA		IMIĘ I NAZWISKO		SPECJALNOŚĆ, NR UPRAWNIENI	DATA
Projektant					PODPIS
Projektant (wsp.)					
Sprawdzający					
Opracował					
TYTUŁ RYSUNKU					
PRZEKRÓJ A-A					
SKALA	FORMAT	DATA WYDANIA	RODZAJ DOK.	NR RYSUNKU	ARKUSZ
1:50	A3×3	2026-09-25	przekrój	PB-AR-05	5/10
					REW.
					0