



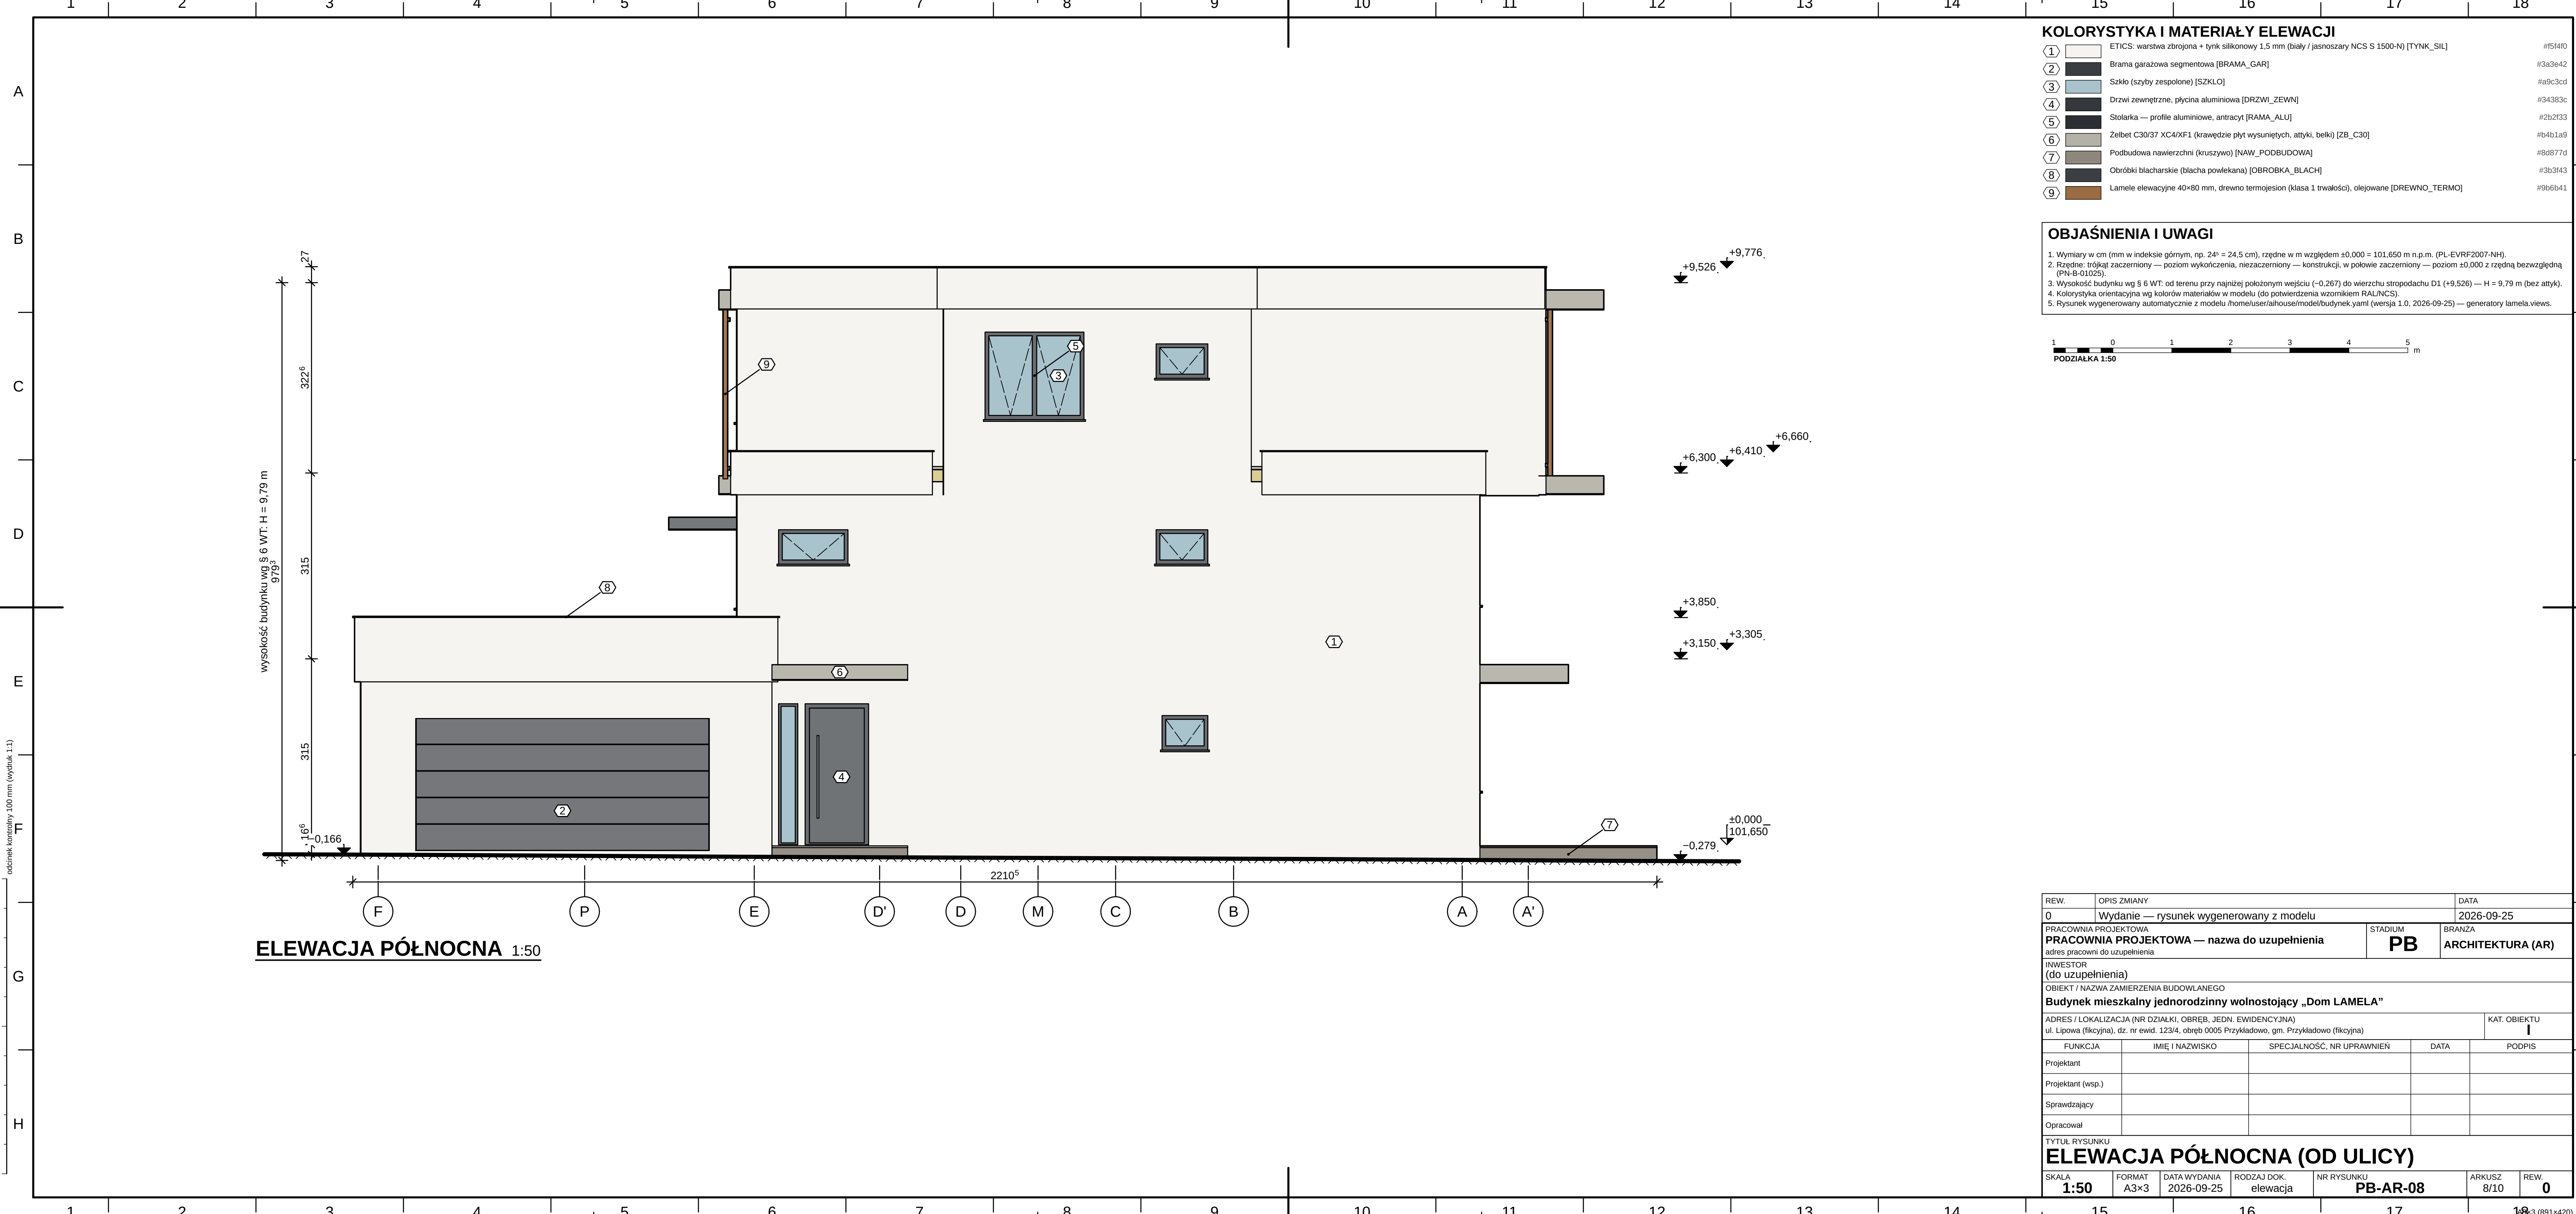

KOLORYSTYKA I MATERIAŁY ELEWACJI		
1	ETICS: warstwa zbrojona + tynk silikonowy 1.5 mm (biały / jasnoszary NCS S 1500-N) [TYNK_SIL]	#f5f4f0
2	Brama garażowa segmentowa [BRAMA_GAR]	#3a3e42
3	Szkle (szyby zespolone) [SZKLO]	#a9c3cd
4	Drzwi zewnętrzne, płycina aluminiowa [DRZWI_ZEWN]	#34383c
5	Stolarka — profile aluminiowe, antracyt [RAMA_ALU]	#2b2f33
6	Żelbet C30/37 XC4/XF1 (krawędzie płyt wysuniętych, attyki, belki) [ZB_C30]	#b4b1a9
7	Podbudowa nawierzchni (kruszywo) [NAW_PODBUDOWA]	#8d877d
8	Ostróbki blacharskie (blacha powlekana) [OBROBKA_BLACH]	#3b3f43
9	Lamele elewacyjne 40×80 mm, drewno termojesion (klasa 1 trwałości), olejowane [DREWNO_TERMO]	#9b6b41

OBJAŚNIENIA I UWAGI	
1. Wymiary w cm (mm w indeksie górnym, np. 24 ⁶ = 24,5 cm), rzędne w m względem ±0.000 = 101,650 m n.p.m. (PL-EVRF2007-NH).	
2. Rzędne: trójkąt zaczerpiony — poziom wykończenia, niezaczerpiony — konstrukcji, w połowie zaczerpiony — poziom ±0.000 z rzędną bezwzględną (PN-B-01025).	
3. Wysokość budynku wg § 6 WT: od terenu przy najniżej położonym wejściu (−0.267) do wierzchu stropodachu D1 (+9.526) — H = 9,79 m (bez attyki).	
4. Kolorystyka orientacyjna wg kolorów materiałów w modelu (do potwierdzenia wzornikiem RALNCS).	
5. Rysunek wygenerowany automatycznie z modelu /home/user/ai/house/model/budynek.yaml (wersja 1.0, 2026-09-25) — generatory lamela.views.	

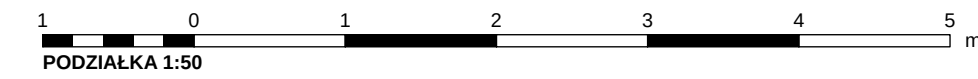

REW.	OPIS ZMIANY			DATA
0	Wydanie — rysunek wygenerowany z modelu			2026-09-25
PRACOWNIA PROJEKTOWA			STADIUM	BRANZA
PRACOWNIA PROJEKTOWA — nazwa do uzupełnienia			PB	ARCHITEKTURA (AR)
adres pracowni do uzupełnienia				
INWESTOR				
(do uzupełnienia)				
OBIEKT / NAZWA ZAMIERZENIA BUDOWLANEGO				
Budynek mieszkalny jednorodzinny wolnostojący „Dom LAMELA”				
ADRES / LOKALIZACJA (NR DZIAŁKI, OBREB, JEDN. EWIDENCYJNA)				KAT. OBIEKTU
ul. Lipowa (fikcyjna), dz. nr ewid. 123/4, obręb 0005 Przykładowo, gm. Przykładowo (fikcyjna)				I
FUNKCJA	IMIĘ I NAZWISKO	SPECJALNOŚĆ, NR UPRAWNIENI	DATA	PODPIS
Projektant				
Projektant (wsp.)				
Sprawdzający				
Opracował				
TYTUŁ RYSUNKU				
ELEWACJA PÓŁNOCNA (OD ULICY)				
SKALA	FORMAT	DATA WYDANIA	RODZAJ DOK.	NR RYSUNKU
1:50	A3x3	2026-09-25	elewacja	PB-AR-08
		ARKUSZ	REW.	
		8/10	0	