



PRZĘKRÓJ A-A 1:50

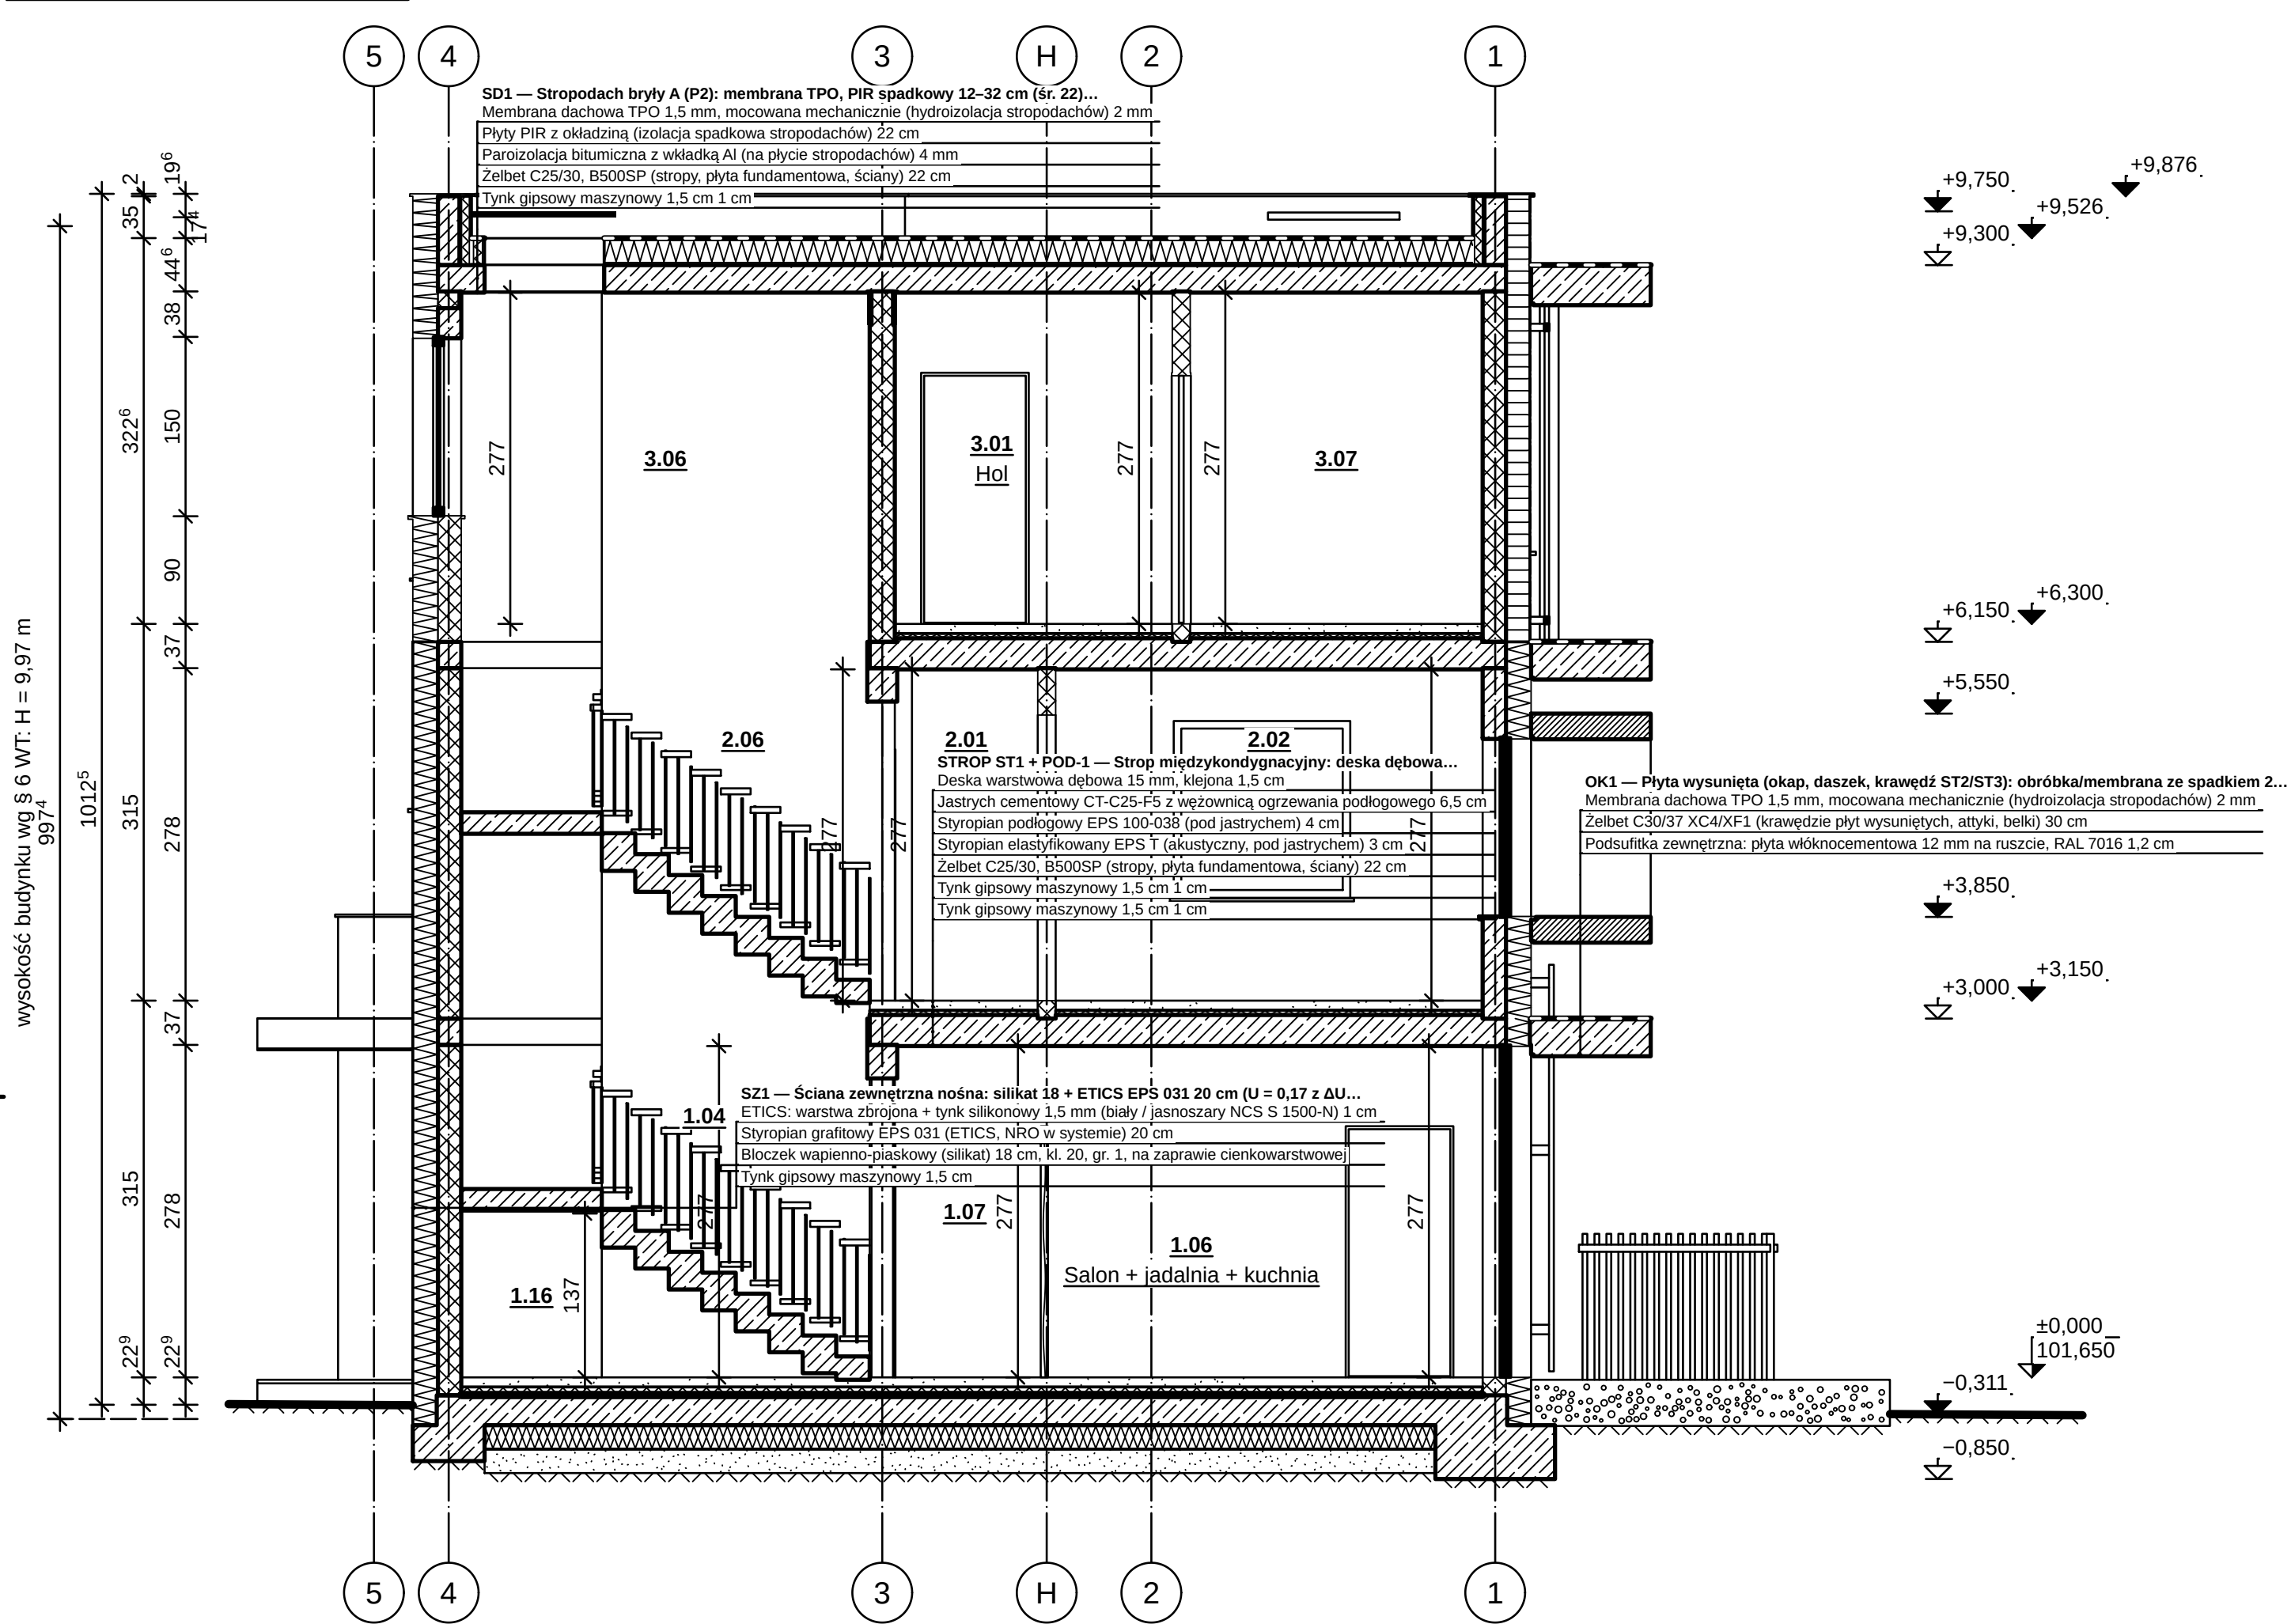

PRZĘKRÓJ B-B 1:50

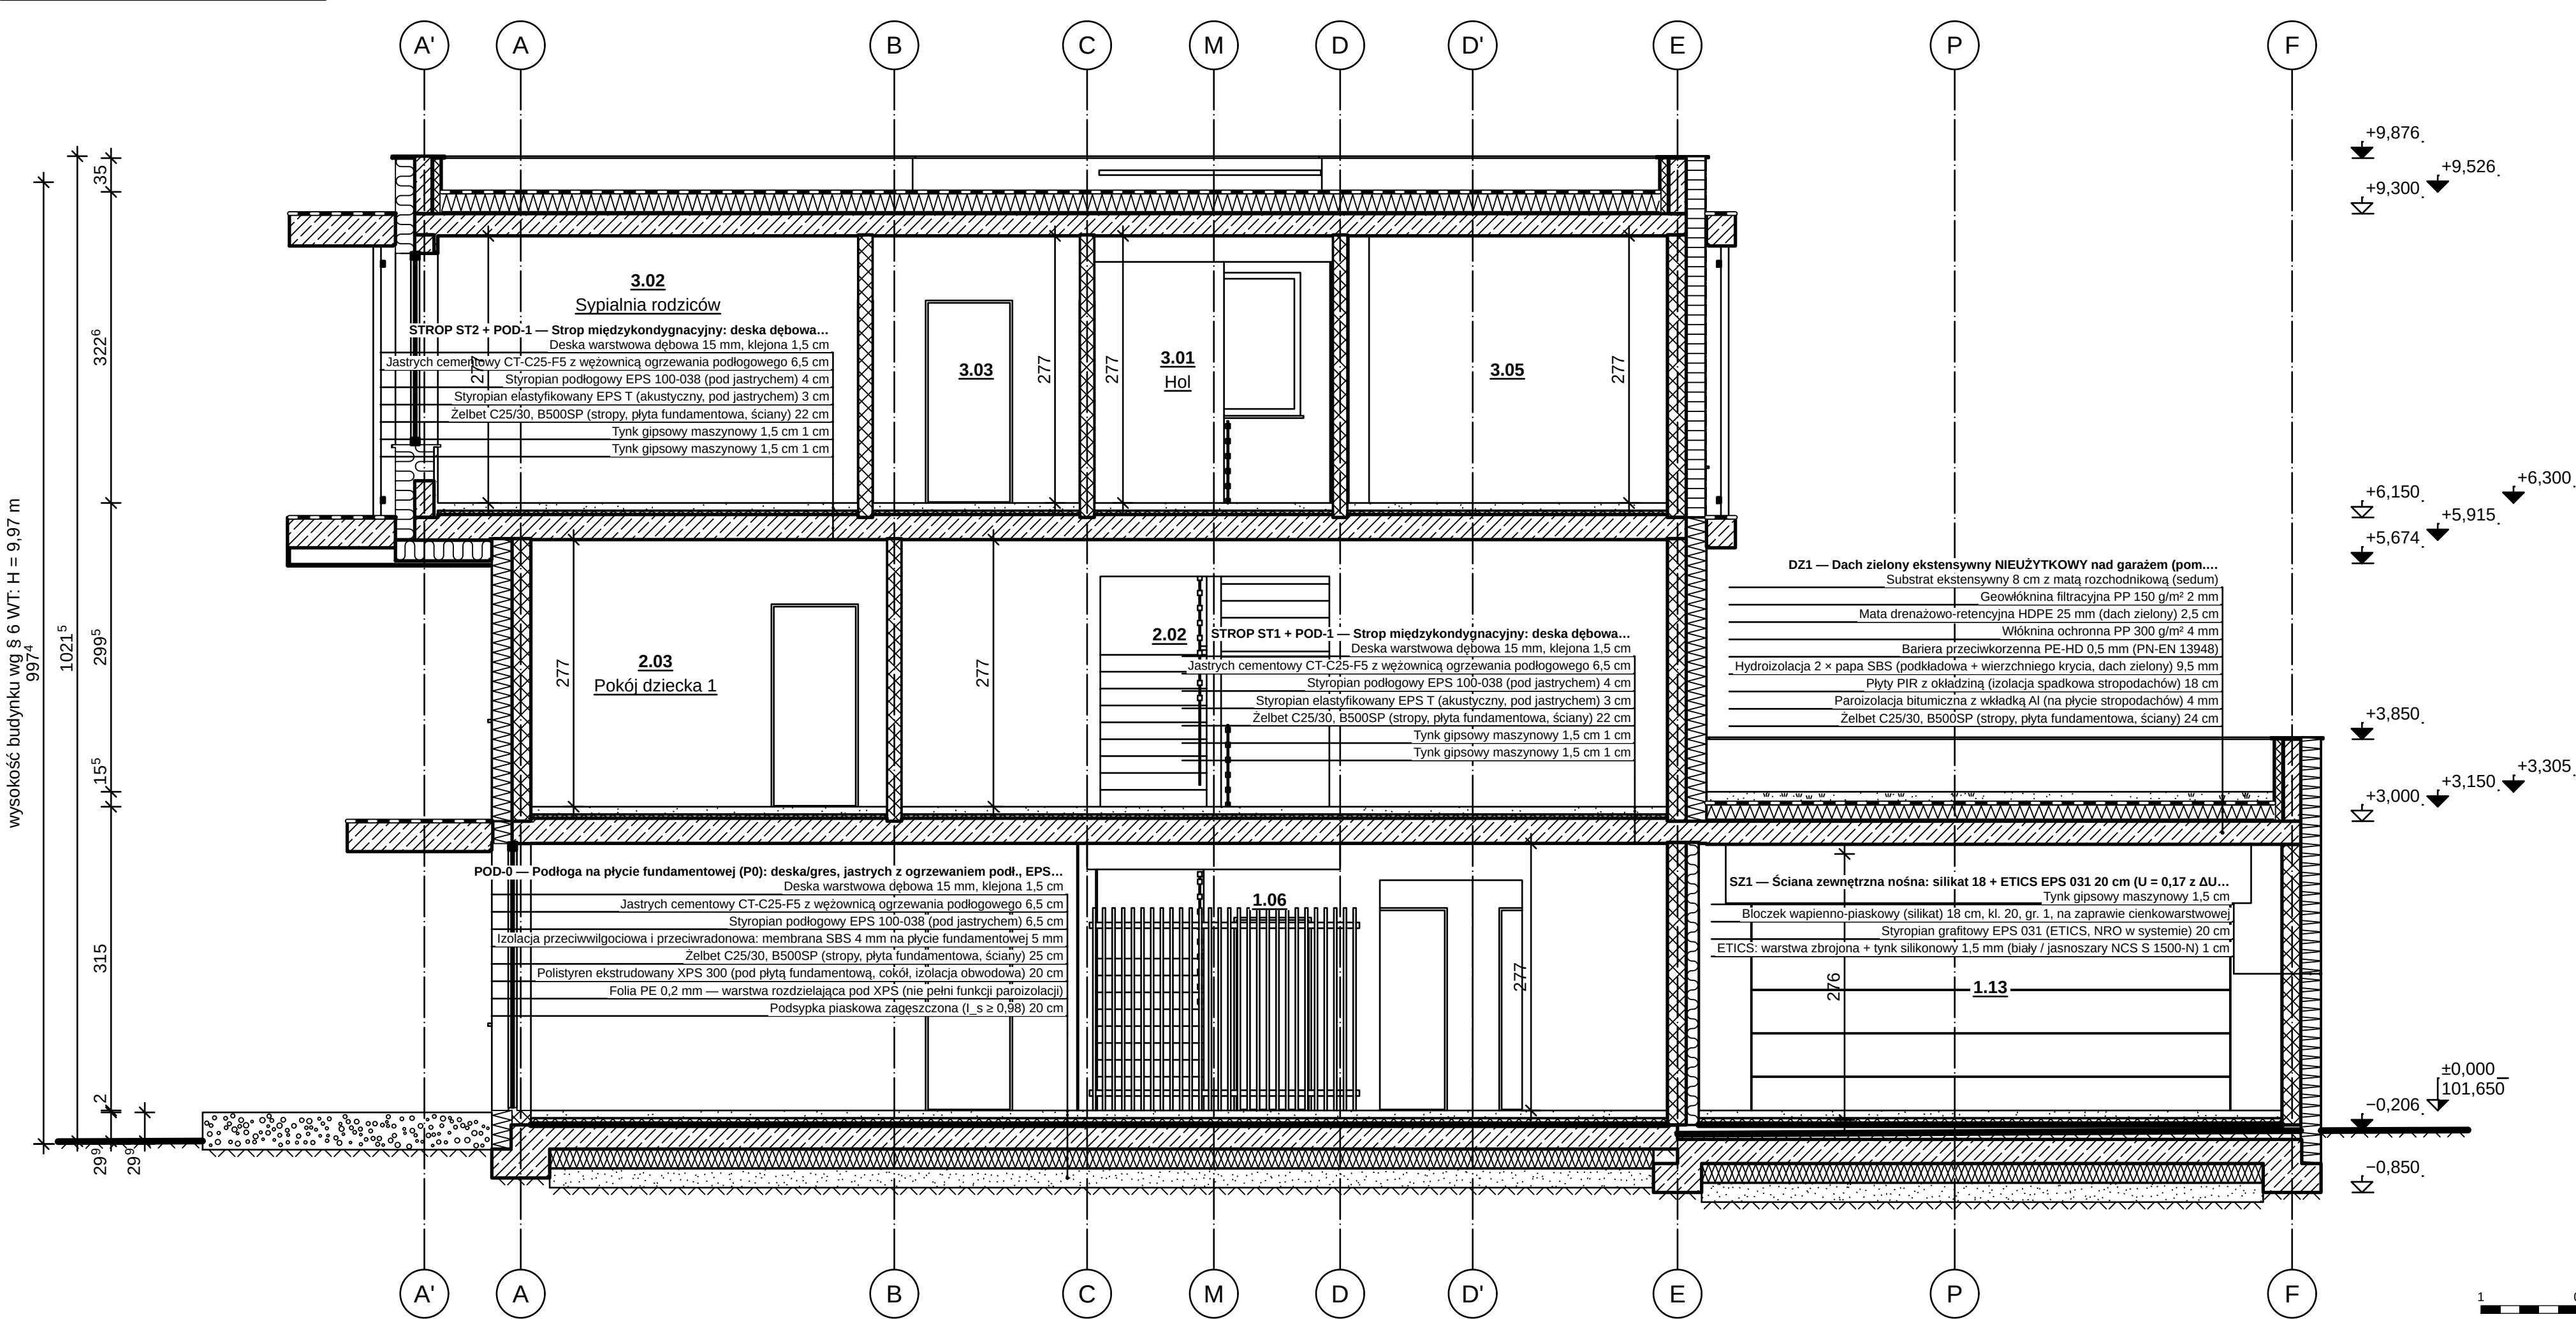

OBJAŚNIENIA I UWAGI

- Wymiary w cm (m w indeksie górnym, np. 24^m = 24,5 cm), rzędne w m względem ±0,000 = 101,650 m n.p.m. (PL-EVRF2007-NH).
- Rzędne: trójkąt zaczerpnięty — poziom wykończenia, niezaczerpnięty — konstrukcji, w polowie zaczerpnięty — poziom ±0,000 z rzędną bezwzględną (PN-B-01025).
- Wysokość budynku wg § 6 WT: od terenu przy najniższej położonym wejściu (-0,348) do wierzchu stropodachu D1 (+9,626) — H = 9,97 m (bez atyki).
- Opisy warstw: kod i nazwa przegrody i modelu, materiały i grubości wg modelu (od góry / od lewej).
- Rysunek projektu technicznego (RPB § 24 pkt 1) wykonany z tego samego stanu modelu co rysunki PB-AR-xx projektu architektoniczno-budowlanego (tom I); stan modelu: SHA-256 42ac7a811873 (budynek, działka, instalacje, wyposażenie).
- Układ warstw przegród, stolarka, wykończenia, odwodnienie — część opisowa PT-1 AR; węzły — detale PT-AR-D.
- Przekrój A-A: opisy warstw pominięte na rysunku (brak miejsca w podziale 1:50); POD-0, STROP ST2 + POD-1 — układ warstw wg zestawienia przegród w części opisowej / przekroju 1:50.
- Przekrój B-B: opisy warstw pominięte na rysunku (brak miejsca w podziale 1:50); SD1, OK1 — układ warstw wg zestawienia przegród w części opisowej / przekroju 1:50.
- Rysunek wygenerowany automatycznie z modelu model/budynek.yamli (wersja 1.0, 2026-09-25) — generatory lamela views.

ZNACZENIA MATERIAŁÓW (PN-B-01030 + przyjęte)

- Lamele dębowe 30x60 mm (ekran komunikacji P0, h 2,10 m);
Deska warstwowa dębowa 15 mm, klejona — przekrój wzdłuż włókna
- grunt rodzimy
- Substrat ekstensywny 8 cm z matą rozchodnikową (sedum)
- Włena mineralna fasadowa (elewacja wentylowana bryły A, A1);
Włena mineralna 035 (szkielet, docieplenie, ściana dom-garaz) — nieader, „LULU”
- Płyty PIR z okładziną (izolacja spadkowa stropodachów) — zrygask z okładzinami
- Obróbki blacharskie (blacha powlekana); Stolarka — profile aluminiowe, antracyt; Rama boksu C: ruszt stalowy ocynkowany w okładzinie z blachy aluminiowej RAL 7016 (pusta w środku); Siat malowana proszkowo (dalsztrady, tygry) — zacementowanie
- Styroplan grafitowy EPS 031 (ETICS, NRO w systemie);
Styroplan podłogowy EPS 100-038 (pod jastycznym); Styroplan elastyczny EPS T (akustyczny, pod jastycznym) — zrygask „VVV”
- Polistyren ekstrudowany XPS 300 (pod płytą fundamentową, cokoł, izolacja obwodowa) — zrygask podłogowy
- Jastycznych cementowy CT-C25-F5 z węzownicą ogrzewania podłogowego — kropki
- Membrana dachowa TPO 1,5 mm, mocowana mechanicznie (hydroizolacja stropodachów); Hydroizolacja 2 x papa SBS (podkładowa + wierzchniego krycia, dach zielony) — pas czarno-biały
- Obróbki blacharskie (blacha powlekana); Stolarka — profile aluminiowe, antracyt; Rama boksu C: ruszt stalowy ocynkowany w okładzinie z blachy aluminiowej RAL 7016 (pusta w środku); Siat malowana proszkowo (dalsztrady, tygry) — zacementowanie
- Szkło (szyby zespolone); Ścianka szklana VSG 2 x 8 mm w ramie aluminiowej (wiatrołap / hol)
- Zelbet C25/30, B500SP (stropy, płyta fundamentowa, ściany);
Zelbet C30/37 XC4/XF1 (krawędzie płyt wysuniętych, atyki, belki) — 45° na przemian ciagle i przerywane
- Podbudowa nawierzchni (kruszywo)
- Membrana fasadowa wiatroizolacyjna UV-stabilna, czarna (sd = 0,02 m)
- Błoczek wapienno-piaskowy 12 cm, kl. 15 (ścianki działowe, licowy w klatce); Błoczek wapienno-piaskowy (silikat) 18 cm, kl. 20, gr. 1, na zaprawie cienkowarstwowej — kratka ukośna 45°/135°
- Paroizolacja bitumiczna z wkładką Al (na płycie stropodachów) — linia kreskowa cienka 3/1 po ciepłej stronie
- Podsyłka piaskowa zagęszczona (L s ≥ 0,98)
- Płyta gipsowo-kartonowa 12,5 mm (GKB / GKBi w łazienkach);
Podsyłka zewnętrzna: płyta włóknocementowa 12 mm na ruszcie, RAL 7016
- Q_g = 0,9
Q_g = 0,9

REW.		OPIS ZMIANY		DATA	
0		Wydanie — rysunek wygenerowany z modelu		2026-09-25	
PRACOWNIA PROJEKTOWA PRACOWNIA PROJEKTOWA — nazwa do uzupełnienia adres pracowni do uzupełnienia				STADIUM PT	BRANŻA ARCHITEKTURA (AR)
INWESTOR (do uzupełnienia)					
OBJEKT / NAZWA ZAMIERZENIA BUDOWLANEGO Budynek mieszkalny jednorodzinny wolnostojący „Dom LAMELA”					
ADRES / LOKALIZACJA (NR DZIAŁKI, OBRĘB, JEDN. EWIDENCYJNA) ul. Lipowa (fikcyjna), dz. nr ewid. 1234, obręb 0005 Przykładowo, gm. Przykładowo (fikcyjna)					KAT. OBIEKTU I
FUNKCJA		IMIĘ I NAZWISKO		SPECJALNOŚĆ, NR UPRAWNIENI	DATA
Projektant		[DO UZUPEŁNIENIA]		[DO UZUPEŁNIENIA]	
Projektant (wsp.)		[DO UZUPEŁNIENIA]		[DO UZUPEŁNIENIA]	
Sprawdzający		nie dotyczy (art. 20 ust. 3 pkt 2 PB)		—	
Opracował		[DO UZUPEŁNIENIA]		[DO UZUPEŁNIENIA]	
TYTUŁ RYSUNKU PRZEKROJE A-A I B-B					
SKALA 1:50	FORMAT 1130x420	DATA WYDANIA 2026-09-25	RODZAJ DOK. przekrój	NR RYSUNKU PT-AR-04	ARKUSZ 4/5
					REW. 0