






ELEWACJA POŁUDNIOWA (OGRODOWA) 1:50

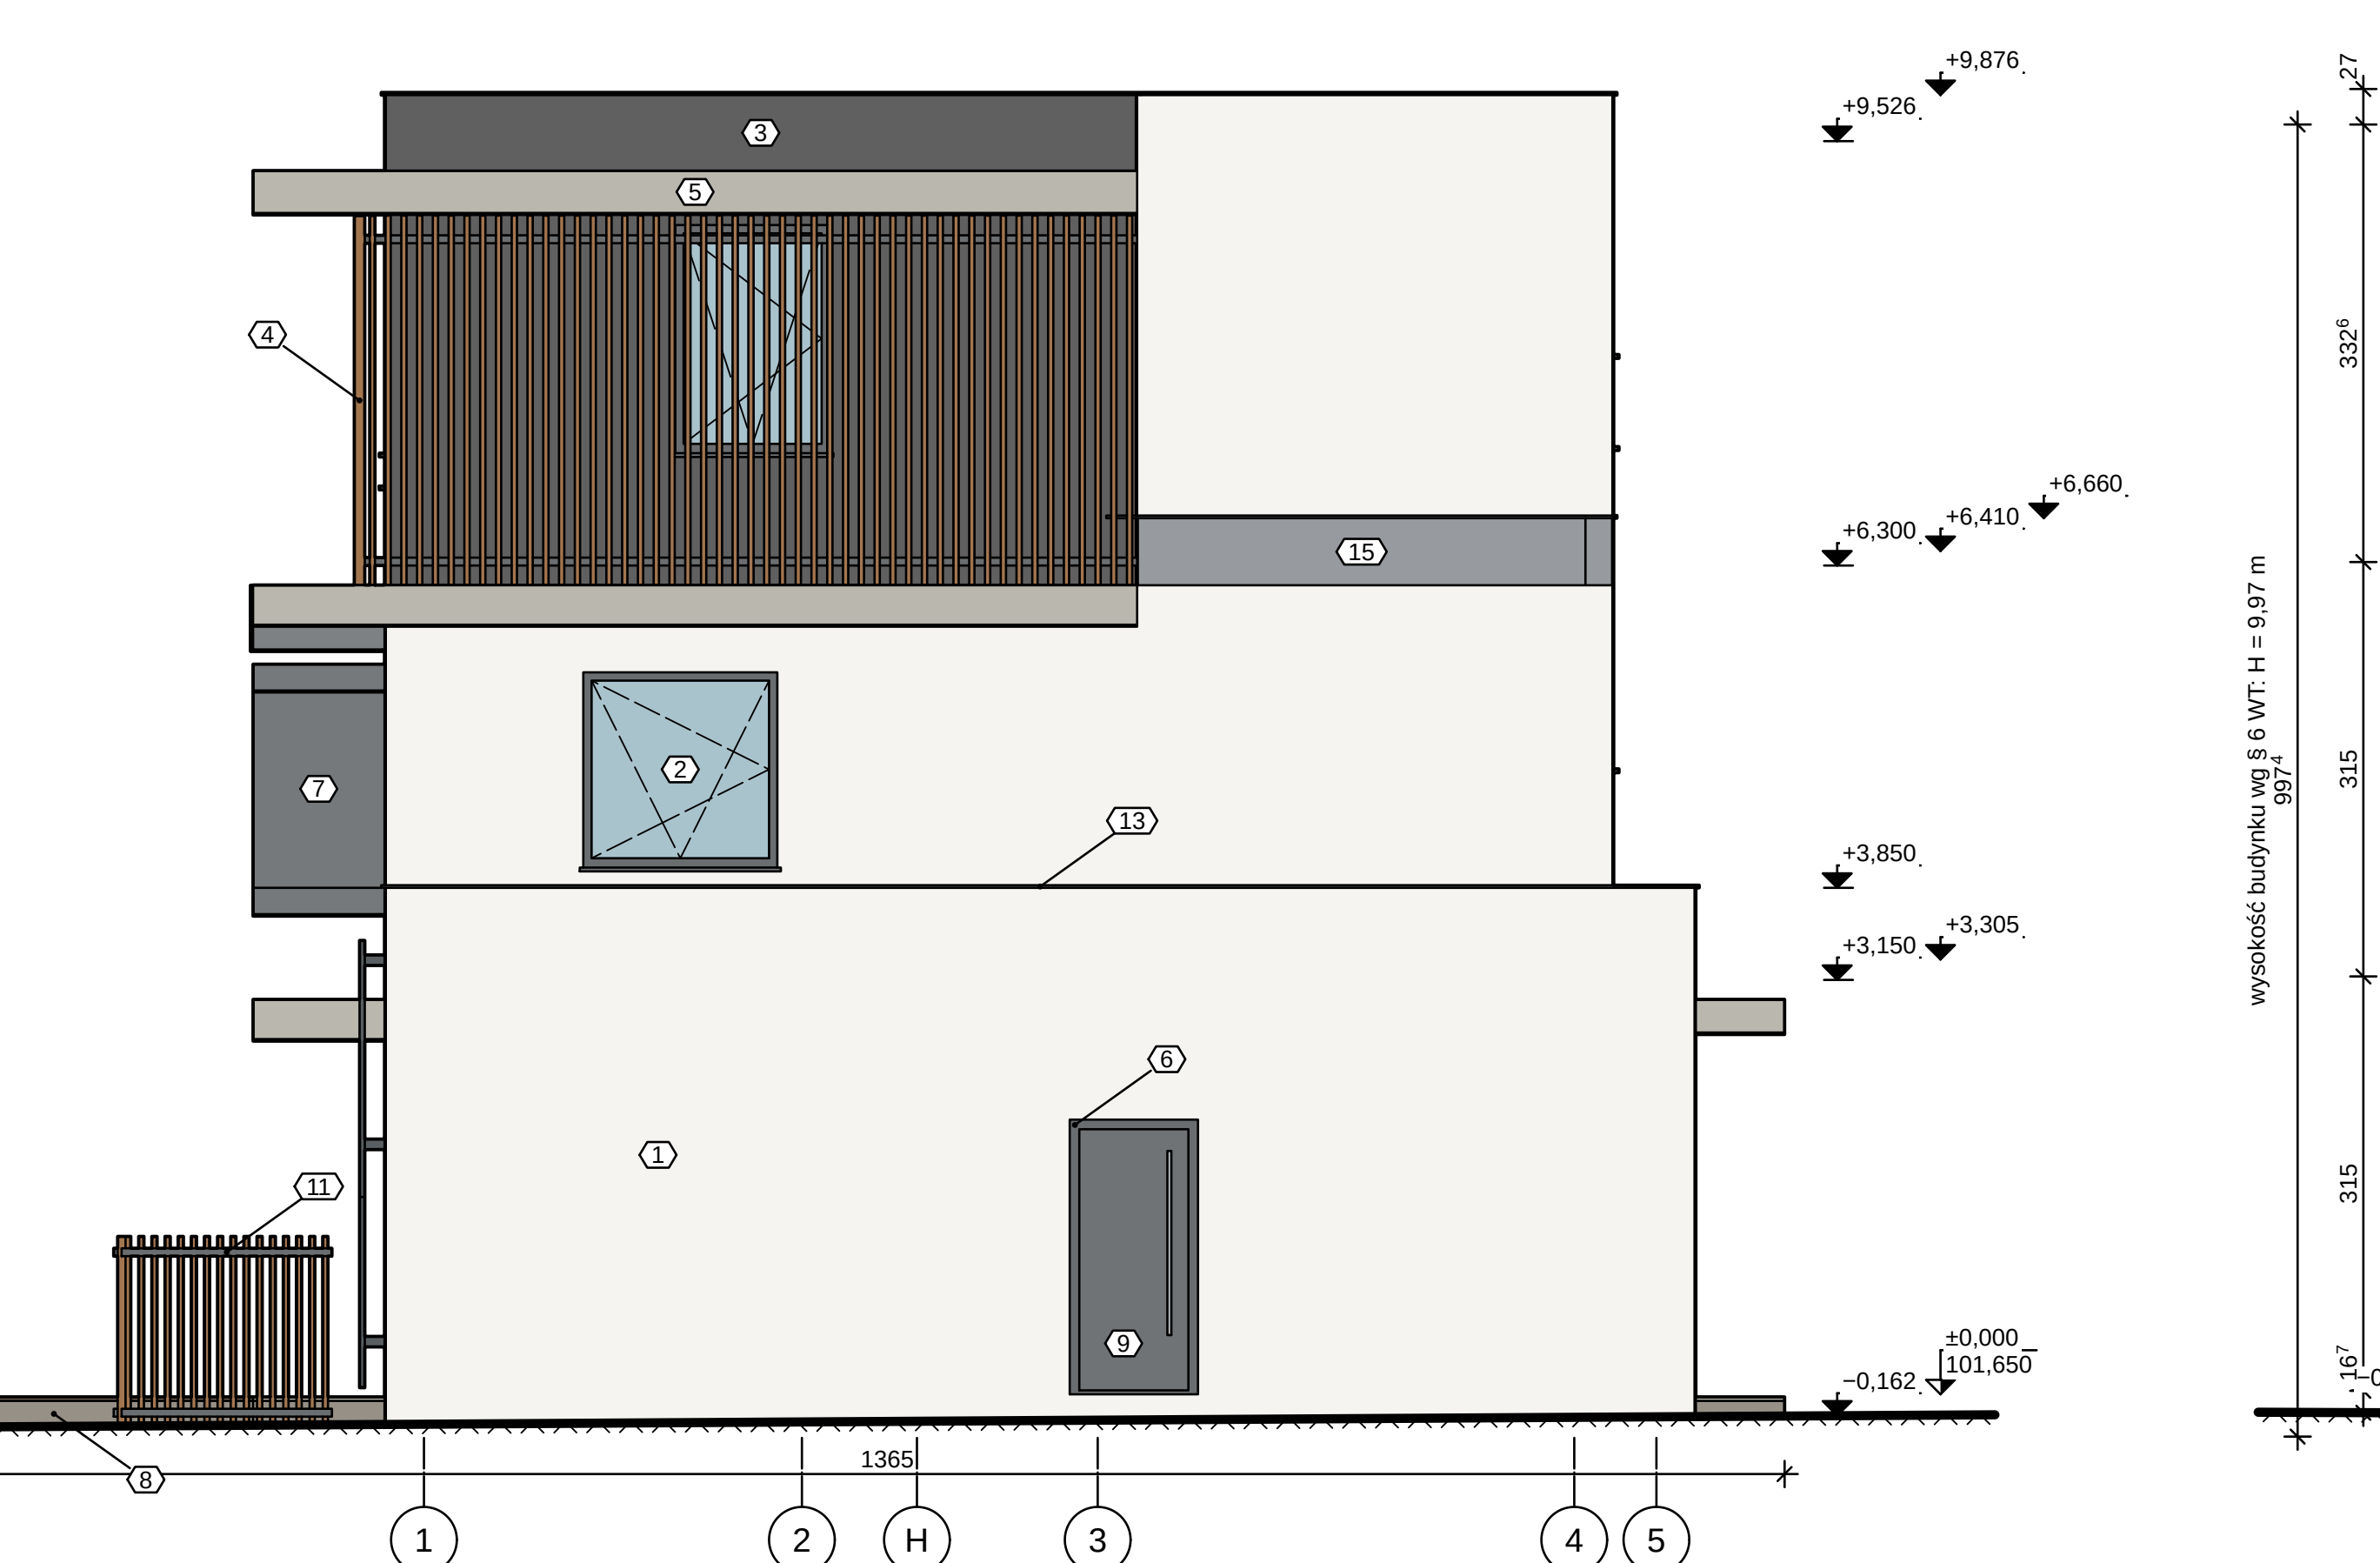

ELEWACJA WSCHODNIA 1:50

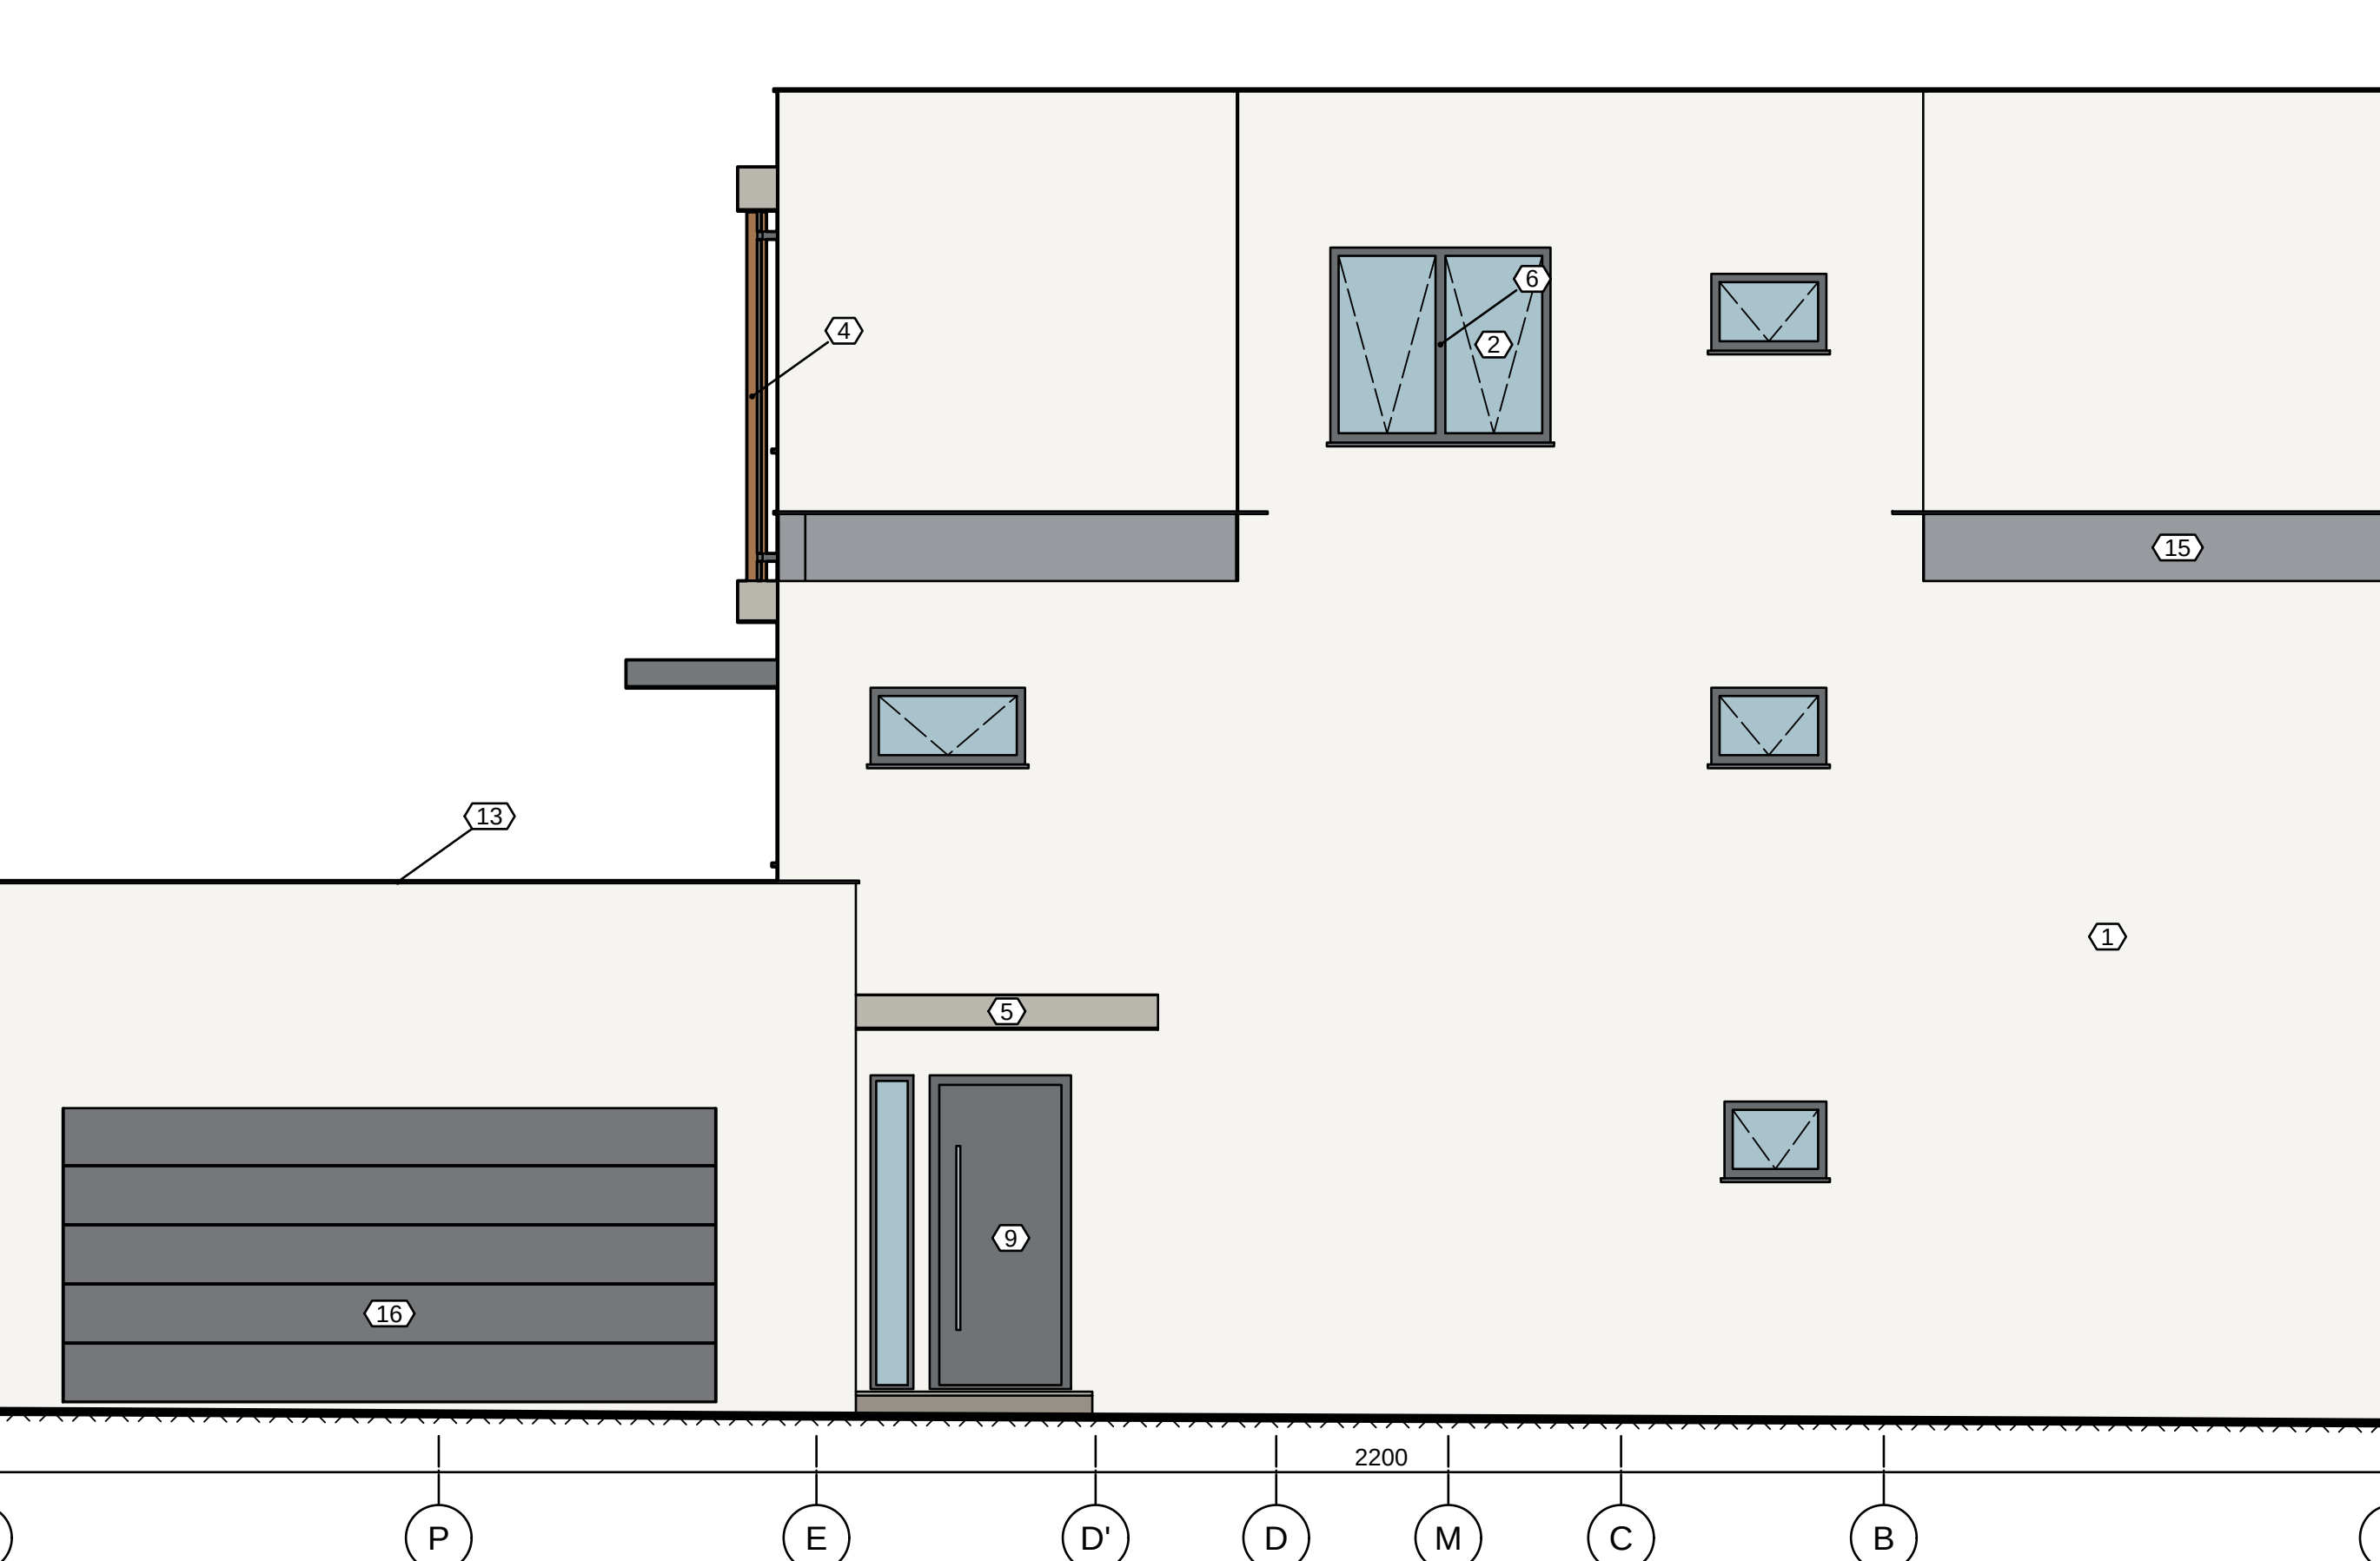

ELEWACJA PÓŁNOCNA (OD ULICY) 1:50

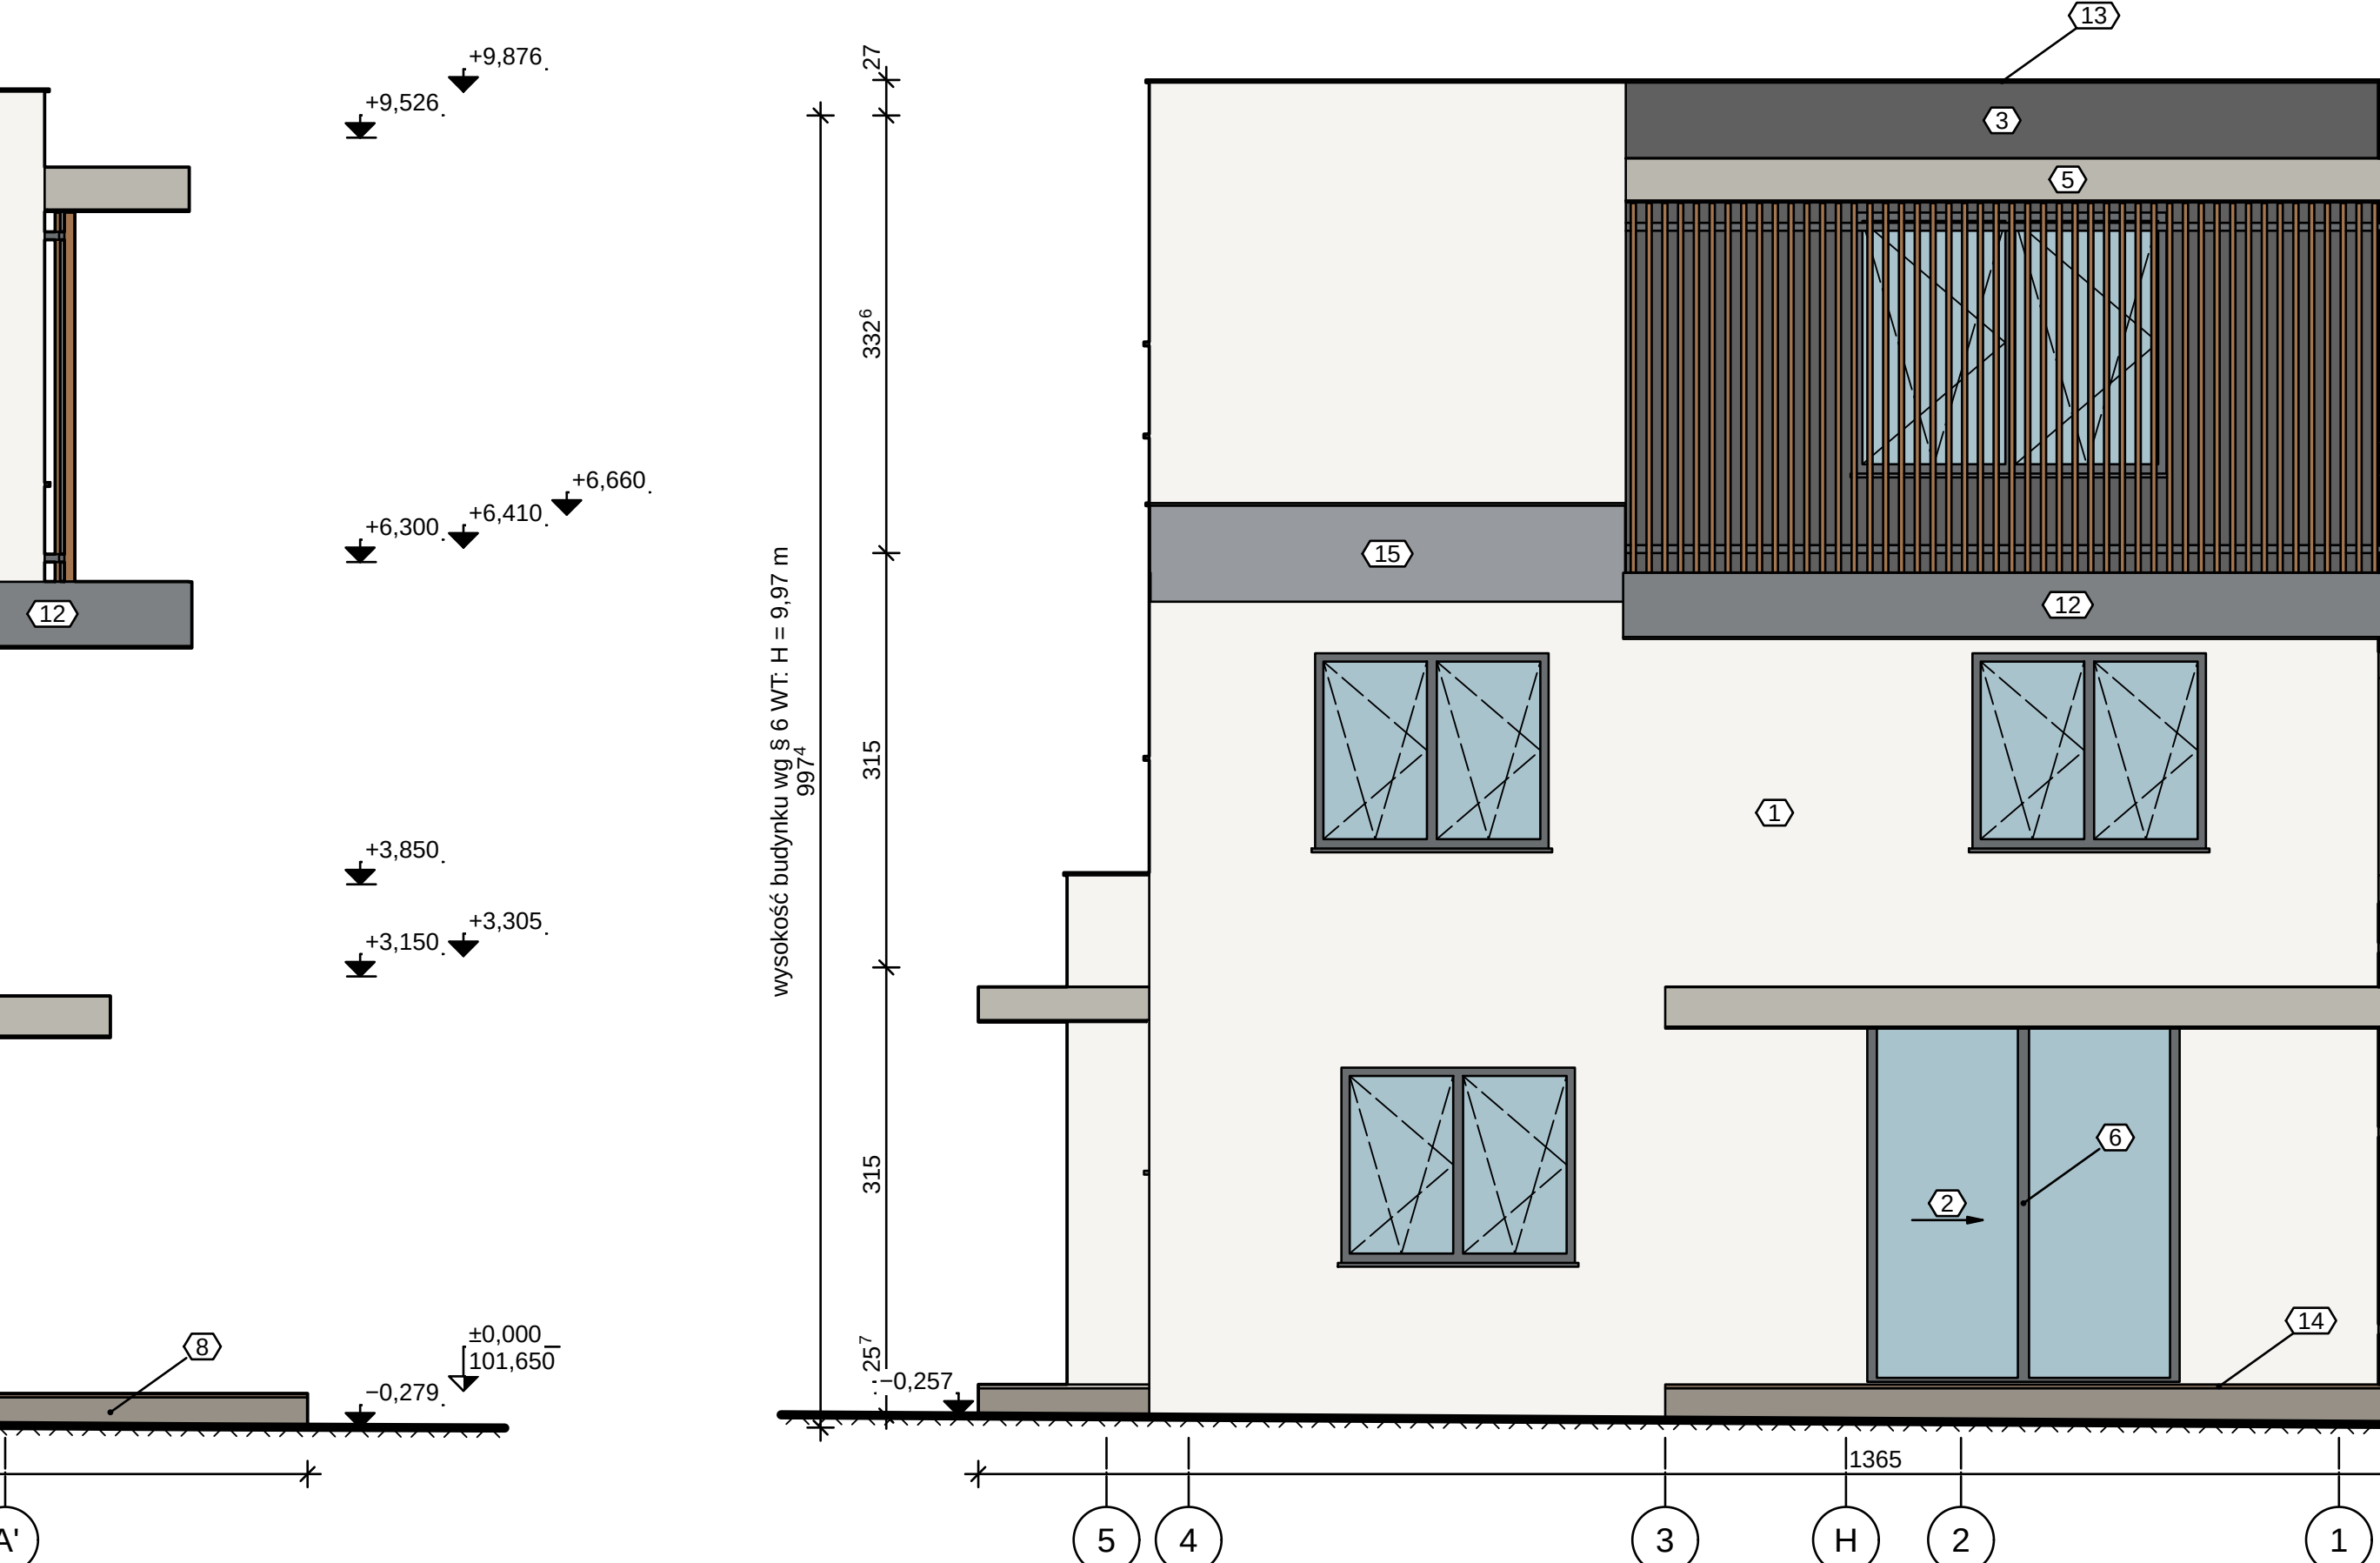

ELEWACJA ZACHODNIA 1:50

OBJAŚNIENIA I UWAGI (cd.)
6. Układ warstw przegród, stolarka, wykończenia, odwodnienie — część opisuwa PT-1 AR; węzły — detale PT-AR-D.
7. Rysunek wygenerowany automatycznie z modelu modelbudynki.yam (wersja 1.0, 2026-09-25) — generatory lamela.views.

KOLORYSTYKA I MATERIAŁY ELEWACJI	
1	ETICS: warstwa zbrojona + tynk silikonowy 1,5 mm (biały / jasnoszary NCS S 1500-N) [TYNK_SIL]
2	Szkle (szyby zespolone) [SZKLO]
3	Membrana fasadowa wiatroizolacyjna UV-stabilna, czarna (sd = 0,02 m) [MEMB_WIATR]
4	Lamele elewacyjne 40x80 mm, drewno termoodporne (klasa 1 trwałości), olejowane [DREWNO_TERMOC]
5	Żelbet C30/37 XC4/XF1 (krawędzie płyt wysuniętych, atyki, belki) [ZB_C30]
6	Stalarka — profile aluminiowe, antracy [RAMA_ALU]
7	Rama boku C: ruszt stalowy ocynkowany w okładzinie z blachy aluminiowej RAL 7016 (pusta w środku) [RAMA_C]
8	Podbudowa nawierzchni (kruszywo) [NAW_PODOBUDOWA]
9	Drzwi zewnętrzne, płycina aluminiowa [DRZWI_ZEWNI]
10	Stal S235 ocynkowana ognioowo, malowana proszkowo RAL 7016 — kratownica pręczy (pręty Ø12 w siatce 0,30 m, rama 40x40) [STAL_OCYNK]
11	Stal malowana proszkowo (balustrady, rygle) [STAL_BAL]
12	Podsufłak zewnętrzny: płyta włóknocementowa 12 mm na ruszcie, RAL 7016 [PODSUF]
13	Obróbki blacharskie (blacha powlekana) [OBROBKA_BLACH]
14	Deska tarasowa [NAW_DESKA]
15	Styropian graficzny EPS 031 (ETICS, NRO w systemie) [EPS031]
16	Brama garażowa segmentowa [BRAMA_GAR]

OBJAŚNIENIA I UWAGI
1. Wymiary w cm (mm w indeksie górnym, np. 24" = 24,5 cm), rzędne w m względem ±0,000 = 101,650 m n.p.m. (PL-EVRP2007-NH).
2. Rzędne: rdzina zaznaczony — poziom wykończenia, niezaznaczony — konstrukcji — poziom zaznaczony — poziom ±0,000 z rzędna bezwzględna (PN-B-01025).
3. Wysokość budynku wg § 6 WT: H = 9,97 m od terenu przy najniższym wejściu (-0,348) do wierzchu strzechy Dach D1 (+9,626) — H = 9,97 m (bez atyki).
4. Kolorystyka orientacyjna wg kolorów materiałów w modelu (do potwierdzenia w rzeczywistości).
5. Rysunek projektu technicznego (RPB § 24 pkt 1) wykonany z tego samego stanu modelu co rysunki PB-AR-xx projektu architektoniczno-budowlanego (tom I), stan modelu: SHA-256 42ac7a811873 (budynek, działka, instalacje, wyposażenie).

012345m				
DZIAŁKA 1:50				
OPIS ZMIANY		DATA		
Wydanie — rysunek wygenerowany z modelu		2026-09-25		
ADRES PRACOWNI PROJEKTOWA — nazwa do uzupełnienia		STADIUM PT		
STOR pracowni do uzupełnienia		BRANŻA ARCHITEKTURA (AR)		
(do uzupełnienia)				
OBJEKT / NAZWA ZAMIERZENIA BUDOWLANEGO				
Budynek mieszkalny jednorodzinny wolnostojący „Dom LAMELA”		KAT. OBJEKTU		
ADRES / LOKALIZACJA (NR DZIAŁKI, OBRĘB. JEJ. EWIDENCYJNA)				
ul. Lipowa (Kielce), dz. nr ewid. 1234, obręb. 0005 Przykładowo, gm. Przykładowo (Kielce)				
FUNKCJA	IMIE I NAZWISKO	SPECJALNOŚĆ, NR UPRAWNIEN	DATA	PODPIS
Projektant	[DO UZUPEŁNIENIA]	[DO UZUPEŁNIENIA]	[DO UZUPEŁNIENIA]	[DO UZUPEŁNIENIA]
Projektant (wsp.)	[DO UZUPEŁNIENIA]	[DO UZUPEŁNIENIA]	[DO UZUPEŁNIENIA]	[DO UZUPEŁNIENIA]
Sprawdzający	nie dotyczy (art. 20 ust. 3 pkt 2 PB)	—	[DO UZUPEŁNIENIA]	[DO UZUPEŁNIENIA]
Opracował	[DO UZUPEŁNIENIA]	[DO UZUPEŁNIENIA]	[DO UZUPEŁNIENIA]	[DO UZUPEŁNIENIA]
TYTUŁ RYSUNKU				
ELEWACJE				
SKALA	FORMAT	DATA WYDANIA	RODZAJ DOK.	NR RYSUNKU
1:50	2130x297	2026-09-25	elewacja	PT-AR-05
REW. 0				