


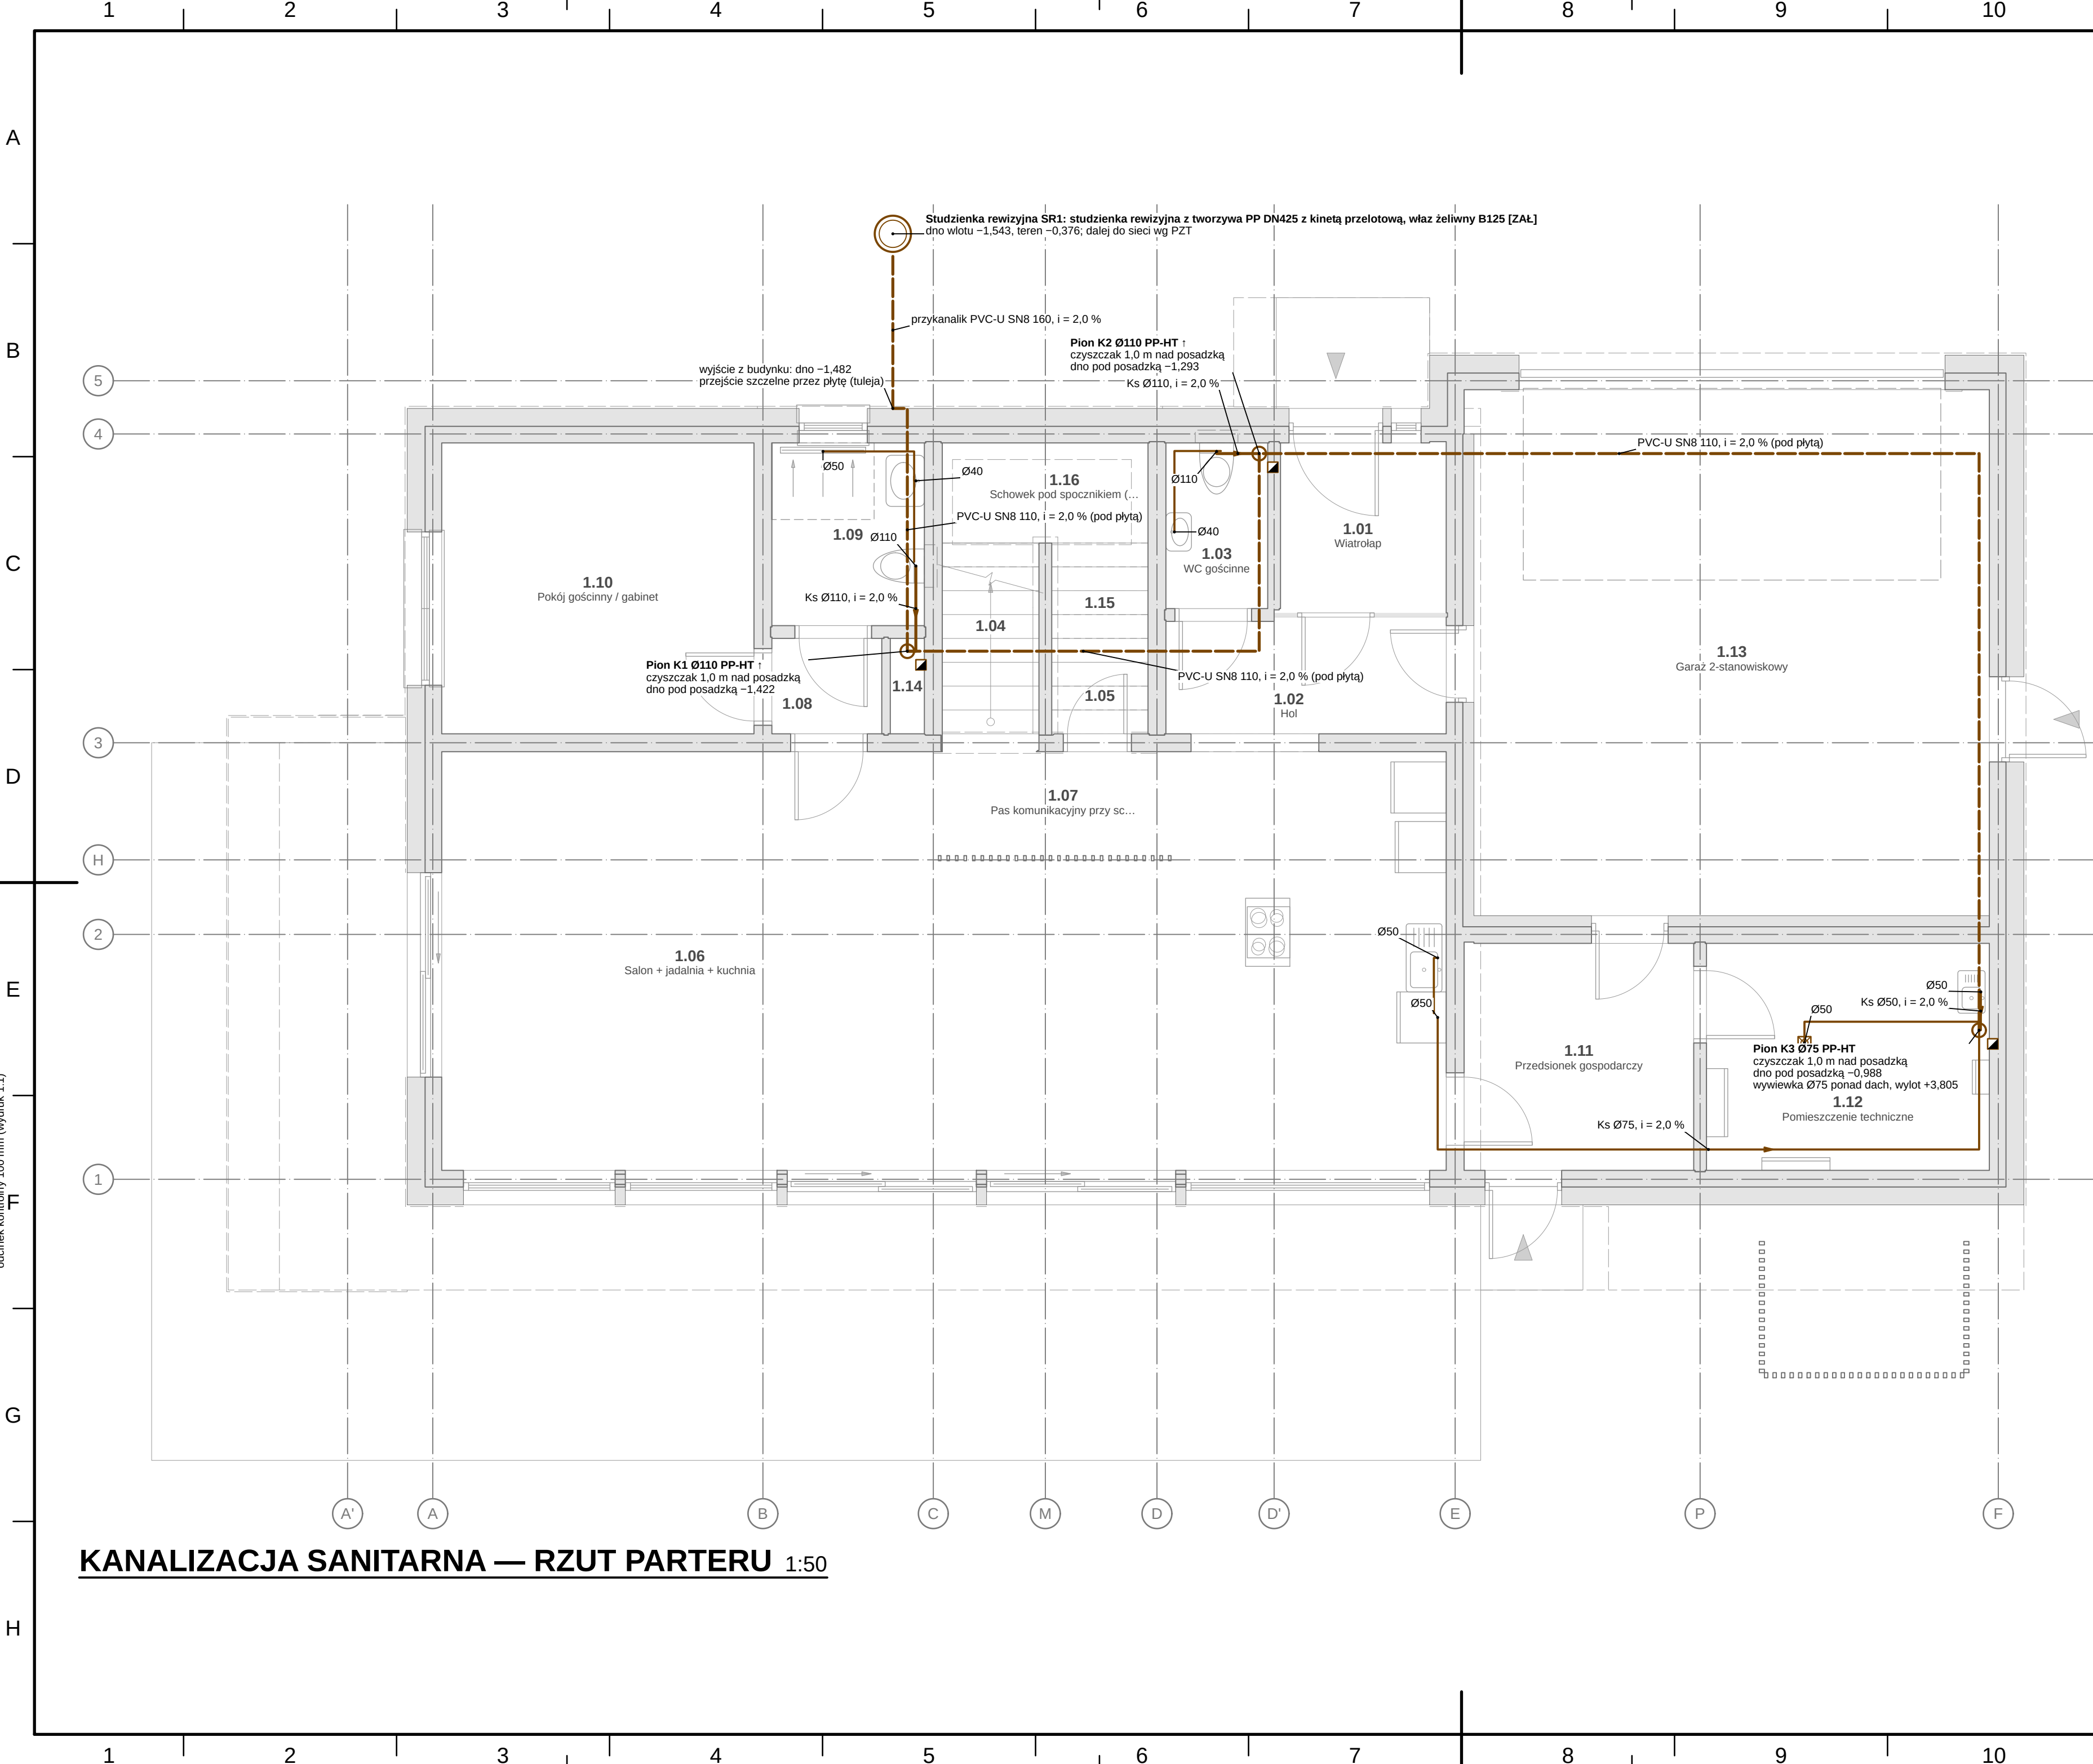

OZNACZENIA — LEGENDA SYMBOLI

Oznaczenia instalacji sanitarnych — praktyka branżowa (PN-B-01410, PN-B-01411, PN-B-01430 — normy wycofane, bez następcy); armatura i urządzenia wg PN-EN ISO 10628-2 / PN-EN ISO 14617; rodzaje powietrza wg PN-EN 16798-3 (ODA, SUP, ETA, EHA). Obowiązuje legenda na arkuszu.



	podkład architektoniczny (rzut AR — ściany przecięte, stolarka, wyposażenie) — linie cienkie szare		kierunek przepływu (spadek przewodu)
	Ks — kanalizacja sanitarna, podejścia i piony PP-HT (PN-EN 1451-1), średnica nominalna wg obliczeń; i — spadek		wpust podłogowy z syfonem (zamknięcie wodne ≥ 50 mm)
	pion kanalizacyjny; i — prowadzony wyżej, i — z kondygnacji wyżej/niżej		przewody odpływowe pod płytą fundamentową i przykanalik PVC-U SN8 (PN-EN 1401-1) — linia kreskowa
	czyszczak (rewizja) na pionie, 1,0 m nad posadzką, z drzwiczkami rewizyjnymi		studzienka rewizyjna (tworzywowa DN425)

WYNIKI OBLICZEŃ — KANALIZACJA (PN-EN 12056-2)

Odcinek	Opis	DN	L [m]	ΣDU	Q [l/s]	i [%]
PZ_0.09	podejście zbiorcze w pom. 0.09 → pion K1	Ø110	3,43	3,1	2,00	2,0
PZ_1.05	podejście zbiorcze w pom. 1.05 → pion K1	Ø110	3,14	3,3	2,00	2,0
PZ_2.04	podejście zbiorcze w pom. 2.04 → pion K1	Ø110	3,14	3,1	2,00	2,0
PZ_0.03	podejście zbiorcze w pom. 0.03 → pion K2	Ø110	2,01	2,5	2,00	2,0
PZ_1.07	podejście zbiorcze w pom. 1.07 → pion K2	Ø110	3,21	3,1	2,00	2,0
PZ_1.08	podejście zbiorcze w pom. 1.08 → pion K2	Ø75	2,52	2,3	1,50	2,0
PZ_0.06	podejście zbiorcze w pom. 0.06 → pion K3	Ø75	7,10	1,6	0,80	2,0
PZ_0.12	podejście zbiorcze w pom. 0.12 → pion K3	Ø50	2,30	1,6	0,80	2,0
PION_K1	pion K1 (P0, P1, P2)	Ø110	7,90	9,5	2,00	—
PION_K2	pion K2 (P0, P1)	Ø110	4,75	7,9	2,00	—
PION_K3	pion K3 (P0)	Ø75	1,60	3,2	0,89	—
KOL1	przewód odpływowy pod posadzką; pion K3 → wł	Ø110	15,22	3,2	0,89	2,0
KOL2	przewód odpływowy pod posadzką; pion K2 → wł	Ø110	6,45	11,1	2,00	2,0
KOL3	przewód odpływowy pod posadzką; pion K1 → wy	Ø110	3,02	20,6	2,27	2,0
PRZ	przykanalik: budynek → studzienka rewizyjna	Ø160	3,05	20,6	2,27	2,0

OBJAŚNIENIA I UWAGI

- Średnice przewodów w mm (d, z×s — rury wielowarstwowe, Ø/DN — kanalizacja, kanały wentylacyjne), przekroje żył w mm², odległości i rzędne w m; ±0,000 = 101,650 m n.p.m. (PL-EVRF2007-NH).
- Rysunki instalacji na podkładzie rzutów architektury (PB-AR); podkład — linie cienkie szare (warstwy I-PODKŁAD*).
- Kanalizacja sanitarna wg PN-EN 12056-1, -2 (system I), -5 i WT § 122–124; obliczenia: lamela.obliczenia.sanitarn.kanalizacja (K = 0,5; ΣDU, Q_{ww}, napełnienia, wentylacja pionów).
- Podejścia i piony: PP-HT (PN-EN 1451-1) lub równoważne; pod płytą i przykanalik: PVC-U SN8 lity (PN-EN 1401-1). Spadki podejść ≥ 2 ‰, przewodów pod płytą 2 ‰ (≥ DN1100).
- Trasy podejść wyznaczono algorytmicznie (ortogonalnie, przy ścianach, do pionów w szachcie SI) — średnice i spadki z obliczeń; przebieg do weryfikacji na budowie.
- Czyszczaki na pionach w najniższej kondygnacji 1,0 m nad posadzką; rewizje w studzience SR1. Piony w szachcie izolowane akustycznie, przejścia przez stropy z opaskami/kolierzami ppoż. wg klasy stropu.
- Odpływ skroplin PC i zmywarki przez syfon; wpusty podłogowe z zamknięciem wodnym ≥ 50 mm.
- ΣDU = 20,6 l/s, Q_{ww} = 2,27 l/s; przykanalik DN150 i=0.02.
- Rysunek wygenerowany automatycznie z modelu model/budynki.yaml (wersja 1.0, 2026-09-25) — generatory lamela.views.

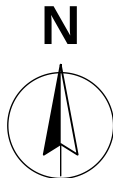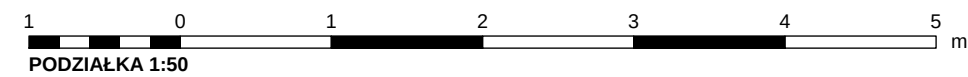

REW.	OPIS ZMIANY			DATA	
0	Wydanie — rysunek wygenerowany z modelu			2026-09-25	
PRACOWNIA PROJEKTOWA PRACOWNIA PROJEKTOWA — nazwa do uzupełnienia			STADIUM PT	BRANŻA INSTALACJE SANITARNE (IS)	
adres pracowni do uzupełnienia					
INWESTOR (do uzupełnienia)					
OBIEKT / NAZWA ZAMIERZENIA BUDOWLANEGO					
Budynek mieszkalny jednorodzinny wolnostojący „Dom LAMELA”					
ADRES / LOKALIZACJA (NR DZIAŁKI, OBREB, JEDN. EWIDENCYJNA)				KAT. OBIEKTU	
ul. Lipowa (fikcyjna), dz. nr ewid. 123/4, obręb 0005 Przykładowo, gm. Przykładowo (fikcyjna)				I	
FUNKCJA	IMIĘ I NAZWISKO		SPECJALNOŚĆ, NR UPRAWNIENI	DATA	PODPIS
Projektant	[DO UZUPEŁNIENIA]		[DO UZUPEŁNIENIA]		
Projektant (wsp.)	[DO UZUPEŁNIENIA]		[DO UZUPEŁNIENIA]		
Sprawdzający	nie dotyczy (art. 20 ust. 3 pkt 2 PB)		—		
Opracował	[DO UZUPEŁNIENIA]		[DO UZUPEŁNIENIA]		
TYTUŁ RYSUNKU					
KANALIZACJA SANITARNA — RZUT PARTERU					
SKALA	FORMAT	DATA WYDANIA	RODZAJ DOK.	NR RYSUNKU	ARKUSZ
1:50	710×420	2026-09-25	rzut instalacji	PT-IS-03	3/11
REW.					0