



[illegible]

Oznaczenia instalacji sanitarnych — praktyka branżowa (PN-B-01410, PN-B-01411, PN-B-01430 — normy wycofane, bez następcy); armatura i urządzenia wg PN-EN ISO 10628-2 / PN-EN ISO 14617; rodzaje powietrza wg PN-EN 16798-3 (ODA, SUP, ETA, EHA). Obowiązuje legenda na arkuszu.

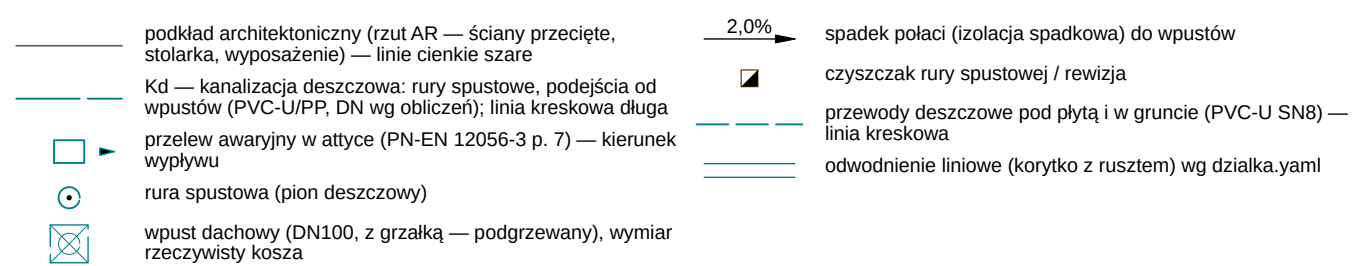

Pole	Type	A [m ²]	Q [l/s]	wpusztów	Q_wp [l/s]	Q_przel. [l/s]	h_spiętrz. [cm]
D1	plaski	87.4	4.02	2	9.00	22.41	5.0
D2	plaski	12.5	0.58	1	4.50	11.21	2.2
D3	plaski	11.2	0.51	1	4.50	11.21	2.0
D4	zielony	59.1	3.78	2	9.00	22.41	4.8
PL-E	taras	23.7	1.09	2	3.40	8.91	2.0
PL-DA	taras	3.0	0.14	1	1.70	5.94	0.6
PL-2	taras	23.0	1.06	2	3.40	11.89	1.6
PL-3	taras	23.0	1.06	2	3.40	11.89	1.6
PL-D	wspornik	6.1	0.28	1	1.70	5.94	1.0

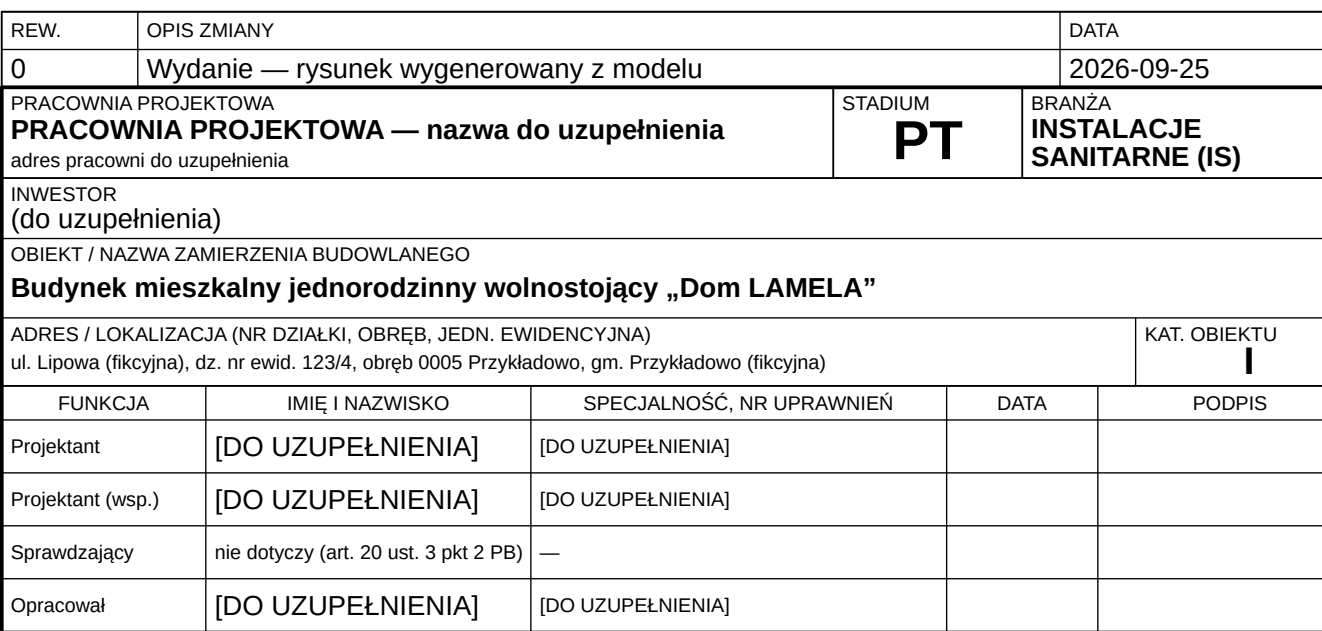

SKALA 1:50	FORMAT 590×841	DATA WYDANIA 2026-09-25	RODZAJ DOK. rzut instalacji	NR RYSUNKU PT-IS-05	ARKUSZ 5/11	REW. 0
----------------------	-------------------	----------------------------	--------------------------------	-------------------------------	----------------	------------------