


odcinek kontroly 100 mm (wydruk 1:1)

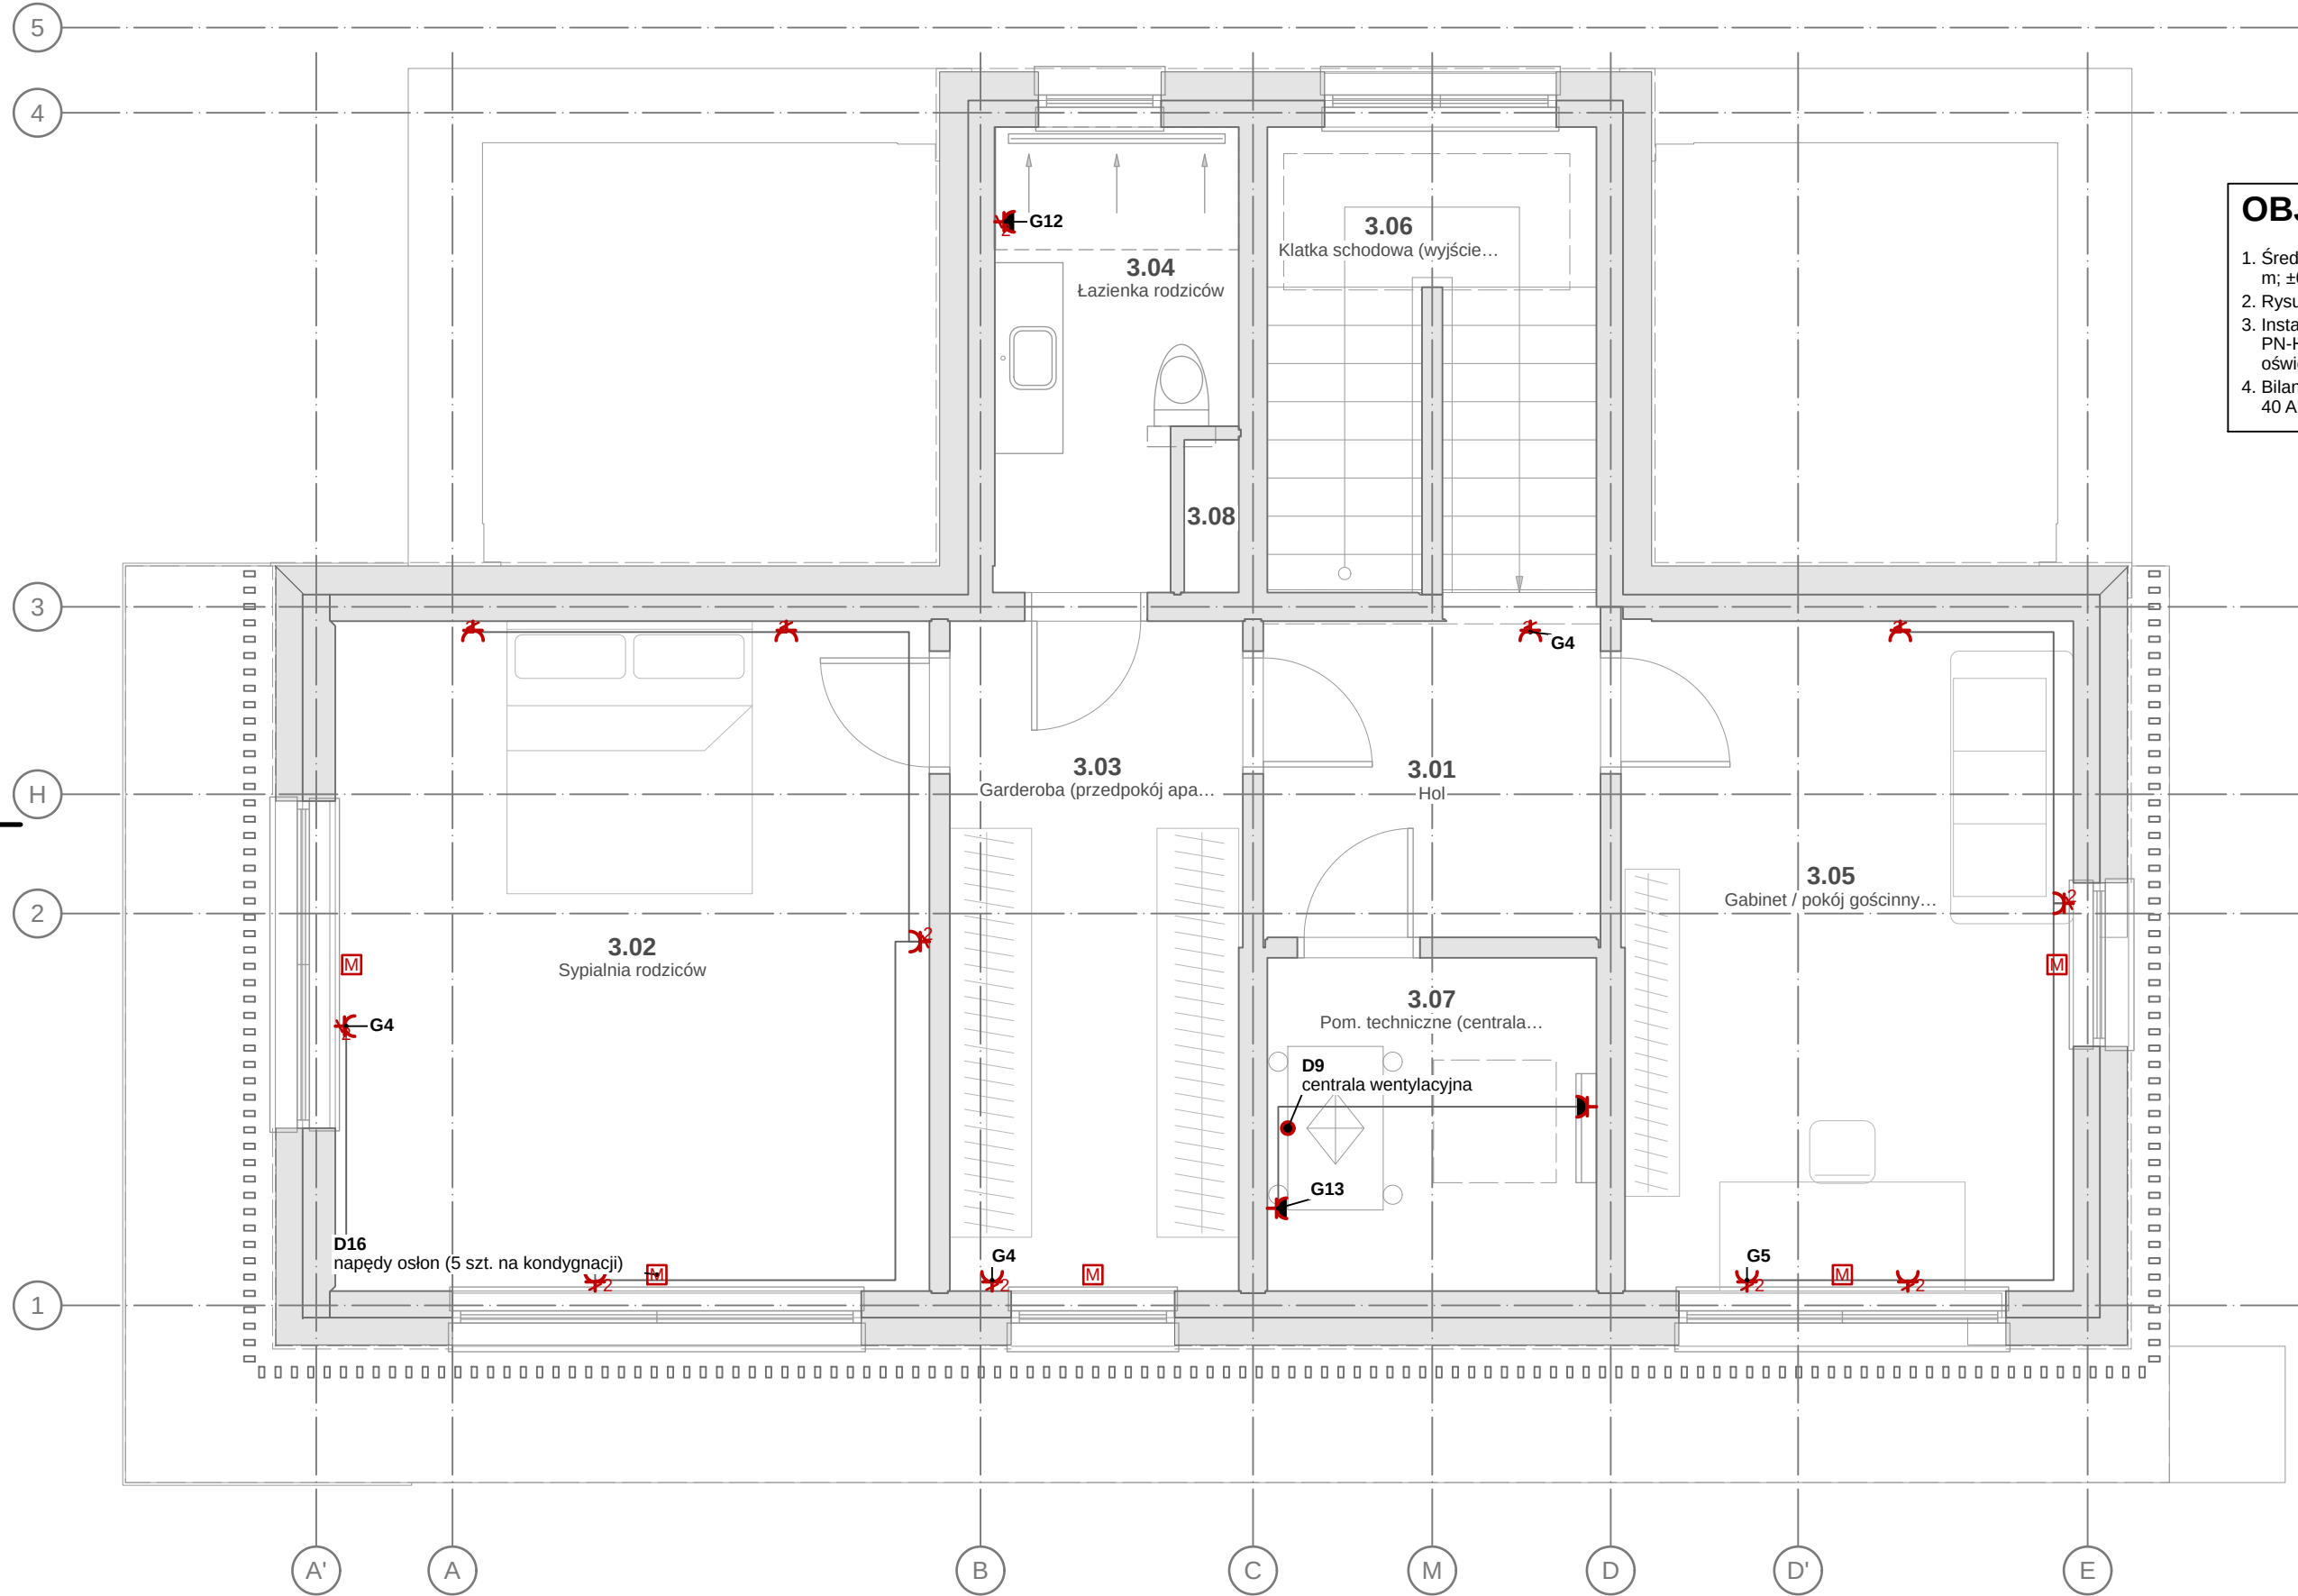

Gniazda i zasilanie urządzeń — rzut II piętra 1:50

### Objaśnienia i uwagi

- Średnice przewodów w mm (d\_xs — rury wielowarstwowe, Ø/DN — kanalizacja, kanały wentylacyjne), przekroje żył w mm², odległości i rzędne w m; ±0,000 = 101,650 m n.p.m. (PL-EVRF2007-NH).
- Rysunki instalacji na podkładzie rzutów architektury (PB-AR); podkład — linie cienkie szare (warstwy I-PODKŁAD\*).
- Instalacja gniazd wtyczkowych i zasilania urządzeń wg PN-HD 60364-4-41 (samoczynne wyłączenie, RCD 30 mA dla gniazd ≤ 32 A — p. 411.3.3), PN-HD 60364-5-52 (przewody), PN-HD 60364-7-701 (łazienki), PN-HD 60364-7-722 (ładowanie EV); WT § 180–188 (obwody gniazd oddzielne od oświetlenia, gniazda ze stykiem ochronnym).
- Bilans mocy (lamela.obliczenia.elektryka.bilans): P\_inst = 71,3 kW, P\_szczyt z DLM = 24,8 kW ≤ P\_przył = 27 kW, zabezpieczenie przedlicznikowe 40 A.

### Oznaczenia — legenda symboli

Symbol instalacji elektrycznych wg IEC 60617 (baza IEC; PN-EN 60617 — wycofana, stosowana jako praktyka branżowa) i PN-EN ISO 14617; oznaczenia teletechniczne — praktyka branżowa. Obowiązuje legenda na arkuszu.

- podkład architektoniczny (rzut AR — ściany przecięte, stolarka, wyposażenie) — linie cienkie szare

przewody obwodów gniazd YDYp 3×2,5 (5×2,5 — 3f) — połączenia punktów (przebieg schematyczny w tynku / w posadzce)

gniazdo wtyczkowe podwójne ze stykiem ochronnym, h = 0,30 m (kuchnia nad blatem 1,10 m)

gniazdo bryzgoszczelne IP44 (łazienki h = 1,20 m, garaż, pom. techniczne, zewnętrzne)

wypust / puszka przyłączeniowa urządzenia zasilanego na stałe (opis: obwód, urządzenie, moc)


M — zasilanie napędu osłony przeciwsłonecznej (żaluzja/screen) przy oknie

### Obwody na arkuszu (lamela.obliczenia.elektryka.obwody)

| Obw. | Odbiorniki   | Zab. | Przewód    | L [m] | ΔU [%] | Faza | RCD              |
|------|---|------|------------|-------|--------|------|------------------|
| G4   | Gniazda P2: 2.02 Sypialnia rodziców, 2.03 Garderoba (przedpokój apartamentu), 2.08 Szacht instalacyjny SI, 2.06 Klatka schodowa (wyjście z biegu 2, pustka), 2.01 Hol | B16  | YDYp 3×2,5 | 22,3  | 2,96   | L1   | RCBO typ A 30 mA |
| G5   | Gniazda P2: 2.05 Gabinet / pokój gościnny   | B16  | YDYp 3×2,5 | 17,1  | 2,35   | L3   | RCBO typ A 30 mA |
| G12  | Gniazda łazienki (2.04 łazienka rodziców)   | B16  | YDYp 3×4   | 29,0  | 2,40   | L1   | RCBO typ A 30 mA |
| G13  | Gniazda garażu / pom. technicznego (IP44)   | B16  | YDYp 3×2,5 | 5,5   | 1,01   | L2   | RCBO typ A 30 mA |
| D9   | Rekuperator (V ≈ 365 m³/h)   | B10  | YDYp 3×1,5 | 20,5  | 0,47   | L2   | RCBO typ A 30 mA |
| D16  | Napędy osłon przeciwsłonecznych (19 szt.)   | B10  | YDYp 3×1,5 | 3,0   | 0,66   | L2   | RCBO typ A 30 mA |

### Objaśnienia i uwagi (cd.)

- Liczbę i rozmieszczenie gniazd wyznaczono algorytmicznie (praktyka branżowa, DIN 18015-2): przy łóżkach, biurkach, sofach, nad blatem kuchennym co ok. 1,1 m, przy umywalkach (poza strefami 0–2), pozostałe równomiernie wzdłuż ścian bez otworów; urządzenia stałe — wypusty/gniazda dedykowane wg obwodów D.
- Wysokości montażu (od posadzki): gniazda 0,30 m; nad blatem 1,10 m; łazienki 1,20 m (IP44); garaż, pom. techniczne 1,10 m (IP44); łączniki 1,10 m.
- Rysunek wygenerowany automatycznie z modelu model/budynek.yaml (wersja 1.0, 2026-09-25) — generatory lamela.views.

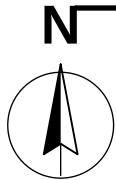

|   |                                         |                            |                                |                                       |
|---|-----------------------------------------|----------------------------|--------------------------------|---------------------------------------|
| REW.   | OPIS ZMIANY                             |                            | DATA                           |                                       |
| 0   | Wydanie — rysunek wygenerowany z modelu |                            | 2026-09-25                     |                                       |
| PRACOWNIA PROJEKTOWA<br>PRACOWNIA PROJEKTOWA — nazwa do uzupełnienia<br>adres pracowni do uzupełnienia                                                      |                                         |                            | STADIUM<br>PT                  | BRANŻA<br>INSTALACJE ELEKTRYCZNE (IE) |
| INWESTOR<br>(do uzupełnienia)   |                                         |                            |                                |                                       |
| OBIEKT / NAZWA ZAMIERZENIA BUDOWLANEGO<br>Budynek mieszkalny jednorodzinny wolnostojący „Dom LAMELA”                                                        |                                         |                            |                                |                                       |
| ADRES / LOKALIZACJA (NR DZIAŁKI, OBRĘB, JEDN. EWIDENCYJNA)<br>ul. Lipowa (fikcyjna), dz. nr ewid. 123/4, obręb 0005 Przykładowo, gm. Przykładowo (fikcyjna) |                                         |                            |                                | KAT. OBIEKTU<br>I                     |
| FUNKCJA   | IMIĘ I NAZWISKO                         | SPECJALNOŚĆ, NR UPRAWNIEŃ  | DATA                           | PODPIS                                |
| Projektant   | [DO UZUPEŁNIENIA]                       | [DO UZUPEŁNIENIA]          |                                |                                       |
| Projektant (wsp.)   | [DO UZUPEŁNIENIA]                       | [DO UZUPEŁNIENIA]          |                                |                                       |
| Sprawdzający   | nie dotyczy (art. 20 ust. 3 pkt 2 PB)   | —                          |                                |                                       |
| Opracował   | [DO UZUPEŁNIENIA]                       | [DO UZUPEŁNIENIA]          |                                |                                       |
| TYTUŁ RYSUNKU<br>GNIAZDA I ZASILANIE URZĄDZEŃ — RZUT II PIĘTRA                                                                                              |                                         |                            |                                |                                       |
| SKALA<br>1:50   | FORMAT<br>730×297                       | DATA WYDANIA<br>2026-09-25 | RODZAJ DOK.<br>rzut instalacji | NR RYSUNKU<br>PT-IE-06                |
|   |                                         |                            | ARKUSZ<br>6/14                 | REW.<br>0                             |