

TOM RYSUNKÓW ARCHITEKTURY — WIDOKI Z MOD

Lp.	Nr rys.	Tytuł rysunku	Skala	Format
1	PB-AR-01	RZUT PARTERU	1:50	A1
2	PB-AR-02	RZUT I PIĘTRA	1:50	A3×3
3	PB-AR-03	RZUT II PIĘTRA	1:50	A3×3
4	PB-AR-04	RZUT DACHU	1:50	A2×3
5	PB-AR-05	PRZEKRÓJ A-A	1:50	A3×3
6	PB-AR-06	PRZEKRÓJ B-B	1:50	A3×3
7	PB-AR-07	ELEWACJA POŁUDNIOWA (OGRODOWA)	1:50	A3×3
8	PB-AR-08	ELEWACJA PÓŁNOCNA (OD ULICY)	1:50	A3×3
9	PB-AR-09	ELEWACJA WSCHODNIA	1:50	A2
10	PB-AR-10	ELEWACJA ZACHODNIA	1:50	A2

PRACOWNIA PROJEKTOWA PRACOWNIA PROJEKTOWA — nazwa do uzupełnienia		STADIUM PB	BRANŻA ARCHITEKTURA (AR)			
INWESTOR (do uzupełnienia)						
OBIEKT / NAZWA ZAMIERZENIA BUDOWLANEGO Budynek mieszkalny jednorodzinny wolnostojący „Dom LAMELA”						
ADRES / LOKALIZACJA (NR DZIAŁKI, OBRĘB, JEDN. EWIDENCYJNA) ul. Lipowa (fikcyjna), dz. nr ewid. 123/4, obręb 0005 Przykładowo, gm. Przykładowo (fikcyjna)				KAT. OBIEKTU I		
FUNKCJA	IMIĘ I NAZWISKO	SPECJALNOŚĆ, NR UPRAWNIEŃ	DATA	PODPIS		
Projektant						
Projektant (wsp.)						
Sprawdzający						
Opracował						
TYTUŁ RYSUNKU SPIS RYSUNKÓW						
SKALA —	FORMAT A4	DATA WYDANIA 2026-09-25	RODZAJ DOK. spis	NR RYSUNKU PB-AR-00	ARKUSZ —	REW.

odcinek kontury 100 mm (wydruk 1:1)


RZUT PARTERU 1:50

ZESTAWIENIE POMIESZCZEŃ					
Nr	Nazwa pomieszczenia	Posadzka	Kat.	Wys. [m]	Pow. [m²]
1.06	Salon + jadalnia + kuchnia	Deska warstwowa dębowa 15 mm, klejona na podst.	podst.	2,77	54,44
1.13	Garaż 2-stanowiskowy	Posadzka żywiczna epoksydowa antypoślizgowa (garaż)	garaż	2,76	37,42
1.10	Pokój gościnny / gabinet	Deska warstwowa dębowa 15 mm, klejona na podst.	podst.	2,77	12,52
1.12	Pomieszczenie techniczne	Płytki gresowe 60×120 na kleju C2TE S1 techn.	podst.	2,76	8,85
1.11	Przedśionek gospodarczy	Płytki gresowe 60×120 na kleju C2TE S1 ruchu	ruchu	2,76	7,18
1.05	Śpiżarnia (pod schodami)	Płytki gresowe 60×120 na kleju C2TE S1 pomoc.	pomoc.	1,90	5,40
1.02	Hol	Płytki gresowe 60×120 na kleju C2TE S1 ruchu	ruchu	2,77	4,44
1.01	Wiatrołap	Płytki gresowe 60×120 na kleju C2TE S1 ruchu	ruchu	2,77	3,89
1.09	Łazienka gościnna (natrysk)	Płytki gresowe 60×120 na kleju C2TE S1 pomoc.	pomoc.	2,77	3,84
1.07	Pas komunikacyjny przy schodach	Deska warstwowa dębowa 15 mm, klejona na podst.	podst.	2,77	3,51
1.04	Klatka schodowa	Deska warstwowa dębowa 15 mm, klejona na podst.	podst.	2,77	2,82
1.03	WC gościnne	Płytki gresowe 60×120 na kleju C2TE S1 pomoc.	pomoc.	2,77	2,32
1.08	Przedpokój gościnny	Deska warstwowa dębowa 15 mm, klejona na podst.	podst.	2,77	1,44
RAZEM powierzchnia netto					148,07
w tym użytkowa (podst. + pomoc.)					115,94


OZNACZENIA MATERIAŁÓW (PN-B-01030 + przyjęte)	
	Włna mineralna 035 (szkielet, docieplenia, ściana dom-garaż)
	Styropian grafityowy EPS 031 (ETICS, NRO w systemie) — zygzak "VVV"
	Błoczek wapienno-piaskowy 12 cm, kl. 15 (ścianki działowe, liczy w klatce); Błoczek wapienno-piaskowy (słiska) 13 cm, kl. 20, gr. 1. na zaprawie cienkowarstwowej — kratka ukośna 45°/135°
	Ścianka szklana VSG 2 x 8 mm w ramie aluminiowej (wiatrołap / hol)
	Żelbet C25/30, B500SP (stropy, płyta fundamentowa, ściany) — 45° na przeniam ciagle i przerywane

OZNACZENIA LINII	
	elementy nad płaszczyzną cięcia (obrys płyt, wsporników, brył wyższych kondygnacji)
	elementy poniżej płaszczyzny cięcia (widok z góry)
	osie konstrukcyjne; linia punktowa z pogrubionymi końcami — ślad przekroju

OBJAŚNIENIA I UWAGI	
1.	Wymiary w cm (mm w indeksie górnym, np. 24 ^o = 24,5 cm), rzędne w m względem ±0,000 = 101,650 m n.p.m. (PL-EVRF2007-NH).
2.	Rzuty: płaszczyzna cięcia +1,10 m nad posadzką kondygnacji. Linia kreskową — elementy nad płaszczyzną cięcia (obrys płyt i wsporników, brył wyższych kondygnacji, otwory w stropie nad, belki); linia cienią — elementy poniżej (widok).
3.	Otwory: licznik — szerokość, mianownik — wysokość w świetle otworu; w nawiasie wysokość parapetu; symbol stolarki wg zestawienia stolarki.
4.	Numeracja pomieszczeń wg PN-B-01025 / PN-EN ISO 4157-2: <nr kondygnacji (parter = 1)> <nr> identyfikator w modelu: <kond> <nr> (parter = 0).
5.	Drzwi: strona otwierania (lewe/prawe) wg modelu — patrząc od strony, w którą otwiera się skrzydło.
6.	Rysunek wygenerowany automatycznie z modelu /home/user/aihouse/model/budynek.yaml (wersja 1.0, 2026-09-25) — generatory lamela.views.

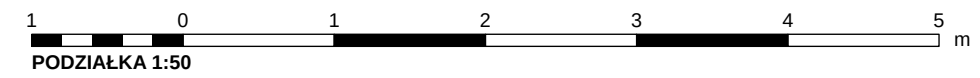

REW.	OPIS ZMIANY	DATA
0	Wydanie — rysunek wygenerowany z modelu	2026-09-25
PRACOWNIA PROJEKTOWA PRACOWNIA PROJEKTOWA — nazwa do uzupełnienia		STADIUM PB
adres pracowni do uzupełnienia		BRANŻA ARCHITEKTURA (AR)
INWESTOR (do uzupełnienia)		
OBJEKT / NAZWA ZAMIERZENIA BUDOWLANEGO Budynek mieszkalny jednorodzinny wolnostojący „Dom LAMELA”		
ADRES / LOKALIZACJA (NR DZIAŁKI, OBRĘB, JEDN. EWIDENCYJNA) ul. Lipowa (fikcyjna), dz. nr ewid. 1234, obręb 0005 Przykładowo, gm. Przykładowo (fikcyjna)		KAT. OBJEKTU I
FUNKCJA	IMIĘ I NAZWISKO	SPECJALNOŚĆ, NR UPRAWNIEN
Projektant		DATA
Projektant (wsp.)		PODPIS
Sprawdzający		
Opracował		
TYTUŁ RYSUNKU RZUT PARTERU		
SKALA 1:50	FORMAT A1	DATA WYDANIA 2026-09-25
RODZAJ DOK. Rzut	NR RYSUNKU PB-AR-01	ARKUSZ 1/10
REW. 0		

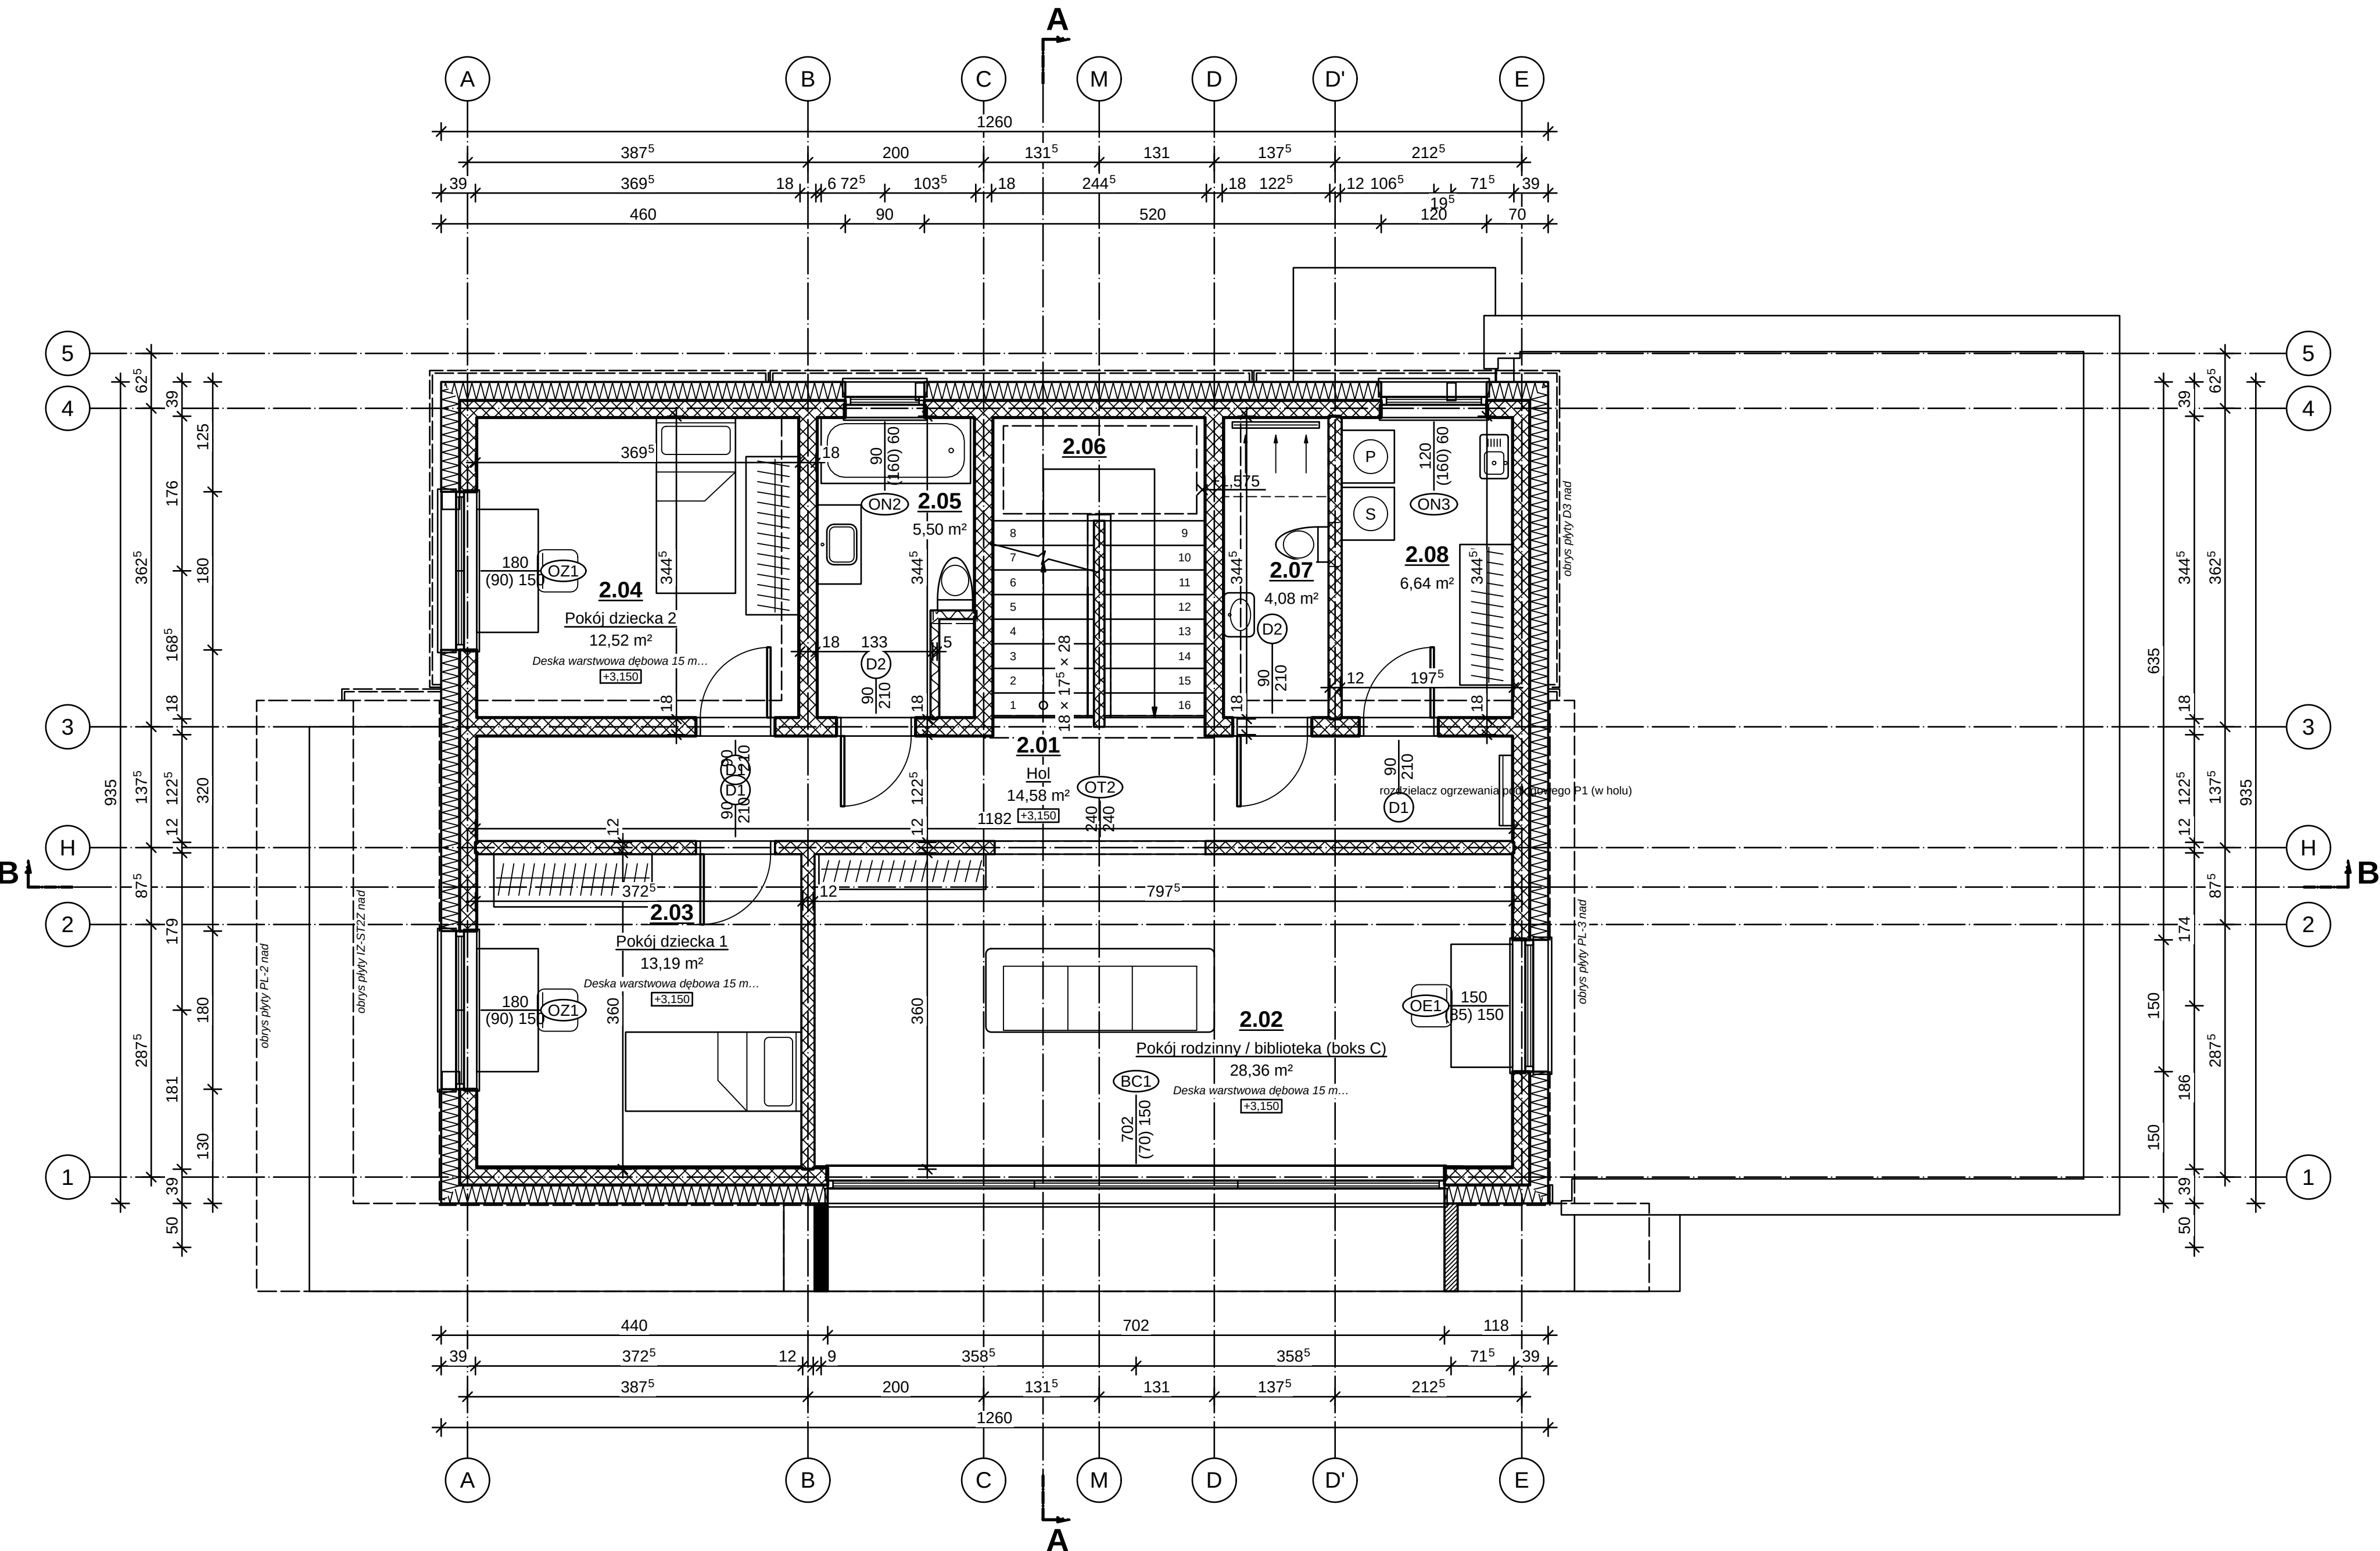

ZESTAWIENIE POMIESZCZEŃ


Nr	Nazwa pomieszczenia	Posadzka	Kat.	Wys. [m]	Pow. [m²]
2.02	Pokój rodzinny / biblioteka (boks C)	Deska warstwowa dębowa 15 mm, klejona	podst.	2,77	28,36
2.01	Hol	Deska warstwowa dębowa 15 mm, klejona	uchu	2,77	14,58
2.03	Pokój dziecka 1	Deska warstwowa dębowa 15 mm, klejona	podst.	2,77	13,19
2.04	Pokój dziecka 2	Deska warstwowa dębowa 15 mm, klejona	podst.	2,77	12,52
2.08	Pralnia z suszarnią	Płytki gresowe 60x120 na kleju C2TE \$1	pomoc.	2,77	6,64
2.05	Łazienka dzieci (wanna)	Płytki gresowe 60x120 na kleju C2TE \$1	pomoc.	2,77	5,50
2.07	WC z natryskiem	Płytki gresowe 60x120 na kleju C2TE \$1	pomoc.	2,77	4,08
2.06	Klatka schodowa	Deska warstwowa dębowa 15 mm, klejona	uchu	2,77	0,00
	RAZEM powierzchnia netto				84,88
	w tym użytkowa (podst. + pomoc.)				70,30

Wetna mineralna 035 (szkielet, docieplenia, ściana dom-garaz) – meander „UUU” Styropian grafitowy EPS 031 (ETICS, NRO w systemie) – zygzak „VVV”	Bloczek wapieno-piaskowy 12 cm, kl. 15 (ściana ścianki, nogi w łazie); Bloczek wapieno-piaskowy (słitka) 18 cm, kl. 20, gr. 1 na zaprawie cienkowarstwowej – kratka ukośna 45°/135° Rama boku C: ruszt stalowy ocynkowany w oddzielnie z blachy aluminiowej RAL 7016 (pusta w środku); Stal konstrukcyjna S355 (slaty RK, rama boku C); cynkowana ognowo + malowana proszkowo RAL 7016 – zacieranie
--	---

— — — — — elementy nad płaszczyzną cięcia (obrysy płyt, wsporników, brył wyższych kondygnacji)
 — — — — — elementy poniżej płaszczyzny cięcia (widok z góry)
 — — — — — osie konstrukcyjne; linia punktowa z pogrubionymi końcami — ślad przekroju

1. Wymiar: x cm (mm w indeksie górnym, np. 24⁺ = 24,5 cm), rzędne y w m względem 0+0 = 101,650 m n.p.m. (PL-EVRF7007-NH).
2. Rzut: planszyczna cisła +1,10 m nad posadzką podziemną. Linia kreskowa – element nad planszyczną cisłą (obrys był i wsporników, brył wyznaczających), otwory w rzucie (nad, belki), linie cisła – elementy poniżej wadoku.
3. Otwory: kreskowano szerokość, miarodajną wysokość w rzucie (nad, belki), wysokość wadoku: parpuł. Symbol stołaki w zestawieniu stołaki.
4. Numeracja pomieszczeń: np. 01025 / PN-EV 01157-2 (01157-2 to kod kondygnacji, 01157-2 to kod identyfikator w zestawieniu stołaki) (parter = 0).
5. Rzut: wygenerowania (level/prawie) w modelu – patrz: od rzutu, w która otwiera się skrzyżło.
6. Druki: stworzona automatycznie z modelu – `path=/user/aihouse/model/budynek.yaml` (wersja 1.0, 2026-09-25) – generatory lambda.views



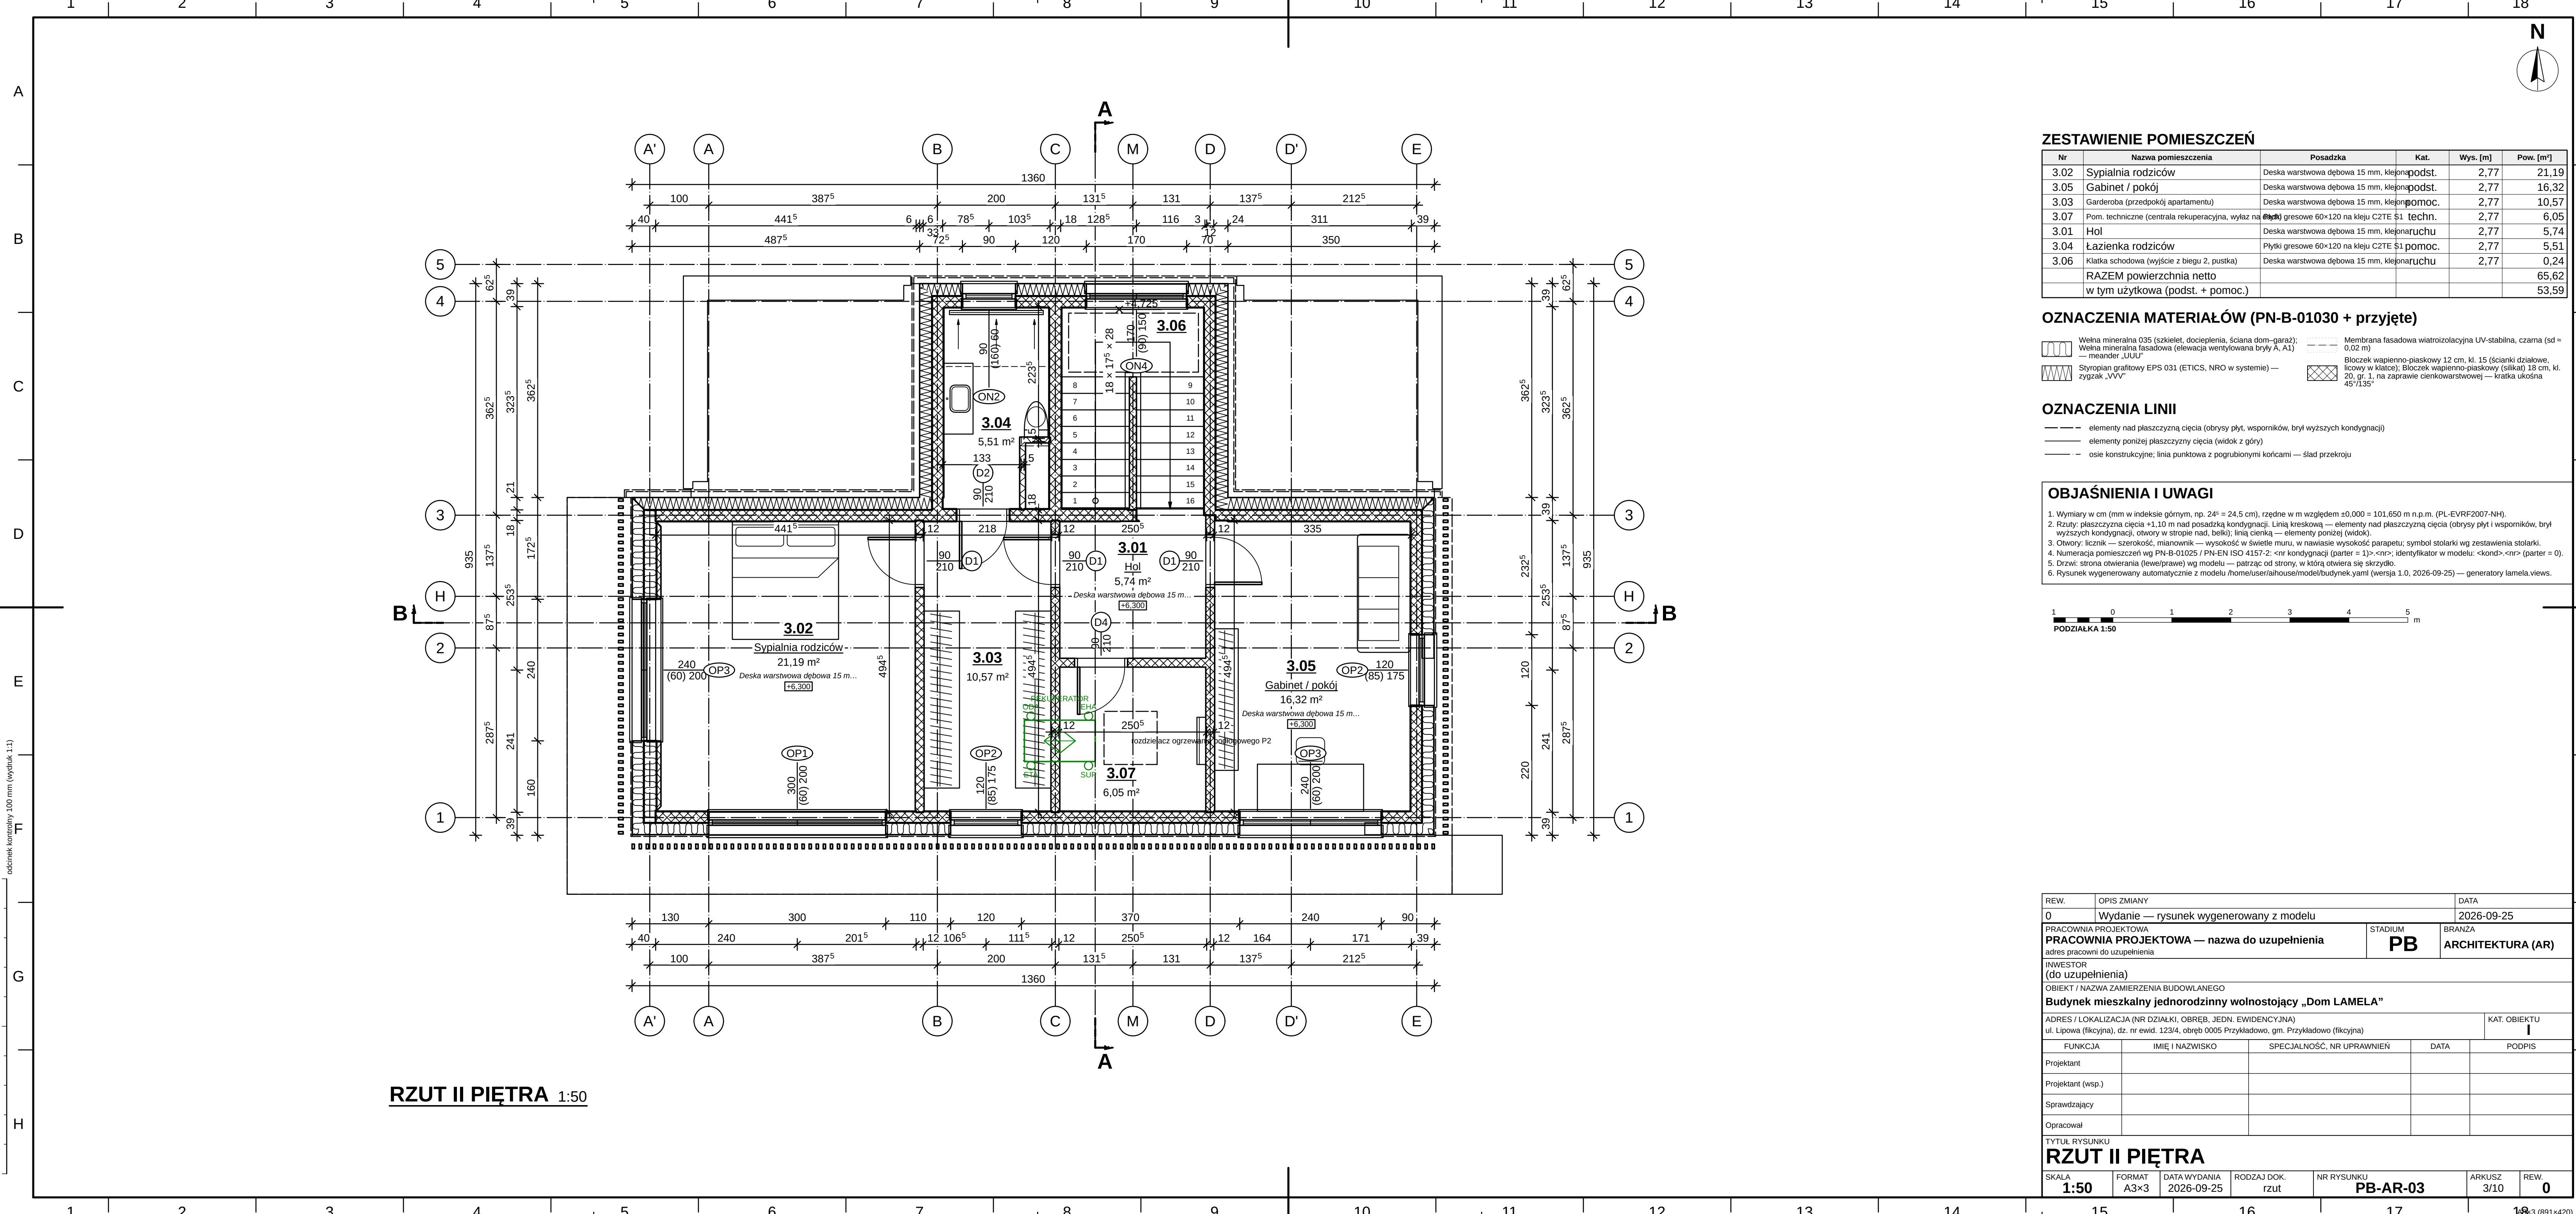

RZUT II PIĘTRA 1:50

ZESTAWIENIE POMIESZCZEŃ

Nr	Nazwa pomieszczenia	Posadzka	Kat.	Wys. [m]	Pow. [m²]
3.02	Sypialnia rodziców	Deska warstwowa dębowa 15 mm, klejona	podst.	2,77	21,19
3.05	Gabinet / pokój	Deska warstwowa dębowa 15 mm, klejona	podst.	2,77	16,32
3.03	Garderoba (przedpokój apartamentu)	Deska warstwowa dębowa 15 mm, klejona	pomoc.	2,77	10,57
3.07	Pom. techniczne (centrala rekuperacyjna, wylaz na dach)	Płytki gresowe 60x120 na kleju C2TE \$1 techn.	techn.	2,77	6,05
3.01	Hol	Deska warstwowa dębowa 15 mm, klejona	ruchu	2,77	5,74
3.04	Łazienka rodziców	Płytki gresowe 60x120 na kleju C2TE \$1	pomoc.	2,77	5,51
3.06	Klatka schodowa (wyjście z biegu 2, pustka)	Deska warstwowa dębowa 15 mm, klejona	ruchu	2,77	0,24
RAZEM powierzchnia netto					65,62
w tym użytkowa (podst. + pomoc.)					53,59

OZNACZENIA MATERIAŁÓW (PN-B-01030 + przyjęte)


	Wetna mineralna 035 (szkielet, docieplenia, ściana dom-garaż); Wetna mineralna fasadowa (elewacja wentylowana bryły A, A1)		Membrana fasadowa wiatroizolacyjna UV-stabilna, czarna (sd = 0,02 m)
	— meander „UUU”		— Błoczek wapienno-piaskowy 12 cm, kl. 15 (ścianki działkowe, licowy w klatce); Błoczek wapienno-piaskowy (silikat) 18 cm, kl. 20, gr. 1; na zaprawie cienkowarstwowej — kratka ukośna 45°/135°
	Styropian grafitowy EPS 031 (ETICS, NRO w systemie) — zygzak „VVV”		

OZNACZENIA LINII

- elementy nad płaszczyzną cięcia (obrysy płyt, wsporników, brył wyższych kondygnacji)
- elementy poniżej płaszczyzny cięcia (widok z góry)
- osie konstrukcyjne; linia punktowa z pogrubionymi końcami — ślad przekroju

OBJAŚNIENIA I UWAGI

- Wymiary w cm (mm w indeksie górnym, np. 24° = 24,5 cm), rzędne w m względem ±0,000 = 101,650 m n.p.m. (PL-EVRF2007-NH).
- Rzuty: płaszczyzna cięcia +1,10 m nad posadzką kondygnacji. Linia kreskowa — elementy nad płaszczyzną cięcia (obrysy płyt i wsporników, brył wyższych kondygnacji, otwory w stropie nad, belki); linia cienka — elementy poniżej (widok).
- Otwory: licznik — szerokość, mianownik — wysokość w świetle muru, w nawiasie wysokość parapetu; symbol stolarki wg zestawienia stolarki.
- Numeracja pomieszczeń wg PN-B-01025 / PN-EN ISO 4157-2: <nr kondygnacji (parter = 1)>.<nr>; identyfikator w modelu: <kond>.<nr> (parter = 0).
- Drzwi: strona otwierania (lewe/prawe) wg modelu — patrząc od strony, w którą otwiera się skrzydło.
- Rysunek wygenerowany automatycznie z modelu /home/user/aihouse/model/budynek.yaml (wersja 1.0, 2026-09-25) — generatory lamela views.

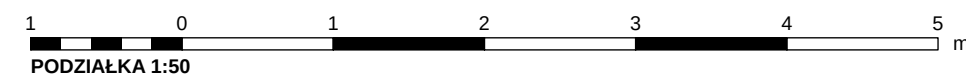

REW.	OPIS ZMIANY			DATA	
0	Wydanie — rysunek wygenerowany z modelu			2026-09-25	
PRACOWNIA PROJEKTOWA PRACOWNIA PROJEKTOWA — nazwa do uzupełnienia			STADIUM PB	BRANŻA ARCHITEKTURA (AR)	
adres pracowni do uzupełnienia					
INWESTOR (do uzupełnienia)					
OBIEKT / NAZWA ZAMIERZENIA BUDOWLANEGO Budynek mieszkalny jednorodzinny wolnostojący „Dom LAMELA”					
ADRES / LOKALIZACJA (NR DZIAŁKI, OBRĘB, JEDN. EWIDENCYJNA) ul. Lipowa (fikcyjna), dz. nr ewid. 123/4, obręb 0005 Przykładowo, gm. Przykładowo (fikcyjna)					KAT. OBIEKTU I
FUNKCJA		IMIĘ I NAZWISKO	SPECJALNOŚĆ, NR UPRAWNIENI	DATA	PODPIS
Projektant					
Projektant (wsp.)					
Sprawdzający					
Opracował					
TYTUŁ RYSUNKU RZUT II PIĘTRA					
SKALA 1:50	FORMAT A3x3	DATA WYDANIA 2026-09-25	RODZAJ DOK. rzut	NR RYSUNKU PB-AR-03	ARKUSZ 3/10
					REW. 0


OZNACZENIA LINII

- elementy nad płaszczyzną cięcia (obryszy płyt, wspomników, brył wyższych kondygracji)
--- elementy poniżej płaszczyzny cięcia (wielok z góry)
--- osie konstrukcyjne; linia punktowa z pogrubionymi końcami — ślad przekroju

OBJAŚNIENIA I UWAGI

1. Wymiary w cm (mm w indeksie górnym, np. 24⁵ = 24,5 cm), rzędy w m względem s.0.000 = 101.650 m n.p.m. (PL-EVRP2007-NH)
2. Rysunek wygenerowany automatycznie z modelu /modeluser/housemodel/budynek-yarni (wersja 1.0, 2026-09-25) — generatory lamela.views.


1 0 1 2 3 4 5 m
PODZIAŁKA 1:50

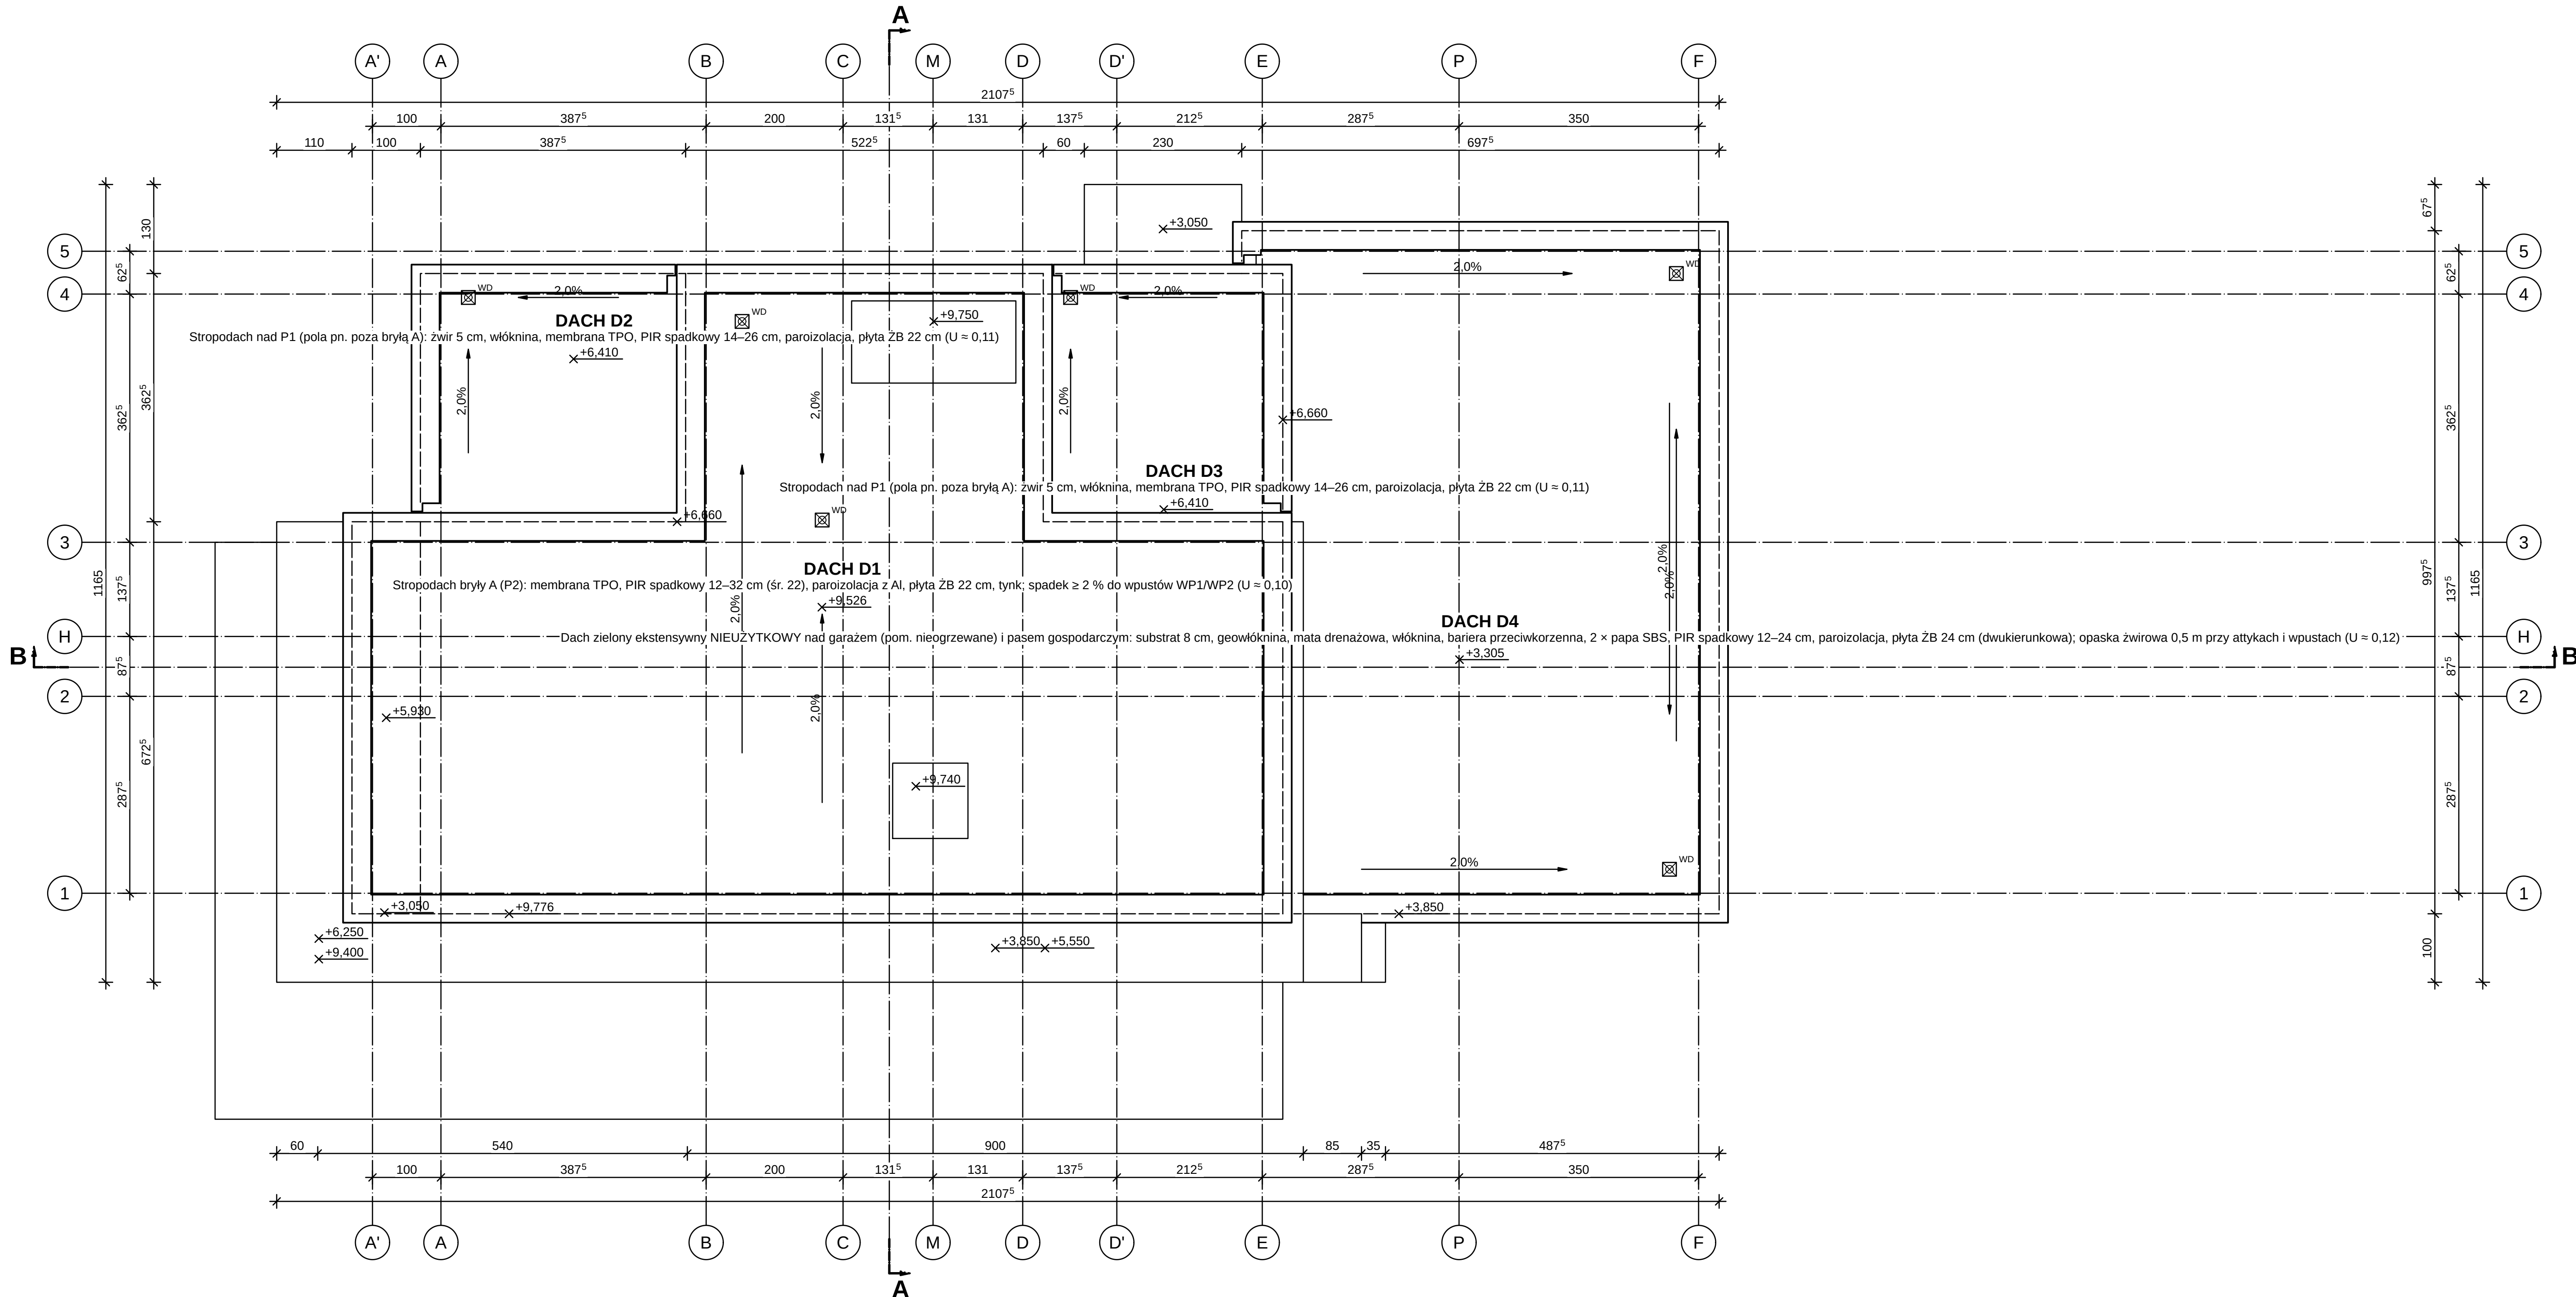

RZUT DACHU 1:50

REW.	OPIS ZMIANY			DATA	
A2-3	Wydanie — rysunek wygenerowany z modelu			2026-09-25	
PRACOWNIA PROJEKTOWA PRACOWNIA PROJEKTOWA — nazwa do uzupełnienia			STADIUM PB	BRANŻA ARCHITEKTURA (AR)	
INWESTOR (do uzupełnienia)					
OBIEKT / NAZWA ZAMIERZENIA BUDOWLANEGO Budynek mieszkalny jednorodzinny wolnostojący „Dom LAMELA”					
ADRES / LOKALIZACJA (NR DZIAŁKI, OBRĘB, JEDN. EWIDENCYJNA) ul. Lipowa (Ikcyjna), dz. nr ewid. 1234, obręb 0005 Przykładowo, gm. Przykładowo (Ikcyjna)				KAT. OBIEKTU I	
FUNKCJA		IMIĘ I NAZWISKO	SPECJALNOŚĆ, NR UPRAWNIEN	DATA	PODOPIS
Projektant					
Projektant (wsp.)					
Sprawdzający					
Opracował					
TYTUŁ RYSUNKU RZUT DACHU					
SKALA 1:50	FORMAT A2x3	DATA WYDANIA 2026-09-25	RODZAJ DOK. rzut	NR RYSUNKU PB-AR-04	ARKUSZ 4/10
				REW.	0

PRZEKRÓJ A-A 1:50

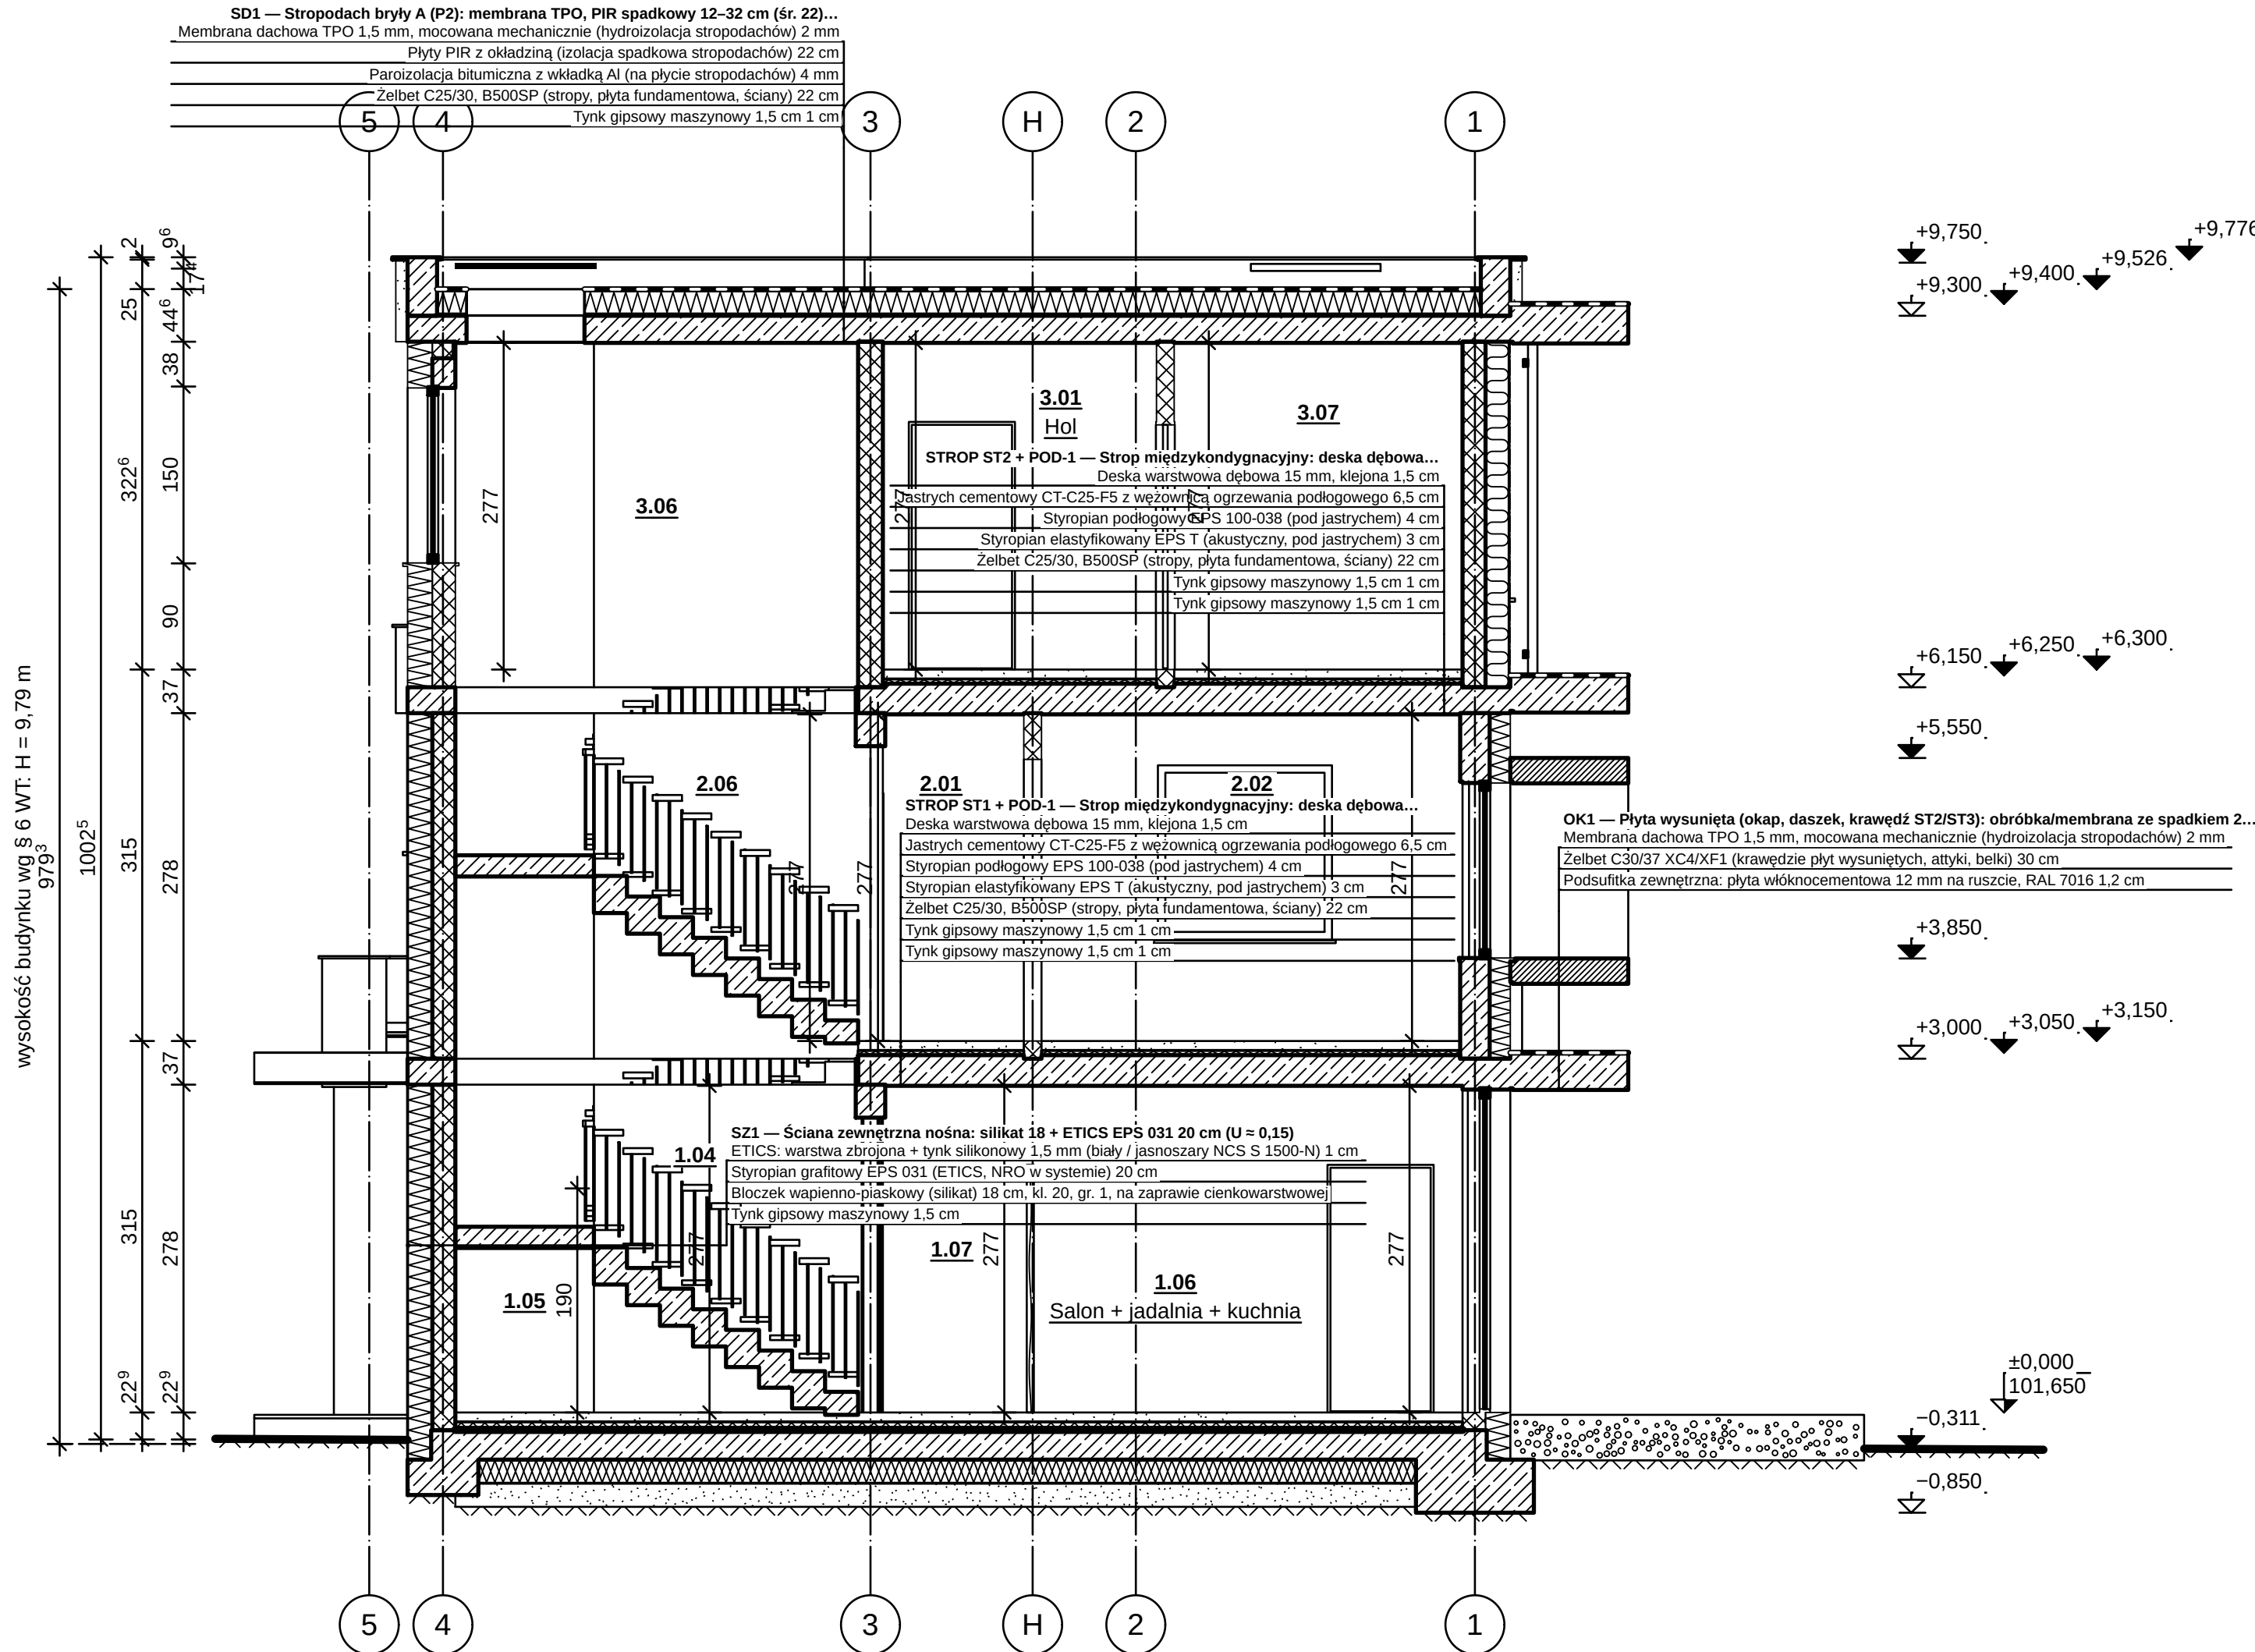


OZNACZENIA MATERIAŁÓW (PN-B-01030 + przyjęte)

	Lamele dębowe 30×60 mm (ekran komunikacji P0, h 2,10 m); Deska warstwowa dębowa 15 mm, klejona — przekrój wzdłuż włókien		Membrana fasadowa wiatroizolacyjna UV-stabilna, czarna (sd = 0,02 m)
	grunt rodzimy		Błoczek wapienno-piaskowy 12 cm, kl. 15 (ścianki działowe, licowy w klatce); Błoczek wapienno-piaskowy (silkat) 18 cm, kl. 20, gr. 1, na zaprawie cienkowarstwowej — krętka ukośna 45°/135°
	Wetna mineralna fasadowa (elewacja wentylowana bryły A, A1) — meander „UUU”		Folia PE 0,2 mm (warstwa rozdzielająca); Paroizolacja bitumiczna z wkładką Al (na płycie stropodachów) — linia kropkowa cienka 3/1 po ciepłej stronie
	Płyty PIR z okładziną (izolacja spadkowa stropodachów) — zygzak z okładziną		Podsypka piaskowa zagęszczona (l_s ≥ 0,98)
	Izolacja przeciwwilgociowa i przeciwdrońowa: membrana SBS 4 mm na płycie fundamentowej — linia bardzo gruba		Obróbki blacharskie (blacha powlekana); Stoiarka — profile aluminiowe, antracyt; Rama boksu C; ruszt stalowy ocynkowany w okładzinie z blachy aluminiowej RAL 7016 (pusia w środku); Stal malowana proszkowo (balustrady, rygle) — zaczerpienie
	Membrana dachowa TPO 1,5 mm, mocowana mechanicznie (hydroizolacja stropodachów) — pas czarno-biały		Szkoło (szyby zespolone); Ścianka szklana VSG 2 × 8 mm w ramie aluminiowej (wiatrołap / hol)
	Styropian grafitowy EPS 031 (ETICS, NRO w systemie); Styropian podłogowy EPS 100-038 (pod jastrychem); Styropian elastykowany EPS T (akustyczny, pod jastrychem) — zygzak „VVV”		Tynk gipsowy maszynowy 1,5 mm ETICS: warstwa zbrojona + tynk silikonowy 1,5 mm (biały / jasnoszary NCS S 1500-N) — kropki nieregularne
	Polistyren ekstrudowany XPS 300 (pod płytą fundamentową, cokół, izolacja obwodowa) — zygzak podwójny		Żelbet C25/30, B500SP (stropy, płyta fundamentowa, ściany); Żelbet C30/37 XC4/XF1 (krawędzie płyt wysuniętych, atyki, belki) — 45° na przemian ciągłe i przerywane
	Jastrych cementowy CT-C25-F5 z węzownicą ogrzewania podłogowego — kropki		Podbudowa nawierzchni (kruszywo)

OBJAŚNIENIA I UWAGI

- Wymiary w cm (mm w indeksie górnym, np. 24⁵ = 24,5 cm), rzędne w m względem ±0,000 = 101,650 m n.p.m. (PL-EVRF2007-NH).
- Rzędne: trójkąt zaczerpiony — poziom wykończenia, niezaczerpiony — konstrukcji, w połowie zaczerpiony — poziom ±0,000 z rzędną bezwzględną (PN-B-01025).
- Wysokość budynku wg § 6 WT: od terenu przy najniższym położonym wejściu (−0,267) do wierzchu stropodachu D1 (+9,526) — H = 9,79 m (bez atyki).
- Opisy warstw: kod i nazwa przegrody z modelu, materiały i grubości wg modelu (od góry / od lewej).
- Opisy warstw pominięte na rysunku (brak miejsca w podziale 1:50): POD-0 — układ warstw wg zestawienia przegród w części opisowej / przekroju 1:50.
- Rysunek wygenerowany automatycznie z modelu /home/user/aihouse/model/budynek.yaml (wersja 1.0, 2026-09-25) — generatory lamela.views.

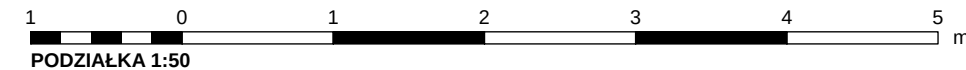

REW.	OPIS ZMIANY	DATA
0	Wydanie — rysunek wygenerowany z modelu	2026-09-25
PRACOWNIA PROJEKTOWA	PRACOWNIA PROJEKTOWA — nazwa do uzupełnienia	STADIUM
adres pracowni do uzupełnienia	PB	BRANZA
INWESTOR	ARCHITEKTURA (AR)	
(do uzupełnienia)		
OBIKT / NAZWA ZAMIERZENIA BUDOWLANEGO		
Budynek mieszkalny jednorodzinny wolnostojący „Dom LAMELA”		
ADRES / LOKALIZACJA (NR DZIAŁKI, OBRĘB, JEDN. EWIDENCYJNA)		KAT. OBIKTU
ul. Lipowa (fikcyjna), dz. nr ewid. 123/4, obręb 0005 Przykładowo, gm. Przykładowo (fikcyjna)		I
FUNKCJA	IMIĘ I NAZWISKO	SPECJALNOŚĆ, NR UPRAWNIEN
Projektant		DATA
Projektant (wsp.)		PODPIS
Sprawdzający		
Opracował		
TYTUŁ RYSUNKU		
PRZEKRÓJ A-A		
SKALA	FORMAT	DATA WYDANIA
1:50	A3×3	2026-09-25
RODZAJ DOK.	NR RYSUNKU	ARKUSZ
przekrój	PB-AR-05	5/10
		REW.
		0

PRZEKRÓJ B-B 1:50

wysokość budynku wg § 6 WT: H = 9,79 m

odcinek kantylajny 100 mm (wydruk 1:1)

SD1 — Stropodach bryły A (P2): membrana TPO, PIR spadkowy 12–32 cm (śr. 22)...
Membrana dachowa TPO 1,5 mm, mocowana mechanicznie (hydroizolacja stropodachów) 2 mm
Płyty PIR z okładziną (izolacja spadkowa stropodachów) 22 cm
Paroizolacja bitumiczna z wkładką Al (na płycie stropodachów) 4 mm
Żelbet C25/30, B500SP (stropy, płyta fundamentowa, ściany) 22 cm
Tynk gipsowy maszynowy 1,5 cm 1 cm

3.02
Sypialnia rodziców

STROP ST2 + POD-1 — Strop międzykondygnacyjny: deska dębowa...
Deska warstwowa dębowa 15 mm, klejona 1,5 cm
Jasnych cementowy CT-C25-F5 z węzownicą ogrzewania podłogowego 6,5 cm
Styropian podłogowy EPS 100-038 (pod jasnym) 4 cm
Styropian elastyczny EPS T (akustyczny, pod jasnym) 3 cm
Żelbet C25/30, B500SP (stropy, płyta fundamentowa, ściany) 22 cm
Tynk gipsowy maszynowy 1,5 cm 1 cm

2.03
Pokój dziecka 1

2.02 STROP ST1 + POD-1 — Strop międzykondygnacyjny: deska dębowa...
Deska warstwowa dębowa 15 mm, klejona 1,5 cm
Jasnych cementowy CT-C25-F5 z węzownicą ogrzewania podłogowego 6,5 cm
Styropian podłogowy EPS 100-038 (pod jasnym) 4 cm
Styropian elastyczny EPS T (akustyczny, pod jasnym) 3 cm
Żelbet C25/30, B500SP (stropy, płyta fundamentowa, ściany) 22 cm
Tynk gipsowy maszynowy 1,5 cm 1 cm

POD-0 — Podłoga na płycie fundamentowej (P0): deska/gres, jasnych z ogrzewaniem podł., EPS...
Deska warstwowa dębowa 15 mm, klejona 1,5 cm
Jasnych cementowy CT-C25-F5 z węzownicą ogrzewania podłogowego 6,5 cm
Styropian podłogowy EPS 100-038 (pod jasnym) 6,5 cm
Izolacja przeciwwilgociowa i przeciwdrań: membrana SBS 4 mm na płycie fundamentowej 5 mm
Żelbet C25/30, B500SP (stropy, płyta fundamentowa, ściany) 25 cm
Polistyren ekstrudowany XPS 300 (pod płytą fundamentową, cokół, izolacja obwodowa) 20 cm
Folia PE 0,2 mm (warstwa rozdzielająca)
Podsypka piaskowa zagęszczona (l_s ≥ 0,98) 20 cm

1.06

DZ1 — Dach zielony ekstensywny NIEUŻYTKOWY nad garażem (pom...
Substrat ekstensywny 8 cm z matą rozchodnikową (sedum)
Geowłókna filtracyjna PP 150 g/m² 2 mm
Mata drenażowo-retencyjna HDPE 25 mm (dach zielony) 2,5 cm
Włókna ochronna PP 300 g/m² 4 mm
Bariera przeciwwilgociowa PE-HD 0,5 mm (PN-EN 13948)
Hydroizolacja 2 + papa SBS (podkładowa + wierzchniego krycia, dach zielony) 9,5 mm
Płyty PIR z okładziną (izolacja spadkowa stropodachów) 18 cm
Paroizolacja bitumiczna z wkładką Al (na płycie stropodachów) 4 mm
Żelbet C25/30, B500SP (stropy, płyta fundamentowa, ściany) 24 cm

SZ1 — Ściana zewnętrzna nośna: silikat 18 + ETICS EPS 031 20 cm (U = 0,15)
Tynk gipsowy maszynowy 1,5 cm
Błoczek wapniowo-piaskowy (silikat) 18 cm, kl. 20, gr. 1, na zaprawie cienkowarstwowej
Styropian grafitowy EPS 031 (ETICS, NRO w systemie) 20 cm
ETICS: warstwa zbrojona + tynk silikonowy 1,5 mm (biały / jasnoszary NCS S 1500-N) 1 cm

1.13

OZNACZENIA MATERIAŁÓW (PN-B-01030 + przyjęte)

- grunt rodzimy
- Substrat ekstensywny 8 cm z matą rozchodnikową (sedum)
- Włókna mineralna 035 (szkielet, docieplenia, ściana dom-garaż); Włókna mineralna fasadowa (elewacja wentylowana bryły A, A1) — meander „UUU”
- Płyty PIR z okładziną (izolacja spadkowa stropodachów) — zygzak z okładzinami
- Izolacja przeciwwilgociowa i przeciwdrań: membrana SBS 4 mm na płycie fundamentowej — linia bardzo gruba
- Membrana dachowa TPO 1,5 mm, mocowana mechanicznie (hydroizolacja stropodachów); Hydroizolacja 2 + papa SBS (podkładowa + wierzchniego krycia, dach zielony) — pas
- Styropian grafitowy EPS 031 (ETICS, NRO w systemie); Styropian podłogowy EPS 100-038 (pod jasnym); Styropian elastyczny EPS T (akustyczny, pod jasnym) — zygzak „VVV”
- Polistyren ekstrudowany XPS 300 (pod płytą fundamentową, cokół, izolacja obwodowa) — zygzak podwójny
- Jasnych cementowy CT-C25-F5 z węzownicą ogrzewania podłogowego — kropki
- Membrana fasadowa wiatroizolacyjna UV-stabilna, czarna (sd = 0,02 m)
- Błoczek wapniowo-piaskowy 12 cm, kl. 15 (ścianki działowe, licowy w klatce); Błoczek wapniowo-piaskowy (silikat) 18 cm, kl. 20, gr. 1, na zaprawie cienkowarstwowej — krętka ukośna 45°/135°
- Folia PE 0,2 mm (warstwa rozdzielająca); Paroizolacja bitumiczna z wkładką Al (na płycie stropodachów) — linia kreskowa cienka 3/1 po ciepłej stronie
- Podsypka piaskowa zagęszczona (l_s ≥ 0,98)
- Obróbki blacharskie (blacha powlekana); Stalarka — profile aluminiowe, antracyt; Stal malowana proszkowo (balustrady, rylce) — zaczerpienie
- Tynk cementowo-wapniowy 1,5 cm (garaż, pom. techniczne); Tynk gipsowy maszynowy 1,5 cm; ETICS: warstwa zbrojona + tynk silikonowy 1,5 mm (biały / jasnoszary NCS S 1500-N) — kropki nieregularne
- Żelbet C25/30, B500SP (stropy, płyta fundamentowa, ściany); Żelbet C30/37 XC4/XF1 (krawędzie płyt wysuniętych, atyki, belki) — 45° na przemian ciagle i przerywane
- Podbudowa nawierzchni (kruźnywo)

OBJAŚNIENIA I UWAGI

1. Wymiary w cm (mm w indeksie górnym, np. 24° = 24,5 cm), rzędne w m względem ±0,000 = 101,650 m n.p.m. (PL-EVRF2007-NH).
2. Rzędne: trójkąt zaczerpienie — poziom wykończenia, niezaczerpienie — konstrukcji, w pokłowie zaczerpienie — poziom ±0,000 z rzędną bezwzględną (PN-B-01025).
3. Wysokość budynku wg § 6 WT: od terenu przy najniższej położonym wejściu (–0,267) do wierzchu stropodachu D1 (+9,526) — H = 9,79 m (bez atyki).
4. Opisy warstw: kod i nazwa przegrody z modelu, materiały i grubości wg modelu (od góry / od lewej).
5. Opisy warstw pominięte na rysunku (brak miejsca w podziale 1:50): STROP ST22 + POD-1, OK1 — układ warstw wg zestawienia przegród w części opisowej / przekroju 1:50.
6. Rysunek wygenerowany automatycznie z modelu /home/user/aihouse/model/budynnek.yaml (wersja 1.0, 2026-09-25) — generatory lamela.views.


1 0 1 2 3 4 5 m
PODZIAŁKA 1:50

REW.	OPIS ZMIANY	DATA
0	Wydanie — rysunek wygenerowany z modelu	2026-09-25
PRACOWNIA PROJEKTOWA		STADIUM
PRACOWNIA PROJEKTOWA — nazwa do uzupełnienia		PB
adres pracowni do uzupełnienia		BRANŻA
INWESTOR		ARCHITEKTURA (AR)
(do uzupełnienia)		
OBIEKT / NAZWA ZAMIERZENIA BUDOWLANEGO		
Budynek mieszkalny jednorodzinny wolnostojący „Dom LAMELA”		
ADRES / LOKALIZACJA (NR DZIAŁKI, OBRĘB, JEDN. EWIDENCYJNA)		KAT. OBIEKTU
ul. Lipowa (fikcyjna), dz. nr ewid. 123/4, obręb 0005 Przykładowo, gm. Przykładowo (fikcyjna)		I
FUNKCJA	IMIĘ I NAZWISKO	SPECJALNOŚĆ, NR UPRAWNIEN
Projektant		DATA
Projektant (wsp.)		PODPIS
Sprawdzający		
Opracował		

TYTUŁ RYSUNKU


PRZEKRÓJ B-B

SKALA	FORMAT	DATA WYDANIA	RODZAJ DOK.	NR RYSUNKU	ARKUSZ	REW.
1:50	A3×3	2026-09-25	przekrój	PB-AR-06	6/10	0

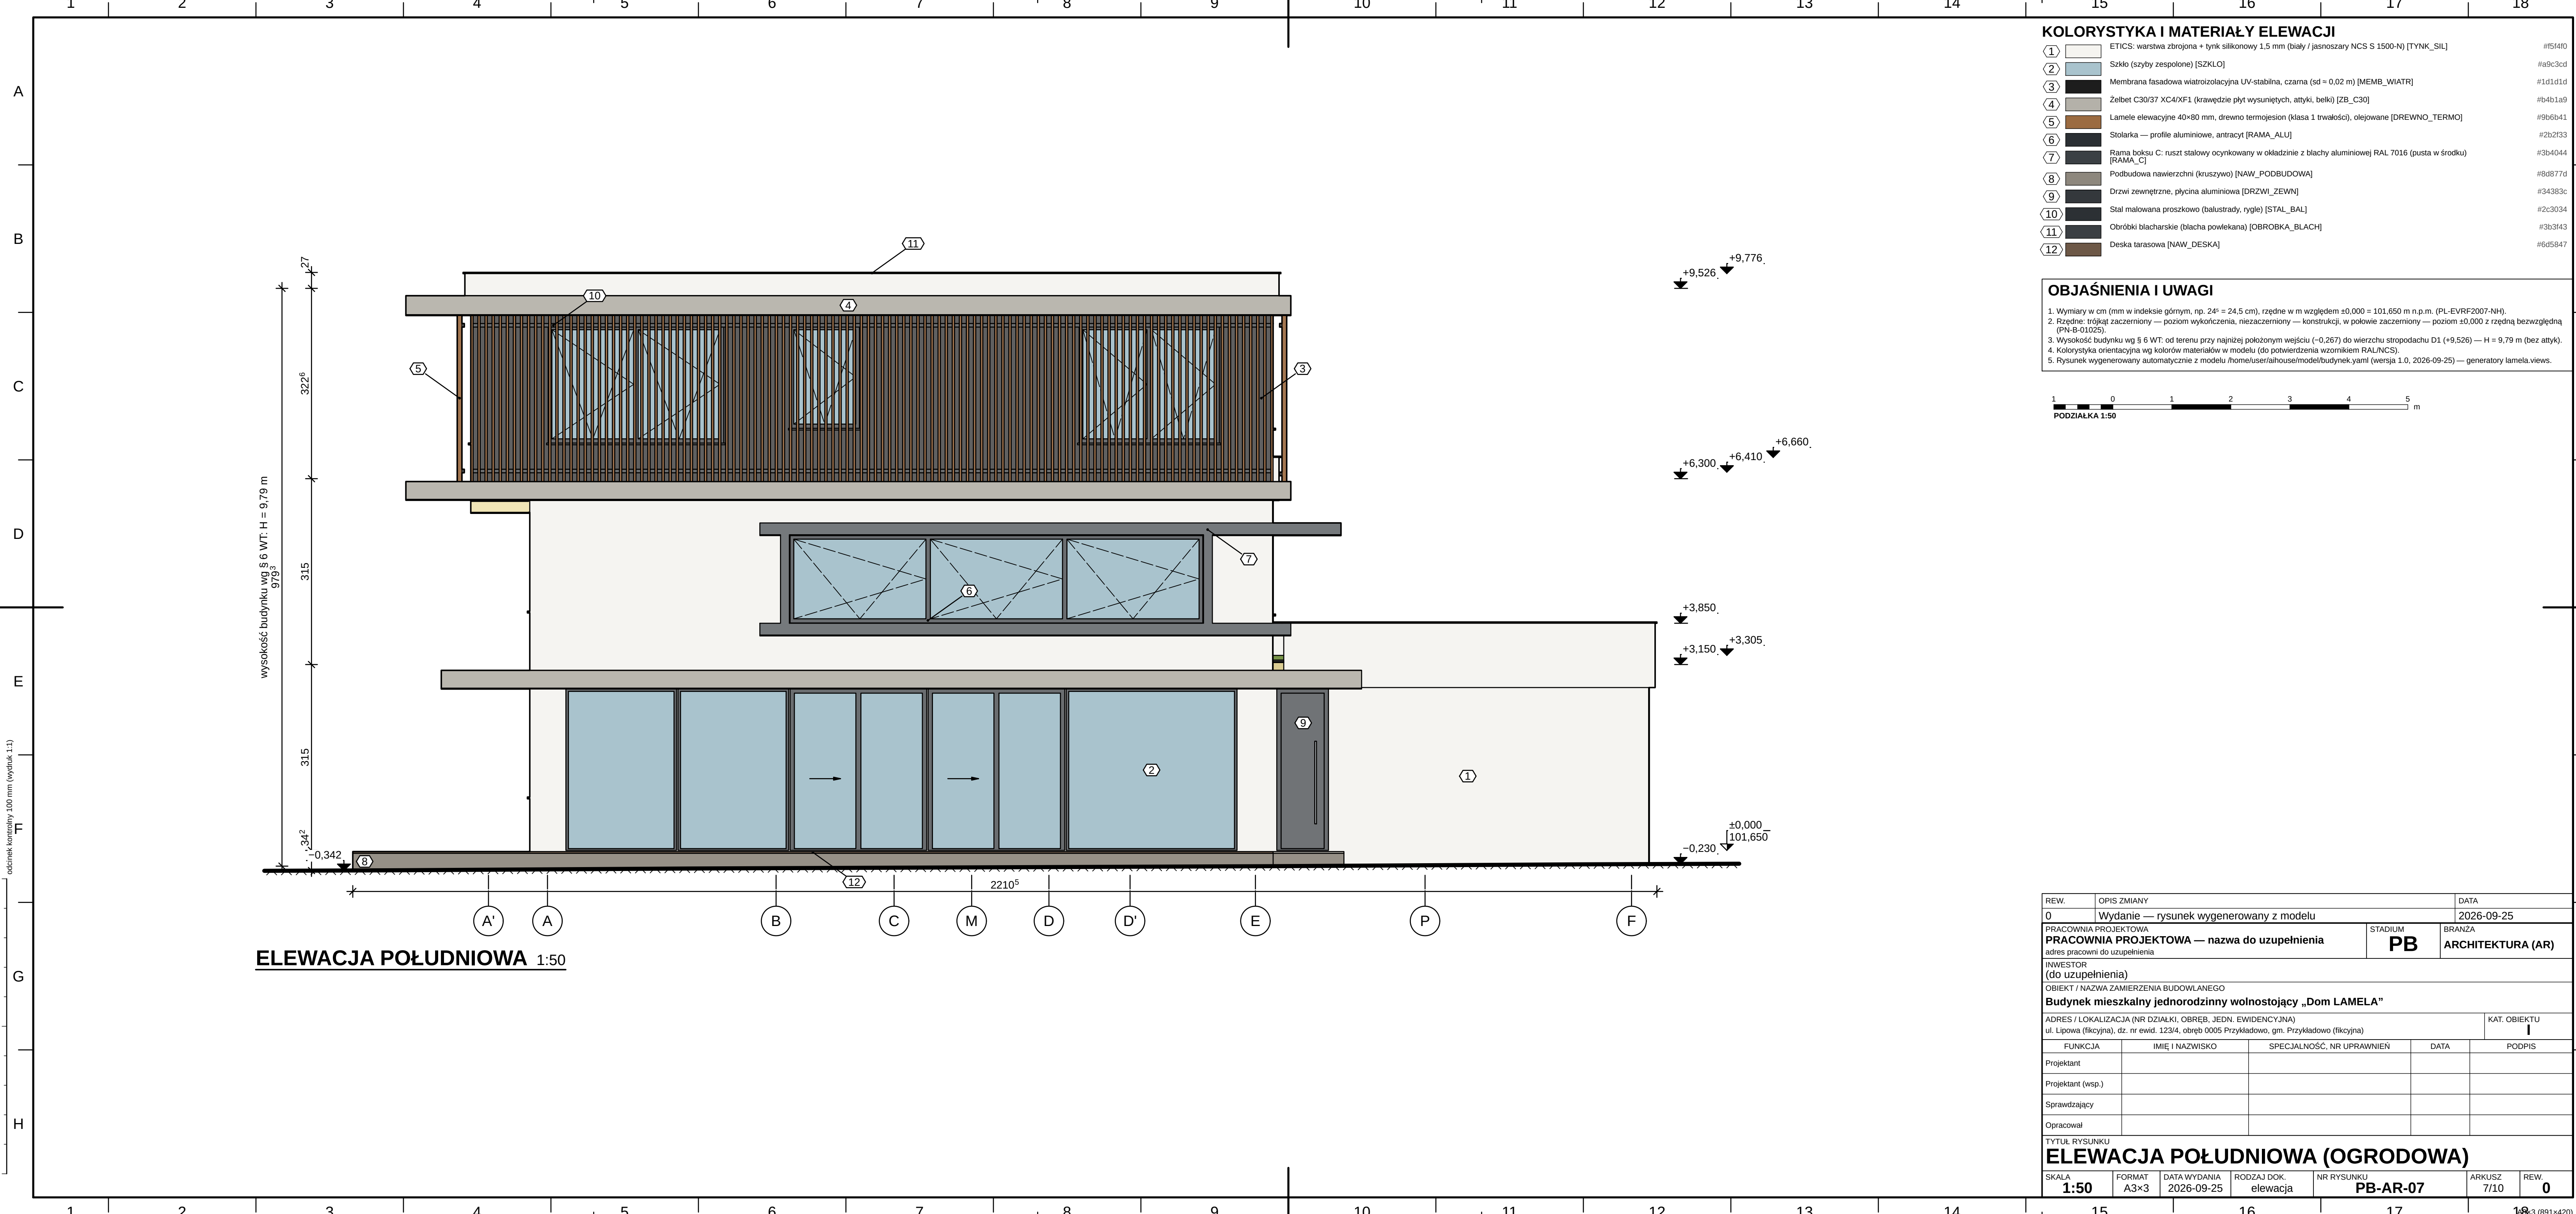


KOLORYSTYKA I MATERIAŁY ELEWACJI		
1	ETICS: warstwa zbrojona + tynk silikonowy 1,5 mm (biały / jasnoszary NCS S 1500-N) [TYNK_SIL]	#f5f4f0
2	Szko (szyby zespolone) [SZKLO]	#a9c3cd
3	Membrana fasadowa wiatroizolacyjna UV-stabilna, czarna (sd = 0,02 m) [MEMB_WIATR]	#1d1d1d
4	Żelbet C30/37 XC4/XF1 (krawędzie płyt wysuniętych, attyki, belki) [ZB_C30]	#b4b1a9
5	Lamele elewacyjne 40×80 mm, drewno termojesion (klasa 1 trwałości), olejowane [DREWNO_TERMO]	#9b6b41
6	Stolarka — profile aluminiowe, antracyt [RAMA_ALU]	#2b2f33
7	Rama boksu C: ruszt stalowy ocynkowany w okładzinie z blachy aluminiowej RAL 7016 (pusta w środku) [RAMA_C]	#3b4044
8	Podbudowa nawierzchni (kruszywo) [NAW_PODBUDOWA]	#8d877d
9	Drzwi zewnętrzne, płycina aluminiowa [DRZWI_ZEWN]	#34383c
10	Stal malowana proszkowo (balustrady, rygle) [STAL_BAL]	#2c3034
11	Obróbki blacharskie (blacha powlekana) [OBROBKA_BLACH]	#3b3f43
12	Deska tarasowa [NAW_DESKA]	#6d5847

OBJAŚNIENIA I UWAGI	
1. Wymiary w cm (mm w indeksie górnym, np. 24 ² = 24,5 cm), rzędne w m względem ±0,000 = 101,650 m n.p.m. (PL-EVRF2007-NH).	
2. Rzędne: trójkąt zaczerpiony — poziom wykończenia, niezaczerpiony — konstrukcji, w polowie zaczerpiony — poziom ±0,000 z rzędną bezwzględną (PN-B-01025).	
3. Wysokość budynku wg § 6 WT: od terenu przy najniższym wejściu (-0,267) do wierzchu stropodachu D1 (+9,526) — H = 9,79 m (bez attyki).	
4. Kolorystyka orientacyjna wg kolorów materiałów w modelu (do potwierdzenia wzornikiem RAL/NCS).	
5. Rysunek wygenerowany automatycznie z modelu /home/user/aihouse/model/budynek.yaml (wersja 1.0, 2026-09-25) — generatory lamela.views.	

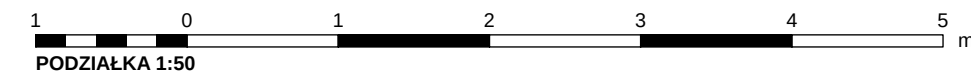

REW.	OPIS ZMIANY			DATA
0	Wydanie — rysunek wygenerowany z modelu			2026-09-25
PRACOWNIA PROJEKTOWA PRACOWNIA PROJEKTOWA — nazwa do uzupełnienia adres pracowni do uzupełnienia			STADIUM PB	BRANŻA ARCHITEKTURA (AR)
INWESTOR (do uzupełnienia)				
OBIEKT / NAZWA ZAMIERZENIA BUDOWLANEGO Budynek mieszkalny jednorodzinny wolnostojący „Dom LAMELA”				
ADRES / LOKALIZACJA (NR DZIAŁKI, OBREB, JEDN. EWIDENCYJNA) ul. Lipowa (fikcyjna), dz. nr ewid. 123/4, obręb 0005 Przykładowo, gm. Przykładowo (fikcyjna)				KAT. OBIEKTU I
FUNKCJA	IMIĘ I NAZWISKO	SPECJALNOŚĆ, NR UPRAWNIENI	DATA	PODPIS
Projektant				
Projektant (wsp.)				
Sprawdzający				
Opracował				
TYTUŁ RYSUNKU ELEWACJA POŁUDNIOWA (OGRODOWA)				
SKALA 1:50	FORMAT A3×3	DATA WYDANIA 2026-09-25	RODZAJ DOK. elewacja	NR RYSUNKU PB-AR-07
ARKUSZ 7/10			REW. 0	

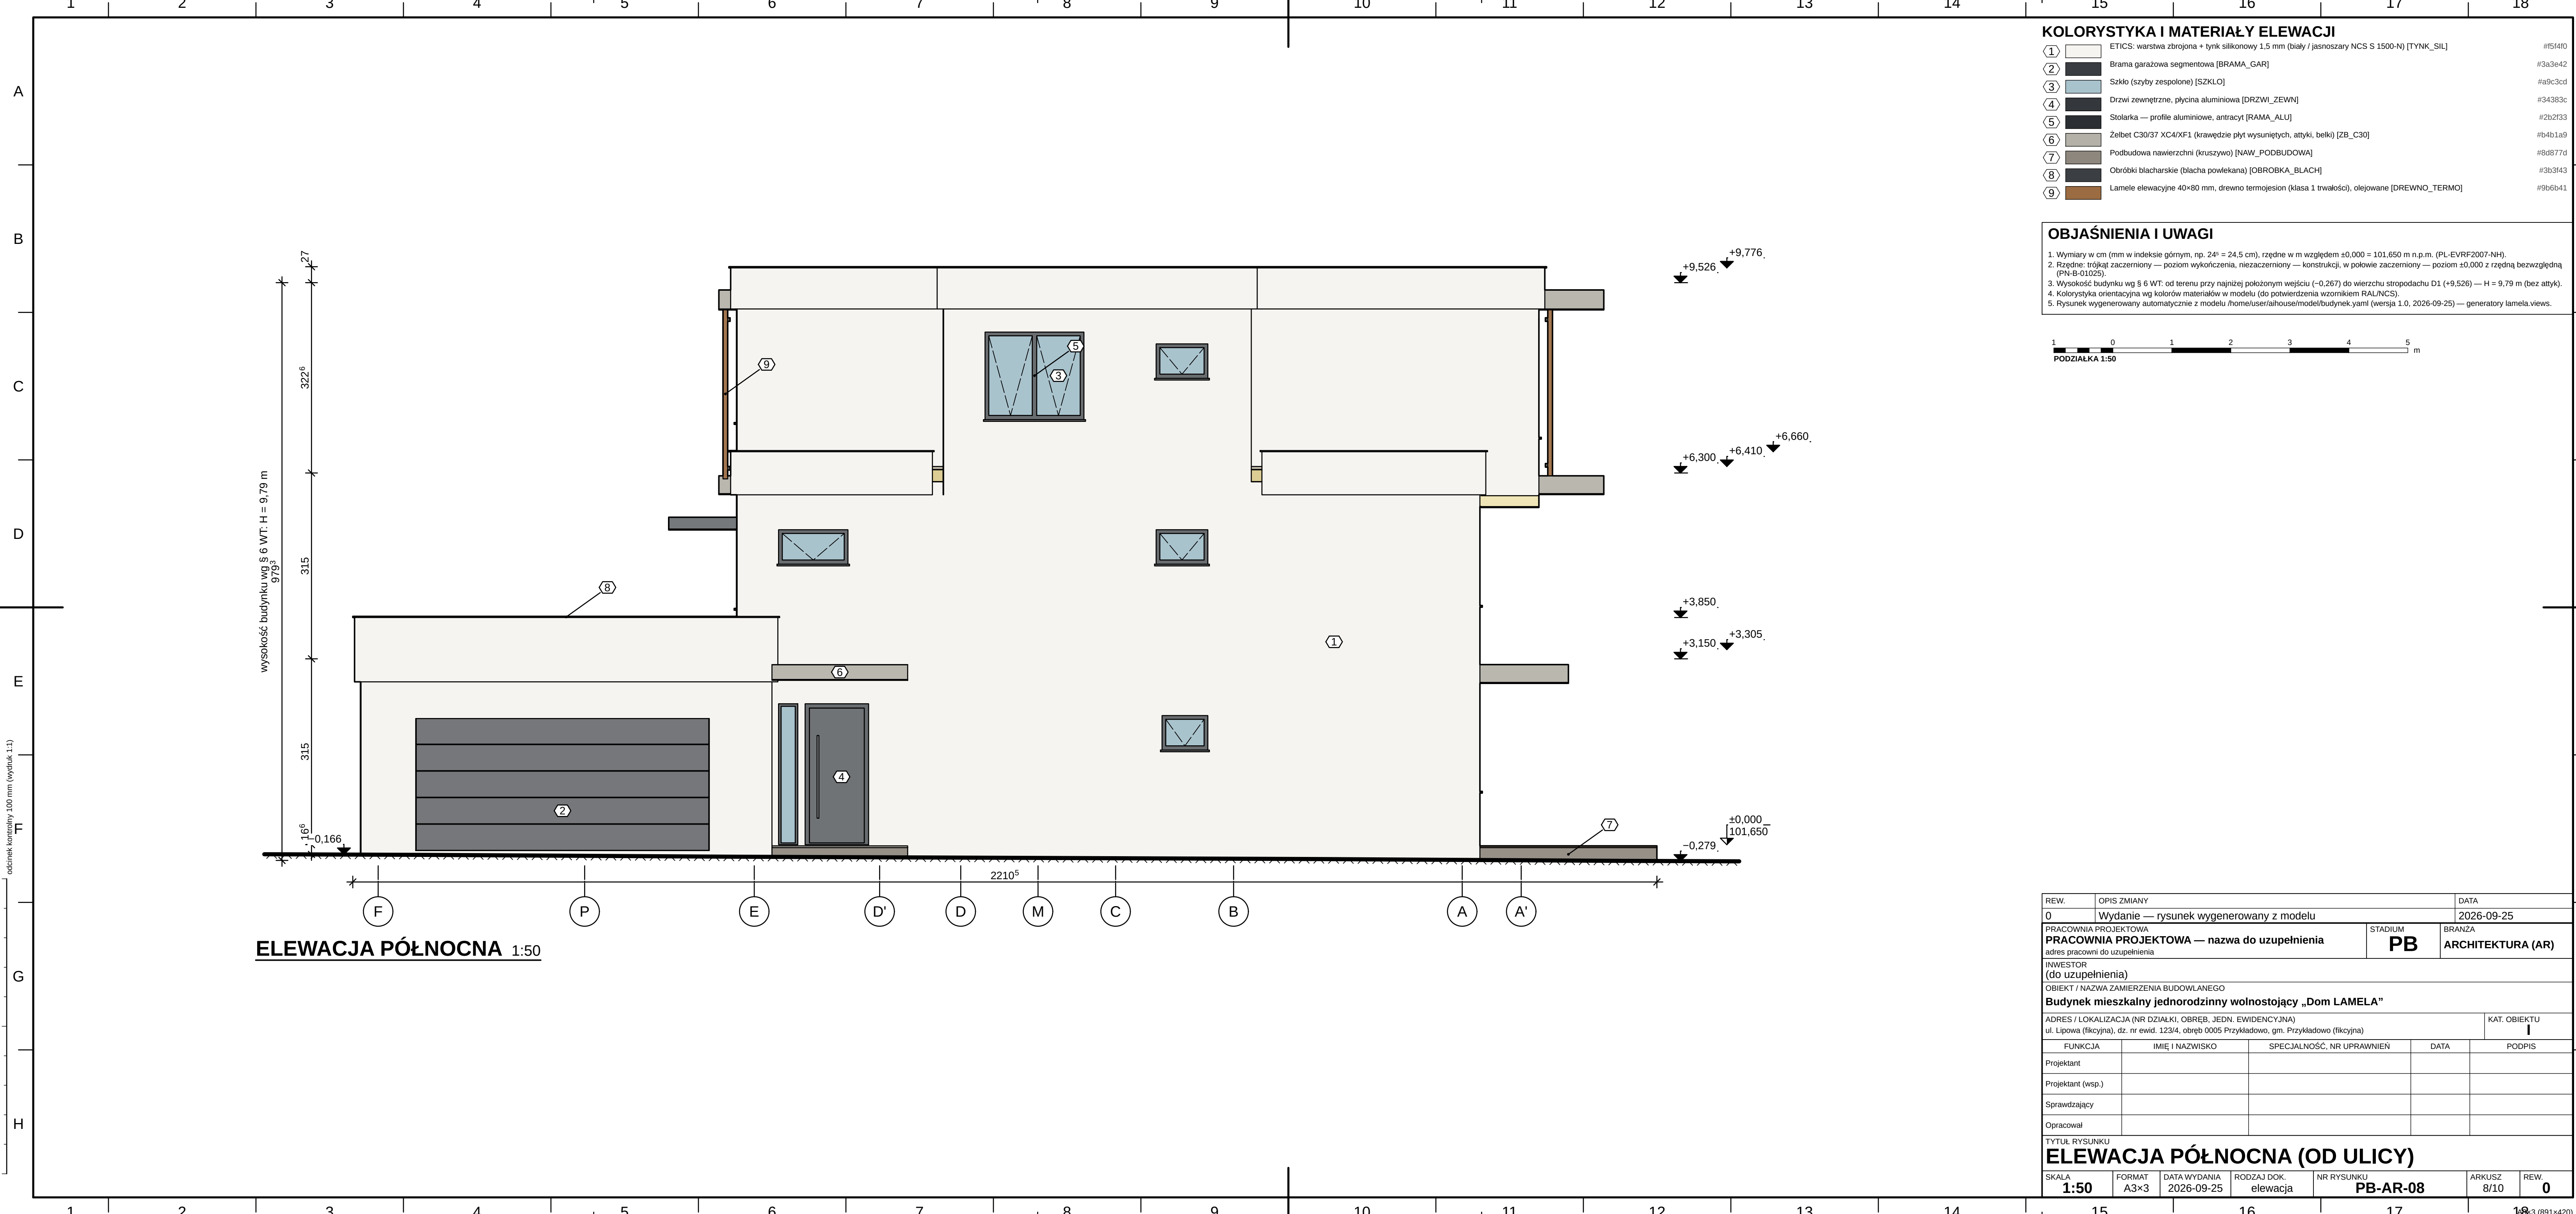


KOLORYSTYKA I MATERIAŁY ELEWACJI


①	ETICS: warstwa zbrojona + tynk silikonowy 1.5 mm (biały / jasnoszary NCS S 1500-N) [TYNK_SIL]	#f5f4f0
②	Brama garażowa segmentowa [BRAMA_GAR]	#3a3e42
③	Szkoło (szyby zespolone) [SZKLO]	#a9c3cd
④	Drzwi zewnętrzne, pływina aluminiowa [DRZWI_ZEWN]	#34383c
⑤	Stołarka — profile aluminiowe, antracyt [RAMA_ALU]	#2b2f33
⑥	Żelbet C30/37 XC4/XP1 (krawędzie płyt wysuniętych, attyki, belki) [ZB_C30]	#b4b1a9
⑦	Podbudowa nawierzchni (kruszywo) [NAW_PODBUDOWA]	#8d877d
⑧	Otróbbki blacharskie (blacha powlekana) [OBROBKA_BLACH]	#3b3f43
⑨	Lamele elewacyjne 40×80 mm, drewno termojesion (klasa 1 trwałości), olejowane [DREWNO_TERMO]	#9b6b41


OBJAŚNIENIA I UWAGI

- Wymiary w cm (mm w indeksie górnym, np. 24⁶ = 24,5 cm), rzędne w m względem ±0,000 = 101,650 m n.p.m. (PL-EVRF2007-NH).
- Rzędne: trójkąt zaczerpiony — poziom wykończenia, niezaczerpiony — konstrukcji, w połowie zaczerpiony — poziom ±0,000 z rzędną bezwzględną (PN-B-01025).
- Wysokość budynku wg § 6 WT: od terenu przy najniżej położonym wejściu (−0,267) do wierzchu stropodachu D1 (+9,526) — H = 9,79 m (bez attyki).
- Kolorystyka orientacyjna wg kolorów materiałów w modelu (do potwierdzenia wzornikiem RALNCS).
- Rysunek wygenerowany automatycznie z modelu /home/user/ai/house/model/budynek.yaml (wersja 1.0, 2026-09-25) — generatory lamela.views.

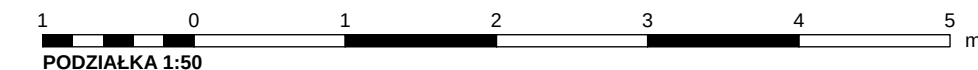


REW.	OPIS ZMIANY				DATA		
0	Wydanie — rysunek wygenerowany z modelu				2026-09-25		
PRACOWNIA PROJEKTOWA				STADIUM	BRANZA		
PRACOWNIA PROJEKTOWA — nazwa do uzupełnienia				PB	ARCHITEKTURA (AR)		
adres pracowni do uzupełnienia							
INWESTOR							
(do uzupełnienia)							
OBIEKT / NAZWA ZAMIERZENIA BUDOWLANEGO							
Budynek mieszkalny jednorodzinny wolnostojący „Dom LAMELA”							
ADRES / LOKALIZACJA (NR DZIAŁKI, OBREB, JEDN. EWIDENCYJNA)					KAT. OBIEKTU		
ul. Lipowa (fikcyjna), dz. nr ewid. 123/4, obręb 0005 Przykładowo, gm. Przykładowo (fikcyjna)					I		
FUNKCJA		IMIĘ I NAZWISKO		SPECJALNOŚĆ, NR UPRAWNIENI		DATA	PODPIS
Projektant							
Projektant (wsp.)							
Sprawdzający							
Opracował							
TYTUŁ RYSUNKU							
ELEWACJA PÓŁNOCNA (OD ULICY)							
SKALA	FORMAT	DATA WYDANIA	RODZAJ DOK.	NR RYSUNKU	ARKUSZ		REW.
1:50	A3x3	2026-09-25	elewacja	PB-AR-08	8/10		0

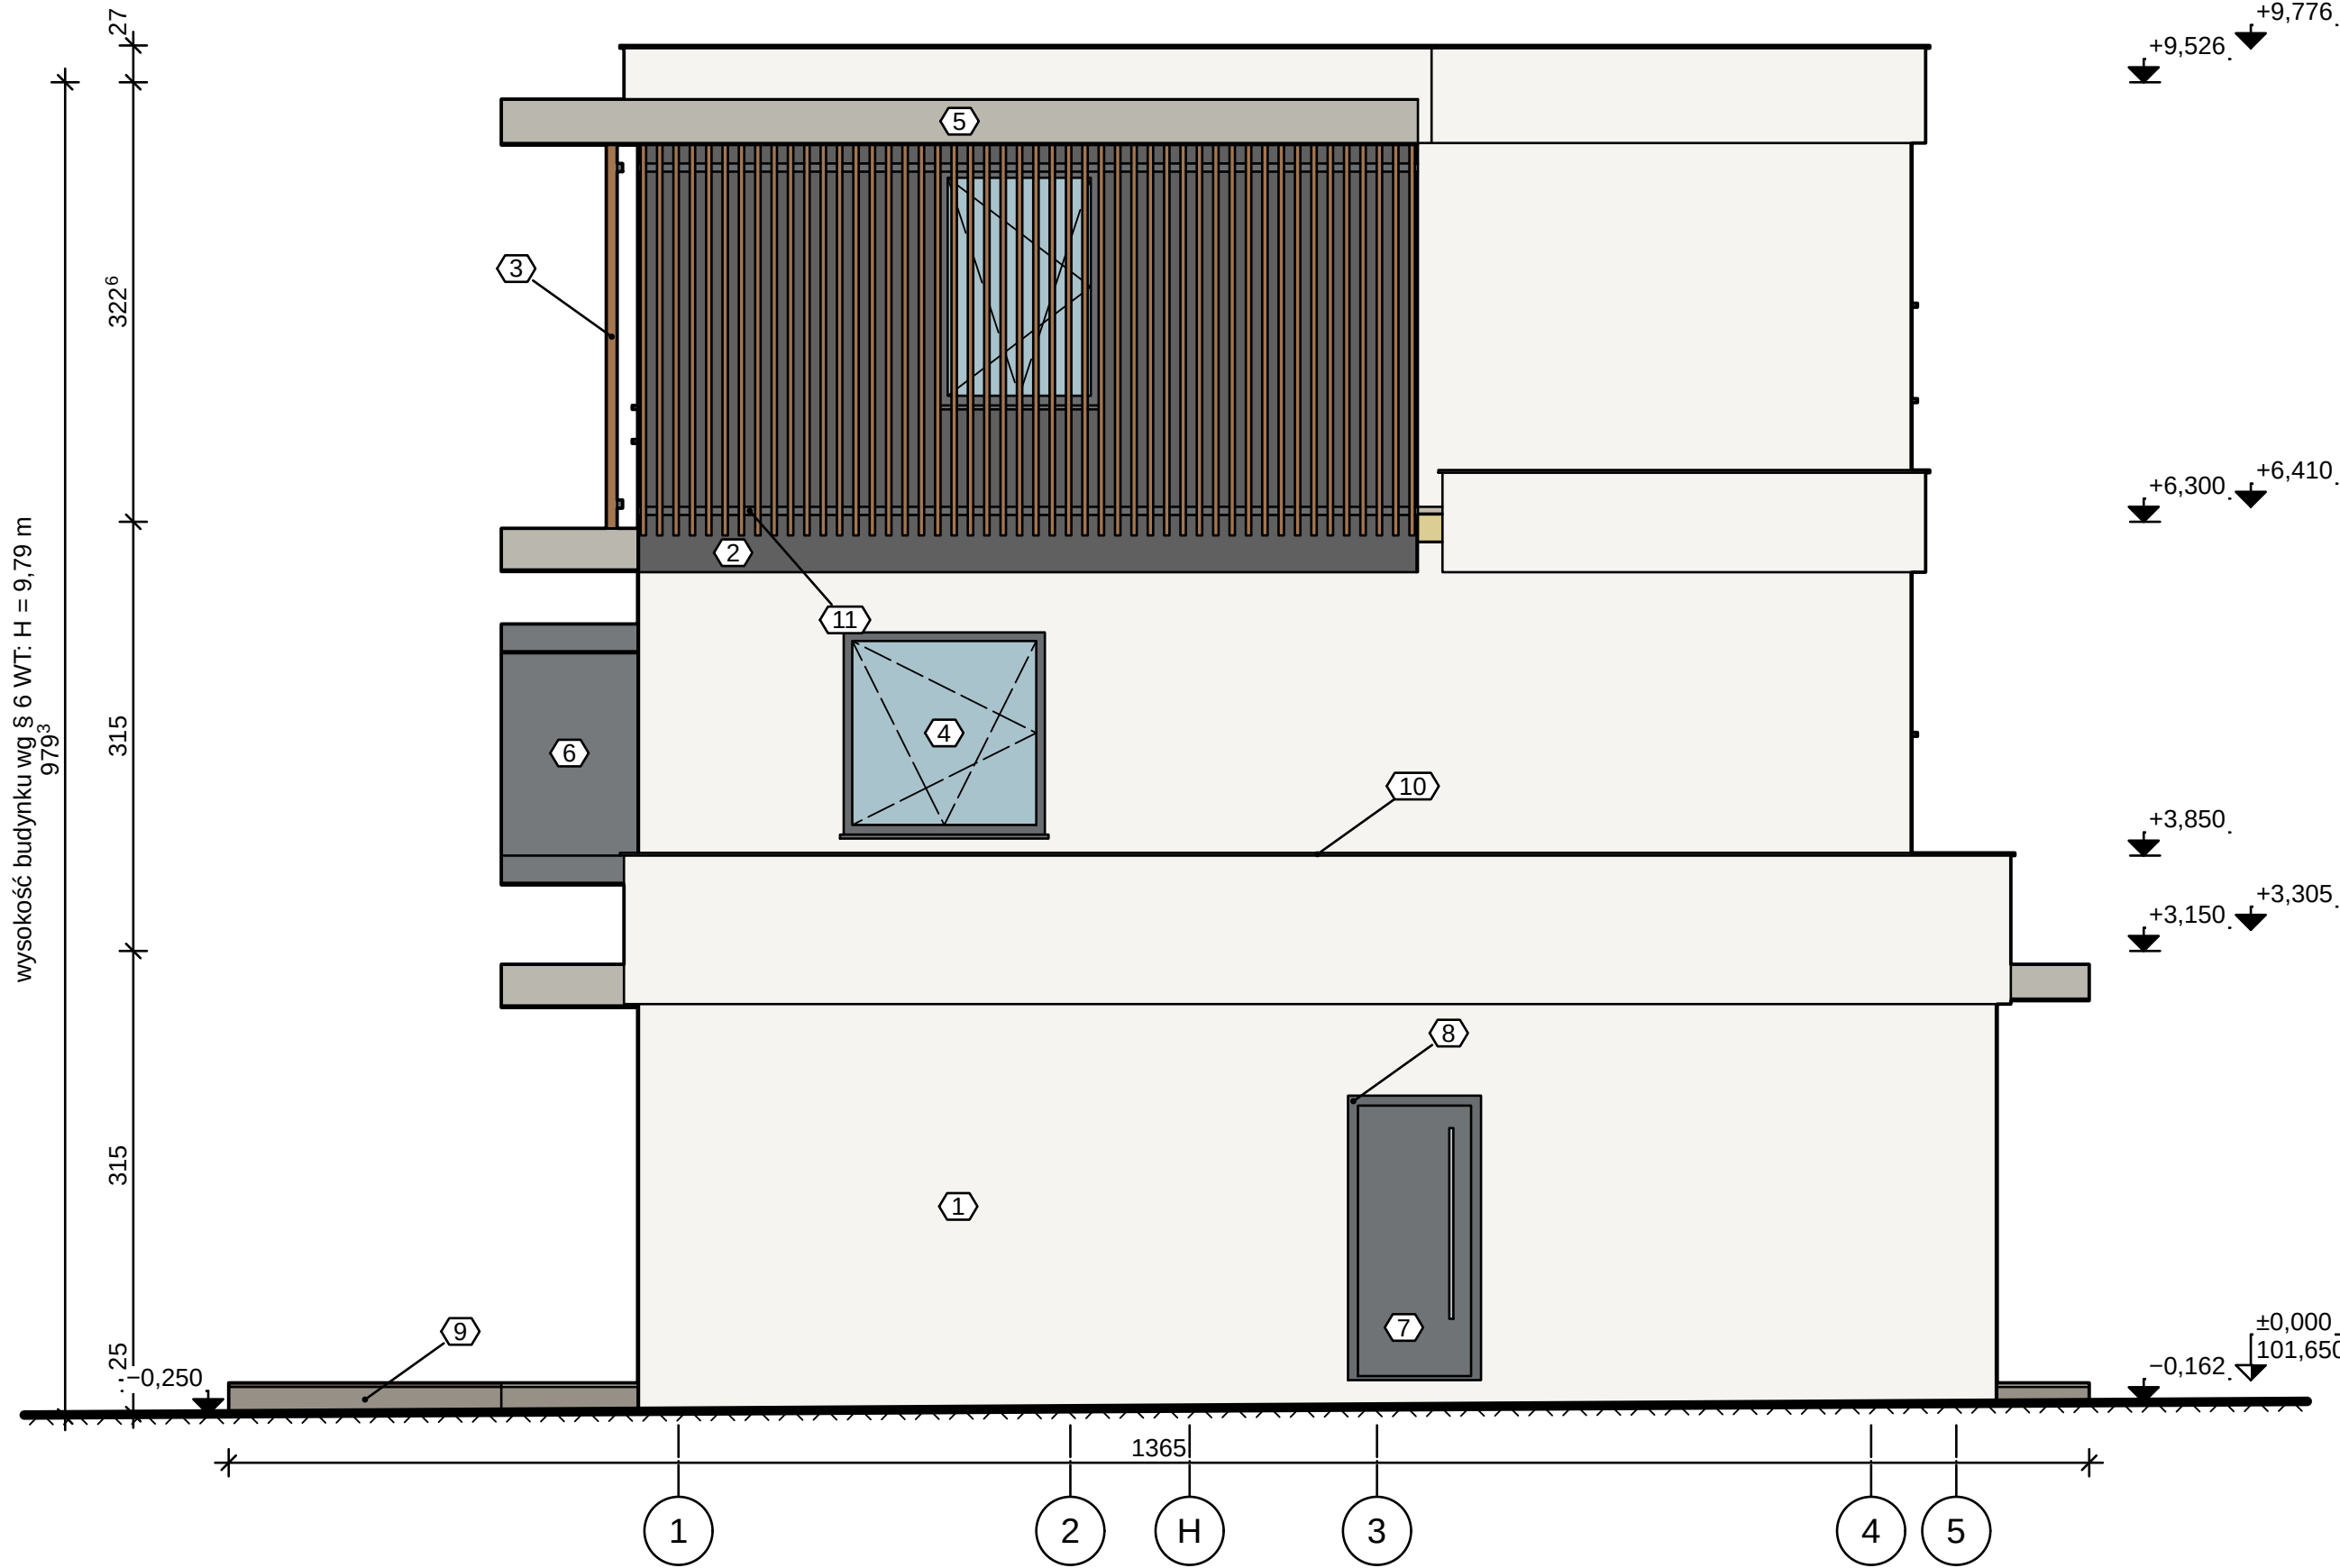

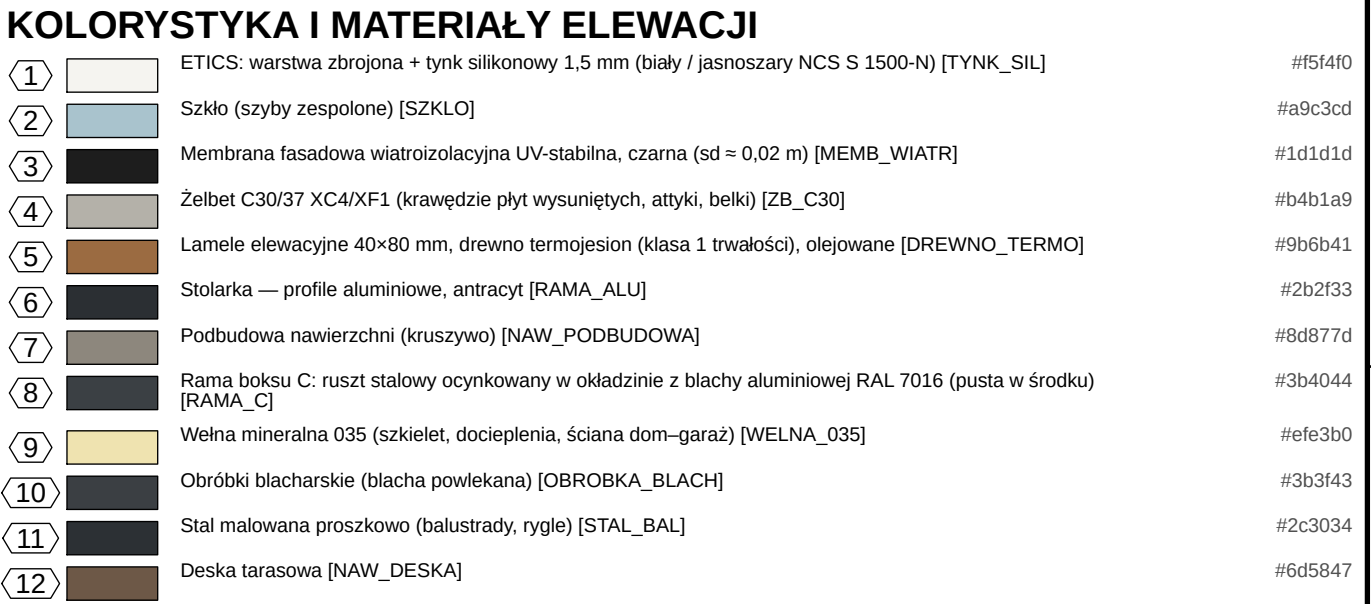

1. Wymiary w cm (mm w indeksie górnym, np. 24⁺ = 24,5 cm), rzędne w m względem ±0,000 = 101,650 m n.p.m. (PL-EVRF2007-NH).
2. Rzędne: trójką zaczerpiony — poziom wykończenia, niezaczerpiony — konstrukcji, w połowie zaczerpiony — poziom ±0,000 z rzędną bezwzględną (PN-B-01025).
3. Wykośnienie budynku wg § 6 WT: od terenu przy najniżej położonym wejściu (−0,267) do wierzchu stropodachu D1 (+9,526) — H = 9,79 m (bez attyki).
4. Kolorystyka orientacyjna wg kolorów materiałów w modelu (do potwierdzenia wzornikiem RAL/NCs).
5. Rysunek wygenerowany automatycznie z modelu /home/user/aihouse/model/budynek.yaml (wersja 1.0, 2026-09-25) — generatory lamela.views.

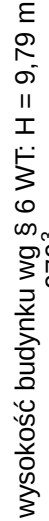

odcinek kontrolny 100 mm (wydruk 1:1)

REW.		OPIS ZMIANY		DATA	
0		Wydanie — rysunek wygenerowany z modelu			2026-09-25
PRACOWNIA PROJEKTOWA PRACOWNIA PROJEKTOWA — nazwa do uzupełnienia adres pracowni do uzupełnienia				STADIUM PB	BRANŻA ARCHITEKTURA (AR)
INWESTOR (do uzupełnienia)					
OBIEKT / NAZWA ZAMIERZENIA BUDOWLANEGO Budynek mieszkalny jednorodzinny wolnostojący „Dom LAMELA”					
ADRES / LOKALIZACJA (NR DZIAŁKI, OBRĘB, JEDN. EWIDENCYJNA) ul. Lipowa (fikcyjna), dz. nr ewid. 123/4, obręb 0005 Przykładowo, gm. Przykładowo (fikcyjna)					KAT. OBIEKTU I
FUNKCJA		IMIĘ I NAZWISKO		SPECJALNOŚĆ, NR UPRAWNIIEŃ	DATA
Projektant					
Projektant (wsp.)					
Sprawdzający					
Opracował					
TYTUŁ RYSUNKU ELEWACJA ZACHODNIA					
SKALA 1:50	FORMAT A2	DATA WYDANIA 2026-09-25	RODZAJ DOK. elewacja	NR RYSUNKU PB-AR-10	ARKUSZ 10/10
					REW. 0