


PROJEKT ZAGOSPODAROWANIA DZIAŁKI — CZĘŚĆ RYSUNKOWA

Lp.	Nr rys.	Tytuł rysunku	Skala	Format
1	PZT-01	PLAN ZAGOSPODAROWANIA DZIAŁKI	1:500	420×530
2	PZT-02	PLAN SZCZEGÓŁOWY — WYMIARY I RZĘDNE	1:200	594×430
3	PZT-03	RYSUNEK KOORDYNACYJNY UZBROJENIA TERENU	1:200	610×450

PRACOWNIA PROJEKTOWA PRACOWNIA PROJEKTOWA — nazwa do uzupełnienia		STADIUM PB	BRANŻA ZAGOSPODAROWANIE TERENU			
INWESTOR (do uzupełnienia)						
OBIEKT / NAZWA ZAMIERZENIA BUDOWLANEGO Budynek mieszkalny jednorodzinny wolnostojący „Dom LAMELA” z zagospodarowaniem działki						
ADRES / LOKALIZACJA (NR DZIAŁKI, OBRĘB, JEDN. EWIDENCYJNA) ul. Lipowa (fikcyjna), dz. nr ewid. 123/4, obręb 0005 Przykładowo, gm. Przykładowo (fikcyjna)			KAT. OBIEKTU I			
FUNKCJA	IMIĘ I NAZWISKO	SPECJALNOŚĆ, NR UPRAWNIEŃ	DATA	PODPIS		
Projektant	[DO UZUPEŁNIENIA]	[DO UZUPEŁNIENIA]				
Projektant (wsp.)	[DO UZUPEŁNIENIA]	[DO UZUPEŁNIENIA]				
Sprawdzający	nie dotyczy (art. 20 ust. 3 pkt 2 PB)	—				
Opracował	[DO UZUPEŁNIENIA]	[DO UZUPEŁNIENIA]				
TYTUŁ RYSUNKU SPIS RYSUNKÓW						
SKALA —	FORMAT A4	DATA WYDANIA 2026-09-25	RODZAJ DOK. spis	NR RYSUNKU PZT-00	ARKUSZ —	REW.

MAPA DO CELÓW PROJEKTOWYCH — PODKŁAD PRZYKŁADOWY

PODKŁAD PRZYKŁADOWY — mapa do celów projektowych fikcyjna [DANE PRZYKŁADOWE – FIKCYJNE], narysowana z modelu działki (działka.yaml); w projekcie rzeczywistym — aktualna mapa do celów projektowych wg art. 34 ust. 3 pkt 1 PB (z klauzulą urzędową lub oświadczeniem geodety — art. 34b PB), treść i opis mapy wg § 32–33 rozp. w sprawie standardów technicznych (t.j. Dz.U. 2022 poz. 1670), znaki wg zał. 4 rozp. w sprawie BDOT500 i mapy zasadniczej (Dz.U. 2021 poz. 1385; oba akty zweryfikowane w ELI 25.09.2026 — status: obowiązujące).

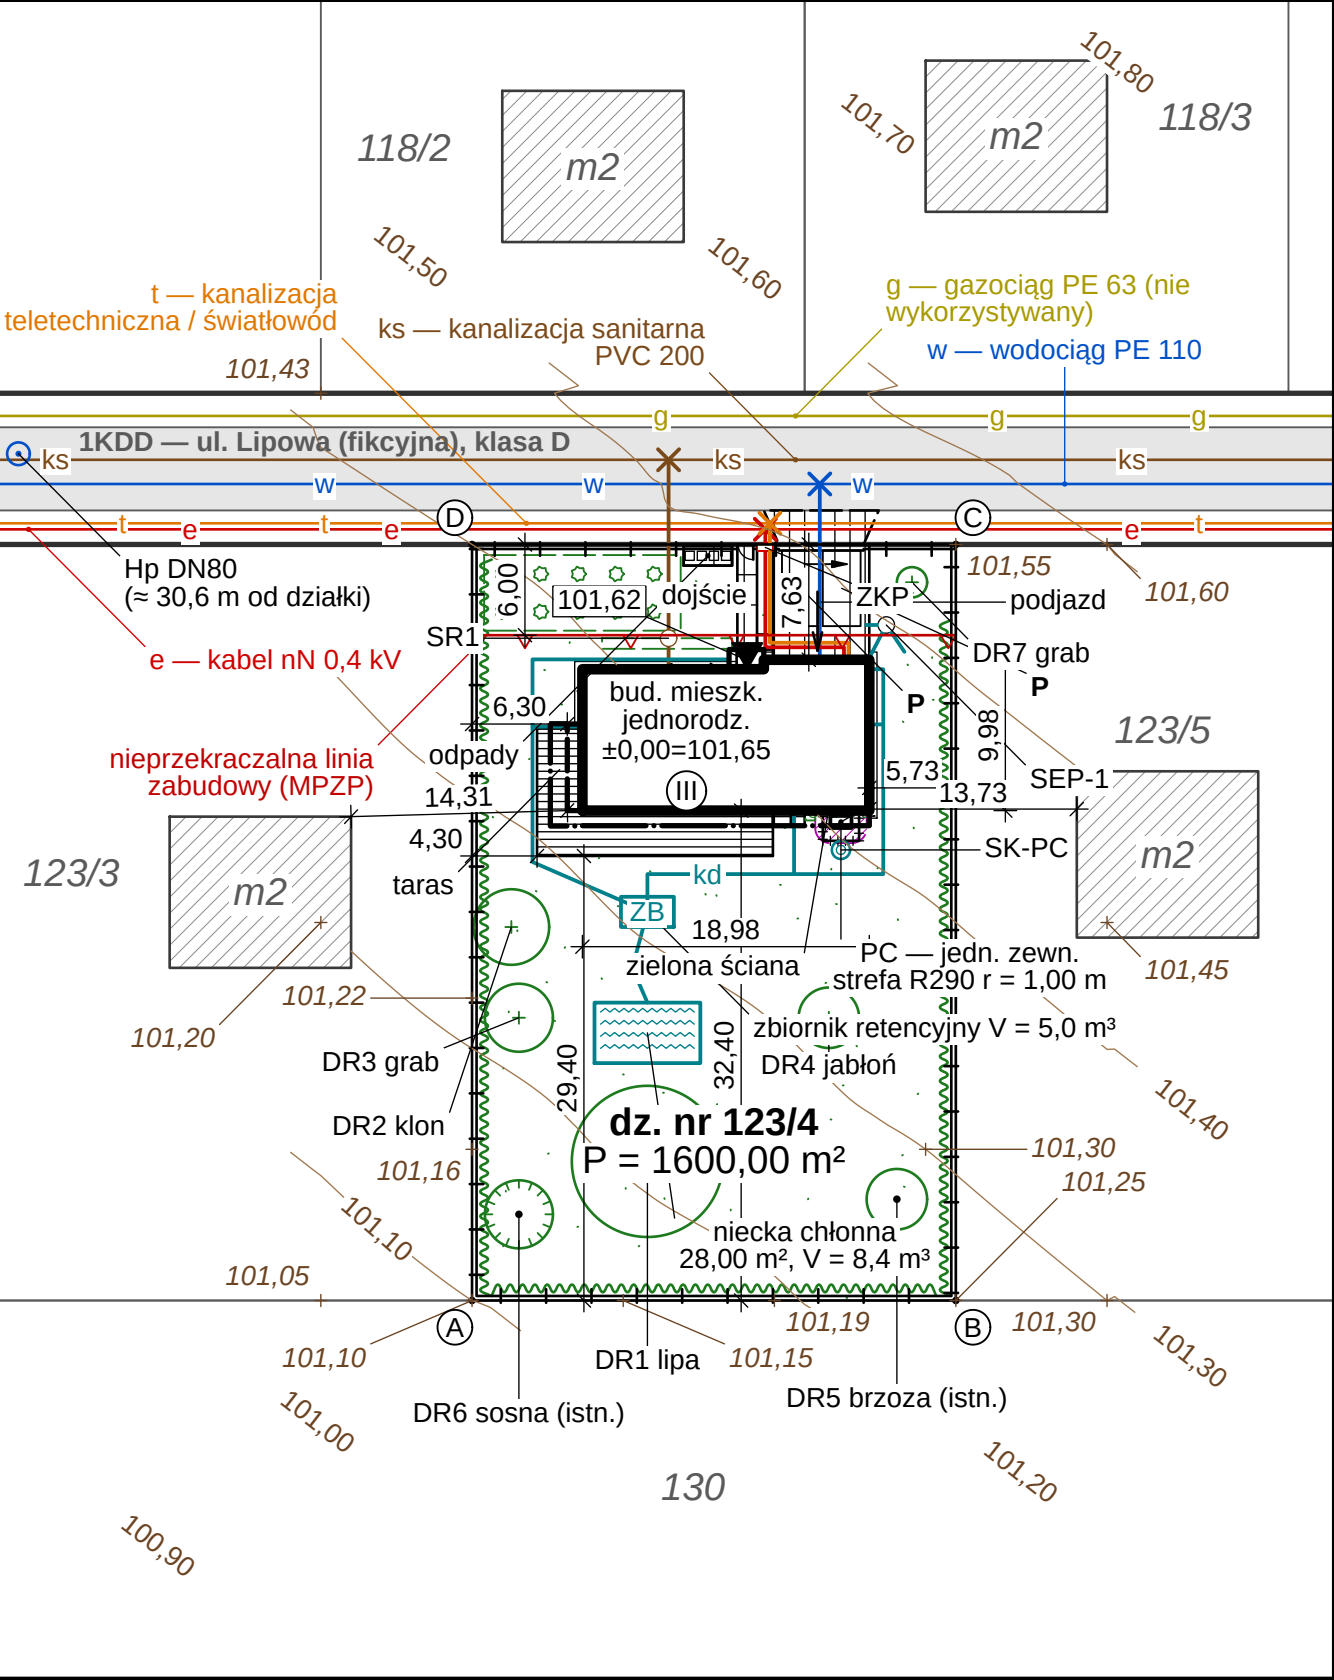

PLAN ZAGOSPODAROWANIA DZIAŁKI 1:500

LEGENDA

-
-

ZESTAWIENIE POWIERZCHNI I WSKAŹNIKÓW ZAGOSPODAROWANIA (RPB § 14 pkt 4, MPZP)

Wskaźnik / element	Projekt	MPZP / wymaganie	Zgodność
Powierzchnia działki nr 123/4	1600,00 m ²	—	
Pow. zabudowy (upzp art. 2 pkt 35)	187,50 m ²	≤ 480,00 m ²	TAK
Udział pow. zabudowy	11,72%	≤ 30%	TAK
— z płytami i okapami (kontrolnie)	218,08 m ² (13,63%)	informacyjnie	TAK
Drogi, dojeżdża, place	64,87 m ²	—	
Taras naziemne, podesty	66,62 m ²	—	
Opaska żwirowa	13,38 m ²	—	
PBC (upzp art. 2 pkt 28)	1270,23 m ² (79,39%)	≥ 800,00 m ² (50%)	TAK
— z 50 % dachu ziel. D4 (rezerwa)	1299,76 m ² (81,24%)	informacyjnie	
Pow. kondygnacji nadz. (P0+P1+P2)	396,39 m ²	80,00 m ² –1280,00 m ²	TAK
Nadziemna intensywność zabudowy	0,248	0,05–0,80	TAK
Wysokość zabudowy (art. 2 pkt 30)	10,47 m	≤ 11,00 m	TAK
Wysokość budynku (WT § 6)	9,97 m	N: ≤ 12,00 m	TAK
Kondygnacje nadziemne	3	≤ 3	TAK
Miejsca postojowe (garaż + zewn.)	2 + 2	≥ 2	TAK
Dach — kąt nachylenia	1,1° (płaski)	płaski ≤ 12° lub 30–45°	TAK
Lico ścian od linii zabudowy	1,63 m	nie przekraczać	TAK
Elementy poza linią zabudowy	brak	—	

MPZP: uchwała nr XII/123/2024 Rady Gminy Przykładowo z 21.03.2024 — teren 3MN (fikcyjny). Limity: ustalenia MPZP przyjęte w projekcie (dane przykładowe) — wypis i wyrys z MPZP [DO UZUPEŁNIENIA]. Wartości z modułu lamela.wskazniki (jedyne źródło; definicje upzp art. 2 pkt 28–35, t.j. Dz.U. 2026 poz. 538): PBC bez nawierzchni ażurowych, opaski, pojemników i terenu nad zbiornikiem; dach zielony (≥ 10 m²) w 50 % — tylko rezerwa. Wysokość zabudowy = z_top 111,85 (wyrzutnia wentylacji (dachowa, szczyt urządzenia)) – t_śr 101,38 (t_min 101,29, t_max 101,48 na obwodzie rzutu ścian zewn.; w każdym punkcie niższa z rzędnych terenu istniejącego/projektowanego). WT § 6: od terenu przy wejściu O0-03 (101,30) do wierzchu stropodachu D1 (bez attyki) — grupa N.

ODLEGŁOŚCI OD GRANIC DZIAŁKI (WT § 12)

Granica	Element (płaszczyzna ściany)	Odl. [m]	Wymagana [m]	Zgodność
S (130)	ściana P0 z otworami	32,40	≥ 4,00	TAK
S (130)	T1 — okap/płyta/taras	29,40	≥ 1,50	TAK
E (123/5)	ściana P0 z otworami	5,73	≥ 4,00	TAK
E (123/5)	ściana P2 bez otworów	15,60	≥ 3,00	TAK
E (123/5)	PL-D — okap/płyta/taras	5,73	≥ 1,50	TAK
N (1KDD)	ściana P0 z otworami	7,63	nie dot. (ust. 10)	—
N (1KDD)	ściana P2 bez otworów	11,88	nie dot. (ust. 10)	—
N (1KDD)	PL-DA — okap/płyta/taras	6,95	nie dot. (ust. 10)	—
W (123/3)	ściana P2 z otworami	6,30	≥ 4,00	TAK
W (123/3)	ściana P2 bez otworów	11,18	≥ 3,00	TAK
W (123/3)	T1 — okap/płyta/taras	4,30	≥ 1,50	TAK

WT § 12 ust. 1: 4,00 m — ściana z oknami/drzwiami, 3,00 m — bez otworów (każda płaszczyzna ściany osobno); ust. 6: 1,50 m — okap, taras, daszek; ust. 10: od działki drogowej — nie dotyczy. Odległość w poziomie w miejscu najmniejszego oddalenia (§ 9). WT stosowane na podstawie art. 102a PB.

OBSZAR ODDZIAŁYWANIA OBIEKTU (PB art. 3 pkt 20; RPB § 14 pkt 8)

Obszar oddziaływania obiektu mieści się w całości w granicach działki 123/4 (PB art. 3 pkt 20); odległości od granic ≥ 4,0 m (ściany z otworami ≥ 5,70 m, płyty ≥ 5,20 m), przesłanianie i nasłonecznienie sąsiednich budynków (≥ 8 m od granic) bez ograniczeń (WT §13, §60), hałas PC ≤ 40 dB(A) nocą na granicy (W-024), wody opadowe zagospodarowane na działce (PW art. 234), brak odprowadzania na drogę. Podstawa ustaleń (RPB § 18 pkt 1): WT § 12, 13, 19, 23, 28–29, 60, 271 (art. 102a PB); u.d.p. art. 43; POS art. 144 ust. 2 i rozp. MS w sprawie dopuszczalnych poziomów hałasu (Dz.U. 2014 poz. 112); PW art. 234; ustalenia MPZP.


OBJAŚNIENIA I UWAGI

- Wymiary i odległości w m (dokładność 0,01 m), rzędne w m n.p.m. (PL-EVRF2007-NH).
- Układ współrzędnych: lokalny układ działki (x → wschód, y → północ, początek w narożniku A); w projekcie rzeczywistym — układ PL-2000 strefa 6 z mapy do celów projektowych.
- Obrys budynku — lico zewnętrzne ścian parteru na wys. 1,0 m nad terenem; wspornik bryły A (II piętro) — obrys wyższych kondygnacji; płyty wspornikowe, okapy i daszek — przewieszenia (PN-B-01027 poz. 1.6).
- Wody opadowe zagospodarowane w granicach działki: rury spustowe → kolektory KD → zbiornik retencyjny szczelny → przelew do niecki chłonnej; odwodnienie liniowe przed bramą — brak spływu na drogę (MPZP; u.d.p. art. 39 ust. 1 pkt 9; WT § 28–29).
- Wymiary i rzędne szczegółowe — rys. PZT-02; uzbrojenie i koordynacja sieci — rys. PZT-03.
- Zjazd z drogi 1KDD pokazano jako przedłużenie bramy do krawędzi jezdni — geometria zastępcza [DO UZUPEŁNIENIA]; szerokość, skosy/łuki, nawierzchnia i przepust wg zezwolenia zarządcy drogi (u.d.p. art. 29 ust. 3a).
- Braki danych modelu (6 poz.) oznaczono [DO UZUPEŁNIENIA]; wykaz: projekt/02_PZT/BRAKI_DANYCH.md.
- Rysunek wygenerowany automatycznie z modelu model/budynek.yaml (wersja 1.0, 2026-09-25) — generatory lamela.views.

10 0 10 20 30 40 50 m
PODZIAŁKA 1:500



REW.	OPIS ZMIANY	DATA
0	Wydanie — rysunek wygenerowany z modelu	2026-09-25
PRACOWNIA PROJEKTOWA PRACOWNIA PROJEKTOWA — nazwa do uzupełnienia		STADIUM PB
adres pracowni do uzupełnienia		BRANŻA ZAGOSPODAROWANIE TERENU
INWESTOR (do uzupełnienia)		
OBIEKT / NAZWA ZAMIERZENIA BUDOWLANEGO Budynek mieszkalny jednorodzinny wolnostojący „Dom LAMELA” z zagospodarowaniem działki		
ADRES / LOKALIZACJA (NR DZIAŁKI, OBRĘB, JEDN. EWIDENCYJNA) ul. Lipowa (fikcyjna), dz. nr ewid. 123/4, obręb 0005 Przykładowo, gm. Przykładowo (fikcyjna)		KAT. OBIEKTU I
FUNKCJA	IMIĘ I NAZWISKO	SPECJALNOŚĆ, NR UPRAWNIENI
Projektant	[DO UZUPEŁNIENIA]	[DO UZUPEŁNIENIA]
Projektant (wsp.)	[DO UZUPEŁNIENIA]	[DO UZUPEŁNIENIA]
Sprawdzający	nie dotyczy (art. 20 ust. 3 pkt 2 PB)	—
Opracował	[DO UZUPEŁNIENIA]	[DO UZUPEŁNIENIA]
TYTUŁ RYSUNKU PLAN ZAGOSPODAROWANIA DZIAŁKI		
SKALA 1:500	FORMAT 420×530	DATA WYDANIA 2026-09-25
RODZAJ DOK. plan zagospodarowania	NR RYSUNKU PZT-01	ARKUSZ 1/3
REW. 0		

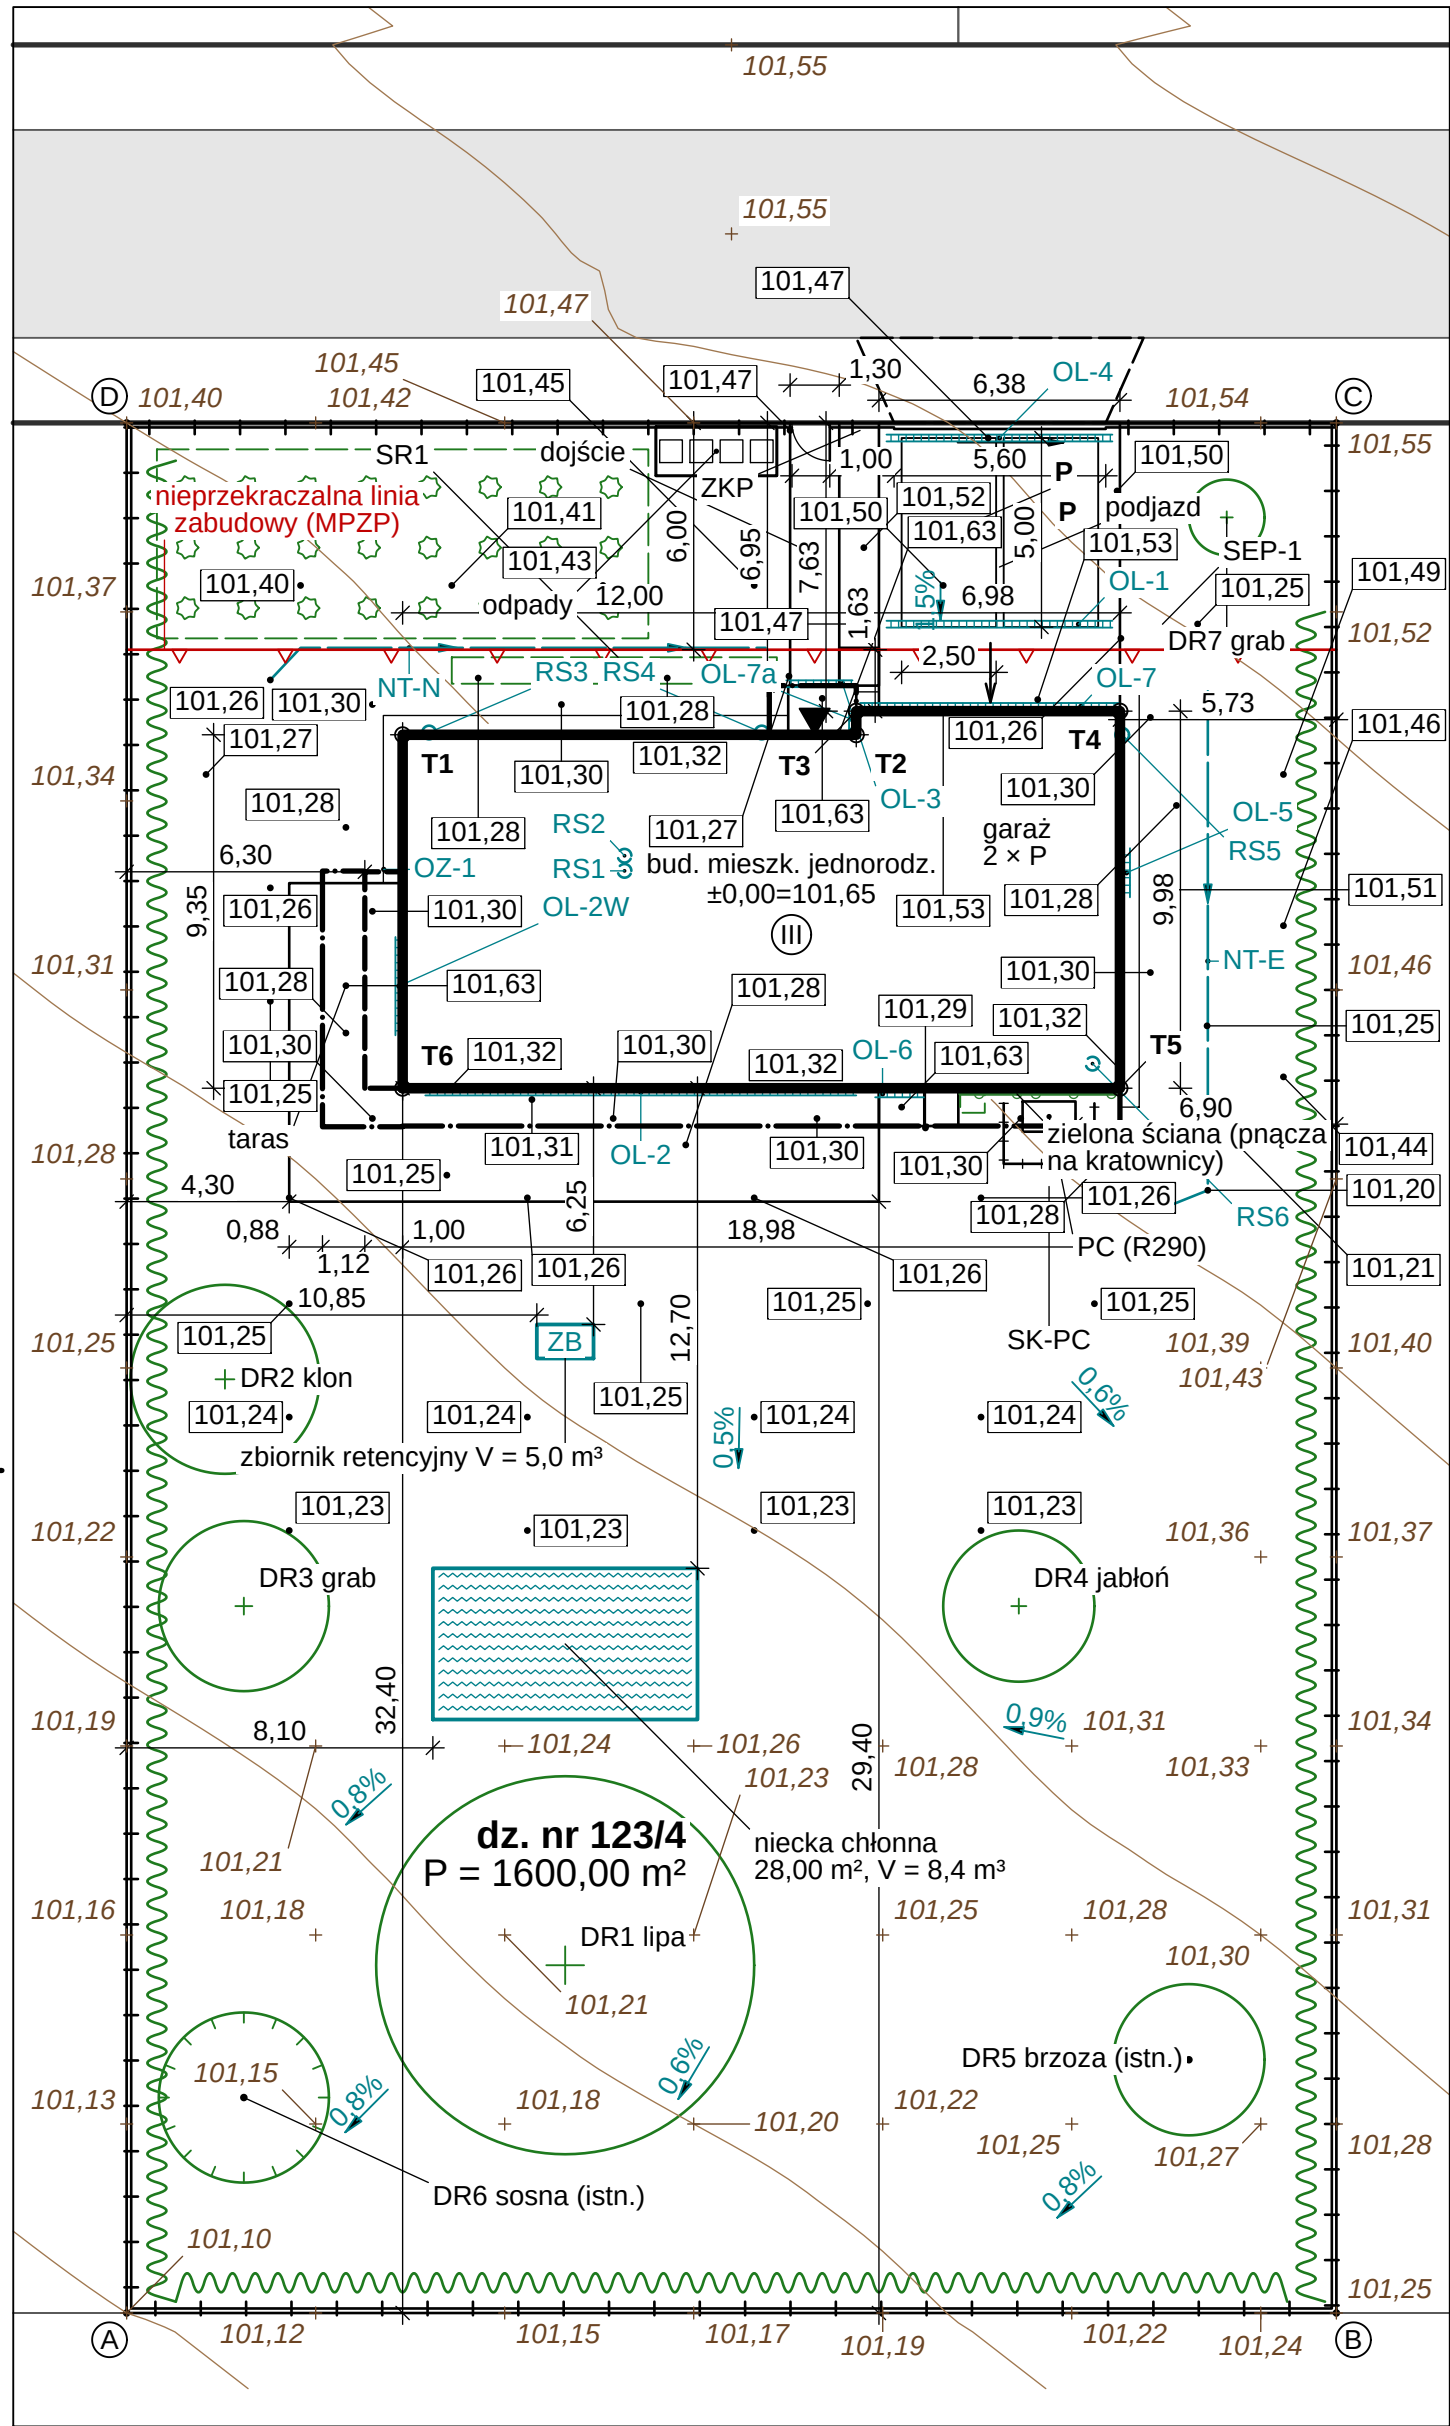

PLAN SZCZEGÓŁOWY — WYMIARY I RZĘDNE 1:200

WYKAZ PUNKTÓW TYCZENIA I GRANICZNYCH

Pkt	x [m]	y [m]	Opis
T1	7,30	41,75	narożnik obrysu parteru
T2	19,30	41,75	narożnik obrysu parteru
T3	19,30	42,38	narożnik obrysu parteru
T4	26,28	42,38	narożnik obrysu parteru
T5	26,28	32,40	narożnik obrysu parteru
T6	7,30	32,40	narożnik obrysu parteru
A	0,00	0,00	punkt graniczny działki
B	32,00	0,00	punkt graniczny działki
C	32,00	50,00	punkt graniczny działki
D	0,00	50,00	punkt graniczny działki

Układ lokalny działki: początek — narożnik A, x → wschód, y → północ. W projekcie rzeczywistym współrzędne w układzie PL-2000 (X — północ, Y — wschód) z mapy do celów projektowych; tyczenie — geodeta uprawniony (PB art. 43 ust. 1).

RZĘDNE CHARAKTERYSTYCZNE [m n.p.m.]

Poziom	Rzędna
±0,00 — posadzka parteru	101,65
T1 — deska kompozytowa na legarach i wspornikach regulowanych, szczeliny 5 mm	101,63
T2 — płyty betonowe 60×60 na podsypce, spadek 2 % od drzwi	101,63
T3 — płyty betonowe 60×60, spadek 2 % od drzwi	101,63
teren proj. przy wejściu głównym	101,62
teren na obwodzie ścian — min.	101,29
teren na obwodzie ścian — maks.	101,48
najwyższy punkt budynku	111,85
zwierciadło wody gruntowej (ZWG)	97,60

Rzędne projektowane terenu: spadek ≥ 2 % od budynku; na granicach działki rzędne istniejące (bez zmiany spływu na działki sąsiednie — WT § 29, PW art. 234).

ODWODNIENIE POWIERZCHNIOWE

Ozn.	Typ	Wymiar	Spadek	Odbiornik
OL-1	liniowe	L = 5,98 m	0,5 %	SEP-1 → NT-E
OL-2	liniowe	L = 11,40 m	0,5 %	opaska / KD-W
OL-2W	liniowe	L = 2,60 m	0,5 %	KD-W
OL-3	liniowe	L = 1,75 m	0,5 %	KD-W
OL-7	liniowe	L = 6,88 m	0,5 %	SEP-1 → NT-E
OL-7a	liniowe	L = 0,70 m	0,5 %	OL-7 → SEP-1
OL-4	liniowe	L = 5,98 m	0,5 %	SEP-1 → NT-E
OZ-1	opaska żwir.	b = 0,50 m	—	—
NT-N	niecka	L = 13,47 m	0,5 %	pas zach. → ogród pd.
NT-E	niecka	L = 14,28 m	0,5 %	ogród pd.
OL-5	liniowe	L = 1,30 m	0,5 %	KD-E
OL-6	liniowe	L = 1,30 m	0,5 %	RS8 → KD-E
NCH-1	niecka	A = 28,00 m²	—	grunt (piaski, ZWG 3,8 m p.p.t.)

DR-0: NIE PROJEKTUJE SIĘ — piaski przepuszczalne, ZWG ≈ 3,8 m p.p.t., posadowienie ≈ 0,5 m p.p.t. (W-285); ochrona płyty: XPS + membrana SBS, opaska żwirowa i spadki terenu

NAWIERZCHNIE UTWARDZONE I TARASY

Ozn.	Nawierzchnia	Pow.	Spadek
U1	podjazd	48,61 m²	1,5 %
U2	dojście	9,04 m²	2,0 %
U3	łącznik dojście-podjazd	1,05 m²	2,0 %
U4	stanowisko pojemników	4,16 m²	2,0 %
U5	fundament jednostki zewn. PC na wibroizolacji	1,12 m²	—
U6	ścieżka gospodarcza	0,90 m²	2,0 %
T1	deska kompozytowa na legarach i wspornikach regulowanych, szczeliny 5 mm	63,08 m²	rz. 101,63
T2	płyty betonowe 60×60 na podsypce, spadek 2 % od drzwi	2,34 m²	rz. 101,63
T3	płyty betonowe 60×60, spadek 2 % od drzwi	1,20 m²	rz. 101,63

Kierunek spadku — strzałki na rysunku (od budynku, do odwodnień liniowych i niecek).

ODLEGŁOŚCI URZĄDZEŃ RETENCJI I PC

Element	Od	d [m]	min [m]	Zgodność
zbiornik	budynek	6,70	3,00	TAK
zbiornik	granica	11,60	2,00	TAK
zbiornik	drzewo	9,06	1,00	TAK
niecka	budynek	12,70	3,00	TAK
niecka	granica	8,10	2,00	TAK
niecka	drzewo	5,00	1,00	TAK
strefa R290	otwory, wpusty, studzienki	—	r = 1,00	TAK


Wymagania retencji — założenia projektowe (R8 pkt 3.5, W-144/W-145; nie przepis); zbiornik — odległość od środka (brak wymiarów w modelu); strefa R290 — W-156 (wytyczne producenta).

LEGENDA


	granica działki budowlanej, punkt graniczny, narożnik (PN-B-01027 poz. 2.7)		drzewo liściaste projektowane (poz. 7.1)
	linia rozgraniczająca drogi publicznej (PN-B-01027 poz. 2.5)		drzewo istniejące — zachowane (poz. 7.2)
	jezdnia drogi publicznej (wg mapy)		ogrodzenie projektowane (poz. 2.8; na granicy — odsunięte graficznie)
	nieprzekraczalna linia zabudowy wg MPZP (PN-B-01027 poz. 2.2)		brama przesuwna (poz. 2.9)
	budynek projektowany — obrys ścian parteru 1,0 m nad terenem (poz. 1.1)		furtka otwierana do wewnątrz działki (WT § 42)
	obrys wyższych kondygnacji poza obrysem parteru (poz. 1.6 d)		ażurowa osłona z lamel jednostki PC (bez dachu, prześwit przy terenie)
	obrys płyt wspornikowych, okapów i daszków — przewieszenia (poz. 1.6 c)		zielona ściana — pnącza na kratownicy stalowej odsuniętej od elewacji
	rzędna ±0,00 (posadzka parteru) w m n.p.m.; w kółku liczba kondygnacji nadziemnych		zbiornik retencyjny szczelny (ZB)
	wejście główne do budynku (poz. 1.7)		niecka chłonna — ogród deszczowy (przelew zbiornika)
	wjazd do garażu		odwodnienie liniowe
	zjazd z drogi publicznej — wg zezwolenia zarządcy drogi [DO UZUPEŁNIENIA]		niecka trawiasta — grot w kierunku spływu rura spustowa: zewnętrzna / w szachcie (RS)
	nawierzchnia z kostki betonowej (poz. 7.10)		warstwica terenu istniejącego (PN-B-01027 poz. 5.2)
	nawierzchnia z płyt betonowych (poz. 7.11)		rzędna terenu istniejącego [m n.p.m.]
	płyty w trawie (ażur) — poza PBC		rzędna terenu projektowanego [m n.p.m.]
	taras naziemny — deska kompozytowa na legarach		spadek nawierzchni [%] — grot w kierunku spadku
	opaska żwirowa 16/32 na geowłókninie		kierunek spływu wód opadowych, spadek terenu [%]
	stanowisko postojowe 2,50 × 5,00 m (WT § 21)		wymiar / odległość w m z dokładnością 0,01 m
	osłona pojemników na odpady — segregacja (WT § 22)		punkt tyczenia (narożnik obrysu parteru) — wykaz współrzędnych
	rabata z krzewami		
	żywoplot projektowany (poz. 7.6)		

OBJAŚNIENIA I UWAGI


- Wymiary i odległości w m (dokładność 0,01 m), rzędne w m n.p.m. (PL-EVRF2007-NH).
- Wymiary obrysu — lico zewnętrzne ścian parteru (1,0 m nad terenem); odległości od granic w miejscu najmniejszego oddalenia (WT § 9), z dokładnością 0,01 m (RPB § 15 ust. 3 w brzmieniu Dz.U. 2026 poz. 597, od 5.11.2026 — stosowane).
- Rzędne terenu istniejącego — z mapy (przykładowej); projektowanego — z modelu (działka.yaml: teren.punkty_projektowane); spadki nawierzchni wg modelu, kierunek wg terenu projektowanego; kierunki spływu na trawnikach — wg spadku terenu projektowanego (interpolacja).
- Wody opadowe z nawierzchni i dachów — na teren własny, do niecek i zbiornika (WT § 28 ust. 2); zakaz zmiany spływu w kierunku działek sąsiednich (WT § 29) i odprowadzania na drogę (u.d.p. art. 39).
- Punkty tyczenia — narożniki obrysu zewnętrznego ścian parteru; współrzędne w wykazie obok rysunku.
- Zjazd — geometria zastępcza [DO UZUPEŁNIENIA] (wg zezwolenia zarządcy drogi).
- Braki danych modelu oznaczono [DO UZUPEŁNIENIA]; wykaz: projekt/02_PZT/BRAKI_DANYCH.md.
- Rysunek wygenerowany automatycznie z modelu model/budynek.yaml (wersja 1.0, 2026-09-25) — generatory lamela.views.

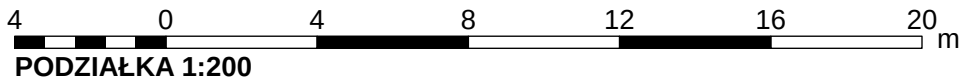

PODZIAŁKA 1:200

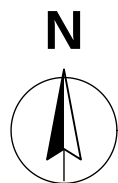

REW.	OPIS ZMIANY		DATA			
0	Wydanie — rysunek wygenerowany z modelu		2026-09-25			
PRACOWNIA PROJEKTOWA PRACOWNIA PROJEKTOWA — nazwa do uzupełnienia adres pracowni do uzupełnienia			STADIUM PB	BRANŻA ZAGOSPODAROWANIE TERENU		
INWESTOR (do uzupełnienia)						
OBIEKT / NAZWA ZAMIERZENIA BUDOWLANEGO Budynek mieszkalny jednorodzinny wolnostojący „Dom LAMELA” z zagospodarowaniem działki						
ADRES / LOKALIZACJA (NR DZIAŁKI, OBRĘB, JEDN. EWIDENCYJNA) ul. Lipowa (fikcyjna), dz. nr ewid. 123/4, obręb 0005 Przykładowo, gm. Przykładowo (fikcyjna)				KAT. OBIEKTU I		
FUNKCJA	IMIĘ I NAZWISKO	SPECJALNOŚĆ, NR UPRAWNIENI		DATA	PODPIS	
Projektant	[DO UZUPEŁNIENIA]	[DO UZUPEŁNIENIA]				
Projektant (wsp.)	[DO UZUPEŁNIENIA]	[DO UZUPEŁNIENIA]				
Sprawdzający	nie dotyczy (art. 20 ust. 3 pkt 2 PB)		—			
Opracował	[DO UZUPEŁNIENIA]	[DO UZUPEŁNIENIA]				
TYTUŁ RYSUNKU PLAN SZCZEGÓŁOWY — WYMIARY I RZĘDNE						
SKALA 1:200	FORMAT 594×430	DATA WYDANIA 2026-09-25	RODZAJ DOK. plan szczegółowy	NR RYSUNKU PZT-02	ARKUSZ 2/3	REW. 0

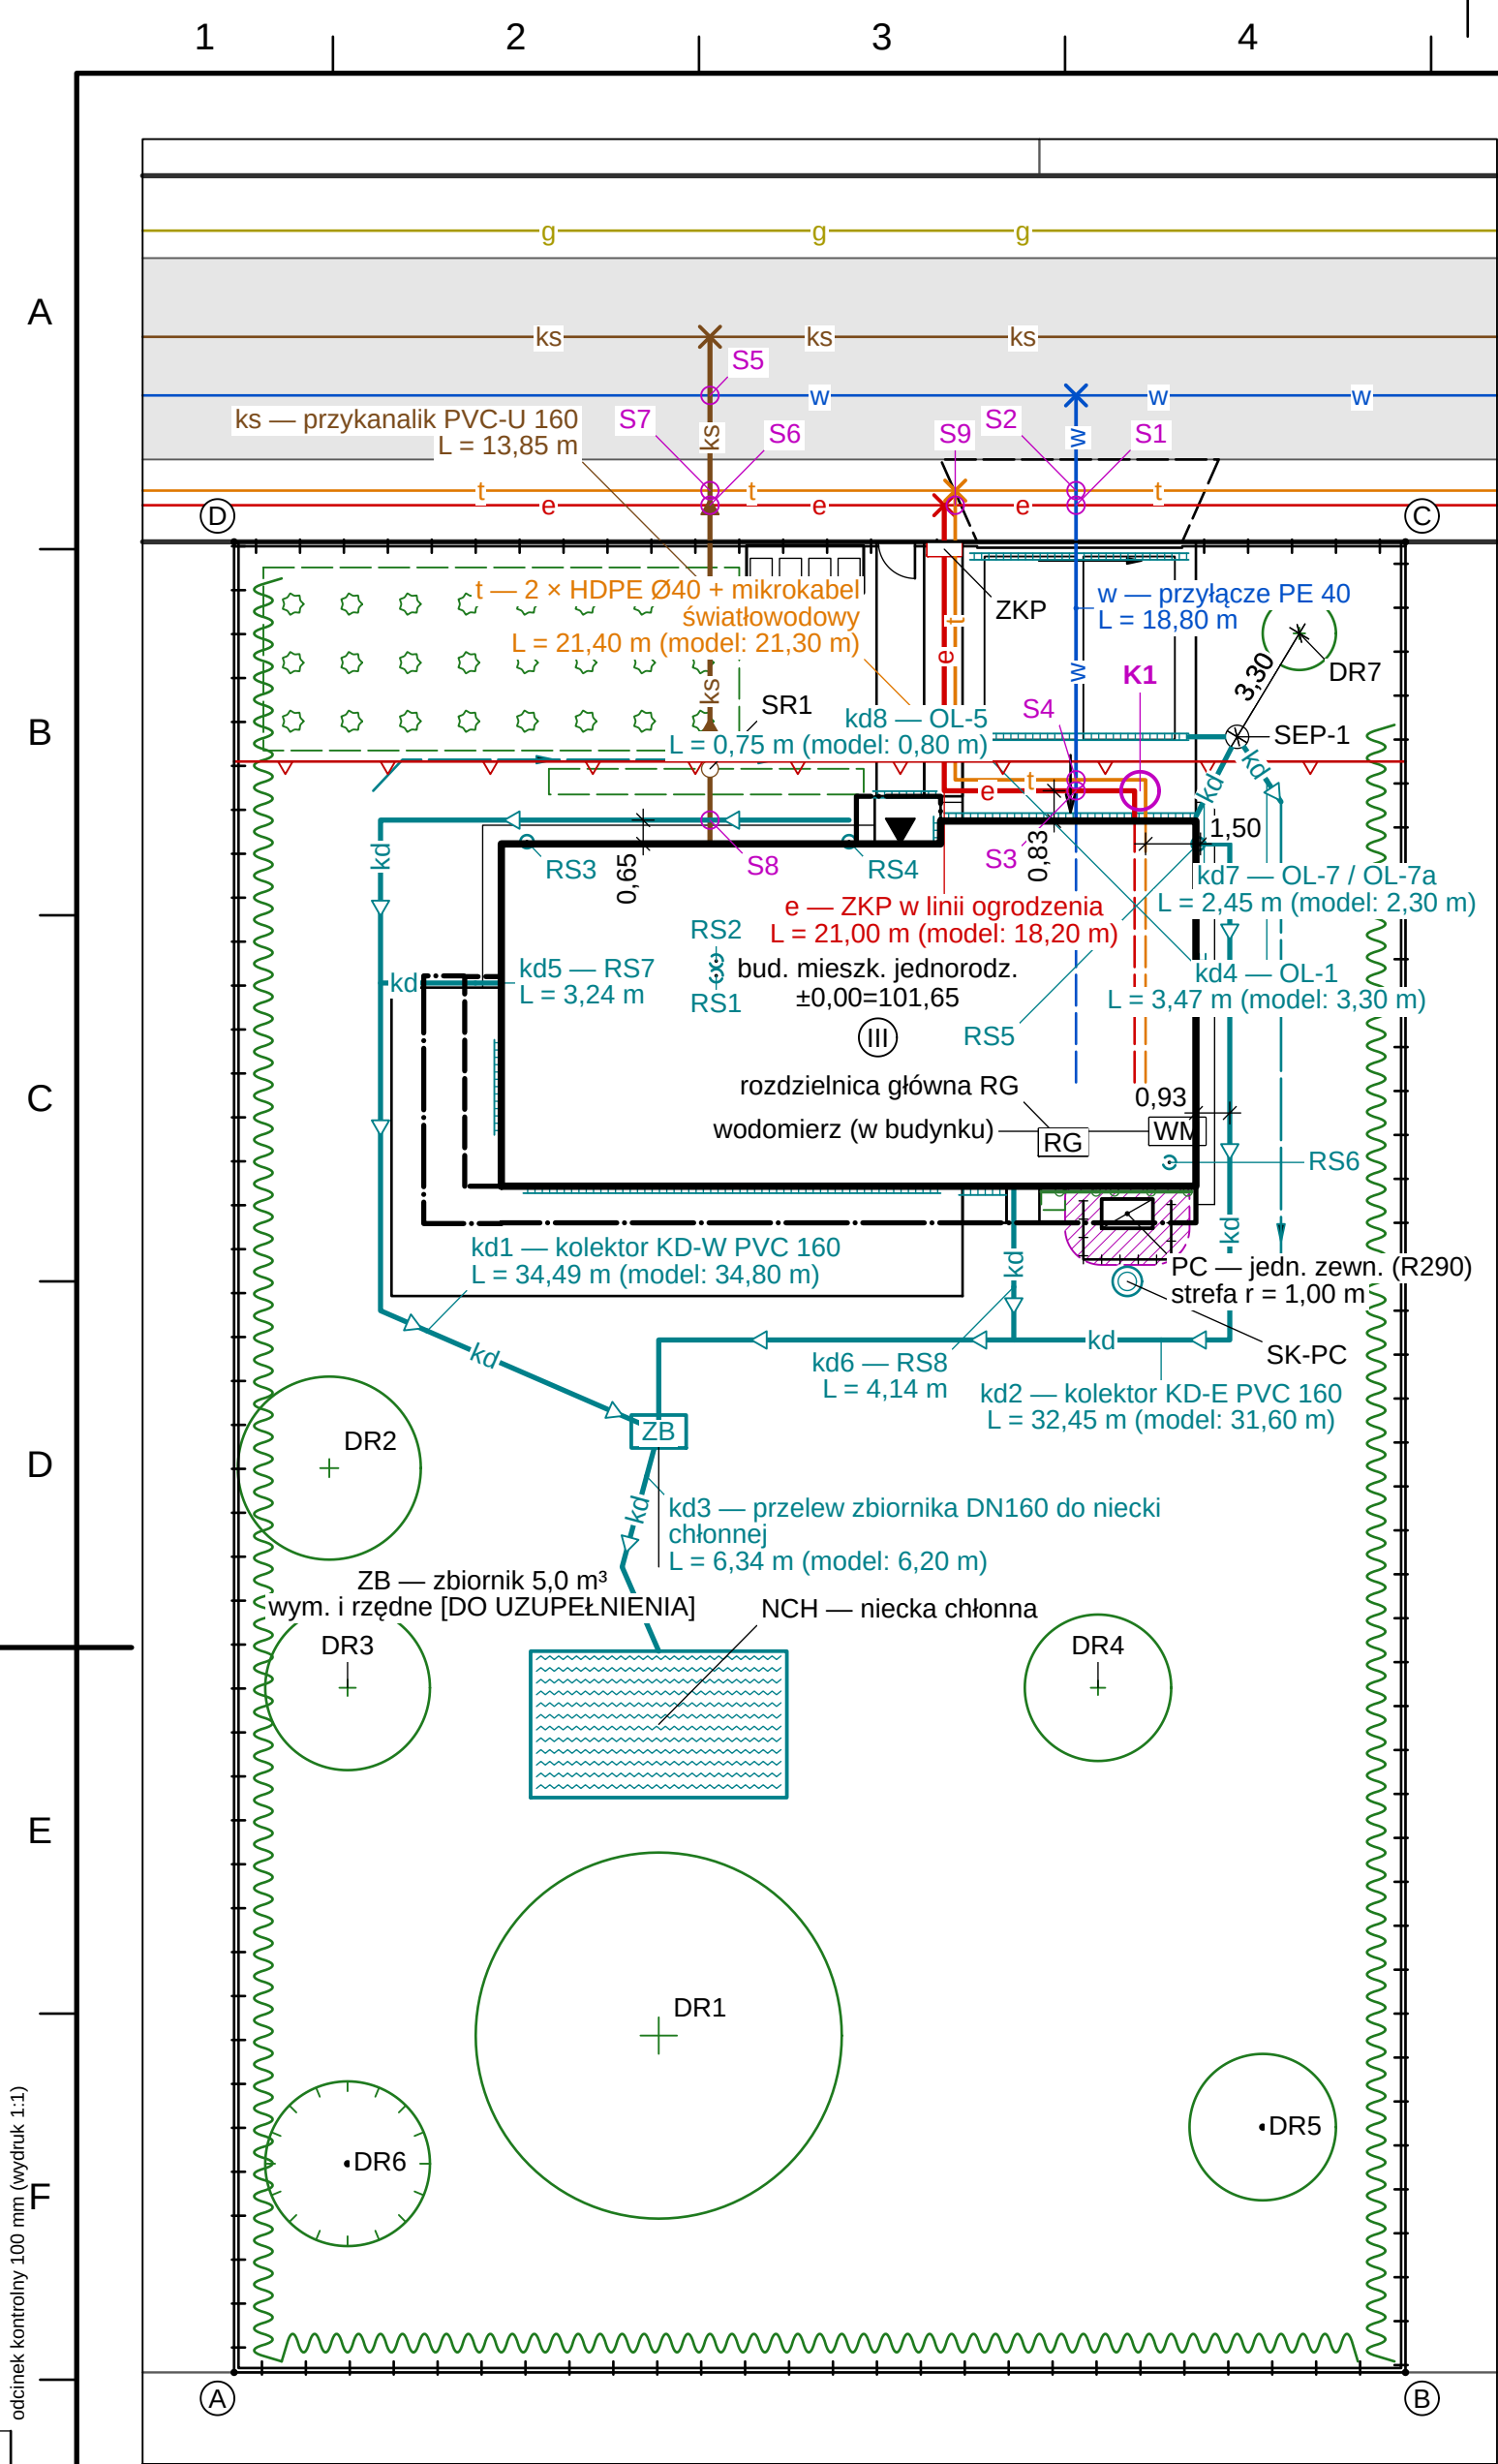

RYSUNEK KOORDYNACYJNY UZBROJENIA TERENU 1:200

OBJAŚNIENIA I UWAGI

- 1. Wymiary i odległości w m (dokładność 0,01 m), rzędne w m n.p.m. (PL-EVRF2007-NH).
- 2. Oznaczenia sieci — kolory i litery wg mapy zasadniczej (zał. 4 rozp. w sprawie BDOT500 i mapy zasadniczej, Dz.U. 2021 poz. 1385): w — wodociąg, ks — kanalizacja sanitarna, kd — kanalizacja deszczowa, e — elektroenergetyczna, t — telekomunikacyjna, g — gazowa; istniejące — linia cienka (wg mapy), projektowane — gruba; w budynku/pod płytą — kreskowa; „x” — włączenie do sieci.
- 3. Przyłącza w granicach działki nie podlegają naradzie koordynacyjnej ZUD (PGiK art. 28b); roboty w pasie drogowym 1KDD — za zezwoleniem zarządcy drogi (u.d.p. art. 40).
- 4. Skrzyżowań: 9; zbliżeń poniżej wartości minimalnych: 1 (tabela „Kolizje i zbliżenia”).
- 5. Wody opadowe: rury spustowe RS → kolektory kd → zbiornik ZB → przelew do niecki chłonnej NCH; odwodnienia liniowe OL → kolektory kd (WT § 28 ust. 2).
- 6. Drenaż opaskowy DR-0: NIE PROJEKTUJE SIĘ — piaski przepuszczalne, ZWG ≈ 3,8 m p.p.t., posadowienie ≈ 0,5 m p.p.t. (W-285); ochrona płyty: XPS + membrana SBS, opaska żwirowa i spadki terenu

KOORDYNACJA — ODLEGŁOŚCI POZIOME MIĘDZY SIECIAMI

Para sieci	d [m]	min [m]	Źródło wymagania	Zgodność
w – ks ist.	3,15	1,50	praktyka proj. (COBRTI INSTAL z. 3)*	TAK
w – kd2	3,40	1,50	praktyka proj. (COBRTI INSTAL z. 3)*	TAK
w – kd4	3,08	1,50	praktyka proj. (COBRTI INSTAL z. 3)*	TAK
w – kd6	3,33	1,50	praktyka proj. (COBRTI INSTAL z. 3)*	TAK
w – kd7	3,28	1,50	praktyka proj. (COBRTI INSTAL z. 3)*	TAK
w – kd8	3,45	1,50	praktyka proj. (COBRTI INSTAL z. 3)*	TAK
e – t ist.	1,02	0,50	N SEP-E-004:2014*	TAK
e – t	0,30	0,50	N SEP-E-004:2014*	warunk.
e – kd1	2,72	0,50	N SEP-E-004:2014*	TAK
e – kd2	1,80	0,50	N SEP-E-004:2014*	TAK
e – kd4	2,09	0,50	N SEP-E-004:2014*	TAK
e – kd7	1,68	0,50	N SEP-E-004:2014*	TAK
e – kd8	1,85	0,50	N SEP-E-004:2014*	TAK
t – kd2	1,50	0,50	praktyka proj.*	TAK
t – kd4	1,66	0,50	praktyka proj.*	TAK
t – kd7	1,38	0,50	praktyka proj.*	TAK
t – kd8	1,55	0,50	praktyka proj.*	TAK
kd4 – DR7 (pień)	3,30	2,00	od pnia*	TAK
kd7 – DR7 (pień)	3,30	2,00	od pnia*	TAK
e – budynek	0,83	—	informacyjnie (lico ściany)	—
kd1 – budynek	0,65	—	informacyjnie (lico ściany)	—
kd2 – budynek	0,93	—	informacyjnie (lico ściany)	—
kd4 – budynek	2,22	—	informacyjnie (lico ściany)	—

* wartości minimalne wg zasad wiedzy technicznej (N SEP-E-004, praktyka projektowa) — NIE są przepisem: WT § 26–28 określają tylko wymagania ogólne uzbrojenia działki; do potwierdzenia w warunkach przyłączenia gestorów [SPRAWDŹ]. „warunk.” — dopuszczalne przy rurach osłonowych.

OBJAŚNIENIA I UWAGI (cd.)

- 7. Braki danych modelu (6 poz.) — [DO UZUPEŁNIENIA]; wykaz: projekt/02_PZT/BRAKI_DANYCH.md.
- 8. Rysunek wygenerowany automatycznie z modelu model/budynek.yaml (wersja 1.0, 2026-09-25) — generatory lamela.views.

SIECI I PRZYŁĄCZA — PROJEKTOWANE I ISTNIEJĄCE

Ozn.	Sieć	Opis	L [m]	L model [m]
w	przyłącze wodociągowe	przyłącze PE 40	18,80	18,80
ks	kanalizacja sanitarna	przykanalik PVC-U 160	13,85	13,90
e	elektroenergetyczna nN (kabel)	ZKP w linii ogrodzenia	21,00	18,20
t	telekomunikacyjna (światłowod)	2 × HDPE Ø40 + mikrokabel światłowodowy	21,40	21,30
kd1	kanalizacja deszczowa	kolektor KD-W PVC 160	34,49	34,80
kd2	kanalizacja deszczowa	kolektor KD-E PVC 160	32,45	31,60
kd3	kanalizacja deszczowa	przelew zbiornika DN160 do niecki chłonnej	6,34	6,20
kd4	kanalizacja deszczowa	OL-1	3,47	3,30
kd5	kanalizacja deszczowa	RS7	3,24	3,20
kd6	kanalizacja deszczowa	RS8	4,14	4,10
kd7	kanalizacja deszczowa	OL-7 / OL-7a	2,45	2,30
kd8	kanalizacja deszczowa	OL-5	0,75	0,80
w ist.	istniejąca (mapa)	wodociąg PE 110	—	—
ks ist.	istniejąca (mapa)	kanalizacja sanitarna PVC 200	—	—
e ist.	istniejąca (mapa)	kabel nN 0,4 kV	—	—
t ist.	istniejąca (mapa)	kanalizacja teletechniczna / światłowod	—	—
g ist.	istniejąca (mapa)	gazociąg PE 63 (nie wykorzystywany)	—	—

L — długość trasy w rzucie (z częścią pod budynkiem, linia kreskowa); średnice, spadki i rzędne dna przewodów [DO UZUPEŁNIENIA] (RPB § 15 ust. 2 pkt 11 — brak w modelu).

OBIEKTY UZBROJENIA I ODWODNIENIA

Ozn.	Opis
ZKP	złącze kablowo-pomiarowe we wnęce ogrodzenia
SR1	studzienka rewizyjna kanalizacji Ø425
PC-JZ	jednostka zewn. PC monoblok R290 w osłonie lamelowej z ekranem akustycznym od tarasu
SEP-1	osadnik z separatorem substancji ropopochodnych
SK-PC	studnia chłonna skroplin PC
HYDR	najbliższy hydrant zewnętrzny DN80
RS1	rura spustowa DN100 (w szachcie) z dachu D1
RS2	rura spustowa DN100 (w szachcie) z dachu D1
RS3	rura spustowa DN100 (zewn.) z dachu D2
RS4	rura spustowa DN100 (zewn.) z dachu D3
RS5	rura spustowa DN100 (zewn.) z dachu D4
RS6	rura spustowa DN100 (w szachcie) z dachu D4

LEGENDA

granica działki budowlanej, punkt graniczny, narożnik (PN-B-01027 poz. 2.7)

linia rozgraniczająca drogi publicznej (PN-B-01027 poz. 2.5)

jezdnia drogi publicznej (wg mapy)

nieprzekraczalna linia zabudowy wg MPZP (PN-B-01027 poz. 2.2)

budynek projektowany — obrys ścian parteru 1,0 m nad terenem (poz. 1.1)

obrys wyższych kondygnacji poza obrysem parteru (poz. 1.6 d)

obrys płyt wspornikowych, okapów i daszku — przewieszenia (poz. 1.6 c)

węście główne do budynku (poz. 1.7)

wjazd do garażu

zjazd z drogi publicznej — wg zezwolenia zarządcy drogi [DO UZUPEŁNIENIA]

nawierzchnia z kostki betonowej (poz. 7.10)

nawierzchnia z płyt betonowych (poz. 7.11)

płyty w trawie (ażur) — poza PBC

taras naziemny — deska kompozytowa na legarach

opaska żwirowa 16/32 na geowłókninie

stanowisko postojowe 2,50 × 5,00 m (WT § 21)

osłona pojemników na odpady — segregacja (WT § 22)

rabata z krzewami

żywoplot projektowany (poz. 7.6)

drzewo liściaste projektowane (poz. 7.1)

drzewo istniejące — zachowane (poz. 7.2)

ogrodzenie projektowane (poz. 2.8; na granicy — odsunięte graficznie)

brama przesuwna (poz. 2.9)

furtka otwierana do wewnątrz działki (WT § 42)

jednostka zewn. pompy ciepła (fundament) i strefa czynnika R290

ażurowa osłona z lamel jednostki PC (bez dachu, prześwit przy terenie)

zielona ściana — pnąca na kratownicy stalowej odsuniętej od elewacji

zbiornik retencyjny szczelny (ZB)

niecka chłonna — ogród deszczowy (przelew zbiornika)

odwodnienie liniowe

niecka trawiasta — grot w kierunku spływu

rura spustowa: zewnętrzna / w szachcie (RS)

miejsce włączenia przyłącza do sieci (PN-B-01027 poz. 6)

złącze kablowo-pomiarowe ZKP (w linii ogrodzenia)

studzienka rewizyjna kanalizacji

studnia chłonna skroplin pompy ciepła

wymiar / odległość w m z dokładnością 0,01 m

skrzyżowanie sieci — zachować odstęp pionowy (tabela)

zbliżenie / kolizja sieci (nr w tabeli koordynacji)

w — sieć wodociągowa istniejąca (mapa)

w — przyłącze wodociągowe projektowane

ks — sieć kanalizacji sanitarnej istniejąca (mapa)

ks — przykanalik sanitarny projektowany

kd — kanalizacja deszczowa projektowana (kolektory, przelew)

e — linia kablowa nN istniejąca (mapa)

e — kabel nN projektowany (ZKP → RG)

t — sieć telekomunikacyjna istniejąca (mapa)

t — przyłącze telekomunikacyjne projektowane

g — sieć gazowa istniejąca (mapa)

SKRZYŻOWANIA SIECI


Nr	Sieci	x [m]	y [m]
S1	w × e ist.	23,00	51,00
S2	w × t ist.	23,00	51,40
S3	w × e	23,00	43,20
S4	w × t	23,00	43,50
S5	ks × w ist.	13,00	54,00
S6	ks × e ist.	13,00	51,00
S7	ks × t ist.	13,00	51,40
S8	ks × kd1	13,00	42,40
S9	t × e ist.	19,70	51,00

Odstępy pionowe na skrzyżowaniach — wg warunków gestorów sieci [DO UZUPEŁNIENIA] (brak rzędnych przewodów w modelu); kable w rurach osłonowych w obrębie skrzyżowań.

KOLIZJE I ZBLIŻENIA

Nr	Rodzaj	Opis	Ocena
K1	zbliżenie sieci	e-t: 0,30 m < 0,50 m	warunk.

K1: dopuszczalne przy ułożeniu w rurach osłonowych — uzgodnić z gestorami

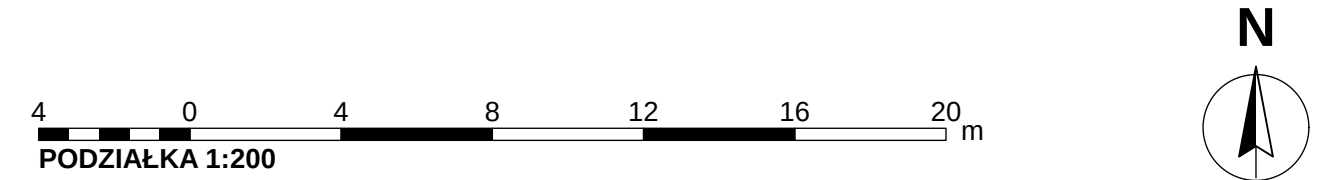

REW.	OPIS ZMIANY		DATA	
0	Wydanie — rysunek wygenerowany z modelu		2026-09-25	
PRACOWNIA PROJEKTOWA PRACOWNIA PROJEKTOWA — nazwa do uzupełnienia adres pracowni do uzupełnienia		STADIUM PB	BRANŻA ZAGOSPODAROWANIE TERENU	
INWESTOR (do uzupełnienia)				
OBIEKT / NAZWA ZAMIERZENIA BUDOWLANEGO Budynek mieszkalny jednorodzinny wolnostojący „Dom LAMELA” z zagospodarowaniem działki				
ADRES / LOKALIZACJA (NR DZIAŁKI, OBRĘB, JEDN. EWIDENCYJNA) ul. Lipowa (fikcyjna), dz. nr ewid. 123/4, obręb 0005 Przykładowo, gm. Przykładowo (fikcyjna)				KAT. OBIEKTU I
FUNKCJA	IMIĘ I NAZWISKO	SPECJALNOŚĆ, NR UPRAWNIENI	DATA	PODPIS
Projektant	[DO UZUPEŁNIENIA]	[DO UZUPEŁNIENIA]		
Projektant (wsp.)	[DO UZUPEŁNIENIA]	[DO UZUPEŁNIENIA]		
Sprawdzający	nie dotyczy (art. 20 ust. 3 pkt 2 PB)	—		
Opracował	[DO UZUPEŁNIENIA]	[DO UZUPEŁNIENIA]		
TYTUŁ RYSUNKU RYSUNEK KOORDYNACYJNY UZBROJENIA TERENU				
SKALA 1:200	FORMAT 610×450	DATA WYDANIA 2026-09-25	RODZAJ DOK. rysunek koordynacyjny	NR RYSUNKU PZT-03
ARKUSZ 3/3		REW. 0		