


OZNACZENIA NA RYSUNKU


- pręt reprezentatywny grupy (warstwa dolna), linia gruba
- pręt z odgięciem 90° — odgięcie (ramię) pokazane w płaszczyźnie rysunku
- linia rozkładu prętów grupy (zasieg), kółko — pręt reprezentatywny
- numer pozycji pręta (zestawienie stali)
- strefa zbrojenia narożnego (0,2·l_{min}) — pręty górą i dołem w 2 kierunkach
- ściany / belki / słupy pod płytą (widok zasłonięty)

OBJAŚNIENIA I UWAGI

1. Wymiary w cm (mm w indeksie górnym, np. 24^s = 24,5 cm), rzędne w m względem ±0,000 = 101,650 m n.p.m. (PL-EVRF2007-NH).
2. Zestawienie stali, strefy zbrojenia narożnego/na ścianinie i dozbrojenia — arkusz PT-BO-17.
3. Stal zbrojeniowa B500SP (klasa ciągliwości C, f_{yk} = 500 MPa) wg PN-H-93220:2018-02 / PN-EN 10080; pręty gięte na zimno na trzpieniach $\phi_m \geq 4\phi$ ($\phi \leq 16$ mm) i $\geq 7\phi$ ($\phi > 16$ mm) — PN-EN 1992-1-1 tabl. 8.1N; oznaczenia prętów i kształtów wg PN-EN ISO 3766 (liczba, nr pozycji, ϕ , rozstaw [cm], długość rozwinięcia l [cm]).
4. Otuliny zapewnić podkładkami dystansowymi (rozstaw $\leq 1,0$ m, dla siatek górnych — podpórki „kobyłki” $\leq 1,0$ m) — PN-EN 13670 p. 6.5; odchyłka wykonawcza $\Delta c_{dev} = 10$ mm uwzględniona w c_{nom} (PN-EN 1992-1-1 4.4.1.3 + NA).
5. Pręty łączyć na zakład l_o (tabela w stopce zestawienia), styki mijankowo — w jednym przekroju ≤ 50 % prętów; odstęp w świetle prętów $\geq \max(\phi; d_g + 5$ mm; 20 mm) — PN-EN 1992-1-1 8.2(2), 8.7.2; pręty dolne w strefie podpory zakotwić $\geq 10\phi$ za licem (9.3.1.2(1) → 9.2.1.5).
6. Betonowanie: beton wg PN-EN 206+A2 I PN-B-06265 (klasa, ekspozycja, D_{max} 16 mm, konsystencja S3); pielęgnacja ≥ 7 dni (klasa pielęgnacji 2 — PN-EN 13670 p. 8.5); przerwy robocze wyłącznie w miejscach uzgodnionych z projektantem.
7. Rozszalowanie i usunięcie podpór: płyty i belki po uzyskaniu ≥ 70 % f_{ck} (PN-EN 13670 p. 5.6 i 8.5), wsporniki — nie wcześniej niż po 28 dniach i po wykonaniu elementów dociążających zaplecze; podpory wtórne do 28 dni.
8. Zbrojenie wynika z obliczeń statycznych (projekt/04_PT_konstrukcja/obliczenia, numeracja pozycji jak na rysunku); kontrola A_{s,prov} $\geq$ A_{s,req} — raport kontrola_zbrojenia.md. Pozycje z niespełnionymi warunkami nośności (wynik „NIE” w raporcie) wymagają zmian przed wydaniem do realizacji.
9. Warstwa dolna: siatka pól wg obliczeń MES (Wood–Armer, obwódnia ULS); pręty kierunku x (równoległe do osi x) — warstwa zewnętrzna, kierunek y — wewnętrzna; na podporach pośrednich przedłużenie $\geq 10\phi$ za oś podpory, na skrajnych — do krawędzi płyty.
10. Rysunek wygenerowany automatycznie z modelu model/budynek.yaml (wersja 1.0, 2026-09-25) — generatory lamela.views.

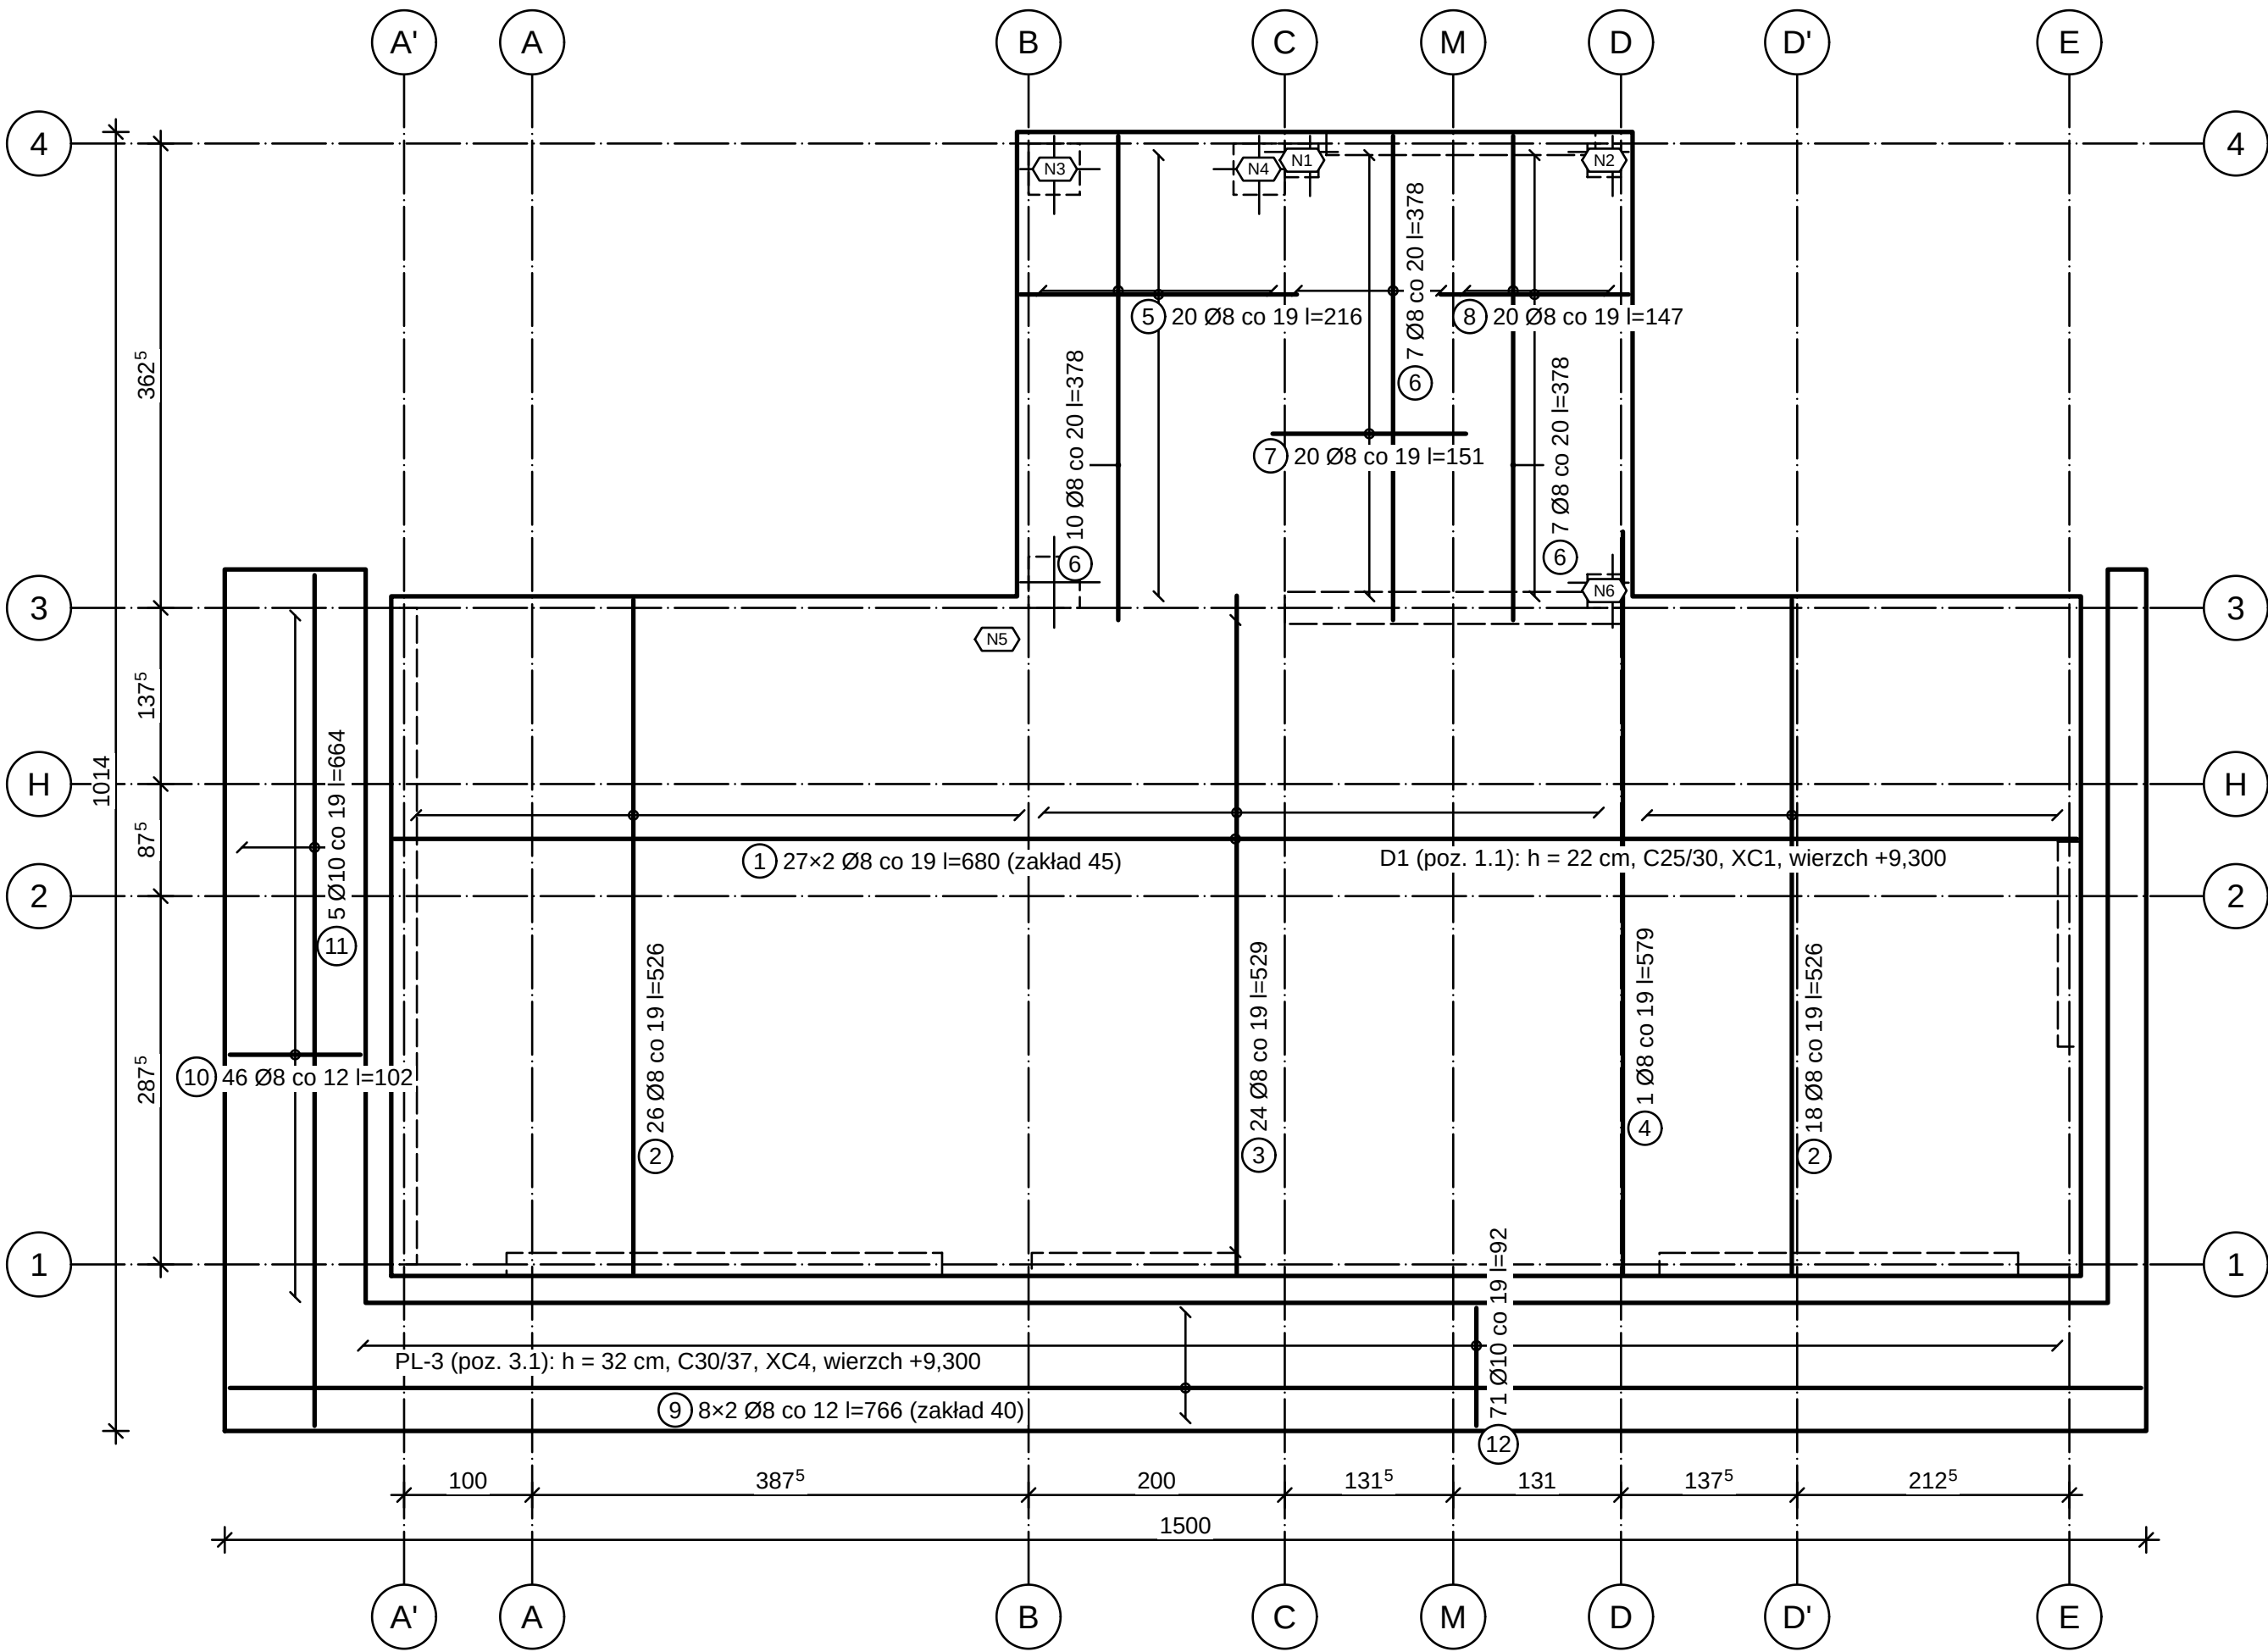

ZBROJENIE DOLNE PŁYT D1, PL-3 1:50

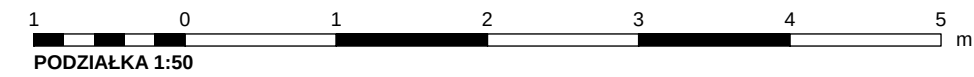

REW.	OPIS ZMIANY			DATA	
0	Wydanie — rysunek wygenerowany z modelu			2026-09-25	
PRACOWNIA PROJEKTOWA PRACOWNIA PROJEKTOWA — nazwa do uzupełnienia adres pracowni do uzupełnienia			STADIUM PT	BRANŻA KONSTRUKCJA (BO)	
INWESTOR (do uzupełnienia)					
OBIEKT / NAZWA ZAMIERZENIA BUDOWLANEGO Budynek mieszkalny jednorodzinny wolnostojący „Dom LAMELA”					
ADRES / LOKALIZACJA (NR DZIAŁKI, OBRĘB, JEDN. EWIDENCYJNA) ul. Lipowa (fikcyjna), dz. nr ewid. 123/4, obręb 0005 Przykładowo, gm. Przykładowo (fikcyjna)					KAT. OBIEKTU I
FUNKCJA		IMIĘ I NAZWISKO	SPECJALNOŚĆ, NR UPRAWNIEN	DATA	PODPIS
Projektant		[DO UZUPEŁNIENIA]	[DO UZUPEŁNIENIA]		
Projektant (wsp.)		[DO UZUPEŁNIENIA]	[DO UZUPEŁNIENIA]		
Sprawdzający		nie dotyczy (art. 20 ust. 3 pkt 2 PB)	—		
Opracował		[DO UZUPEŁNIENIA]	[DO UZUPEŁNIENIA]		
TYTUŁ RYSUNKU ZBROJENIE DOLNE STROPODACHU					
SKALA 1:50	FORMAT 400×594	DATA WYDANIA 2026-09-25	RODZAJ DOK. rysunek zbrojenia	NR RYSUNKU PT-BO-15	ARKUSZ 15/26
					REW. 0