

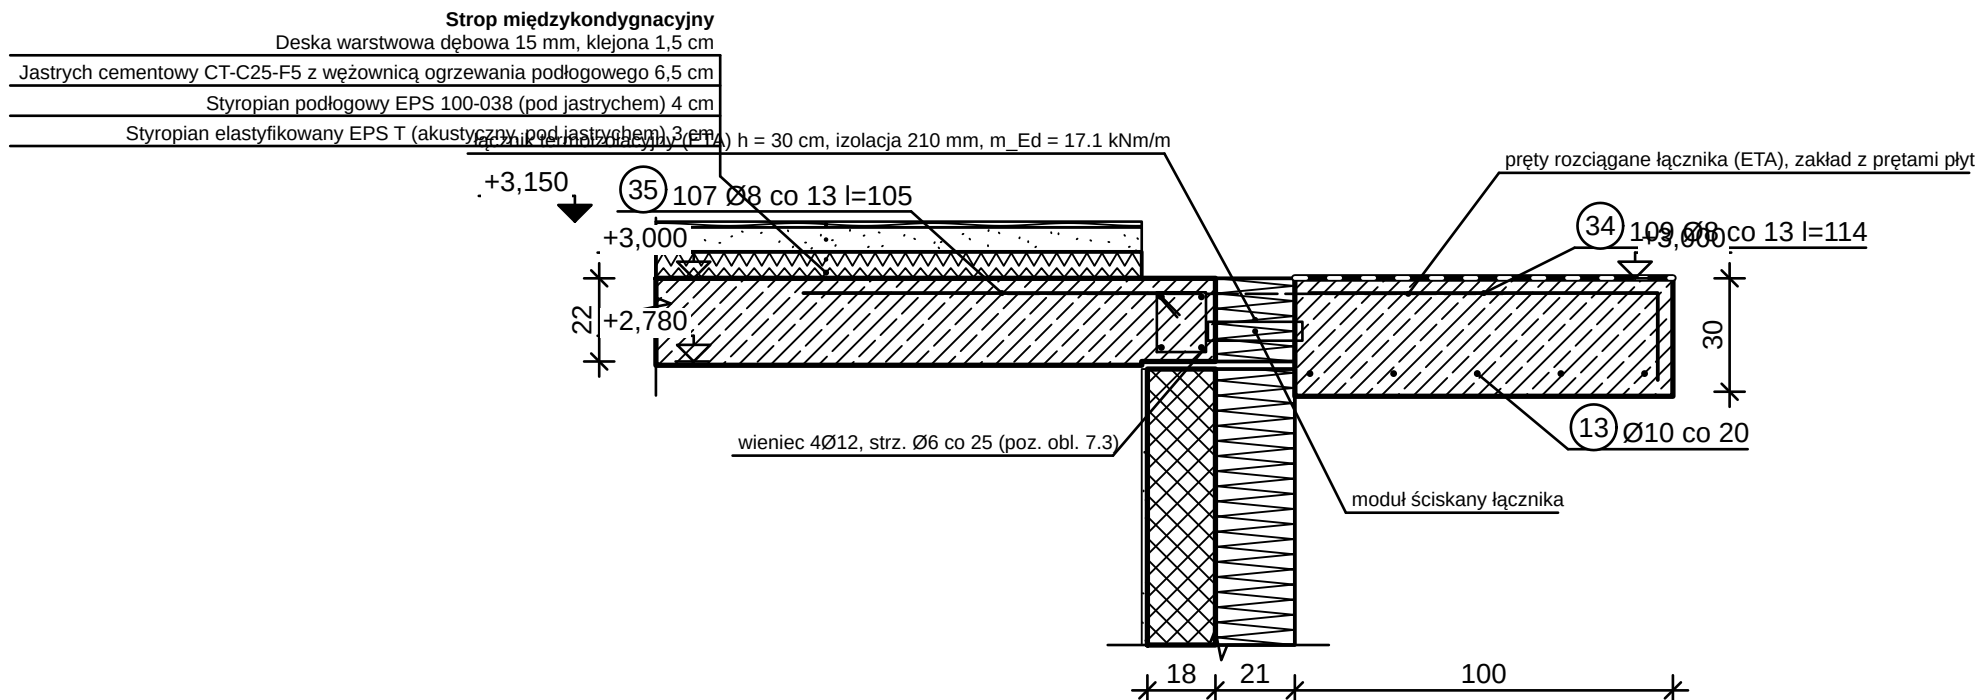


OBJAŚNIENIA I UWAGI


1. Wymiary w cm (mm w indeksie górnym, np. 24^s = 24,5 cm), rzędne w m względem ±0,000 = 101,650 m n.p.m. (PL-EVRF2007-NH).
2. Węzły strópów: warstwę wg przegród z modelu; zbrojenie — numery pozycji jak na arkuszach zbrojenia płyt poziomą (warstwa dolna/górna); wieniec wg pozycji obliczeniowej wieńców.
3. Otulina (c_{nom}) — wg klasy ekspozycji elementów (PN-EN 1992-1-1 tabl. 4.4N + NA, Δc_{dev} = 10 mm); podkładki dystansowe wg PN-EN 13670.
4. Stal B500SP (PN-H-93220), beton wg arkuszy zbrojenia; oznaczenia prętów wg PN-EN ISO 3766.
5. Rysunek wygenerowany automatycznie z modelu model/budynek.yaml (wersja 1.0, 2026-09-25) — generatory lamela.views.

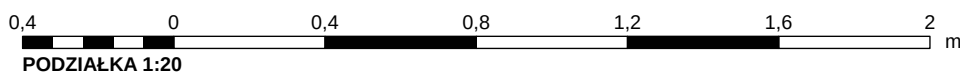

WĘZEŁ WSPORNIKA PL-E — ŁĄCZNIK TERMOIZOLACYJNY 1:20

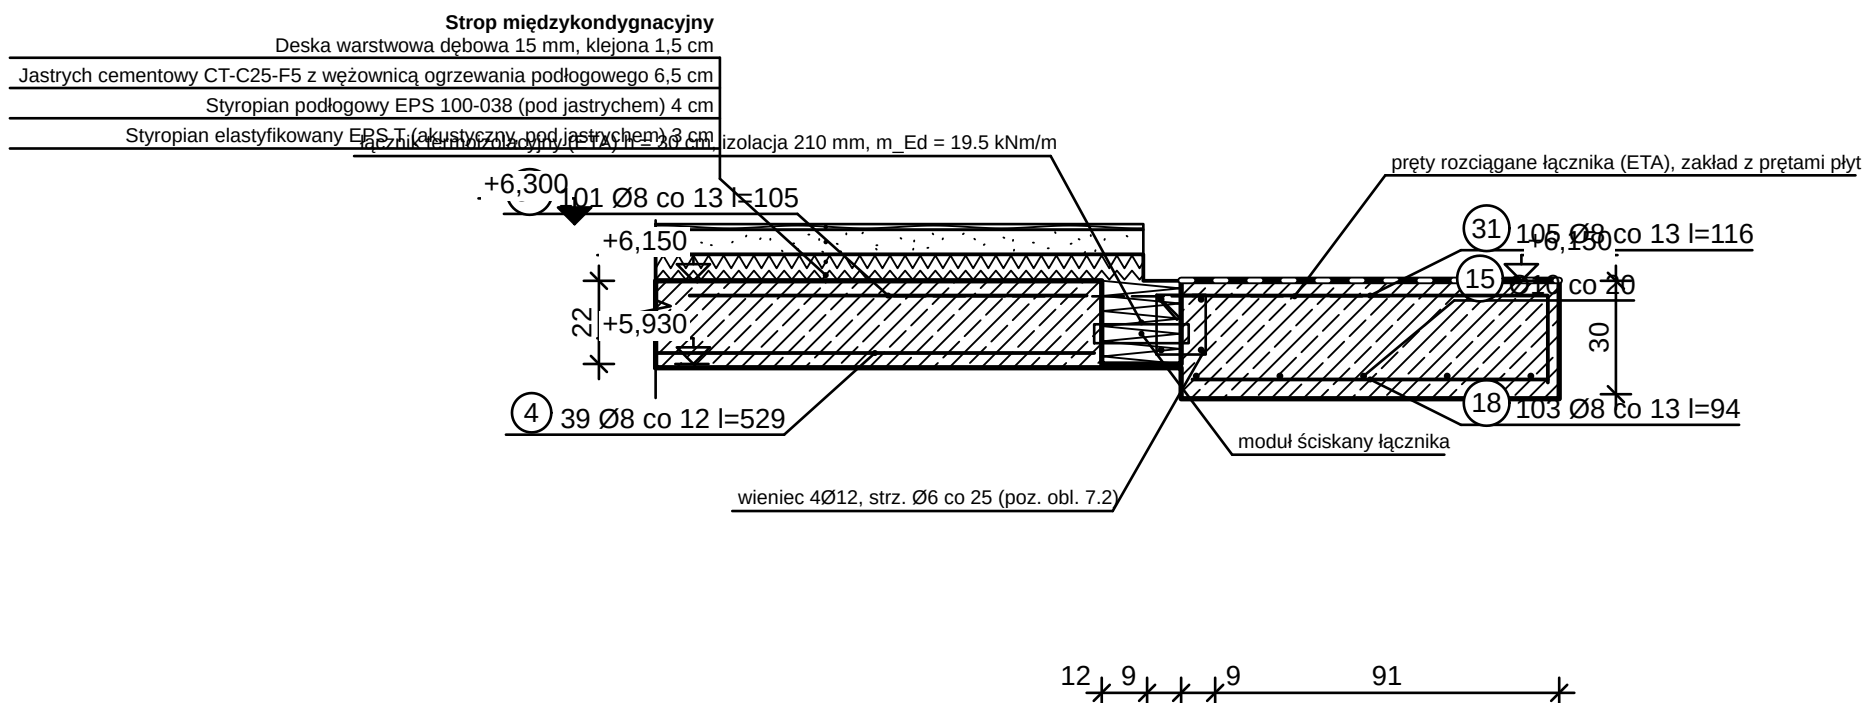

WĘZEŁ WSPORNIKA PL-2 — ŁĄCZNIK TERMOIZOLACYJNY 1:20

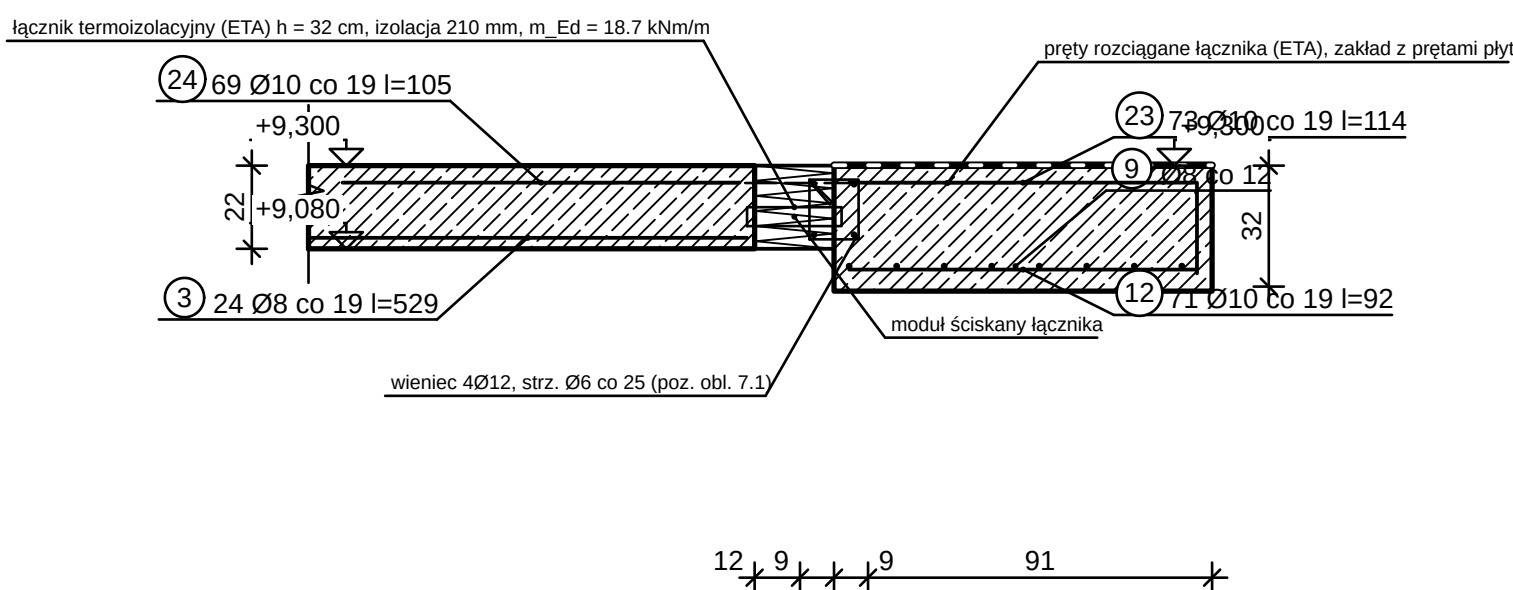

WEZEŁ WSPORNIKA PL-3 — ŁĄCZNIK TERMOIZOLACYJNY 1:20

OPIS ZMIANY		DATA				
0	Wydanie — rysunek wygenerowany z modelu		2026-09-25			
PRACOWNIA PROJEKTOWA PRACOWNIA PROJEKTOWA — nazwa do uzupełnienia adres pracowni do uzupełnienia		STADIUM PT	BRANŻA KONSTRUKCJA (BO)			
INWESTOR (do uzupełnienia)						
OBIEKT / NAZWA ZAMIERZENIA BUDOWLANEGO Budynek mieszkalny jednorodzinny wolnostojący „Dom LAMELA”						
ADRES / LOKALIZACJA (NR DZIAŁKI, OBRĘB, JEDN. EWIDENCYJNA) ul. Lipowa (fikcyjna), dz. nr ewid. 123/4, obręb 0005 Przykładowo, gm. Przykładowo (fikcyjna)			KAT. OBIEKTU I			
FUNKCJA	IMIĘ I NAZWISKO	SPECJALNOŚĆ, NR UPRAWNIEŃ	DATA	PODPIS		
Projektant	[DO UZUPEŁNIENIA]	[DO UZUPEŁNIENIA]				
Projektant (wsp.)	[DO UZUPEŁNIENIA]	[DO UZUPEŁNIENIA]				
Sprawdzający	nie dotyczy (art. 20 ust. 3 pkt 2 PB)	—				
Opracował	[DO UZUPEŁNIENIA]	[DO UZUPEŁNIENIA]				
TYTUŁ RYSUNKU WĘZŁ Y WSPORNIKÓW Z ŁĄCZNIKAMI TERMOIZOLACYJNYMI						
SKALA 1:20	FORMAT 310×594	DATA WYDANIA 2026-09-25	RODZAJ DOK. przekrój konstrukcyjny	NR RYSUNKU PT-BO-18	ARKUSZ 18/26	REW. 0