



OBJAŚNIENIA I UWAGI


- Wymiary w cm (mm w indeksie górnym, np. 24⁵ = 24,5 cm), rzędne w m względem ±0,000 = 101,650 m n.p.m. (PL-EVRF2007-NH).
- Przekroje fundamentu: warstwy wg przegrody podłogi na gruncie i ściany z modelu; izolacja obwodowa wg PN-EN ISO 13793; zbrojenie — numery pozycji jak na arkuszu zbrojenia fundamentu.
- Otuliny (c_nom) — wg klasy ekspozycji elementów (PN-EN 1992-1-1 tabl. 4.4N + NA, Δc_dev = 10 mm); podkładki dystansowe wg PN-EN 13670.
- Stal B500SP (PN-H-93220), beton wg arkuszy zbrojenia; oznaczenia prętów wg PN-EN ISO 3766.
- Rysunek wygenerowany automatycznie z modelu model/budynek.yaml (wersja 1.0, 2026-09-25) — generatory lamela.views.

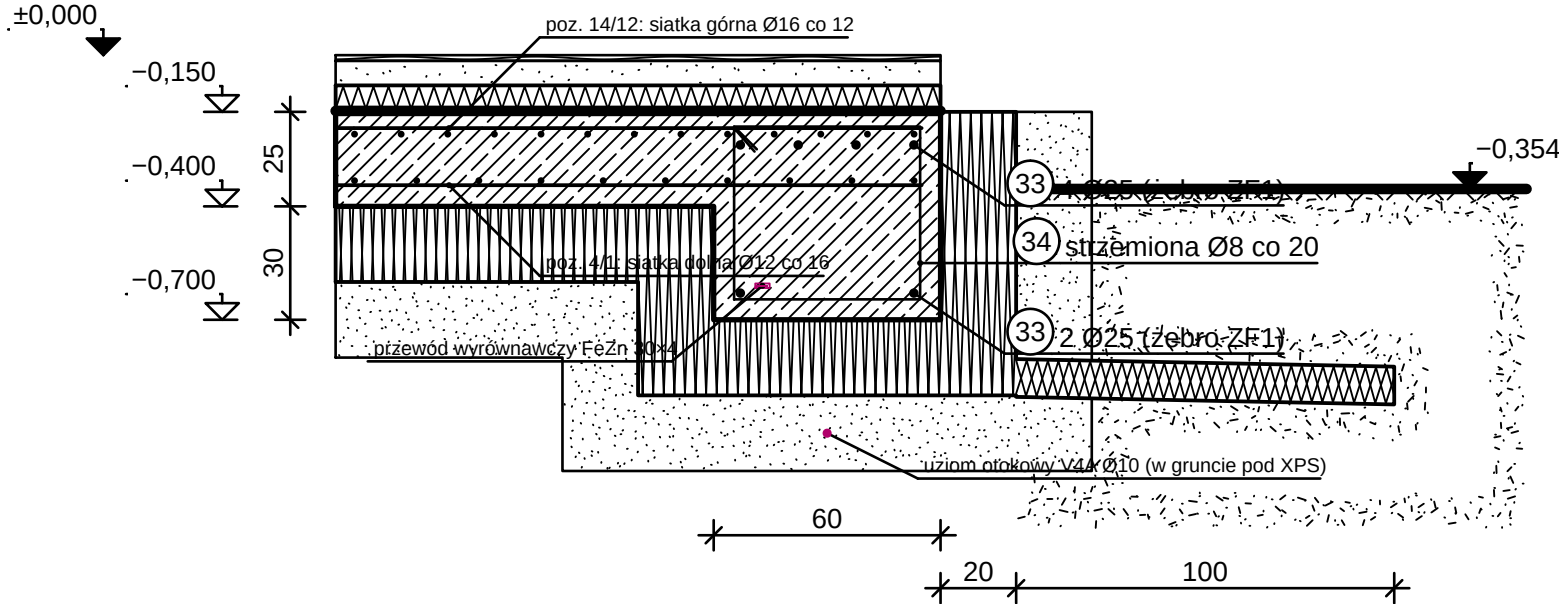

PRZEKRÓJ 1-1 — ŻEBRO ZF1 1:20

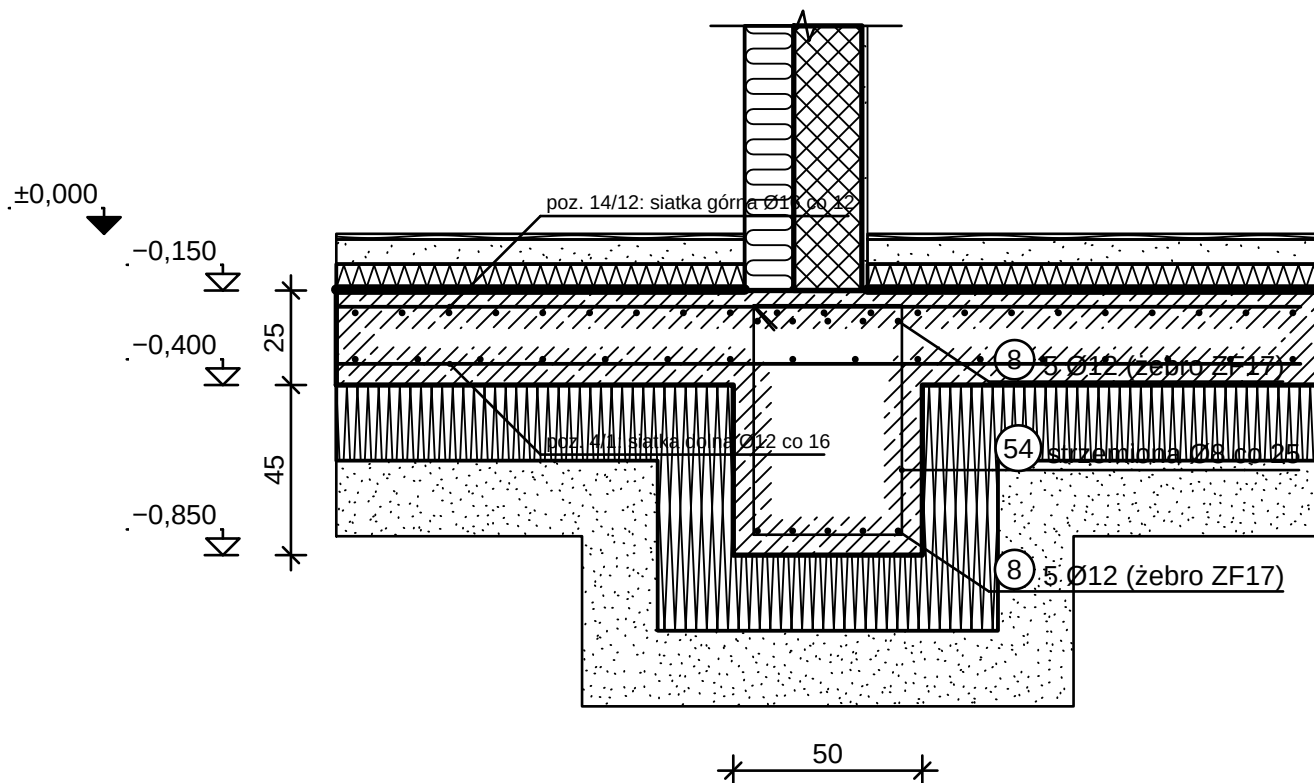

PRZEKRÓJ 2-2 — ŻEBRO ZF17 1:20

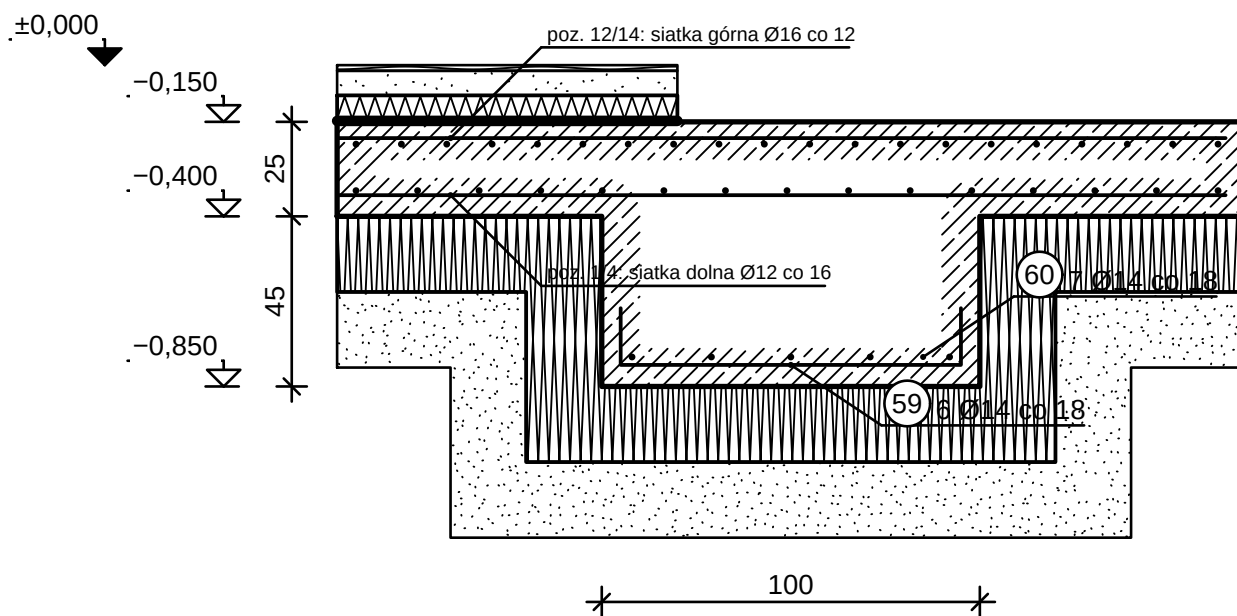

PRZEKRÓJ 3-3 — POGRUBIENIE SF1 1:20

REW.	OPIS ZMIANY			DATA
0	Wydanie — rysunek wygenerowany z modelu			2026-09-25
PRACOWNIA PROJEKTOWA PRACOWNIA PROJEKTOWA — nazwa do uzupełnienia adres pracowni do uzupełnienia			STADIUM PT	BRANŻA KONSTRUKCJA (BO)
INWESTOR (do uzupełnienia)				
OBIEKT / NAZWA ZAMIERZENIA BUDOWLANEGO Budynek mieszkalny jednorodzinny wolnostojący „Dom LAMELA”				
ADRES / LOKALIZACJA (NR DZIAŁKI, OBRĘB, JEDN. EWIDENCYJNA) ul. Lipowa (fikcyjna), dz. nr ewid. 123/4, obręb 0005 Przykładowo, gm. Przykładowo (fikcyjna)				KAT. OBIEKTU I
FUNKCJA	IMIĘ I NAZWISKO	SPECJALNOŚĆ, NR UPRAWNIEN	DATA	PODPIS
Projektant	[DO UZUPEŁNIENIA]	[DO UZUPEŁNIENIA]		
Projektant (wsp.)	[DO UZUPEŁNIENIA]	[DO UZUPEŁNIENIA]		
Sprawdzający	nie dotyczy (art. 20 ust. 3 pkt 2 PB)	—		
Opracował	[DO UZUPEŁNIENIA]	[DO UZUPEŁNIENIA]		
TYTUŁ RYSUNKU PRZEKROJE CHARAKTERYSTYCZNE FUNDAMENTU				
SKALA 1:20	FORMAT 260×594	DATA WYDANIA 2026-09-25	RODZAJ DOK. przekrój konstrukcyjny	NR RYSUNKU PT-BO-02
				ARKUSZ 2/27
				REW. 0