

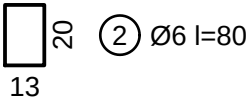
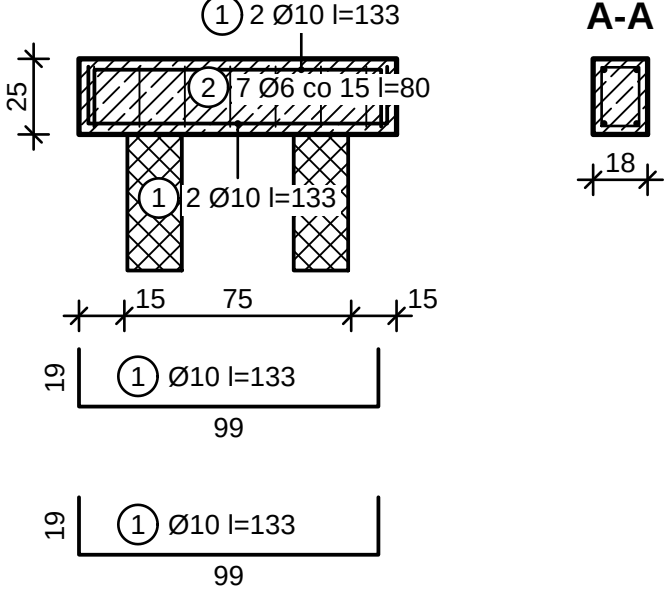




NA — 18×25 cm, L = 0,75 m, C25/30

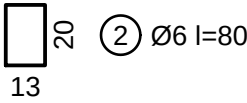



ND — 18×25 cm, L = 1,30 m, C25/30

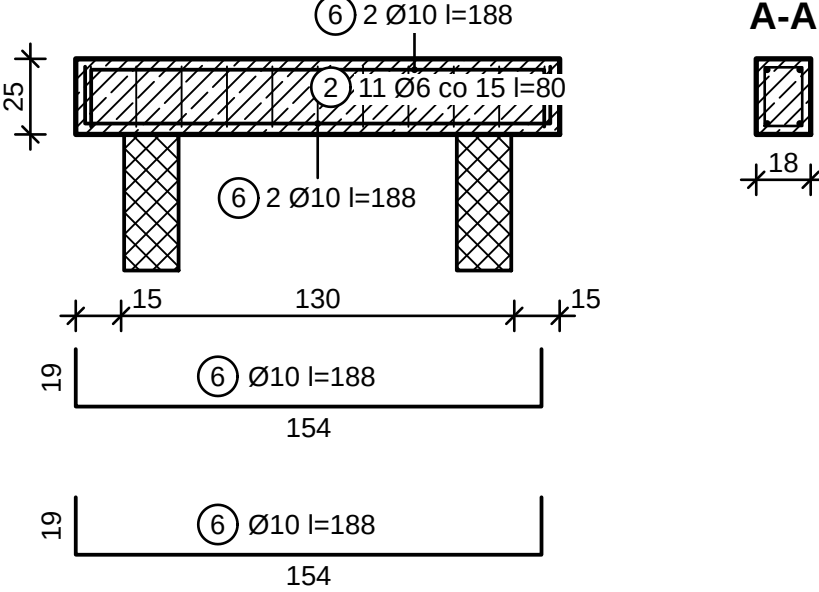

NC — 18×24 cm, L = 1,30 m, C25/30

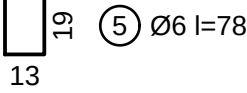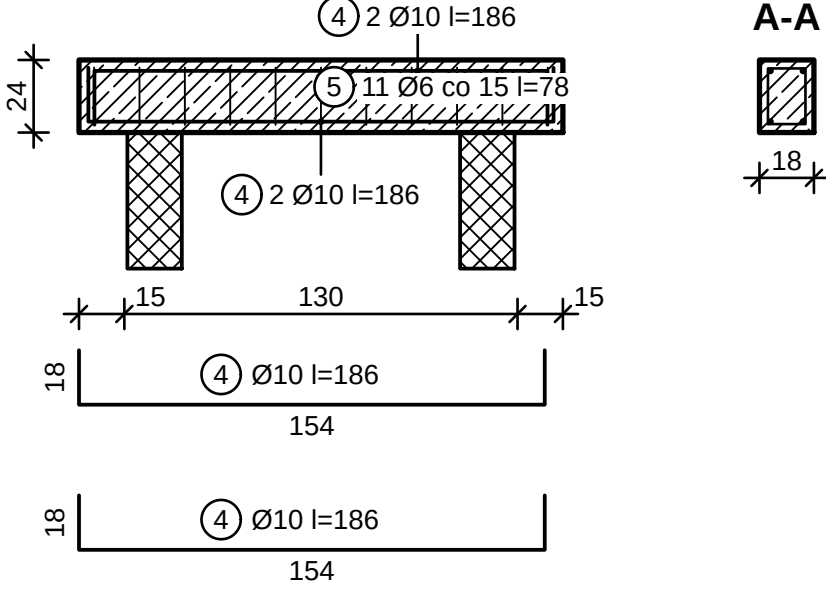

NB — 18×25 cm, L = 1,20 m, C25/30

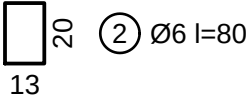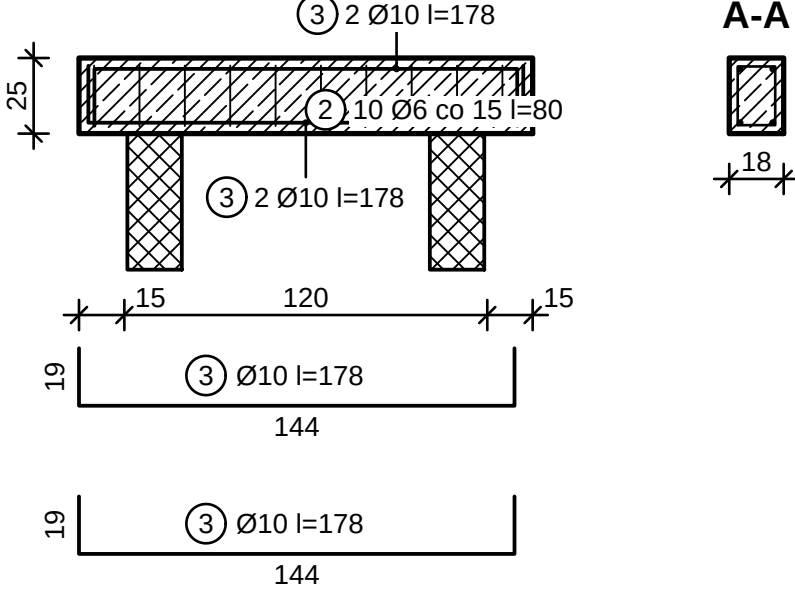

ZBROJENIE NADPROŻY NA, NB, NC, ND 1:25

TYPY NADPROŻY — OTWORY I POZYCJE OBLICZEŃ

Typ	Otwory	Poz. obl.	Szt.
NA	O0-10	6.4	1
NB	O0-13, O0-17	6.10, 6.7	2
NC	O0-06	6.1	1
ND	O0-14, O0-15, O0-22, O0-24, O1-03, O1-09, O1-10, O1-12, O2-06, O2-10	6.13, 6.14, 6.16, 6.20, 6.21, 6.23, 6.28, 6.30, 6.8, 6.9	10


ZESTAWIENIE STALI

Poz.	Ø [mm]	Kształt ISO 3766, wymiary [cm]	Dług. [cm]	Liczba [szt.]	Elem.	Ø6 [m]	Ø10 [m]
1	10	21: a=19 b=99 c=19	133	4	N-O0-1		5,32
2	6	51: a=13 b=20	80	150	N-O0-1	120,00	
3	10	21: a=19 b=144 c=19	178	8	N-O0-1		14,24
4	10	21: a=18 b=154 c=18	186	4	N-O0-0		7,44
5	6	51: a=13 b=19	78	11	N-O0-0	8,58	
6	10	21: a=19 b=154 c=19	188	40	N-O0-1		75,20
		Długość całkowita [m]				128,6	102,2
		Masa jednostkowa [kg/m]				0,222	0,617
		Masa [kg]				28,5	63,0
		RAZEM stal B500SP [kg]					91,5

O0-10, O0-13, O0-06, O0-14: beton C25/30, XC1, otulina strzemion c_nom = 25 mm (tabl. 4.4N + NA).

OBJAŚNIENIA I UWAGI

- Wymiary w cm (mm w indeksie górnym, np. 24⁵ = 24,5 cm), rzędne w m względem ±0,000 = 101,650 m n.p.m. (PL-EVRF2007-NH).
- Belki: pręty dolne i górne z odgięciami 90° w strefach podporowych (zakotwienie ≥ L_{bd} od lica podpory — PN-EN 1992-1-1 9.2.1.4), strzemiona zamknięte z hakami 135° (8.5, rys. 8.5), pierwsze strzemie 5 cm od lica podpory; rozstaw wg obliczeń (6.2.3), s ≤ min(0,75·d; 400 mm) (9.6N).
- Przekrój A-A — w środku rozpiętości; długości prętów l — długości rozwinięcia (wymiary zewnętrzne, odliczenie gięcia wg PN-EN ISO 3766).
- Betonowanie: beton wg PN-EN 206+A2 i PN-B-06265 (klasa, ekspozycja, D_{max} 16 mm, konsystencja S3); pielęgnacja ≥ 7 dni (klasa pielęgnacji 2 — PN-EN 13670 p. 8.5); przerwy robocze wyłącznie w miejscach uzgodnionych z projektantem.
- Rozszalowanie i usunięcie podpór: płyty i belki po uzyskaniu ≥ 70 % f_{ck} (PN-EN 13670 p. 5.6 i 8.5), wsporniki — nie wcześniej niż po 28 dniach i po wykonaniu elementów dociągających zaplecze; podpory wtórne do 28 dni.
- Nadproża pogrupowano w typy (jednakowy przekrój, długość i zbrojenie z obliczeń); liczby sztuk w zestawieniu — łącznie dla wszystkich nadproży typu.
- Rysunek wygenerowany automatycznie z modelu model/budynek.yaml (wersja 1.0, 2026-09-25) — generatory lamela.views.

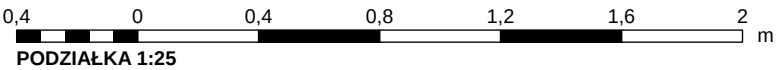

REW.	OPIS ZMIANY			DATA			
0	Wydanie — rysunek wygenerowany z modelu			2026-09-25			
PRACOWNIA PROJEKTOWA PRACOWNIA PROJEKTOWA — nazwa do uzupełnienia adres pracowni do uzupełnienia			STADIUM PT	BRANŻA KONSTRUKCJA (BO)			
INWESTOR (do uzupełnienia)							
OBIEKT / NAZWA ZAMIERZENIA BUDOWLANEGO Budynek mieszkalny jednorodzinny wolnostojący „Dom LAMELA”							
ADRES / LOKALIZACJA (NR DZIAŁKI, OBREB, JEDN. EWIDENCYJNA) ul. Lipowa (fikcyjna), dz. nr ewid. 123/4, obręb 0005 Przykładowo, gm. Przykładowo (fikcyjna)				KAT. OBIEKTU I			
FUNKCJA	IMIĘ I NAZWISKO		SPECJALNOŚĆ, NR UPRAWNIEN		DATA	PODPIS	
Projektant	[DO UZUPEŁNIENIA]		[DO UZUPEŁNIENIA]				
Projektant (wsp.)	[DO UZUPEŁNIENIA]		[DO UZUPEŁNIENIA]				
Sprawdzający	nie dotyczy (art. 20 ust. 3 pkt 2 PB)		—				
Opracował	[DO UZUPEŁNIENIA]		[DO UZUPEŁNIENIA]				
TYTUŁ RYSUNKU ZBROJENIE NADPROŻY (1)							
SKALA 1:25	FORMAT 410×420	DATA WYDANIA 2026-09-25	RODZAJ DOK. rysunek zbrojenia	NR RYSUNKU PT-BO-23		ARKUSZ 23/27	REW. 0