


ODWODNIENIE DACHÓW — RZUT DACHU 1:50

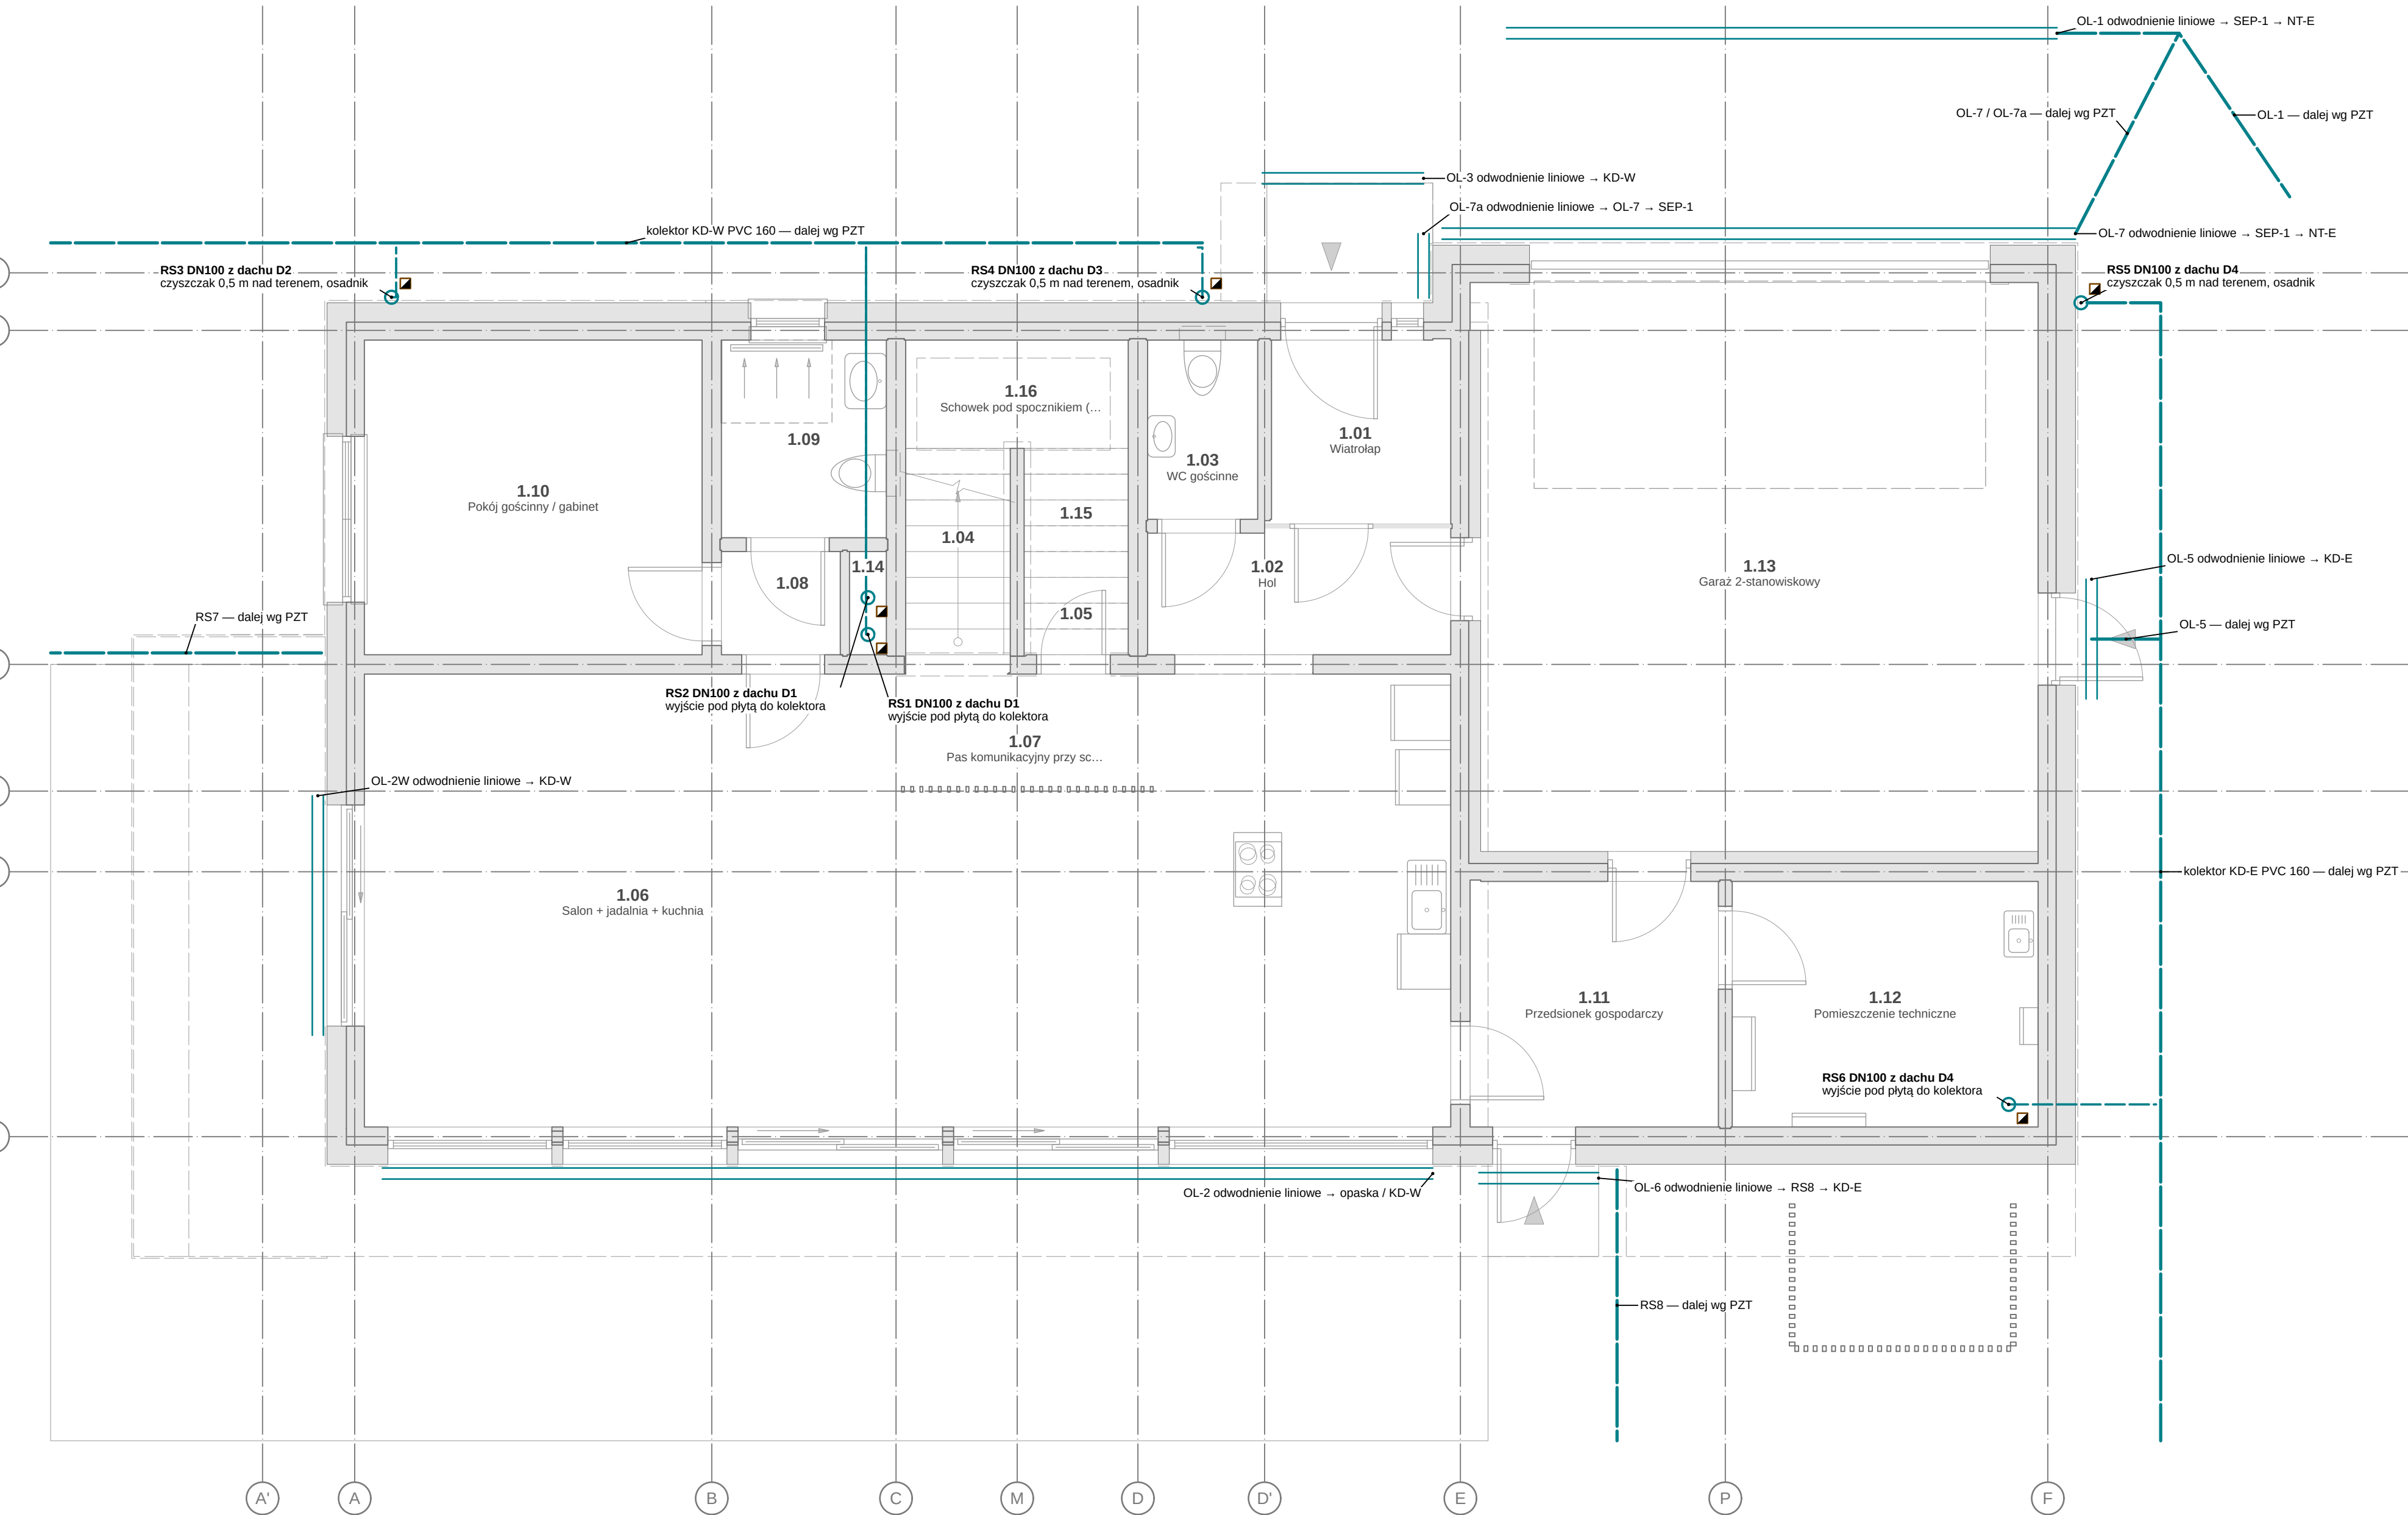

ODWODNIENIE DACHÓW — RZUT PARTERU (RURY SPUSTOWE) 1:50

OBJAŚNIENIA I UWAGI

- Srednice przewodów w mm (d, z+s — rury wielowarstwowe, Ø/DN — kanalizacja, kanały wentylacyjne), przekroje żył w mm², odległości i rzędne w m; ±0,000 = 101,650 m n.p.m. (PL-EVRF2007-NH).
- Rysunki instalacji na podkładzie rzutów architektury (PB-AR); podkład — linie cienkie szare (warstwy I-PODKŁAD¹).
- Odwodnienie dachów wg PN-EN 12056-3 i WT 5.28, § 29; natężenie deszczu wg modelu PANDA (IMCN) — lamela obliczenia sanitarne, deszczowa; wody opadowe zagospodarowane na działce (zbiornik retencyjny + niecka chłonna), bez odprowadzania do kanalizacji sanitarnej.
- Wpusty dachowe z grzałką (podgrzewane), z kolierzem do membrany/lapy i koszem liściowym; przelewy awaryjne w atykach — dno przelewu powyżej poziomu pokrycia przy wypuscie (odpływ normalny przez wpusty).
- Rury spustowe wewnętrzne w izolacji termicznej i akustycznej (otulina ≥ 20 mm); przejścia przez stropy z uszczelnieniem ppot. wg klasy stropu.
- Dachy: A = 249,0 m², Q = 12,51 l/s; zbiornik 5,0 m³, niecka 19,5 m².
- Rysunek wygenerowany automatycznie z modelu model/budnek.yamł (wersja 1.0, 2026-09-25) — generatory lamela.views.

OZNACZENIA — LEGENDA SYMBOLI

Oznaczenia instalacji sanitarnych — praktyka branżowa (PN-B-01411, PN-B-01410, PN-B-01430 — normy wycofane, bez następcy), amatura i urzędzenia wg PN-EN ISO 10682-2 / PN-EN ISO 14617; rodzaje powierza wg PN-EN 10798-3 (ODA, SUP, ETA, EWA). Obowiązuje legenda na arkuszu.

- podkład architektoniczny (rzut AR — ściany przecięte, stolarka, wyposażenie) — linie cienkie szare
- Kd — kanalizacja deszczowa: rury spustowe, podejścia od wpustów (PVC-U/PSP; DN wg obliczeń); linia kreskowa długa
- przelew awaryjny w atyce (PN-EN 12056-3 p. 7) — kierunek wypływu
- rysunek (pion deszczowy)
- wpuszczak rury spustowej / rewizja
- przewody deszczowe pod płytą i w gruncie (PVC-U SN8) — linia kreskowa
- odwodnienie liniowe (korytko z rusztem) wg działka.yamł

WYNIKI OBLICZEŃ — ODWODNIENIE DACHÓW (PN-EN 12056-3)

Pole	Typ	A [m²]	Q [l/s]	wpustów	Q wp [l/s]	Q przeł. [l/s]	h, spiętr. [cm]
D1	plaski	87,4	4,02	2	9,00	22,41	5,0
D2	plaski	12,5	0,58	1	4,50	11,21	2,2
D3	plaski	11,2	0,52	1	4,50	11,21	2,0
D4	zielony	59,1	3,78	2	9,00	22,41	4,8
PL-E	taras	23,7	1,09	2	3,40	8,91	2,0
PL-DA	taras	3,0	0,14	1	1,70	5,94	0,6
PL-2	taras	23,0	1,06	2	3,40	11,89	1,6
PL-3	taras	23,0	1,06	2	3,40	11,89	1,6
PL-D	wspornik	6,1	0,28	1	1,70	5,94	1,0

100 mm (wydruk 1:1)

1 0 1 2 3 4 5 m

PODZIAŁKA 1:50

REW. 0

OPIS ZMIANY

DATA

2026-09-25

PRACOWNIA PROJEKTOWA

PRACOWNIA PROJEKTOWA — nazwa do uzupełnienia

STADIUM

PT

BRANŻA

INSTALACJE SANITARNE (IS)

INWESTOR (do uzupełnienia)

OBIEKT / NAZWA ZAMIERZENIA BUDOWLANEGO

Budynek mieszkalny jednorodzinny wolnostojący „Dom LAMELA”

ADRES / LOKALIZACJA (NR DZIAŁKI, OBRĘB, JEDN. EWIDENCYJNA)

ul. Lipowa (fikcyjna), dz. nr ewid. 123/4, obręb 0005 Przykładowo, gm. Przykładowo (fikcyjna)

KAT. OBIEKTU

I

FUNKCJA

IMIĘ I NAZWISKO

SPECJALNOŚĆ, NR UPRAWNIEN

DATA

PODPIS

Projektant

[DO UZUPEŁNIENIA]

[DO UZUPEŁNIENIA]

Projektant (wsp.)

[DO UZUPEŁNIENIA]

[DO UZUPEŁNIENIA]

Sprawdzający

nie dotyczy (art. 20 ust. 3 pkt 2 PB)

—

Opracował

[DO UZUPEŁNIENIA]

[DO UZUPEŁNIENIA]

TYTUŁ RYSUNKU

ODWODNIENIE DACHÓW — RZUT DACHU I RZUT PARTERU

SKALA

1:50

FORMAT

590×841

DATA WYDANIA

2026-09-25

RODZAJ DOK.

rzut instalacji

NR RYSUNKU

PT-IS-05

ARKUSZ

5/11

REW.

0

