

A

B


C

D


E

F

odcinek kontroly 100 mm (wydruk 1:1)

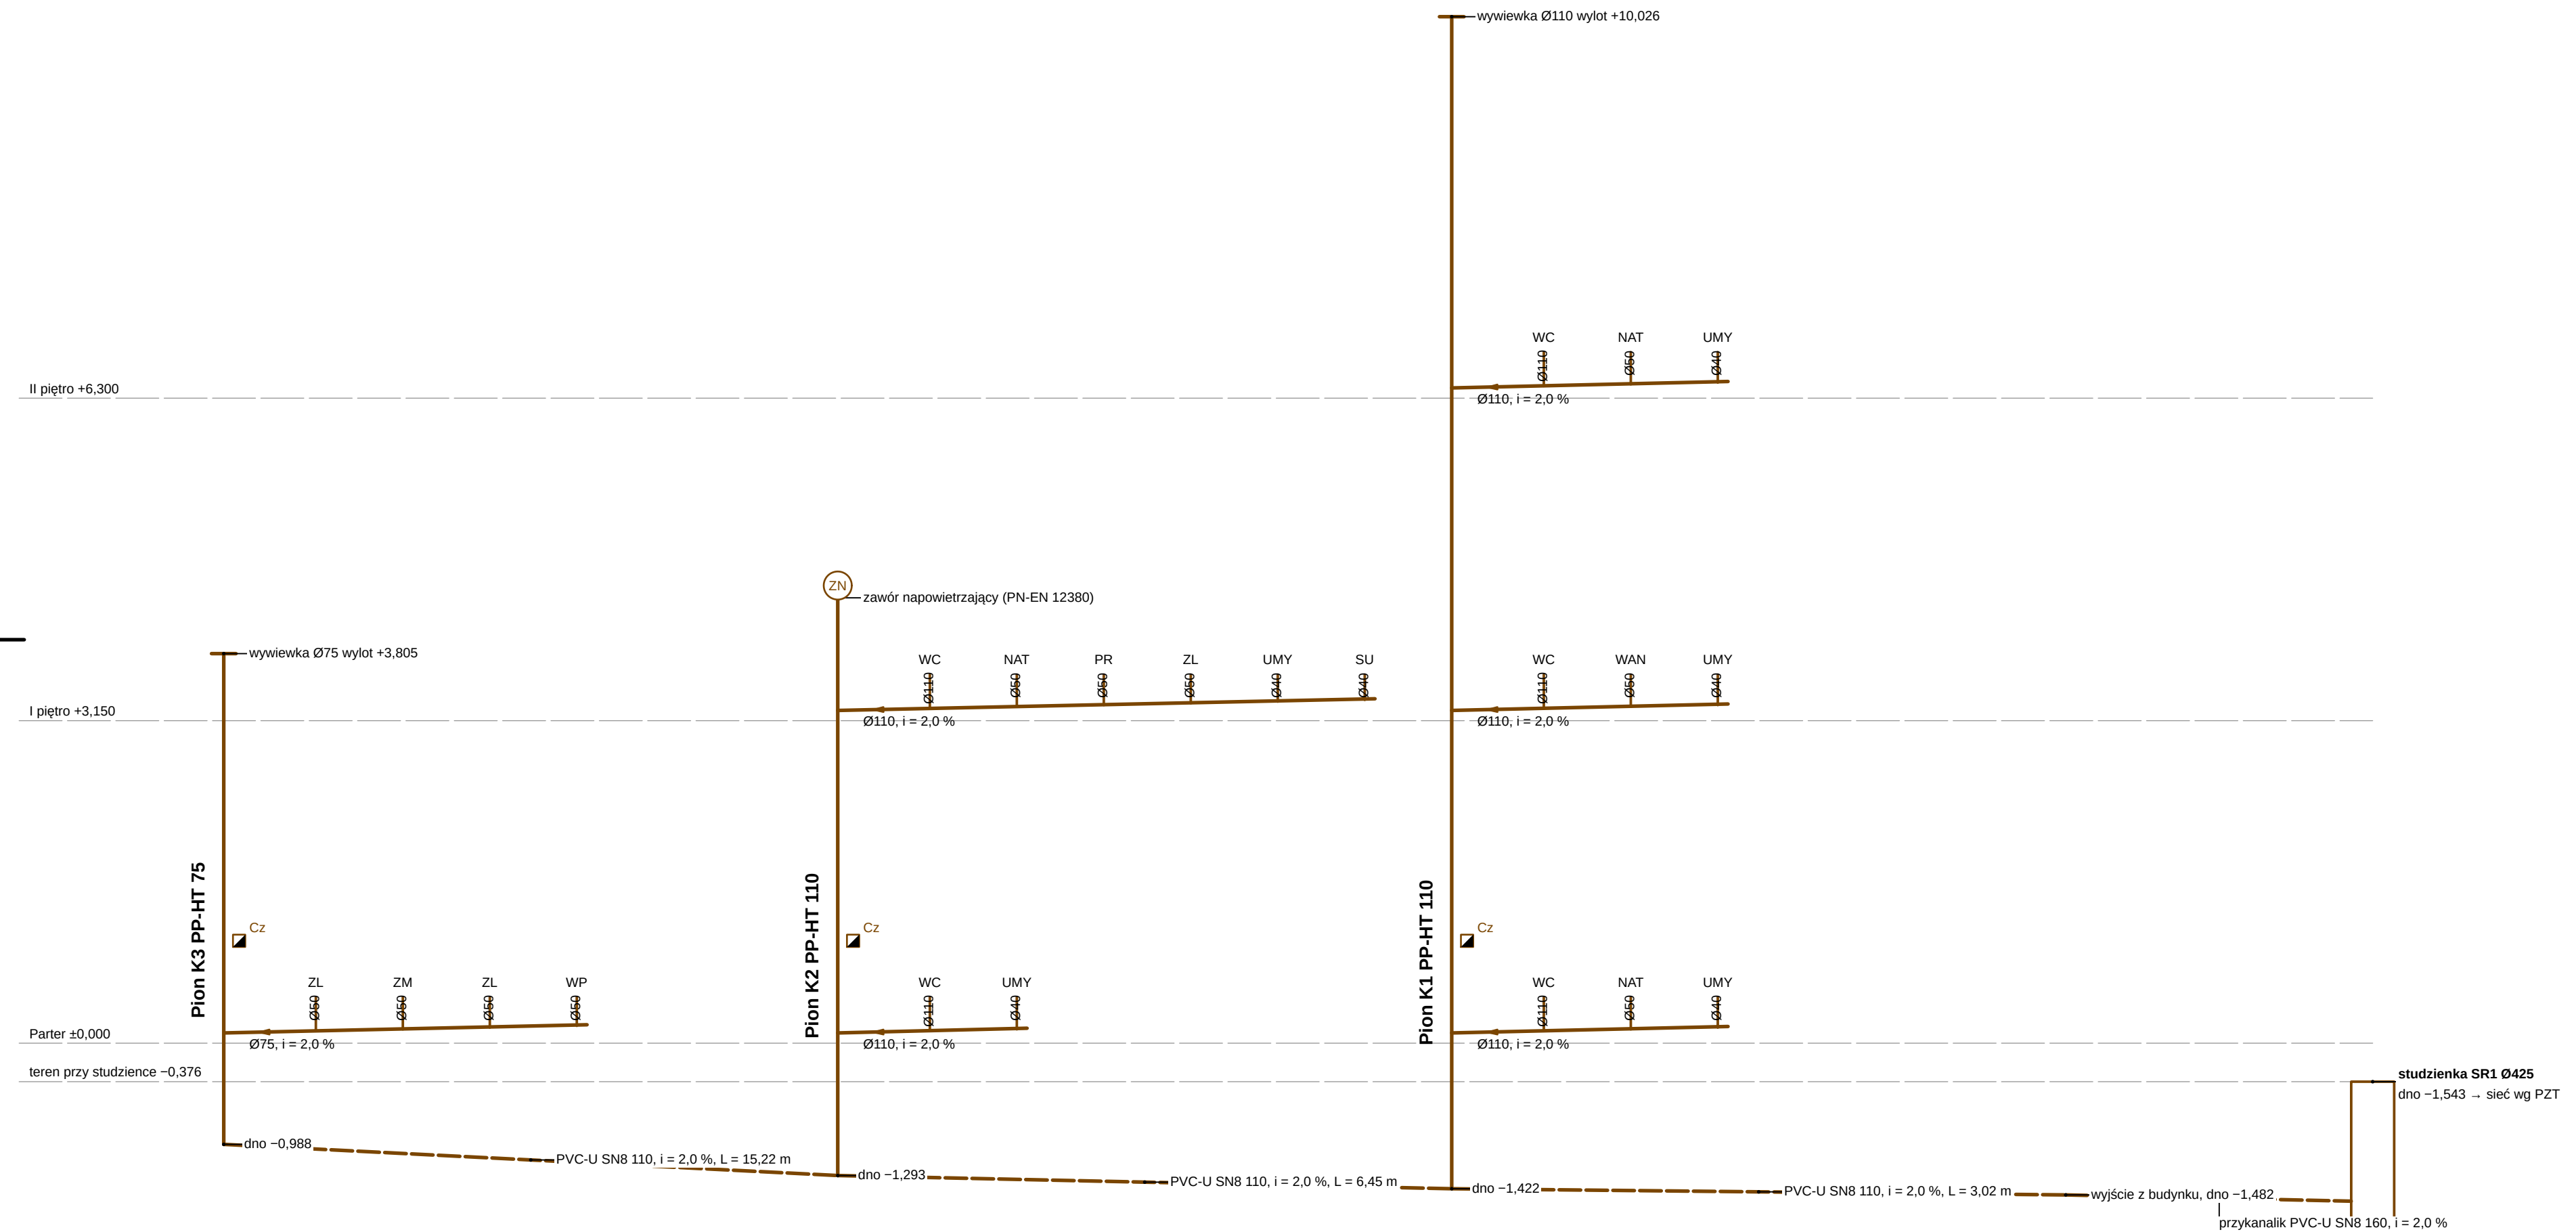

ROZWINIĘCIE KANALIZACJI SANITARNEJ (PIONY)

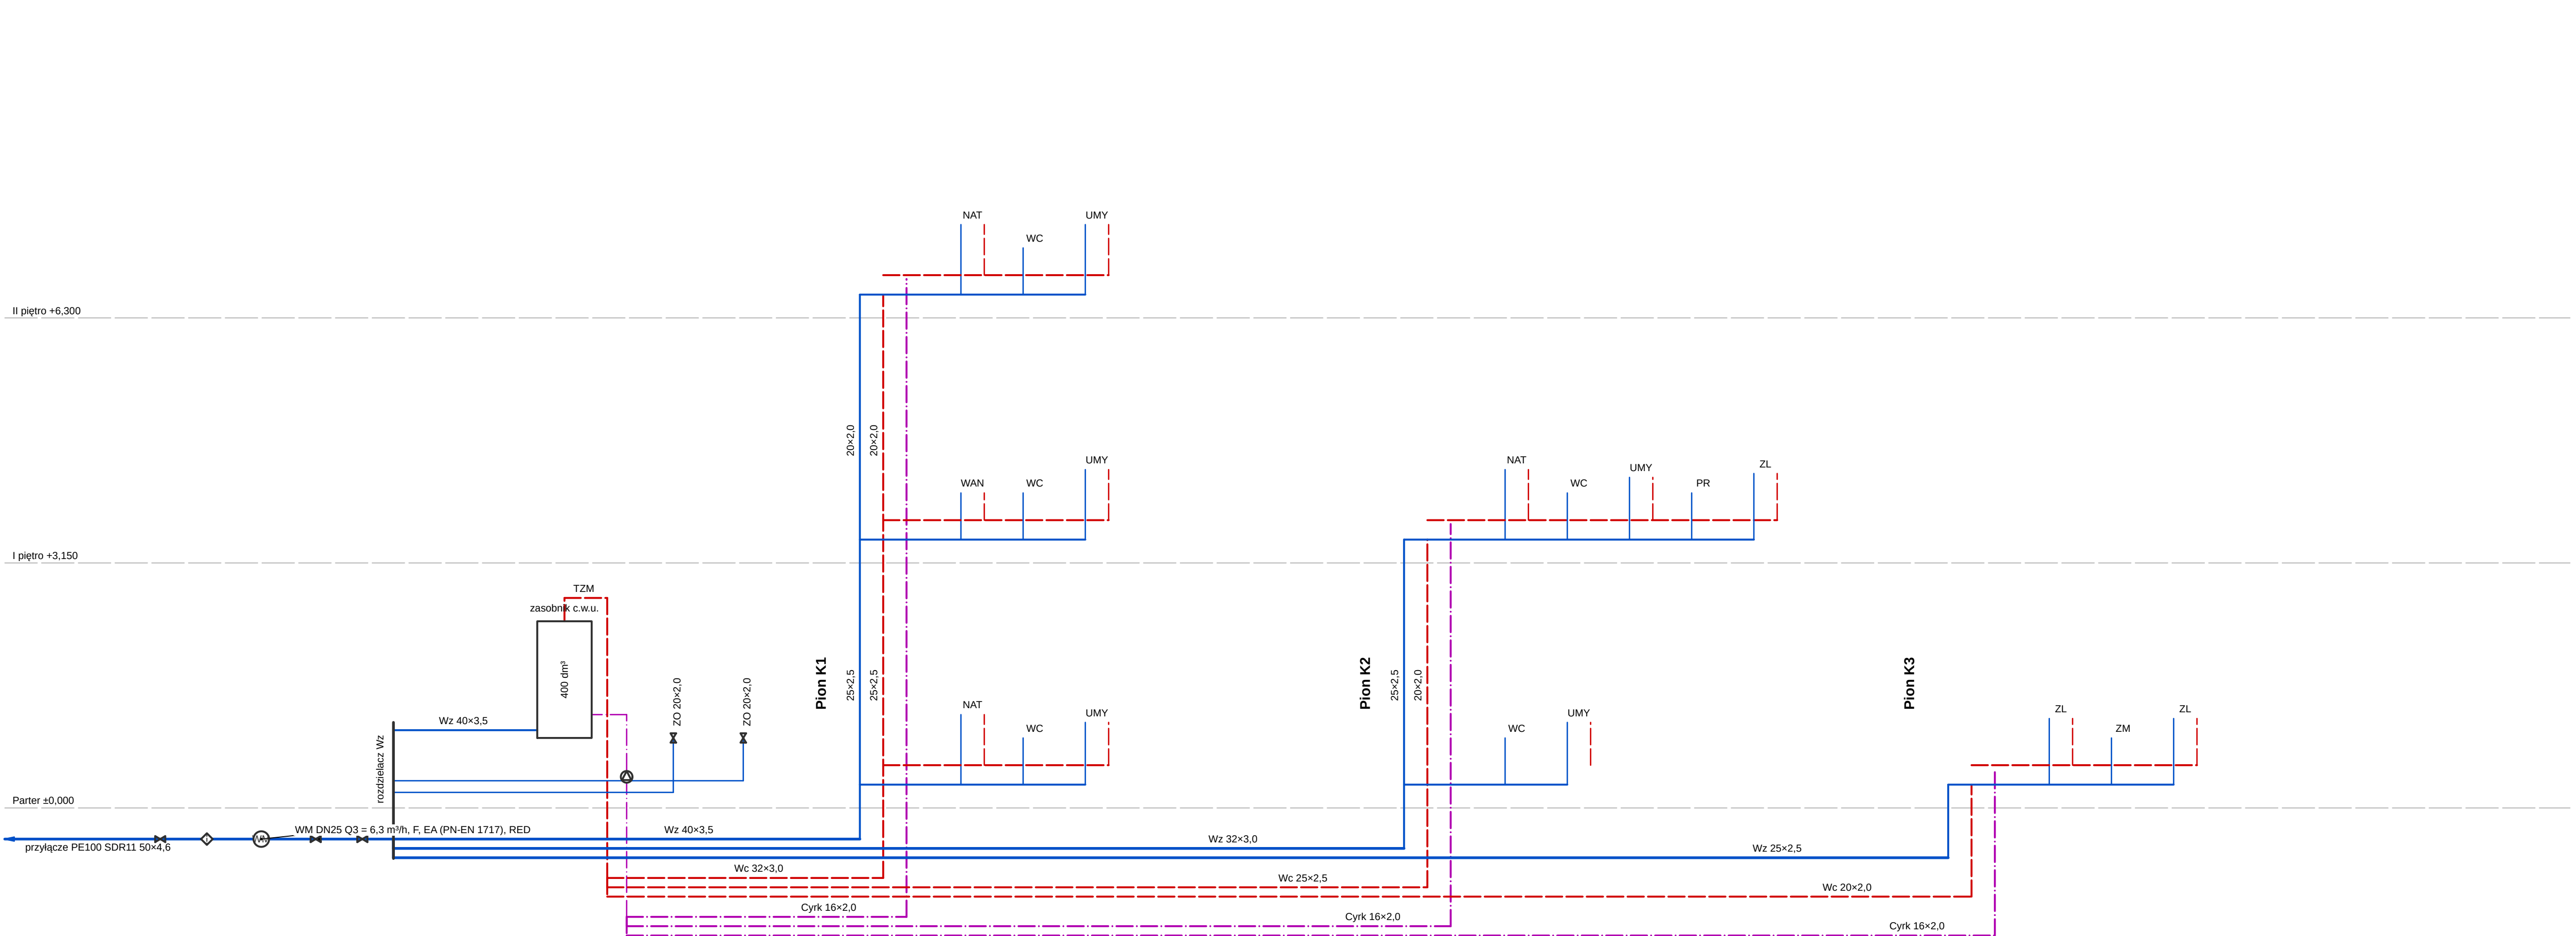

ROZWINIĘCIE INSTALACJI WODOCIĄGOWEJ

OZNACZENIA — LEGENDA SYMBOLI

- Ks — pion / podejście PP-HT (PN-EN 1451-1)
- przewód pod płytą / przykanalik PVC-U SN8 (PN-EN 1401-1)
- czyszczak na pionie (1,0 m nad posadzką)
- zawór napowietrzający pionu
- Wz — woda zimna
- Wc — ciepła woda użytkowa
- Cyrk — cyrkulacja c.w.u.
- wodomierz; F — filtr; EA — zawór antyskażeniowy (zwrtny); zawory odcinające
- Wz — woda zimna

PIONY I PRZEWODY ODPŁYWOWE (obliczenia PN-EN 12056-2)

Odcinek	Rodzaj	DN	ZDU	Q [l/s]	L [m]
PION_K1	pion	Ø110	9,5	2,00	7,90
PION_K2	pion	Ø110	7,9	2,00	4,75
PION_K3	pion	Ø75	3,2	0,89	1,60
KOL1	poziom	Ø110	3,2	0,89	15,22
KOL2	poziom	Ø110	11,1	2,00	6,45
KOL3	poziom	Ø110	20,6	2,27	3,02
PRZ	przykanalik	Ø160	20,6	2,27	3,05

OBJAŚNIENIA I UWAGI

- Schemat bez skali: rzędne w m względem ±0,000 (posadzka parteru), średnice w mm.
- Rysunki instalacji na podkładzie rzutów architektury (PB-AR); podkład — linie cienkie szare (warstwy i-PODKŁAD).
- Rozwinięcie kanalizacji: os pionowa w skali rzędnych (1:50), os pozioma umowna. Podejścia pokazano schematycznie (kolejność przyborów wg średnic), rzędne dna przewodów pod płytą z obliczeń (lamela.obliczenia.sanitarne.kanalizacja).
- Wentylacja pionów: K1 — wywiewka ponad dach; K2 — zawór napowietrzający PN-EN 12380 (dozwolony); K3 — wywiewka ponad dach.
- Rozwinięcie instalacji wodociągowej: os pionowa w skali rzędnych, os pozioma umowna; wysokości wypływów wg PN-92/B-01:706 (praktyka projektowa). Średnice z obliczeń (lamela.obliczenia.sanitarne.woda); punkt krytyczny PRY18 (c.w.u.), p. wym = 325 kPa.
- Oznaczenia przyborów: WC — miska ustępowa, UMY — umywalka, NAT — natrysk, WAN — wanna, ZL — zlewomywak, ZLG — zlew gospodarczy, ZM — zmywarka, PR — pralka, ZO — zawór ogrodowy.
- Rysunek wygenerowany automatycznie z modelu modelibudynk.yamli (wersja 1.0, 2026-09-25) — generatory lamela.views.

REW.	OPIS ZMIANY	DATA
0	Wydanie — rysunek wygenerowany z modelu	2026-09-25
PRACOWNIA PROJEKTOWA — nazwa do uzupełnienia		STADIUM
adres pracowni do uzupełnienia		BRANŻA
INWESTOR		INSTALACJE
(do uzupełnienia)		SANITARNE (IS)
OBIEKT / NAZWA ZAMIERZENIA BUDOWLANEGO		
Budynek mieszkalny jednorodzinny wolnostojący „Dom LAMELA”		
ADRES / LOKALIZACJA (NR DZIAŁKI, OBRĘB, JEDN. EWIDENCYJNA)		KAT. OBIEKTU
ul. Lipowa (fikcyjna), dz. nr ewid. 123/4, obręb 0005 Przykładowo, gm. Przykładowo (fikcyjna)		I
FUNKCJA	IMIĘ I NAZWISKO	SPECJALNOŚĆ, NR UPRAWNIEŃ
Projektant	[DO UZUPEŁNIENIA]	[DO UZUPEŁNIENIA]
Projektant (wsp.)	[DO UZUPEŁNIENIA]	[DO UZUPEŁNIENIA]
Sprawdzający	nie dotyczy (art. 20 ust. 3 pkt 2 PB)	—
Opracował	[DO UZUPEŁNIENIA]	[DO UZUPEŁNIENIA]
TYTUŁ RYSUNKU		
KANALIZACJA I WODOCIĄG — ROZWINIĘCIA		
SKALA	FORMAT	DATA WYDANIA
—	1410×297	2026-09-25
RODZAJ DOK.	NR RYSUNKU	ARKUSZ
schemat instalacji	PT-IS-10	10/11
REW.	0	