


PRZEKRÓJ B-B 1:50

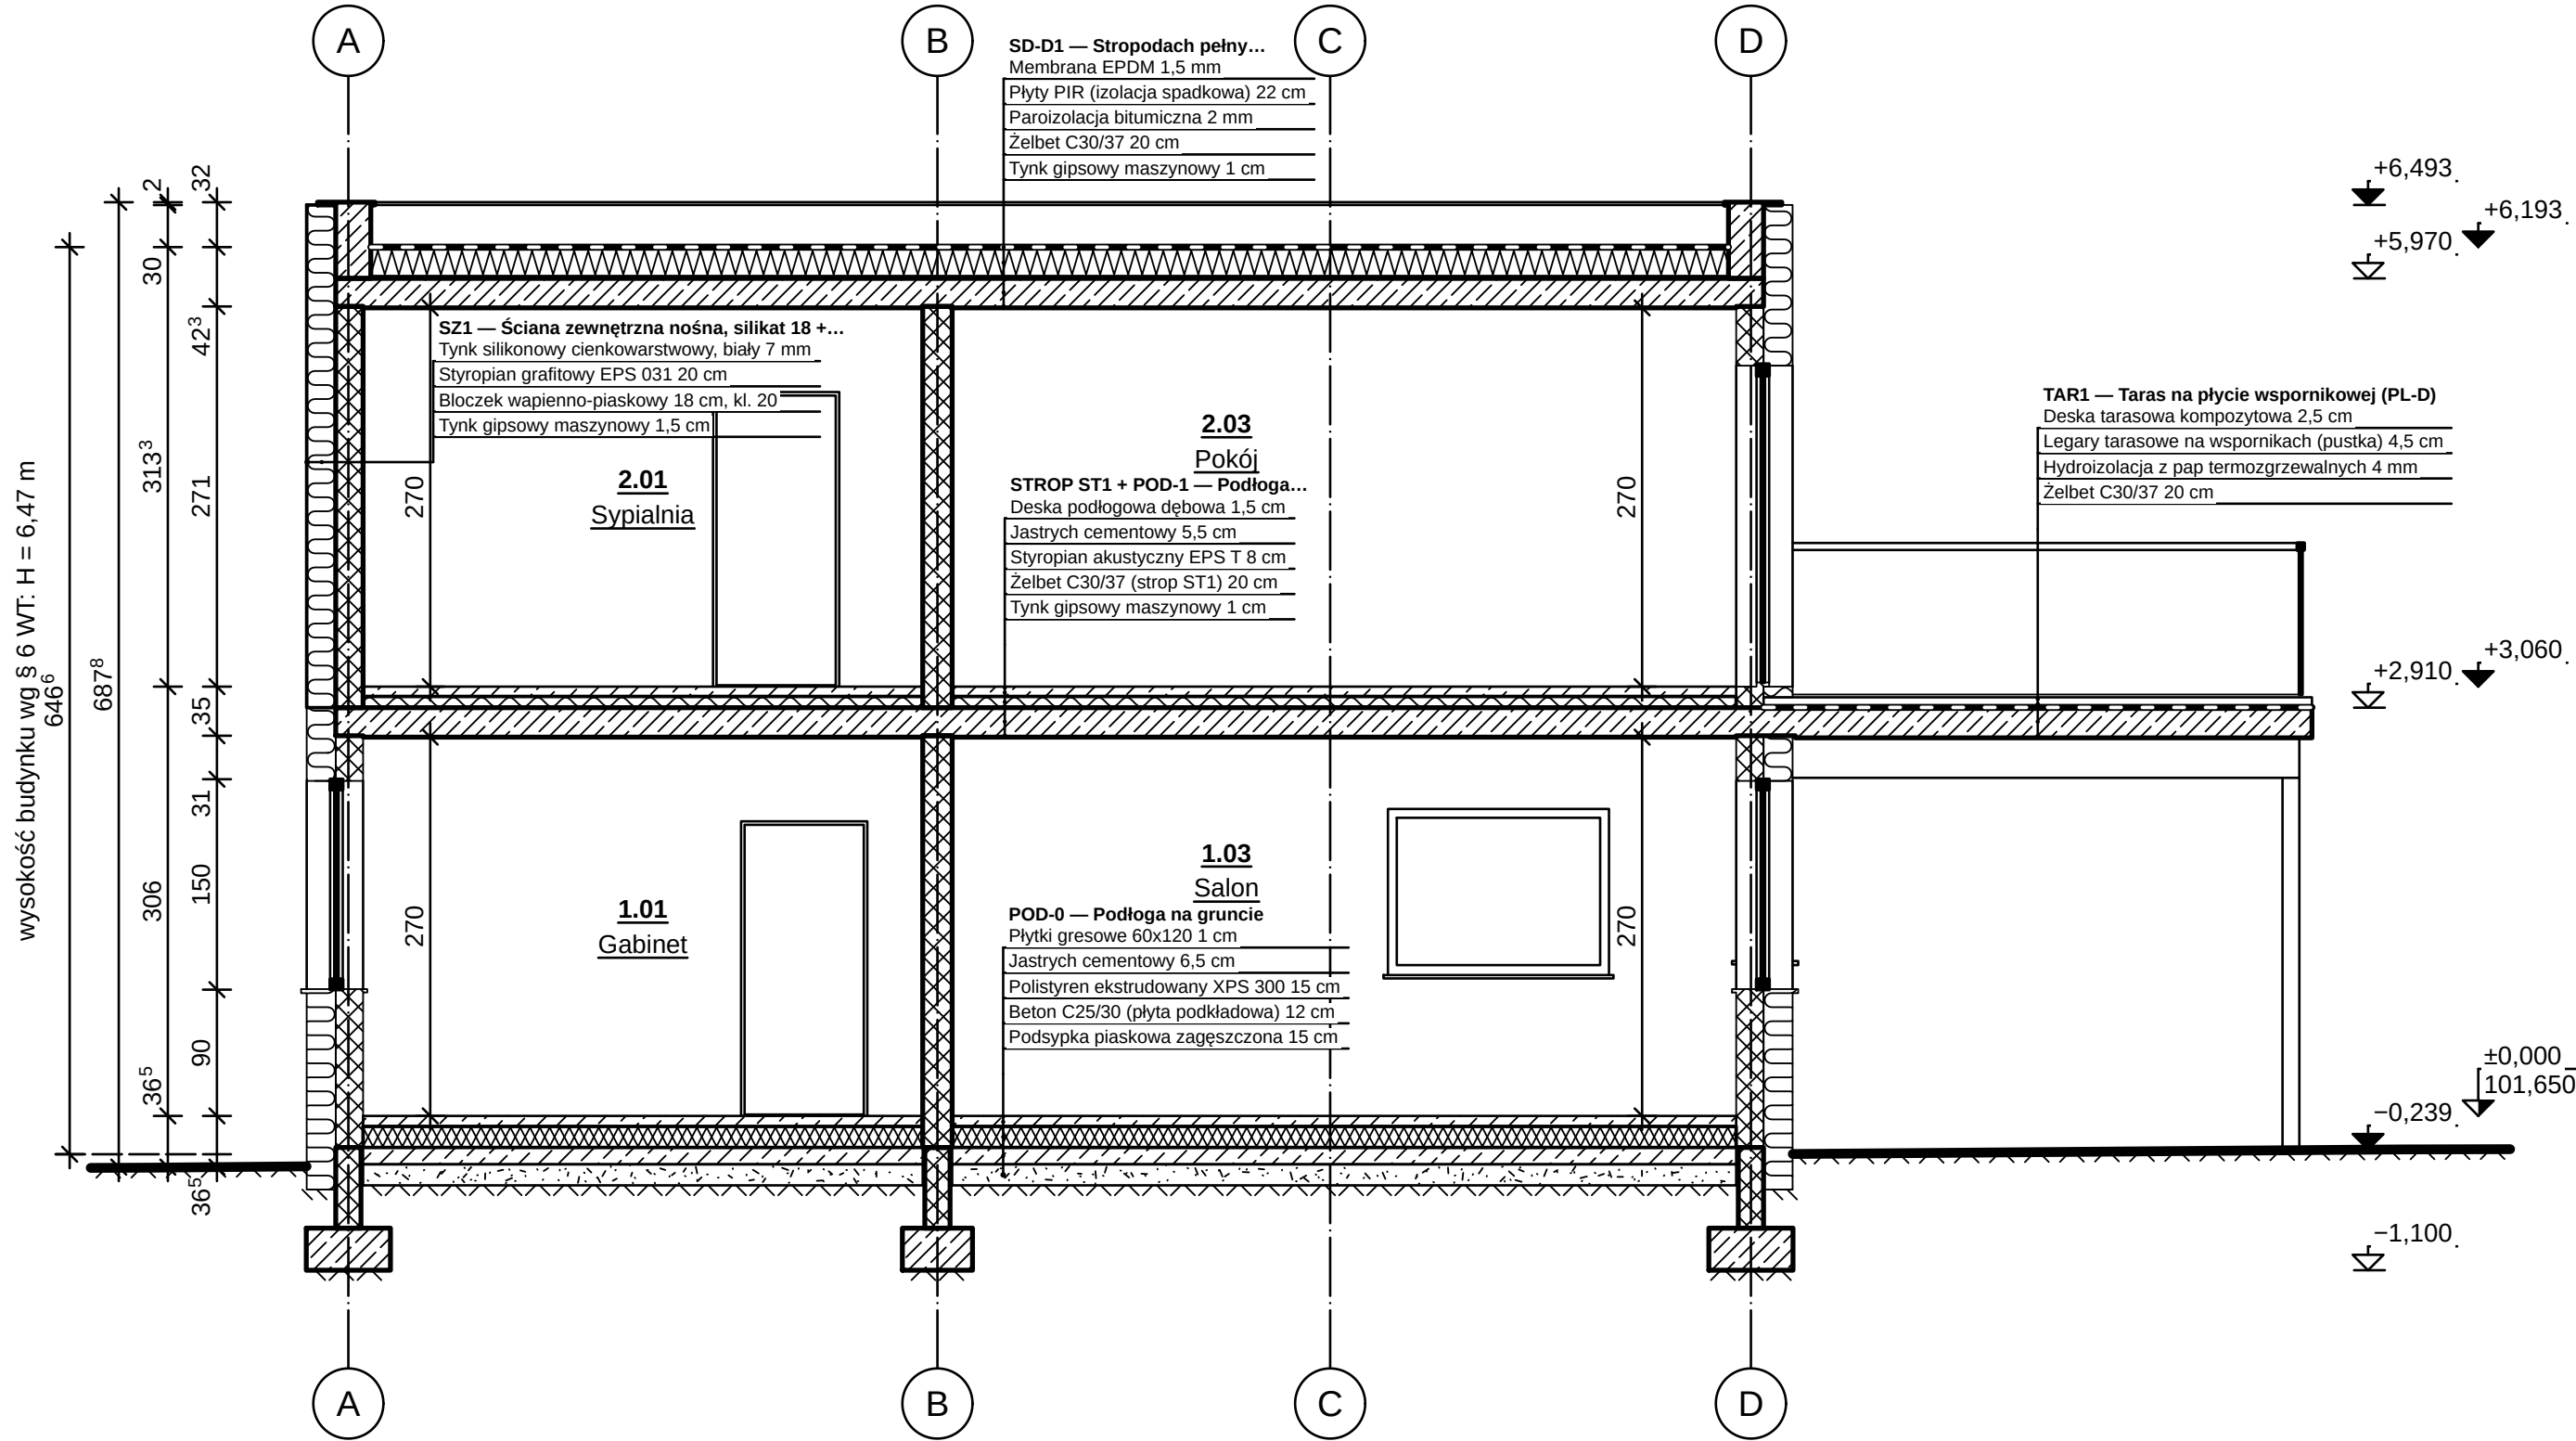

OZNACZENIA MATERIAŁÓW (PN-B-01030 + przyjęte)

	Jastyrych cementowy; Beton C25/30 (plyta podkładowa) — 45° przerywane		Łłoczek wapienno-piaskowy 18 cm, kl. 20 — kratka ukośna 45°/135°
	grunt rodzimy		Podsypka piaskowa zagęszczona
	Styropian grafitowy EPS 031; Styropian akustyczny EPS T — meander „UUU”		Paroizolacja bitumiczna — linia kreskowa cienka 3/1 po ciepłej stronie
	Płyty PIR (izolacja spadkowa) — zygzak z okładzinami		Obróbki blacharskie (blacha powlekana); Stalarka — profile aluminiowe, antracyt; Stal nierdzewna (pochwyty) — zaczerpienie
	Membrana EPDM 1,5 mm; Hydroizolacja z pap termozgrzewalnych — pas czarno-biały		Żelbet C30/37 — 45° na przemian ciągłe i przerywane
	Polistyren ekstrudowany XPS 300 — zygzak podwójny		

OBJAŚNIENIA I UWAGI

- Wymiary w cm (mm w indeksie górnym, np. 24^e = 24,5 cm), rzędne w m względem ±0,000 = 101,650 m n.p.m. (PL-EVRF2007-NH).
- Rzędne: trójkąt zaczerpiony — poziom wykończenia, niezaczerpiony — konstrukcji, w połowie zaczerpiony — poziom ±0,000 z rzędną bezwzględną (PN-B-01025).
- Wysokość budynku wg § 6 WT: od terenu przy najniższej położonym wejściu (−0,273) do wierzchu stropodachu D1 (+6,193) — H = 6,47 m (bez attyk).
- Opisy warstw: kod i nazwa przegrody z modelu, materiały i grubości wg modelu (od góry / od lewej).
- MODEL TESTOWY — rysunek próbny generatorów widoków, dane nie stanowią projektu.
- Rysunek wygenerowany automatycznie z modelu model/test/dom_testowy.yam (wersja 1.0, 2026-09-25) — generatory lamela.views.



REW.		OPIS ZMIANY		DATA	
0		Próba generatorów widoków z modelu testowego		2026-09-25	
PRACOWNIA PROJEKTOWA PRACOWNIA PROJEKTOWA — nazwa do uzupełnienia adres pracowni do uzupełnienia				STADIUM PB	BRANŻA ARCHITEKTURA (AR)
INWESTOR (do uzupełnienia)					
OBIEKT / NAZWA ZAMIERZENIA BUDOWLANEGO					
Budynek testowy pipeline'u (model testowy) — NIE jest projektem Domu LAMELA					
ADRES / LOKALIZACJA (NR DZIAŁKI, OBRĘB, JEDN. EWIDENCYJNA) dz. nr ewid. T-1/1, obręb 0000 Testowo					KAT. OBIEKTU I
FUNKCJA		IMIĘ I NAZWISKO		SPECJALNOŚĆ, NR UPRAWNIENI	DATA
Projektant					
Projektant (wsp.)					
Sprawdzający					
Opracował					
TYTUŁ RYSUNKU					
PRZEKRÓJ B-B					
SKALA 1:50	FORMAT A3×3	DATA WYDANIA 2026-09-25	RODZAJ DOK. przekrój	NR RYSUNKU T-AR-05	ARKUSZ 5/9
					REW. 0