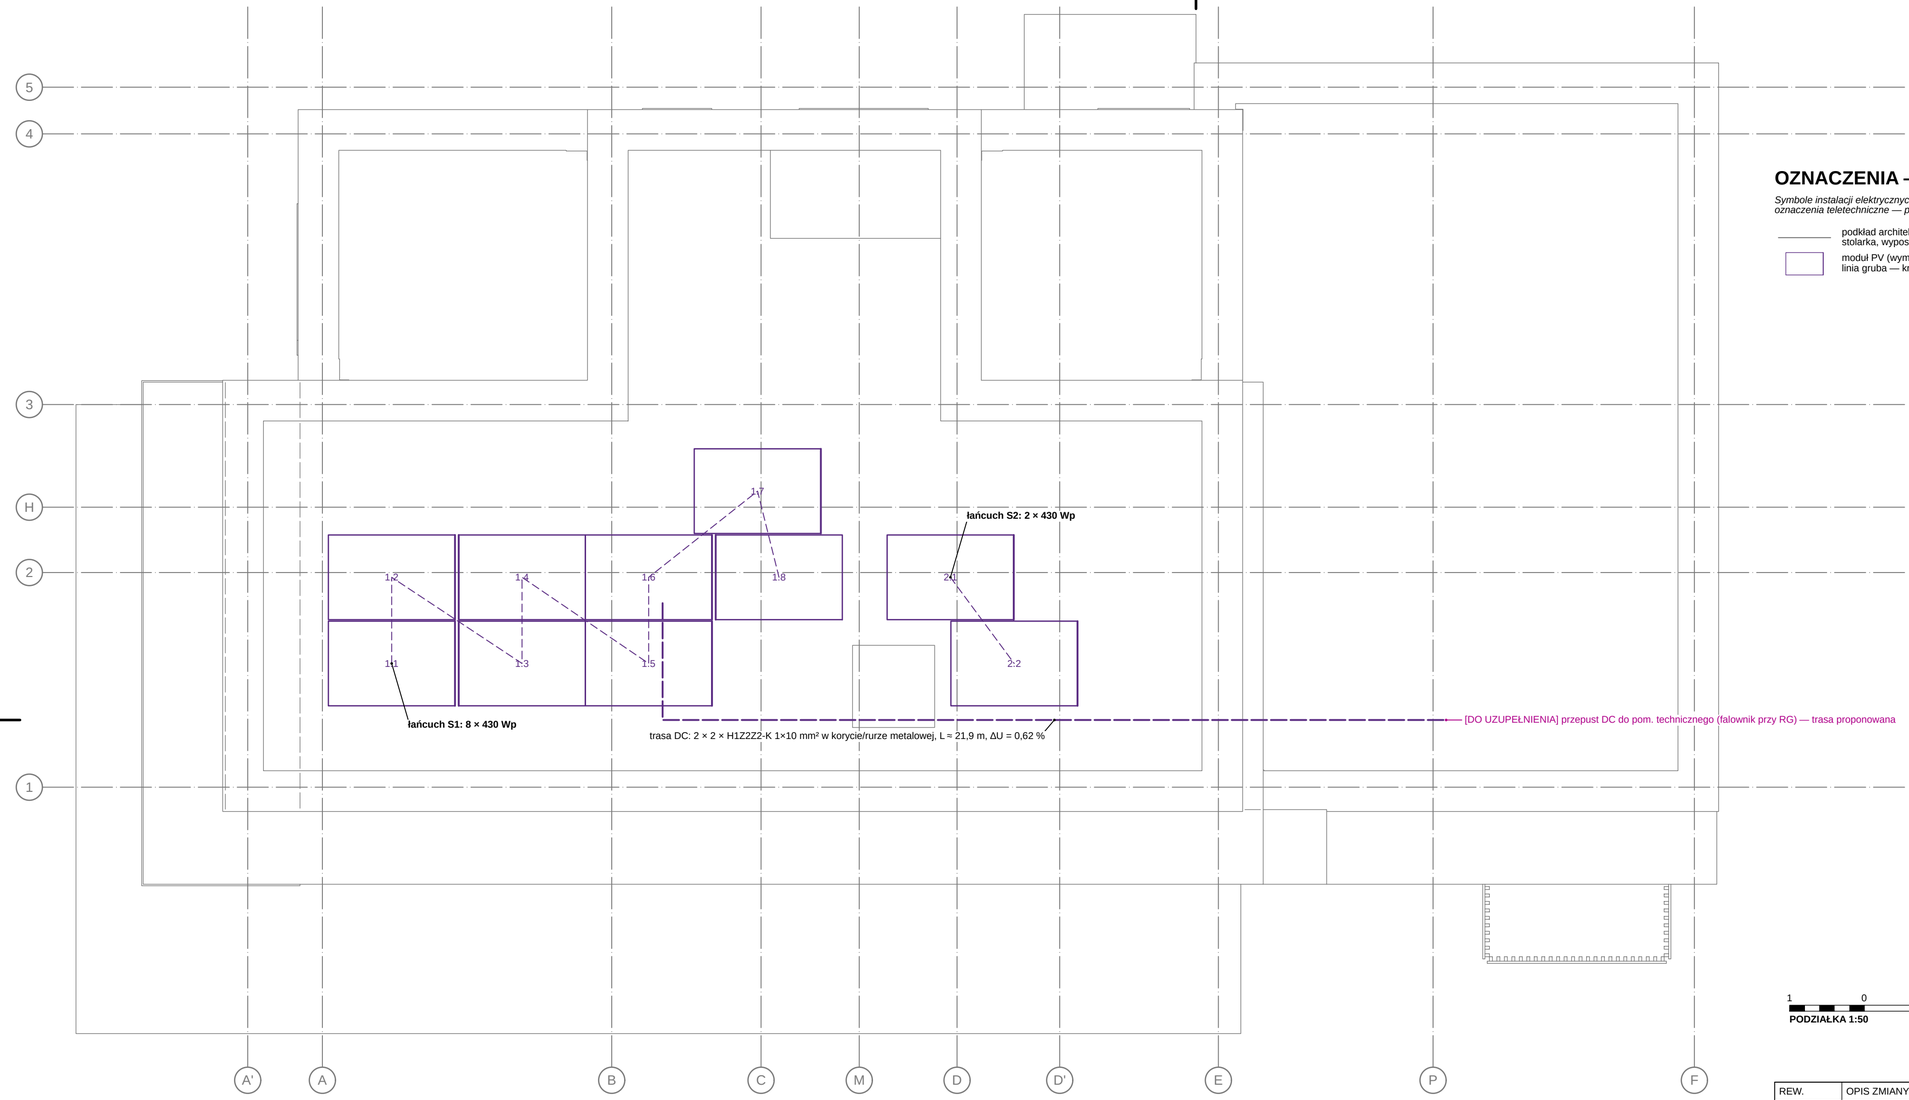


OZNACZENIA — LEGENDA SYMBOLI

Symbole instalacji elektrycznych wg IEC 60617 (baza IEC; PN-EN 60617 — wycofana, stosowana jako praktyka branżowa) i PN-EN ISO 14617; oznaczenia teletechniczne — praktyka branżowa. Obowiązuje legenda na arkuszu.

- podkład architektoniczny (rzut AR — ściany przecięte, stolarka, wyposażenie) — linie cienkie szare
- moduł PV (wymiar rzeczywisty, układ wschód–zachód 10°; linia gruba — krawędź wyższa); <łańcuch>.<nr>
- trasa przewodów DC (H1Z2Z2-K) w korytach/rurach metalowych

N

1 0 1 2 3 4 5 m

PODZIAŁKA 1:50

odcinek kontrolny 100 mm (wydruk 1:1)

INSTALACJA FOTOWOLTAICZNA — RZUT DACHU 1:50

OBJAŚNIENIA I UWAGI

1. Średnice przewodów w mm (d_z×s — rury wielowarstwowe, Ø/DN — kanalizacja, kanały wentylacyjne), przekroje żył w mm², odległości i rzędne w m; ±0,000 = 101,650 m n.p.m. (PL-EVRF2007-NH).
2. Rysunki instalacji na podkładzie rzutów architektury (PB-AR); podkład — linie cienkie szare (warstwy I-PODKLAD*).
3. Instalacja fotowoltaiczna wg PN-HD 60364-7-712, PN-EN 62446-1 (dokumentacja, badania), WT § 184 i art. 29 ust. 4 pkt 3 lit. c PB (moc ≤ 6,5 kWp): 15 × 430 Wp = 6,45 kWp, układ EW10, E ≈ 5610 kWh/a (PVGIS; obliczenia lamela.obliczenia.elektryka.pv).
4. Łańcuchy: 2 × do 8 modułów; U_oc,max = 350 V, U_mpp 196–298 V, I_sc = 14,0 A (obliczenia) — sprawdzić z DTR wybranych modułów i falownika (dane przykładowe, lub równoważne).
5. Rozmieszczenie modułów wyznaczono algorytmicznie w polu użytkowym dachu (odsunięcie ≥ 1,0 m od krawędzi, odstępy od otworów, wpustów, czerpni, wyrzutni i wywiewek); konstrukcja balastowa niskoprofilowa — górna krawędź ≤ wierzchu attyki; obciążenia i balast wg PN-EN 1991-1-4 (projekt konstrukcji).
6. Konstrukcję wsporczą PV połączyć z GSU przewodem wyrównawczym ≥ 6 mm² Cu (712.444.5.5.101); odstęp separacyjny od ewentualnych zwodów wg PN-EN IEC 62305-3.
7. Rysunek wygenerowany automatycznie z modelu model/budynek.yaml (wersja 1.0, 2026-09-25) — generatory lamela.views.

WYNIKI OBLICZEŃ — PV (lamela.obliczenia.elektryka.pv)

Wielkość	Wartość
moduły	15 × PV-430 TOPCon (dane przykładowe)
moc	6,45 kWp
falownik	FAL-6K-3P (dane przykładowe)
energia roczna	5610 kWh/a
pole dachu / użytkowe	87,4 / 47,2 m²

REW.	OPIS ZMIANY	DATA
0	Wydanie — rysunek wygenerowany z modelu	2026-09-25

PRACOWNIA PROJEKTOWA
PRACOWNIA PROJEKTOWA — nazwa do uzupełnienia
adres pracowni do uzupełnienia

STADIUM **PT**

BRANŻA **INSTALACJE ELEKTRYCZNE (IE)**

INWESTOR
(do uzupełnienia)

OBIEKT / NAZWA ZAMIERZENIA BUDOWLANEGO
Budynek mieszkalny jednorodzinny wolnostojący „Dom LAMELA”

ADRES / LOKALIZACJA (NR DZIAŁKI, OBRĘB, JEDN. EWIDENCYJNA)
ul. Lipowa (fikcyjna), dz. nr ewid. 123/4, obręb 0005 Przykładowo, gm. Przykładowo (fikcyjna)

KAT. OBIEKTU **I**

FUNKCJA	IMIĘ I NAZWISKO	SPECJALNOŚĆ, NR UPRAWNIEŃ	DATA	PODPIS
Projektant	[DO UZUPEŁNIENIA]	[DO UZUPEŁNIENIA]		
Projektant (wsp.)	[DO UZUPEŁNIENIA]	[DO UZUPEŁNIENIA]		
Sprawdzający	nie dotyczy (art. 20 ust. 3 pkt 2 PB)	—		
Opracował	[DO UZUPEŁNIENIA]	[DO UZUPEŁNIENIA]		

TYTUŁ RYSUNKU
INSTALACJA FOTOWOLTAICZNA — RZUT DACHU

SKALA	FORMAT	DATA WYDANIA	RODZAJ DOK.	NR RYSUNKU	ARKUSZ	REW.
1:50	690×420	2026-09-25	rzut instalacji	**PT-IE-10**	10/14	**0**

nst. 690×420