
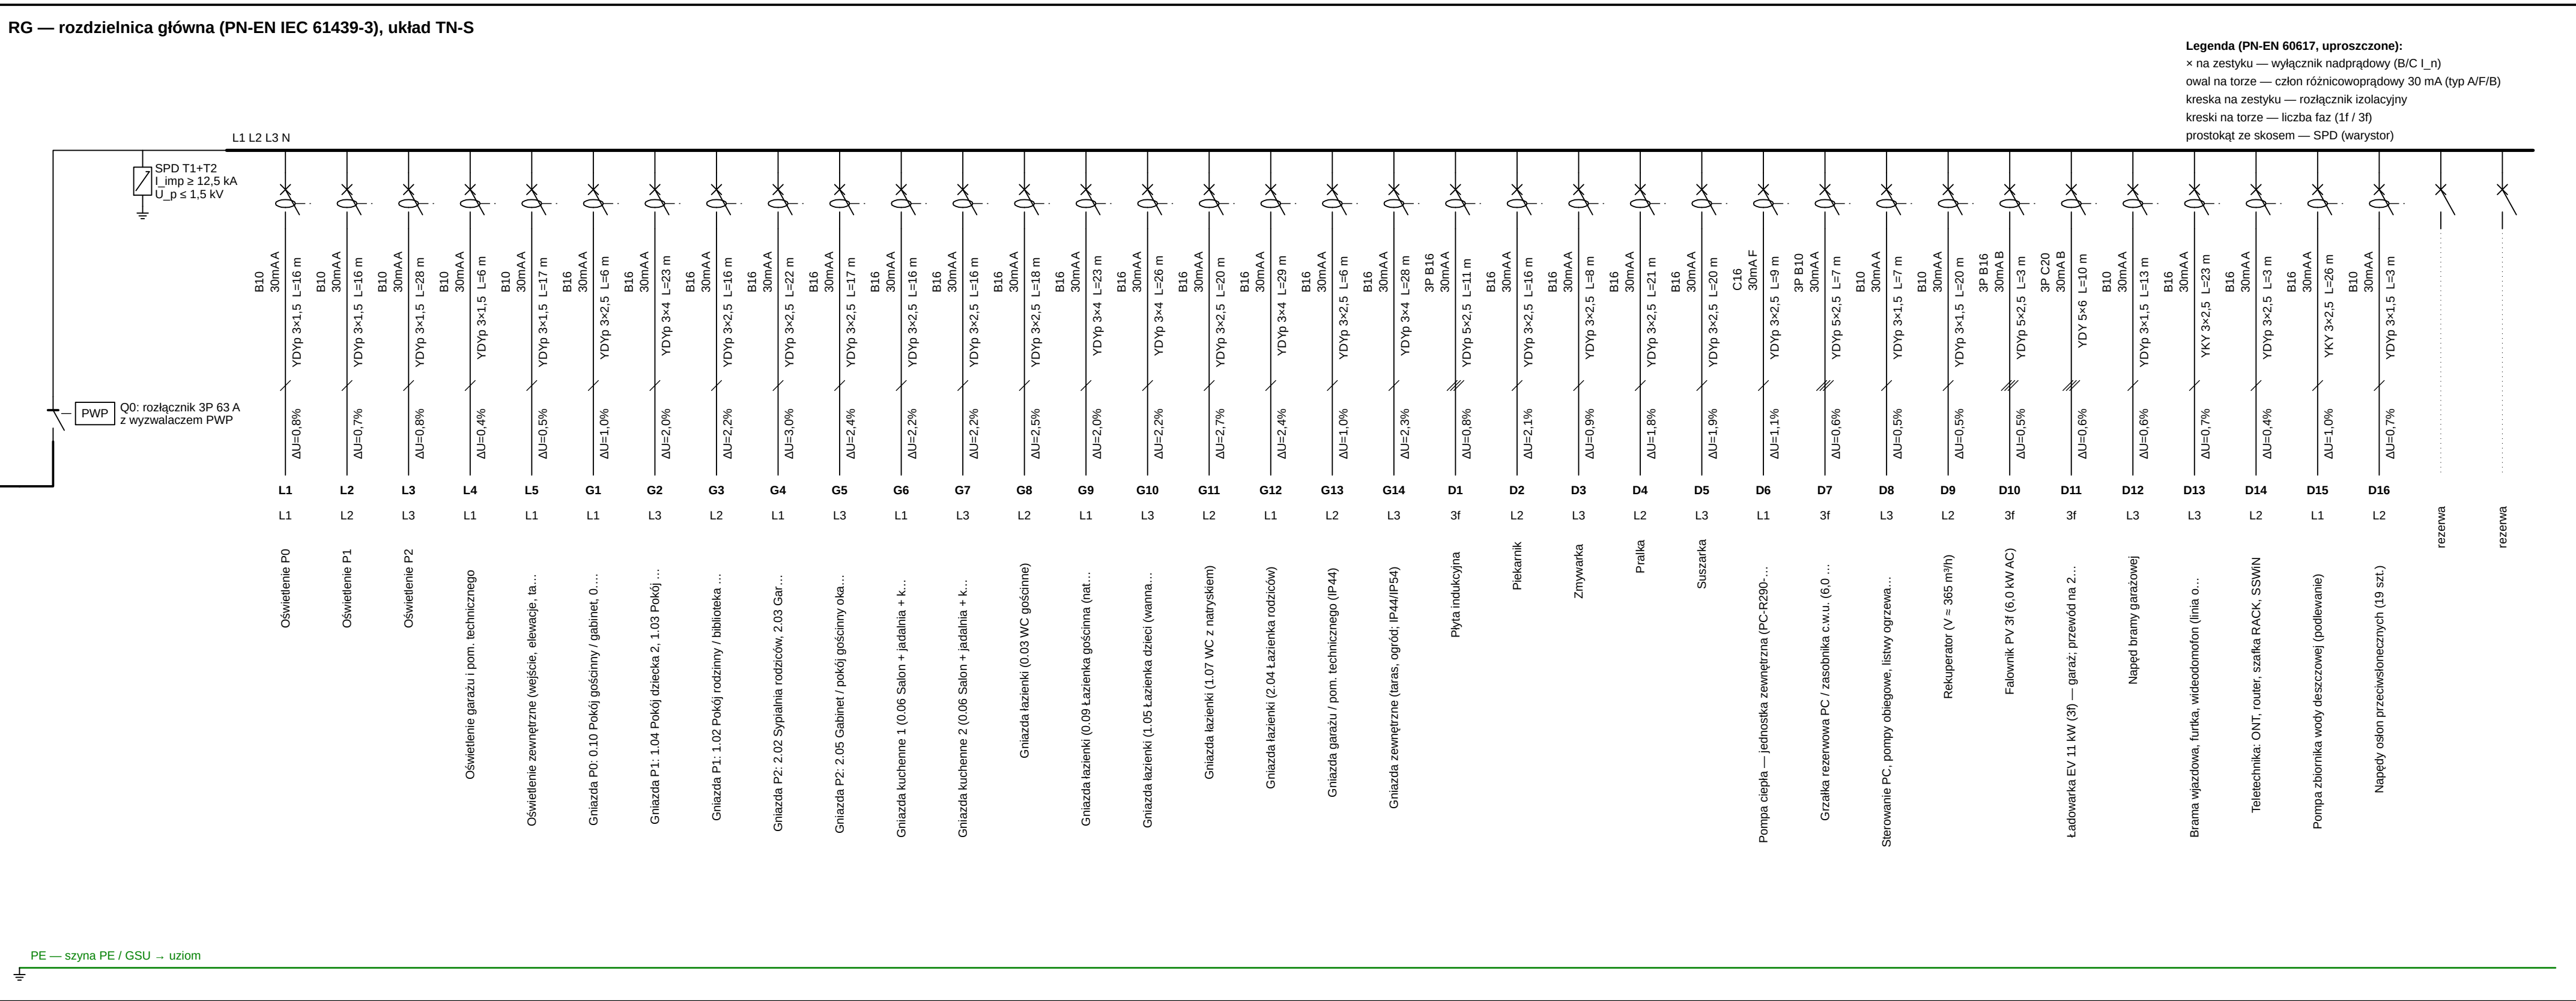


odcinek kontroly 100 mm (wydruk 1:1)

SCHEMAT IDEOWY ROZDZIELNICY GŁÓWNEJ RG

Schemat ideowy RG — Dom LAMELA. Dane przykładowe [ZAL]; wartości z obliczeń obwodów (lamela.obliczenia.elektryka.obwody).

WLZ YKY 5×25, L = 28,3 m
ΔU = 0,37 % (ziemia, D1)

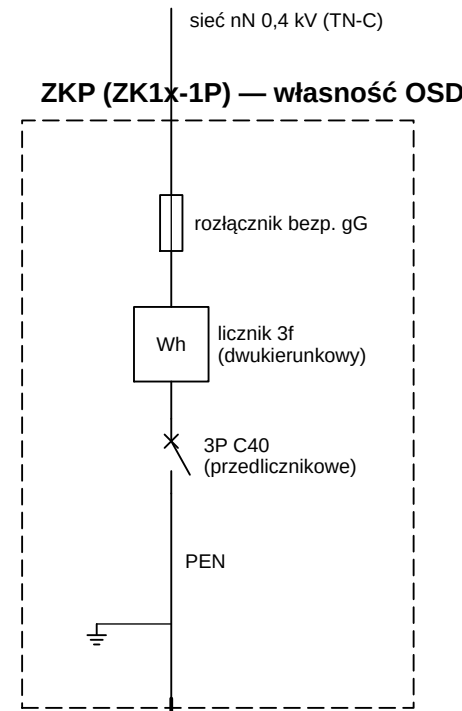

OZNACZENIA

Legenda symboli — na schemacie (PN-EN 60617 / PN-EN ISO 14617 w uproszczeniu; oznaczenia instalacji sanitarnych — praktyka branżowa).

linie schematu — wg legendy na rysunku

OBJAŚNIENIA I UWAGI

- Schemat bez skali; rzędne w m względem ±0,000 (posadzka parteru), średnice w mm.
- Rysunki instalacji na podkładzie rzutów architektury (PB-AR); podkład — linie cienkie szare (warstwy I-PODKŁAD*).
- Schemat odwzorzony wektorowo z funkcji lamela.obliczenia.elektryka.schemat_rg (dane: obwody, WLZ, SPD, PWP) — treść i wartości z obliczeń na aktualnym modelu; skala rysunkowa 1.23 mm/jedn. (pismo ≥ 1,8 mm), przesunięto 0 napisów kolidujących.
- Dane urządzeń przykładowe (bez nazw handlowych) — do zastąpienia DTR wybranych wyrobów (lub równoważnych).
- WLZ YKY 5×25, L = 28,3 m; SPD: SPD typ 1+2 (T1+T2), I_imp ≥ 12,5 kA/biegun, U_p ≤ 1,5 kV, U_c ≥ 275 V; układ 3+1 (TN-S) lub 4+0 przy rozdziale PEN w RG.
- Aparatura modułowa wg PN-EN 60898-1, PN-EN 61009-1, PN-EN 61008-1; rozdzielnica wg PN-EN IEC 61439-3; PWP wg WT § 183 (przycisk przy wejściu, oznakowany).
- Rysunek wygenerowany automatycznie z modelu model/budynek.yaml (wersja 1.0, 2026-09-25) — generatory lamela.views.

REW.	OPIS ZMIANY		DATA	
0	Wydanie — rysunek wygenerowany z modelu		2026-09-25	
PRACOWNIA PROJEKTOWA PRACOWNIA PROJEKTOWA — nazwa do uzupełnienia adres pracowni do uzupełnienia			STADIUM PT	BRANŻA INSTALACJE ELEKTRYCZNE (IE)
INWESTOR (do uzupełnienia)				
OBIEKT / NAZWA ZAMIERZENIA BUDOWLANEGO Budynek mieszkalny jednorodzinny wolnostojący „Dom LAMELA”				
ADRES / LOKALIZACJA (NR DZIAŁKI, OBRĘB, JEDN. EWIDENCYJNA) ul. Lipowa (fikcyjna), dz. nr ewid. 123/4, obręb 0005 Przykładowo, gm. Przykładowo (fikcyjna)				KAT. OBIEKTU I
FUNKCJA	IMIĘ I NAZWISKO	SPECJALNOŚĆ, NR UPRAWNIEŃ	DATA	PODPIS
Projektant	[DO UZUPEŁNIENIA]	[DO UZUPEŁNIENIA]		
Projektant (wsp.)	[DO UZUPEŁNIENIA]	[DO UZUPEŁNIENIA]		
Sprawdzający	nie dotyczy (art. 20 ust. 3 pkt 2 PB)	—		
Opracował	[DO UZUPEŁNIENIA]	[DO UZUPEŁNIENIA]		
TYTUŁ RYSUNKU SCHEMAT ROZDZIELNICY GŁÓWNEJ RG				
SKALA —	FORMAT 870×297	DATA WYDANIA 2026-09-25	RODZAJ DOK. schemat instalacji	NR RYSUNKU PT-IE-14
				ARKUSZ 14/14
				REW. 0