


ZBROJENIE DOLNE PŁYTY FUNDAMENTOWEJ PF1+PF2 1:50


OBJAŚNIENIA I UWAGI

- Wymiary w cm (mm w indeksie górnym, np. 24⁵ = 24,5 cm), rzędne w m względem ±0,000 = 101,650 m n.p.m. (PL-EVRF2007-NH).
- Zestawienie stali, strefy zbrojenia narożnego/na ścinanie i dozbrojenia — arkusz PT-BO-05.
- Naroża żeber obwodowych: pręty narożne L (poz. 47) 24 Ø20, ramiona l₀ = 110 cm — po 2 dołem i 2 górą w każdym narożu i na styku żeber (ciągłość zbrojenia podłużnego, PN-EN 1992-1-1 8.7).
- Stal zbrojeniowa B500SP (klasa ciągliwości C, f_{yk} = 500 MPa) wg PN-H-93220:2018-02 / PN-EN 10080; pręty gięte na zimno na trzpieniach ϕ $\geq$ 4 ϕ ($\phi \leq 16$ mm) i $\geq 7\phi$ ($\phi > 16$ mm) — PN-EN 1992-1-1 tabl. 8.1N; oznaczenia prętów i kształtów wg PN-EN ISO 3766 (liczba, nr pozycji, Ø, rozstaw [cm], długość rozwinięcia l [cm]).
- Otulinę zapewnić podkładkami dystansowymi (rozstaw $\leq 1,0$ m, dla siatek górnych — podpórki „kobylicy” $\leq 1,0$ m) — PN-EN 13670 p. 6.5; odchyłka wykonawcza Δc_{dev} = 10 mm uwzględniona w c_{nom} (PN-EN 1992-1-1 4.4.1.3 + NA).
- Pręty łączące na zakład l₀ (tabela w stopce zestawienia), styki mijankowo — w jednym przekroju ≤ 50 % prętów; odstęp w świetle prętów $\geq \max(\phi; d_g + 5$ mm; 20 mm) — PN-EN 1992-1-1 8.2(2), 8.7.2; pręty dolne w strefie podpory zakotwić $\geq 10\phi$ za licem (9.3.1.2(1) → 9.2.1.5).
- Siatki płyty: dołem Ø14 co 15, górą Ø14 co 7,5 cm w obu kierunkach — dobór modułu (dobierz „siatkę”) z A_{s,req} (MES płyty fundamentowej (90 % pola poza żebrami)); dozbrojenia (obszary kreskowe D...) — pręty między prętami siatki; pręty > 12 m łączone na zakład (mijankowo).
- Kolejność robót: podsypka zagęszczona (l_s $\geq 0,98$) → XPS (płyty układane mijankowo, szczelnie) → folia PE → zbrojenie żeber i płyty, uziom/przewód wyrównawczy, tuleje przejść → betonowanie płyty z żebrami jednym zabiegiem (bez przerw roboczych) → pielęgnacja ≥ 7 dni (PN-EN 13670 p. 8.5).
- Płyta fundamentowa — analiza MES na podłożu sprężystym (moduł płyty fundamentowa: płyta ACM z żebrami jako pasma h = h_{płyty} + h_{żebra}, sprężyny Winklera, kontakt jednostronny, 30 obliczeń: kombinacje STR × 3 warianty k_s = 2652, 5303 i 10606 kN/m³ z M₀ i wymiarów płyty — Bowles (5-16a), PN-EN 1997-1 zał. F.2; weryfikacja: belka Hetényiego, błąd < 1 %). Maks. docisk p_d = 364 kPa (q_{Rd,lok} = 319 kPa), osiadanie w_k = 44 mm, odrywanie 0 % powierzchni.
- UWAGA — MES płyty wykazuje niespełnione warunki: Docisk lokalny do podłoża (pasma pod żebrami) (364 > 319) [WYMAGA ZMIANY MODELU].
- Strefy zakreskowane ($\mu > \mu_{lim}$, 16 el. MES): przekrój podwójnie zbrojony — A_{s1} w warstwie rozciąganej (siatka + dozbrojenie/pręty żebra), A_{s2} w warstwie przeciwnie (ujęte w wymaganiu tej warstwy); pręty ściskane objęte strzemiionami żebra s $\leq 15\phi$ (PN-EN 1992-1-1 9.2.1.2(3)).
- Rysunek wygenerowany automatycznie z modelu model/budynek.yaml (wersja 1.0, 2026-09-25) — generatory lamela.views.

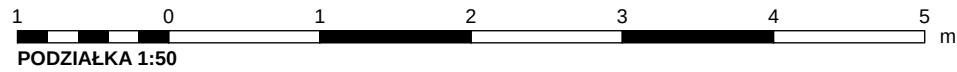

OZNACZENIA NA RYSUNKU

- pręt reprezentatywny grupy (warstwa dolna), linia gruba
— pręt z odgięciem 90° — odgięcie (ramię) pokazane w płaszczyźnie rysunku
— linia rozkładu prętów grupy (zasięg), kółko — pręt reprezentatywny
③ numer pozycji pręta (zestawienie stali)
--- żebra i pogrubienia pod płytą (zbrojenie — przekroje 1-1, 2-2, 3-3)

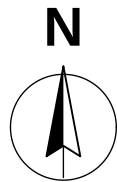

REW.	OPIS ZMIANY			DATA		
0	Wydanie — rysunek wygenerowany z modelu			2026-09-25		
PRACOWNIA PROJEKTOWA PRACOWNIA PROJEKTOWA — nazwa do uzupełnienia adres pracowni do uzupełnienia			STADIUM PT	BRANŻA KONSTRUKCJA (BO)		
INWESTOR (do uzupełnienia)						
OBIEKT / NAZWA ZAMIERZENIA BUDOWLANEGO Budynek mieszkalny jednorodzinny wolnostojący „Dom LAMELA”						
ADRES / LOKALIZACJA (NR DZIAŁKI, OBRĘB, JEDN. EWIDENCYJNA) ul. Lipowa (fikcyjna), dz. nr ewid. 123/4, obręb 0005 Przykładowo, gm. Przykładowo (fikcyjna)				KAT. OBIEKTU I		
FUNKCJA	IMIĘ I NAZWISKO	SPECJALNOŚĆ, NR UPRAWNIEŃ	DATA	PODPIS		
Projektant						
Projektant (wsp.)						
Sprawdzający						
Opracował						
TYTUŁ RYSUNKU ZBROJENIE DOLNE PŁYTY FUNDAMENTOWEJ						
SKALA 1:50	FORMAT A2	DATA WYDANIA 2026-09-25	RODZAJ DOK. rysunek zbrojenia	NR RYSUNKU PT-BO-03	ARKUSZ 3/26	REW. 0