


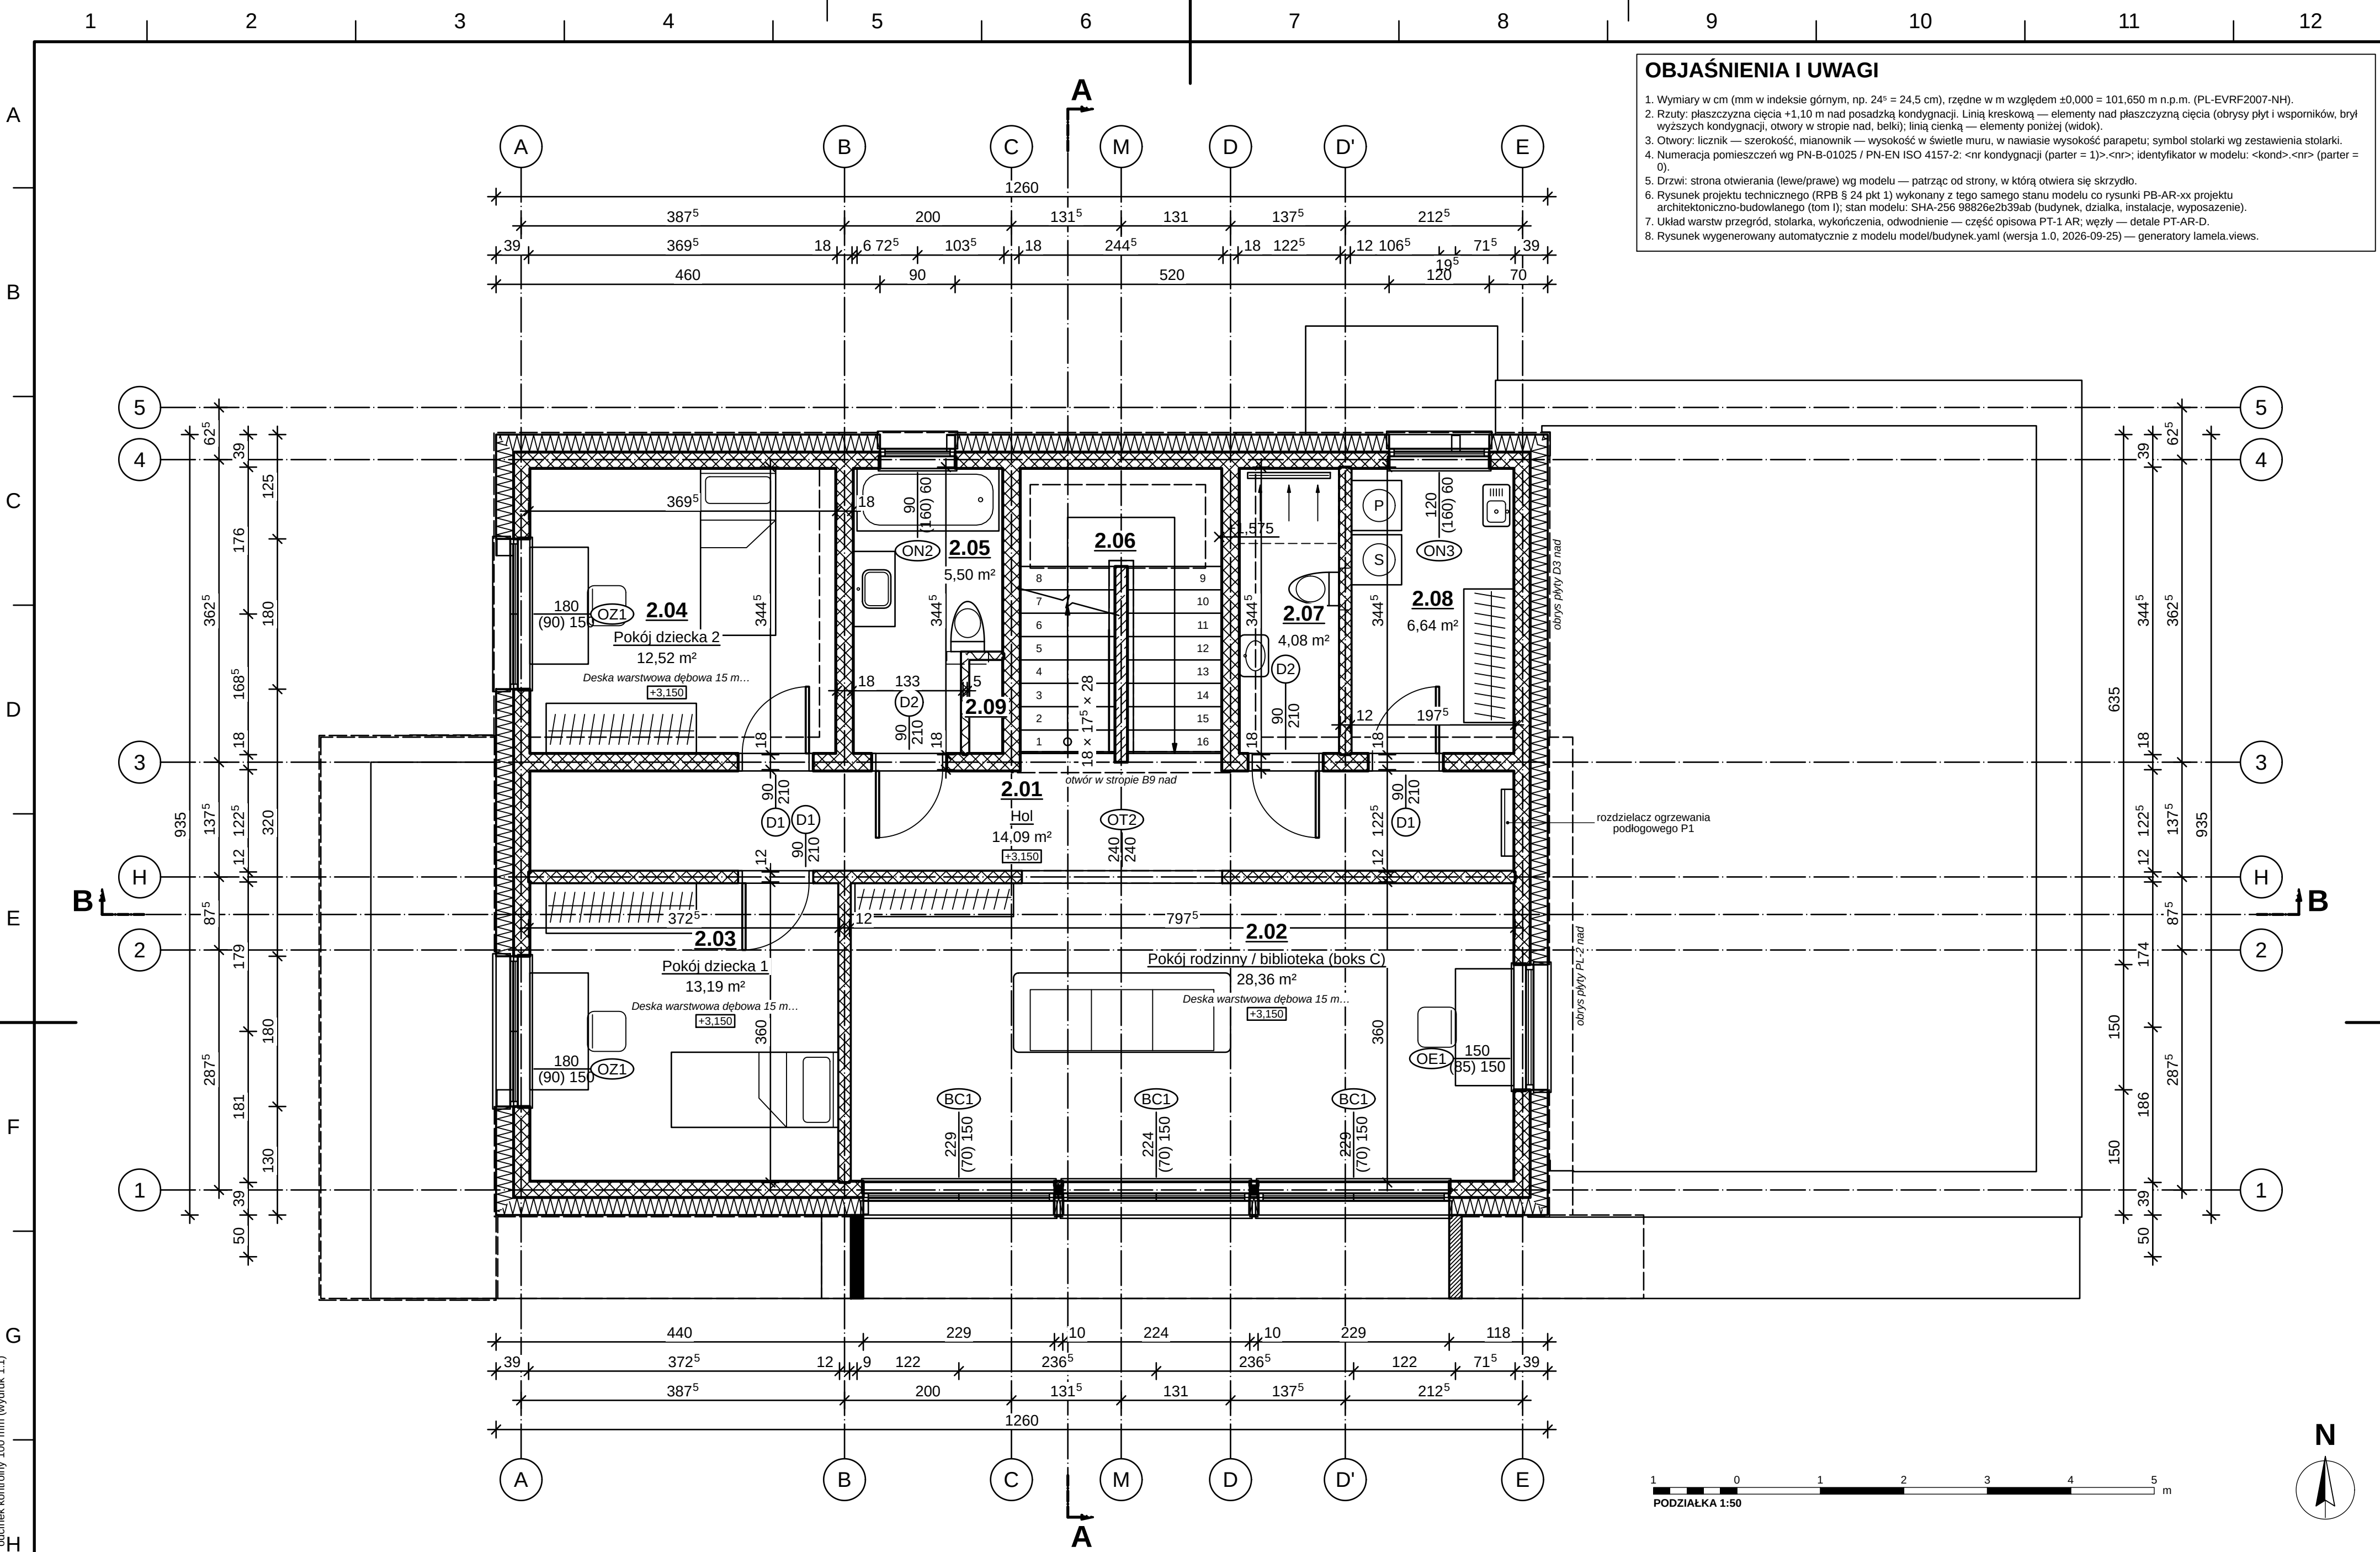

OBJAŚNIENIA I UWAGI

- Wymiary w cm (mm w indeksie górnym, np. 24⁵ = 24,5 cm), rzędne w m względem ±0,000 = 101,650 m n.p.m. (PL-EVRF2007-NH).
- Rzuty: płaszczyzna cięcia +1,10 m nad posadzką kondygnacji. Linia kreskową — elementy nad płaszczyzną cięcia (obrysy płyt i wsporników, bryły wyższych kondygnacji, otwory w stropie nad, belki); linią cieniłą — elementy poniżej (widok).
- Otwory: licznik — szerokość, mianownik — wysokość w świetle muru, w nawiasie wysokość parapetu; symbol stolarki wg zestawienia stolarki.
- Numeracja pomieszczeń wg PN-B-01025 / PN-EN ISO 4157-2: <nr kondygnacji (parter = 1)>, <nr>; identyfikator w modelu: <kond>, <nr> (parter = 0).
- Drzwi: strona otwierania (lewe/prawe) wg modelu — patrzac od strony, w którą otwiera się skrzydło.
- Rysunek projektu technicznego (RPB § 24 pkt 1) wykonany z tego samego stanu modelu co rysunki PB-AR-xx projektu architektoniczno-budowlanego (tom I); stan modelu: SHA-256 98826e2b39ab (budynek, działka, instalacje, wyposażenie).
- Układ warstw przegród, stolarka, wykończenia, odwodnienie — część opisowa PT-1 AR; węzły — detale PT-AR-D.
- Rysunek wygenerowany automatycznie z modelu model/budynek.yaml (wersja 1.0, 2026-09-25) — generatory lamela.views.

RZUT I PIĘTRA 1:50

ZESTAWIENIE POMIESZCZEŃ

Nr	Nazwa pomieszczenia	Posadzka	Kat.	Wys. [m]	Pow. [m²]
2.02	Pokój rodzinny / biblioteka (boks C)	Deska warstwowa dębowa 15 mm, klejona	podst.	2,77	28,36
2.01	Hol	Deska warstwowa dębowa 15 mm, klejona	ruchu	2,77	14,09
2.03	Pokój dziecka 1	Deska warstwowa dębowa 15 mm, klejona	podst.	2,77	13,19
2.04	Pokój dziecka 2	Deska warstwowa dębowa 15 mm, klejona	podst.	2,77	12,52
2.08	Pralnia z suszarnią	Płytki gresowe 60×120 na kleju C2TE S1	pomoc.	2,77	6,64
2.05	Łazienka dzieci (wanna)	Płytki gresowe 60×120 na kleju C2TE S1	pomoc.	2,77	5,50
2.07	WC z natryskiem	Płytki gresowe 60×120 na kleju C2TE S1	pomoc.	2,77	4,08
2.06	Klatka schodowa	Deska warstwowa dębowa 15 mm, klejona	ruchu	2,77	0,49
2.09	Szacht instalacyjny SI		techn.	2,77	0,45
RAZEM powierzchnia netto					85,33
w tym podstawowa + pomocnicza					70,30

OZNACZENIA MATERIAŁÓW (PN-B-01030 + przyjęte)

- Włna mineralna 035 (szkielet, docieplenia, ściana dom-garaż) — meander „UUU”
- Styropian grafitowy EPS 031 (ETICS, NRO w systemie) — zygzak „VVV”
- Bluszcz wapienno-piaskowy 12 cm, kl. 15 (ścianki działowe, licowy w klatce); Bluszcz wapienno-piaskowy (silikat) 18 cm, kl. 20, gr. 1, na zaprawie cienkowarstwowej — kratka ukośna 45°/135°
- Rama boksu C: ruszt stalowy ocynkowany w układzinie z blachy aluminiowej RAL 7016 (pusta w środku); Stal konstrukcyjna S355 (słupy RK, rama boksu C), cynkowana ogniowo + malowana proszkowo RAL 7016 — zaczerpnięcie
- Żelbet C25/30, B500SP (stropy, płyta fundamentowa, ściany); Żelbet C30/37 XC4/XF1 (krawędzie płyt wysuniętych, attyki, belki) — 45° na przemian ciagle i przerywane

OZNACZENIA LINII

- elementy nad płaszczyzną cięcia (obrysy płyt, wsporników, bryły wyższych kondygnacji)
- elementy poniżej płaszczyzny cięcia (widok z góry)
- osie konstrukcyjne; linia punktowa z pogrubionymi końcami — ślad przekroju

REW.	OPIS ZMIANY		DATA			
0	Wydanie — rysunek wygenerowany z modelu		2026-09-25			
PRACOWNIA PROJEKTOWA PRACOWNIA PROJEKTOWA — nazwa do uzupełnienia adres pracowni do uzupełnienia			STADIUM PT	BRANŻA ARCHITEKTURA (AR)		
INWESTOR (do uzupełnienia)						
OBIEKT / NAZWA ZAMIERZENIA BUDOWLANEGO Budynek mieszkalny jednorodzinny wolnostojący „Dom LAMELA”						
ADRES / LOKALIZACJA (NR DZIAŁKI, OBRĘB, JEDN. EWIDENCYJNA) ul. Lipowa (fikcyjna), dz. nr ewid. 123/4, obręb 0005 Przykładowo, gm. Przykładowo (fikcyjna)				KAT. OBIEKTU I		
FUNKCJA	IMIĘ I NAZWISKO		SPECJALNOŚĆ, NR UPRAWNIENI	DATA	PODPIS	
Projektant	[DO UZUPEŁNIENIA]		[DO UZUPEŁNIENIA]			
Projektant (wsp.)	[DO UZUPEŁNIENIA]		[DO UZUPEŁNIENIA]			
Sprawdzający	nie dotyczy (art. 20 ust. 3 pkt 2 PB)		—			
Opracował	[DO UZUPEŁNIENIA]		[DO UZUPEŁNIENIA]			
TYTUŁ RYSUNKU RZUT I PIĘTRA						
SKALA 1:50	FORMAT 594×490	DATA WYDANIA 2026-09-25	RODZAJ DOK. rzut	NR RYSUNKU PT-AR-02	ARKUSZ 2/5	REW. 0