

TOM PRÓBNY — SILNIK RYSUNKOWY

Lp.	Nr rys.	Tytuł rysunku	Skala	Format
1	DEMO-01	RZUT PRÓBNY — FRAGMENT PARTERU	1:50	A3
2	DEMO-02	PRZEKRÓJ PRÓBNY A-A	1:50, 1:20	A3
3	DEMO-03	TABLICA OZNACZEŃ: MATERIAŁY I SYMBOLE	—	A2

PRACOWNIA PROJEKTOWA

STADIUM

BRANŻA

INWESTOR

OBIEKT / NAZWA ZAMIERZENIA BUDOWLANEGO

ADRES / LOKALIZACJA (NR DZIAŁKI, OBRĘB, JEDN. EWIDENCYJNA)

KAT. OBIEKTU

FUNKCJA	IMIĘ I NAZWISKO	SPECJALNOŚĆ, NR UPRAWNIEŃ	DATA	PODPIS
Projektant				
Projektant (wsp.)				
Sprawdzający				
Opracował				

TYTUŁ RYSUNKU

SPIS RYSUNKÓW

SKALA

—

FORMAT


A4

DATA

NR RYSUNKU

00

REWIZJA

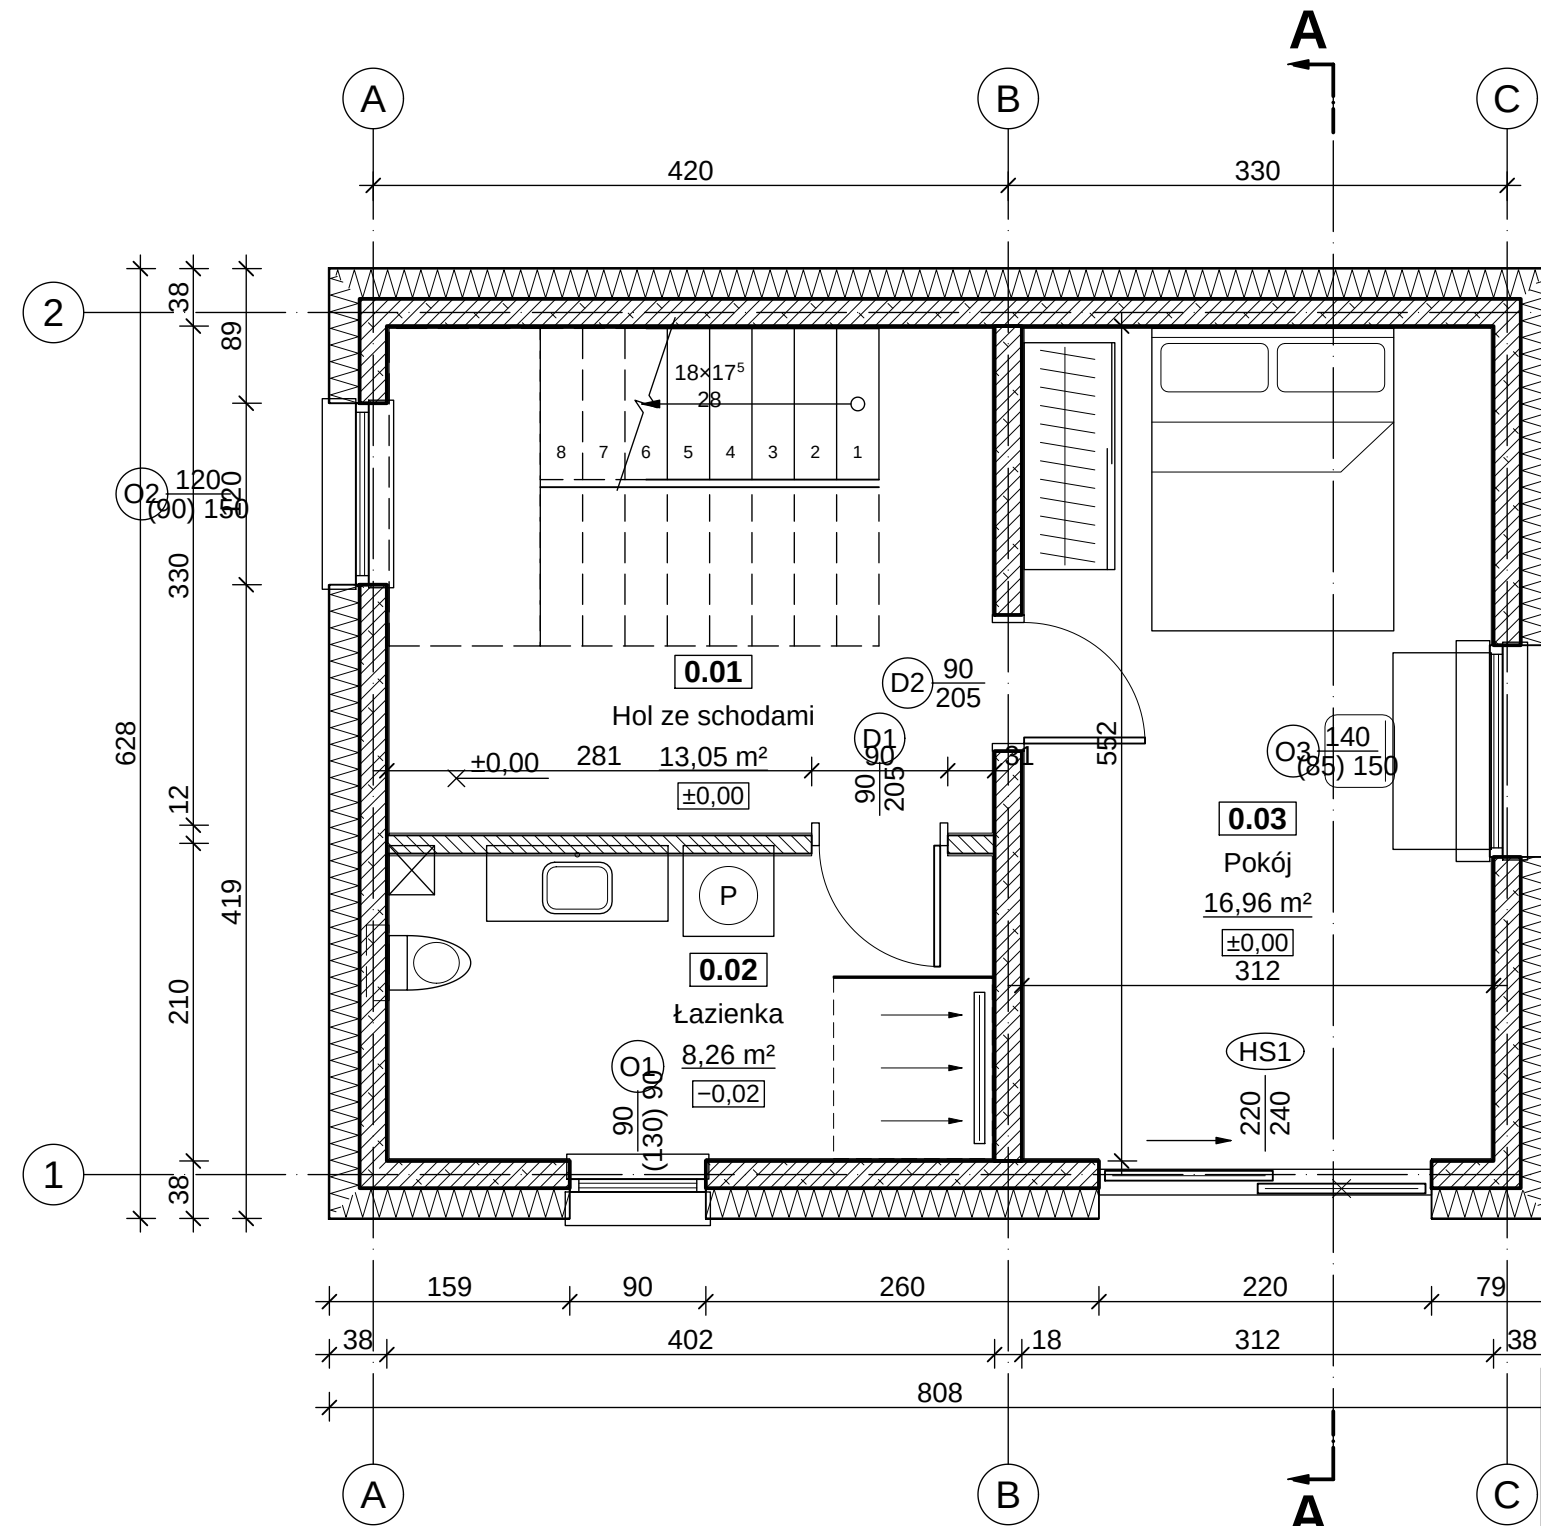

RZUT PARTERU — FRAGMENT 1:50

ZESTAWIENIE POMIESZCZEŃ

Nr	Nazwa pomieszczenia	Posadzka	Pow. [m²]
0.01	Hol ze schodami	gres	13,05
0.02	Łazienka	gres	8,26
0.03	Pokój	deska	16,96
RAZEM			38,27

ZESTAWIENIE OTWORÓW (w świetle muru)


Symbol	Szer. [cm]	Wys. [cm]	Parapet [cm]
O1	90	90	130
HS1	220	240	0
O2	120	150	90
O3	140	150	85
D1	90	205	—
D2	90	205	—

OZNACZENIA MATERIAŁÓW



	Mur z cegieł i pustaków ceramicznych		Izolacja termiczna twarda (EPS) — zygzak
	Mur z bloczków wapienno-piaskowych (silikatowych)		Tynk, zaprawa

UWAGI

- Wymiary w cm (mm w indeksie górnym), rzędne w m. Rzędna $\pm 0,00$ = posadzka parteru = 101,65 m n.p.m.
- Wymiary otworów w świetle muru: licznik — szerokość, mianownik — wysokość, w nawiasie wysokość parapetu.
- Rysunek testowy silnika — dane nie stanowią projektu.

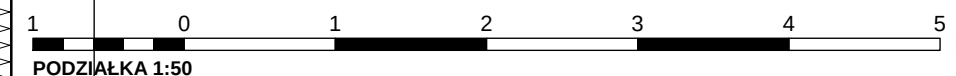

REW.	OPIS ZMIANY		DATA	
0	Wydanie do weryfikacji silnika rysunkowego		2026-09-25	
PRACOWNIA PROJEKTOWA PRACOWNIA PROJEKTOWA — nazwa do uzupełnienia adres pracowni do uzupełnienia		STADIUM PB	BRANŻA ARCHITEKTURA	
INWESTOR (do uzupełnienia)				
Budynek mieszkalny jednorodzinny „Dom LAMELA” — PRÓBA SILNIKA RYSUNKOWEGO (rysunek testowy)				
ADRES / LOKALIZACJA (NR DZIAŁKI, OBRĘB, JEDN. EWIDENCYJNA) dz. nr ewid. 123/4, obręb 0005 Przykładowo, jedn. ewid. Przykładowo (dane fikcyjne)				KAT. OBIEKTU I
FUNKCJA	IMIĘ I NAZWISKO	SPECJALNOŚĆ, NR UPRAWNIEN	DATA	PODPIS
Projektant				
Projektant (wsp.)				
Sprawdzający				
Opracował				
TYTUŁ RYSUNKU RZUT PRÓBNY — FRAGMENT PARTERU				
SKALA 1:50	FORMAT A3	DATA 09.2026	NR RYSUNKU DEMO-01	REWIZJA 0

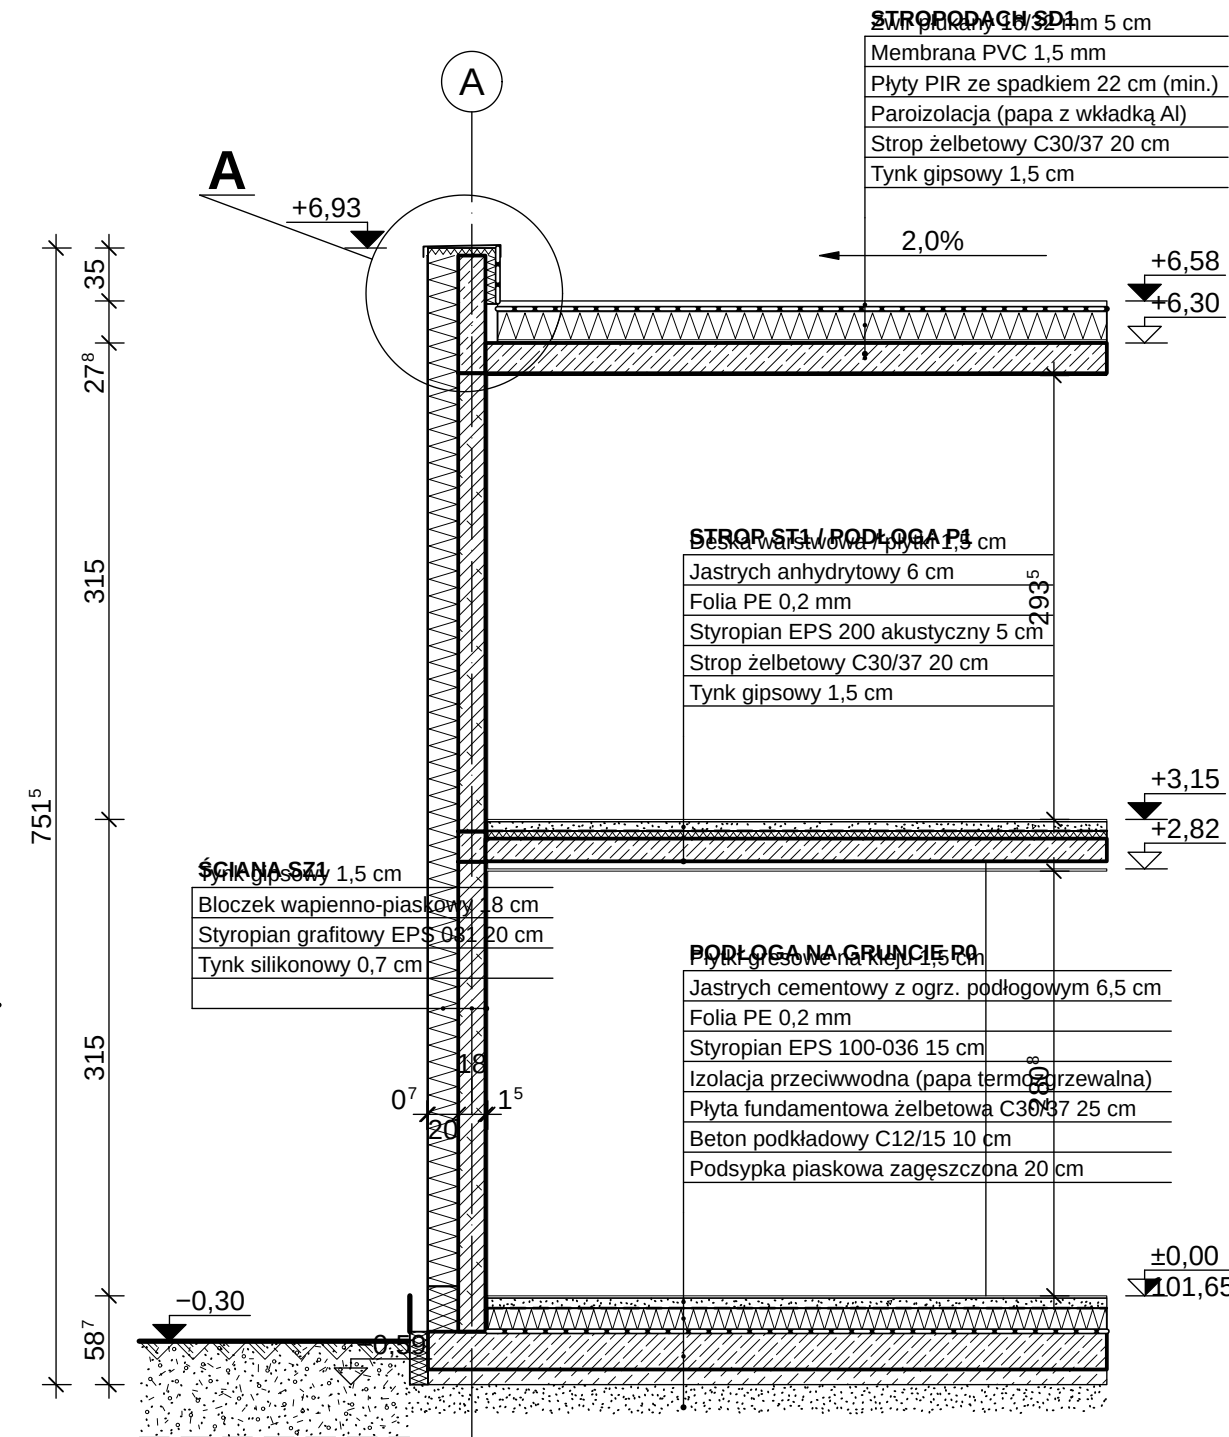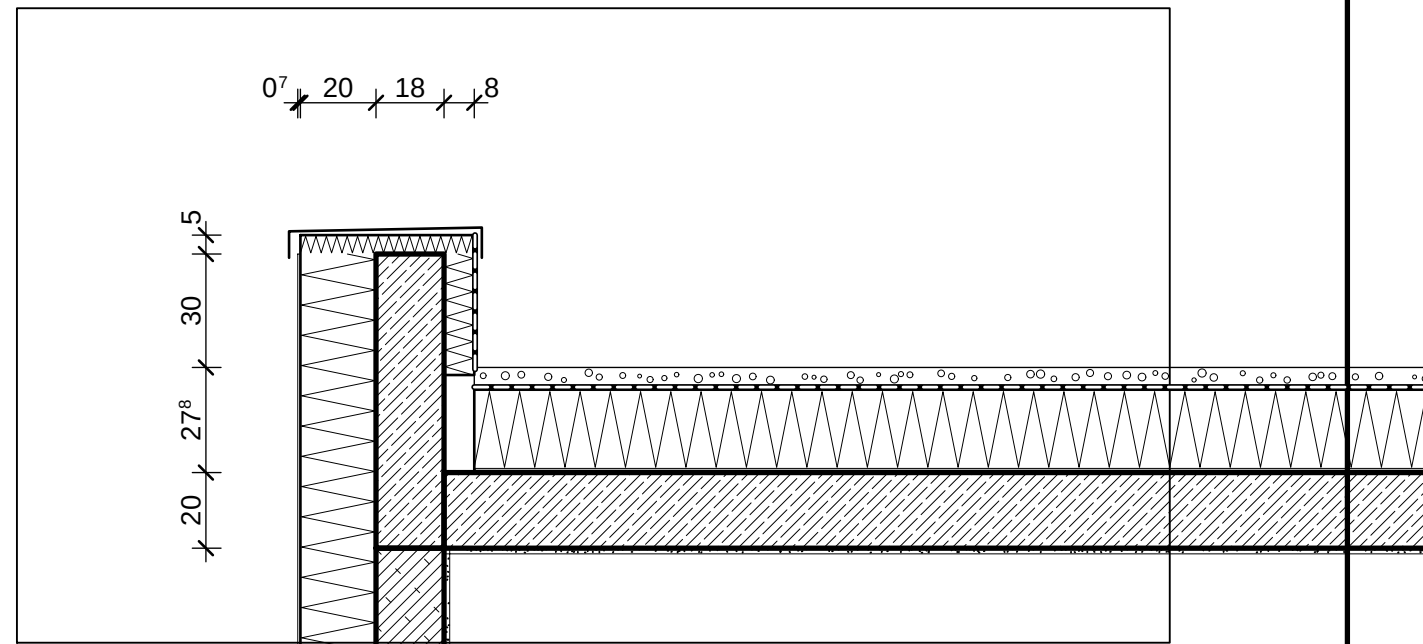**DETAL A — ATTYKA 1:20****UWAGI**

- Rzędne w m względem $\pm 0,00 = 101,65$ m n.p.m.; wymiary w cm.
- Trójkąt zaczerńiony — rzędna wykończenia, niezaczerńiony — rzędna konstrukcji, w połowie zaczerńiony — poziom $\pm 0,00$ z rzędną bezwzględną.
- Rysunek testowy silnika — dane nie stanowią projektu.

1 0
PODZIAŁKA 1:50

1 2 3 0,2 4 0,2 6,4 0,6 0,8 1
PODZIAŁKA 1:20

PRACOWNIA PROJEKTOWA PRACOWNIA PROJEKTOWA — nazwa do uzupełnienia		STADIUM PB		BRANŻA ARCHITEKTURA	
adres pracowni do uzupełnienia					
INWESTOR (do uzupełnienia)					
Budynek mieszkalny jednorodzinny „Dom LAMELA” — PRÓBA SILNIKA RYSUNKOWEGO (rysunek testowy)					
ADRES / LOKALIZACJA (NR DZIAŁKI, OBRĘB, JEDN. EWIDENCYJNA) dz. nr ewid. 123/4, obręb 0005 Przykładowo, jedn. ewid. Przykładowo (dane fikcyjne)					KAT. OBIEKTU I
FUNKCJA	IMIĘ I NAZWISKO	SPECJALNOŚĆ, NR UPRAWNIEN		DATA	PODPIS
Projektant					
Projektant (wsp.)					
Sprawdzający					
Opracował					
TYTUŁ RYSUNKU PRZEKRÓJ PRÓBNY A-A					
SKALA 1:50, 1:20	FORMAT A3	DATA 09.2026	NR RYSUNKU DEMO-02		REWIZJA 0

OZNACZENIA MATERIAŁÓW W PRZEKROJACH (PN-B-01030:2000 + oznaczenia przyjęte)

	Beton zbrojony (żelbet) <i>PN-B-01030:2000 poz. 4</i>		Izolacja termiczna miękka (wełna mineralna) — „wężyk” <i>PN-B-01030:2000 poz. 12</i>		Płyta gipsowo-kartonowa <i>oznaczenie przyjęte (odmiana poz. 2)</i>
	Beton niezbrojony, kamień <i>PN-B-01030:2000 poz. 3</i>		Izolacja termiczna twarda (EPS) — zygzak <i>PN-B-01030:2000 poz. 12</i>		Jastrych (wylewka) cementowy/anhydrytowy <i>oznaczenie przyjęte (zaprawa + kruszywo)</i>
	Beton lekki <i>PN-B-01030:2000 poz. 5</i>		Izolacja termiczna twarda (XPS) — zygzak podwójny <i>oznaczenie przyjęte (odmiana poz. 12)</i>		Płytki ceramiczne / gres (okładzina) <i>oznaczenie przyjęte</i>
	Beton komórkowy (autoklawizowany) <i>PN-B-01030:2000 poz. 5 (beton lekki)</i>		Izolacja termiczna twarda (PIR/PUR) — zygzak z okładzinami <i>oznaczenie przyjęte (odmiana poz. 12)</i>		Grunt rodzimy (powierzchnia gruntu w przekroju) <i>PN-B-01030:2000 poz. 1</i>
	Mur z cegieł i pustaków ceramicznych <i>PN-B-01030:2000 poz. 7</i>		Izolacja przeciwwodna (papa, membrana) — pas czarno-biały <i>PN-B-01030:2000 poz. 13</i>		Nasyp, zasypka (grunt nasypowy) <i>oznaczenie przyjęte</i>
	Mur z bloczków wapienno-piaskowych (silikatowych) <i>oznaczenie przyjęte (odmiana poz. 7 PN-B-01030)</i>		Izolacja przeciwwilgociowa — linia pogrubiona praktyka (PN-B-01025:2004)		Piasek, podsypka piaskowa <i>PN-B-01030:2000 poz. 2 (podsypka)</i>
	Drewno — przekrój prostopadły do włókien <i>PN-B-01030:2000 poz. 8a</i>		Paroizolacja (folia PE) — linia kreskowa <i>oznaczenie przyjęte</i>		Żwir, tłuczeń <i>oznaczenie przyjęte</i>
	Drewno — przekrój wzdłuż włókien <i>PN-B-01030:2000 poz. 8b</i>		Membrana paroprzepuszczalna / wiatroizolacja <i>oznaczenie przyjęte</i>		Pospółka (mieszanka piaskowo-żwirowa) <i>oznaczenie przyjęte</i>
	Sklejka <i>PN-B-01030:2000 poz. 9</i>		Szkoło i inne materiały przezroczyste <i>PN-B-01030:2000 poz. 14</i>		Ziemia urodzajna (humus) <i>oznaczenie przyjęte</i>
	Płyty drewnopochodne (OSB, MFP, wiórowe) <i>PN-B-01030:2000 poz. 10</i>		Tworzywa sztuczne <i>PN-B-01030:2000 poz. 15</i>		
	Metale (stal, aluminium) — zaczerwienie <i>PN-B-01030:2000 poz. 11</i>		Tynk, zaprawa <i>PN-B-01030:2000 poz. 2</i>		

SYMBOLE GRAFICZNE (PN-B-01025, PN-EN 60617, PN-EN ISO 10628, PN-EN ISO 11091)

Strzałka północy 	Oś konstrukcyjna 	Oznaczenie przekroju 	Oznaczenie pomieszczenia 	Symbol stolarki 	Rzędna — rzut (X / ramka) 	Rzędne — przekrój 	Spadek / pochylnia 	Wejście do budynku
Odnośnik szczegółu 	Wymiar (cm, mm w indeksie) 	Otwór w stropie 	Gniazdo 1f / 2× / IP44 / 3f 	Łącznik 1-bieg. / 2-bieg. / schodowy 	Oprawa sufit. / ścienna / LED 	Rozdzielnica / puszka / uziemienie 	Czujnik ruchu / dzwonek / wideodomofon 	Gniazdo RJ45 / TV / SPD
Pion / zawór / zawór zwrotny 	Wodomierz / filtr / pompa 	Rury: W / C / Cy / K 	Rozdzielacz / zasobnik / pompa ciepła 	Czyszczak / wpust / rewizja 	Kratka / anemostat N / W 	Czerpnia / wyrzutnia 	Rekuperator 	Grzejnik / ogrzewanie podłogowe
Drzewo istn. / proj. / do wycinki 	Drzewo iglaste / krzew / żywopłot 	Trawnik / kostka 	Słup / hydrant / studzienka 	Złącze ZK / skrzynka 	Granica działki z punktami 	Linia zabudowy 	Warstwiec / pkt wysokościowe 	Brama przesuwna / furtka

odcinek kontrolny 100 mm (wydruk 1:1)

PRACOWNIA PROJEKTOWA PRACOWNIA PROJEKTOWA — nazwa do uzupełnienia adres pracowni do uzupełnienia			STADIUM PB	BRANŻA WIELOBRANŻOWY
INWESTOR (do uzupełnienia)				
Budynek mieszkalny jednorodzinny „Dom LAMELA” — PRÓBA SILNIKA RYSUNKOWEGO (rysunek testowy)				
ADRES / LOKALIZACJA (NR DZIAŁKI, OBRĘB, JEDN. EWIDENCYJNA) dz. nr ewid. 123/4, obręb 0005 Przykładowo, jedn. ewid. Przykładowo (dane fikcyjne)				KAT. OBIEKTU I
FUNKCJA	IMIĘ I NAZWISKO	SPECJALNOŚĆ, NR UPRAWNIEŃ	DATA	PODPIS
Projektant				
Projektant (wsp.)				
Sprawdzający				
Opracował				
TYTUŁ RYSUNKU TABLICA OZNACZEŃ: MATERIAŁY I SYMBOLE				
SKALA —	FORMAT A2	DATA 09.2026	NR RYSUNKU DEMO-03	REWIZJA 0