


# TOM PRÓBNY — SILNIK RYSUNKOWY

| Lp. | Nr rys. | Tytuł rysunku                         | Skala      | Format |
|-----|---------|---------------------------------------|------------|--------|
| 1   | DEMO-01 | RZUT PRÓBNY — FRAGMENT PARTERU        | 1:50       | A3     |
| 2   | DEMO-02 | PRZEKRÓJ PRÓBNY A-A                   | 1:50, 1:20 | A3     |
| 3   | DEMO-03 | TABLICA OZNACZEŃ: MATERIAŁY I SYMBOLE | —          | A2     |

|                                                            |                 |                           |            |              |
|------------------------------------------------------------|-----------------|---------------------------|------------|--------------|
| PRACOWNIA PROJEKTOWA                                       |                 | STADIUM                   | BRANŻA     |              |
| INWESTOR                                                   |                 |                           |            |              |
| OBIEKT / NAZWA ZAMIERZENIA BUDOWLANEGO                     |                 |                           |            |              |
| ADRES / LOKALIZACJA (NR DZIAŁKI, OBRĘB, JEDN. EWIDENCYJNA) |                 |                           |            | KAT. OBIEKTU |
| FUNKCJA                                                    | IMIĘ I NAZWISKO | SPECJALNOŚĆ, NR UPRAWNIEŃ | DATA       | PODPIS       |
| Projektant                                                 |                 |                           |            |              |
| Projektant (wsp.)                                          |                 |                           |            |              |
| Sprawdzający                                               |                 |                           |            |              |
| Opracował                                                  |                 |                           |            |              |
| TYTUŁ RYSUNKU                                              |                 |                           |            |              |
| SPIS RYSUNKÓW                                              |                 |                           |            |              |
| SKALA                                                      | FORMAT          | DATA                      | NR RYSUNKU | REWIZJA      |
| —                                                          | A4              |                           | 00         |              |

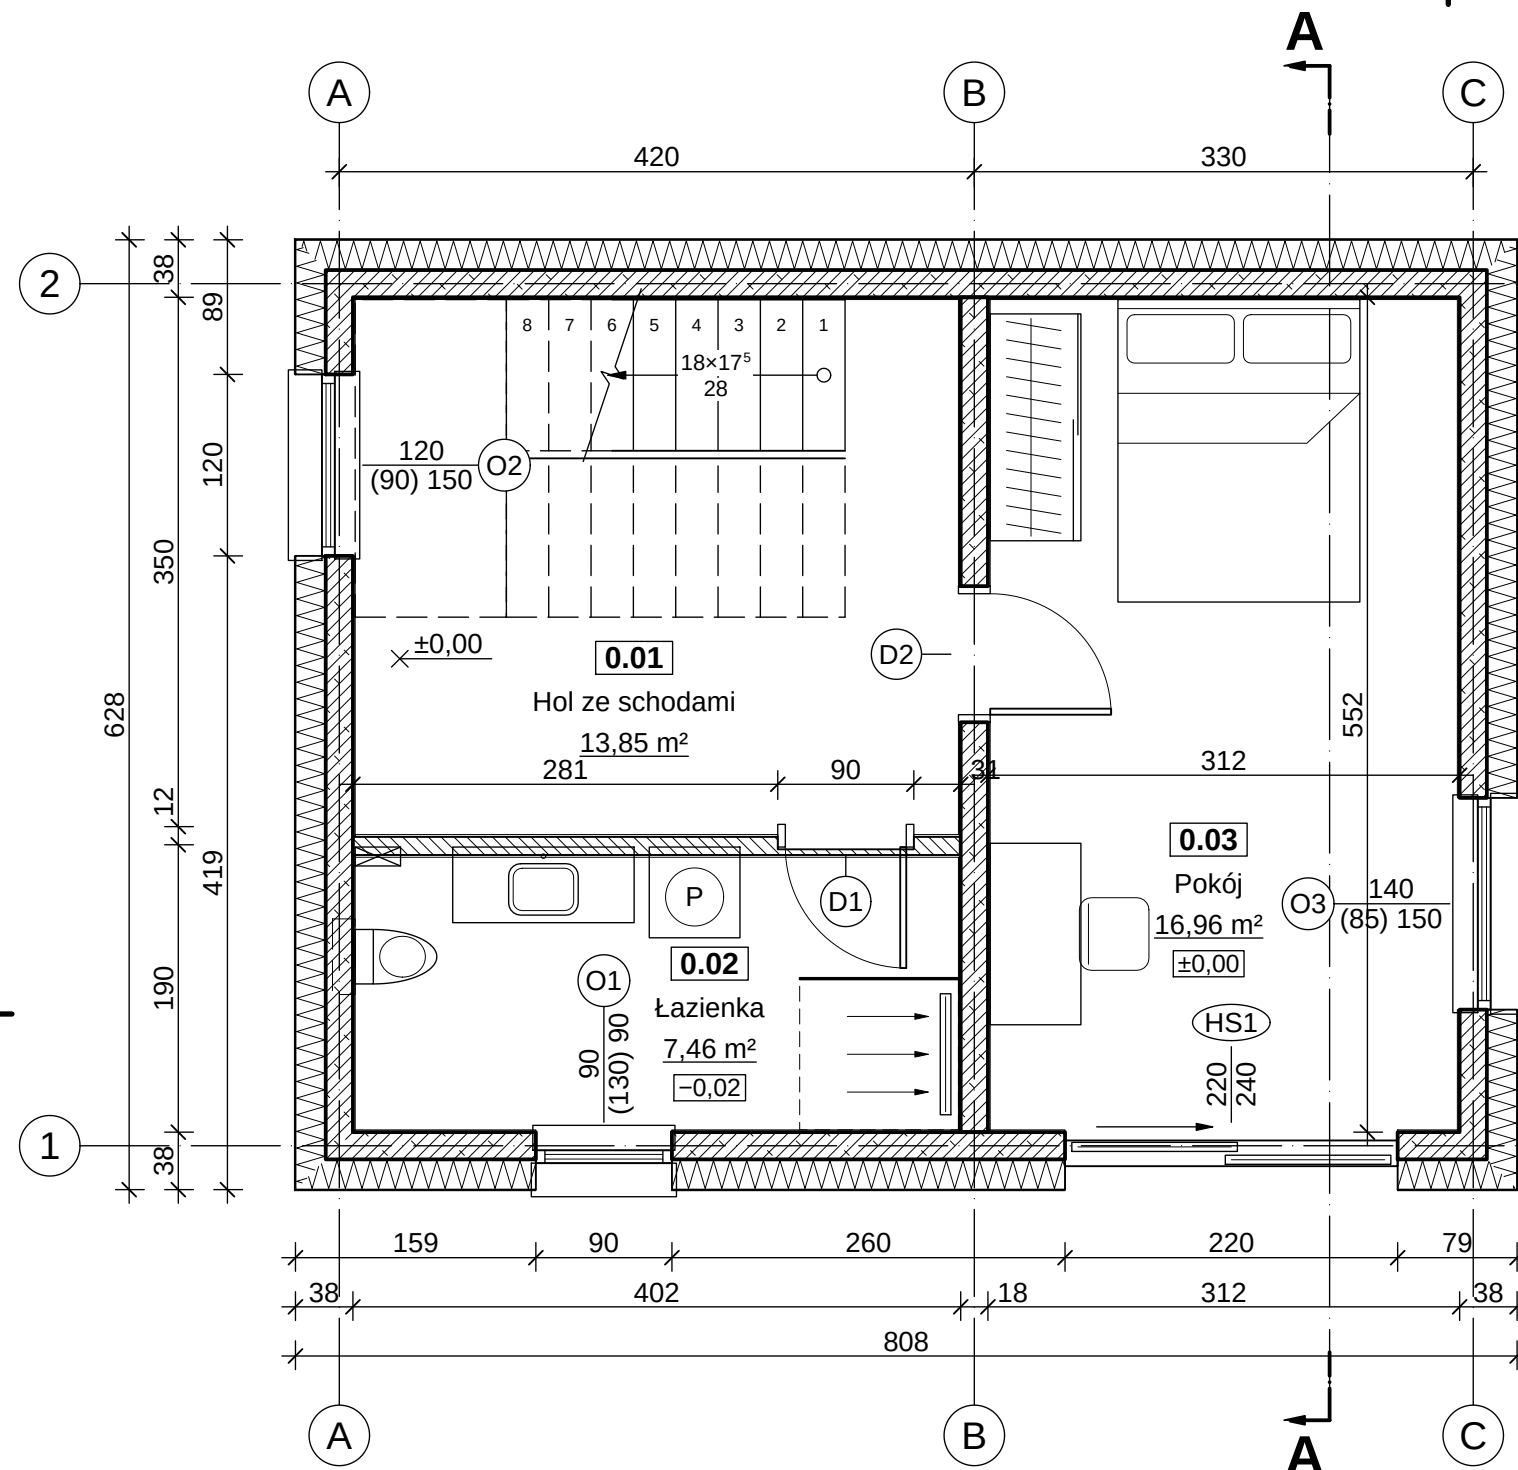

RZUT PARTERU — FRAGMENT 1:50

## ZESTAWIENIE POMIESZCZEŃ

| Nr    | Nazwa pomieszczenia | Posadzka | Pow. [m²] |
|-------|---------------------|----------|-----------|
| 0.01  | Hol ze schodami     | gres     | 13,85     |
| 0.02  | Łazienka            | gres     | 7,46      |
| 0.03  | Pokój               | deska    | 16,96     |
| RAZEM |                     |          | 38,27     |

## ZESTAWIENIE OTWORÓW (w świetle muru)


| Symbol | Szer. [cm] | Wys. [cm] | Parapet [cm] |
|--------|------------|-----------|--------------|
| O1     | 90         | 90        | 130          |
| HS1    | 220        | 240       | 0            |
| O2     | 120        | 150       | 90           |
| O3     | 140        | 150       | 85           |
| D1     | 90         | 205       | —            |
| D2     | 90         | 205       | —            |

## OZNACZENIA MATERIAŁÓW



|  |                                                   |  |                                          |
|--|---------------------------------------------------|--|------------------------------------------|
|  | Mur z bloczków wapienno-piaskowych (silikatowych) |  | Izolacja termiczna twarda (EPS) — zygzak |
|  | Mur z cegieł i pustaków ceramicznych              |  | Tynk, zaprawa                            |

## UWAGI


- Wymiary w cm (mm w indeksie górnym), rzędne w m. Rzędna  $\pm 0,00$  = posadzka parteru = 101,65 m n.p.m.
- Wymiary otworów w świetle muru: licznik — szerokość, mianownik — wysokość, w nawiasie wysokość parapetu.
- Rysunek testowy silnika — dane nie stanowią projektu.

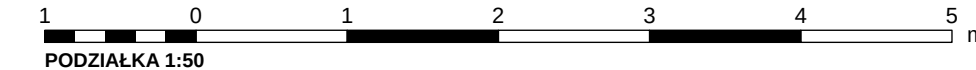

|   |                                            |                            |                               |                          |
|---|--------------------------------------------|----------------------------|-------------------------------|--------------------------|
| REW.   | OPIS ZMIANY                                |                            | DATA                          |                          |
| 0   | Wydanie do weryfikacji silnika rysunkowego |                            | 2026-09-25                    |                          |
| PRACOWNIA PROJEKTOWA<br><b>PRACOWNIA PROJEKTOWA — nazwa do uzupełnienia</b><br>adres pracowni do uzupełnienia                                     |                                            | STADIUM<br><b>PB</b>       | BRANŻA<br><b>ARCHITEKTURA</b> |                          |
| INWESTOR<br>(do uzupełnienia)   |                                            |                            |                               |                          |
| OBIEKT / NAZWA ZAMIERZENIA BUDOWLANEGO<br><b>Budynek mieszkalny jednorodzinny „Dom LAMELA” — PRÓBA SILNIKA RYSUNKOWEGO (rysunek testowy)</b>      |                                            |                            |                               |                          |
| ADRES / LOKALIZACJA (NR DZIAŁKI, OBRĘB, JEDN. EWIDENCYJNA)<br>dz. nr ewid. 123/4, obręb 0005 Przykładowo, jedn. ewid. Przykładowo (dane fikcyjne) |                                            |                            |                               | KAT. OBIEKTU<br><b>I</b> |
| FUNKCJA   | IMIĘ I NAZWISKO                            | SPECJALNOŚĆ, NR UPRAWNIENI | DATA                          | PODPIS                   |
| Projektant   |                                            |                            |                               |                          |
| Projektant (wsp.)   |                                            |                            |                               |                          |
| Sprawdzający   |                                            |                            |                               |                          |
| Opracował   |                                            |                            |                               |                          |
| TYTUŁ RYSUNKU<br><b>RZUT PRÓBNY — FRAGMENT PARTERU</b>                                                                                            |                                            |                            |                               |                          |
| SKALA<br><b>1:50</b>   | FORMAT<br><b>A3</b>                        | DATA<br>09.2026            | NR RYSUNKU<br><b>DEMO-01</b>  | REWIZJA<br><b>0</b>      |

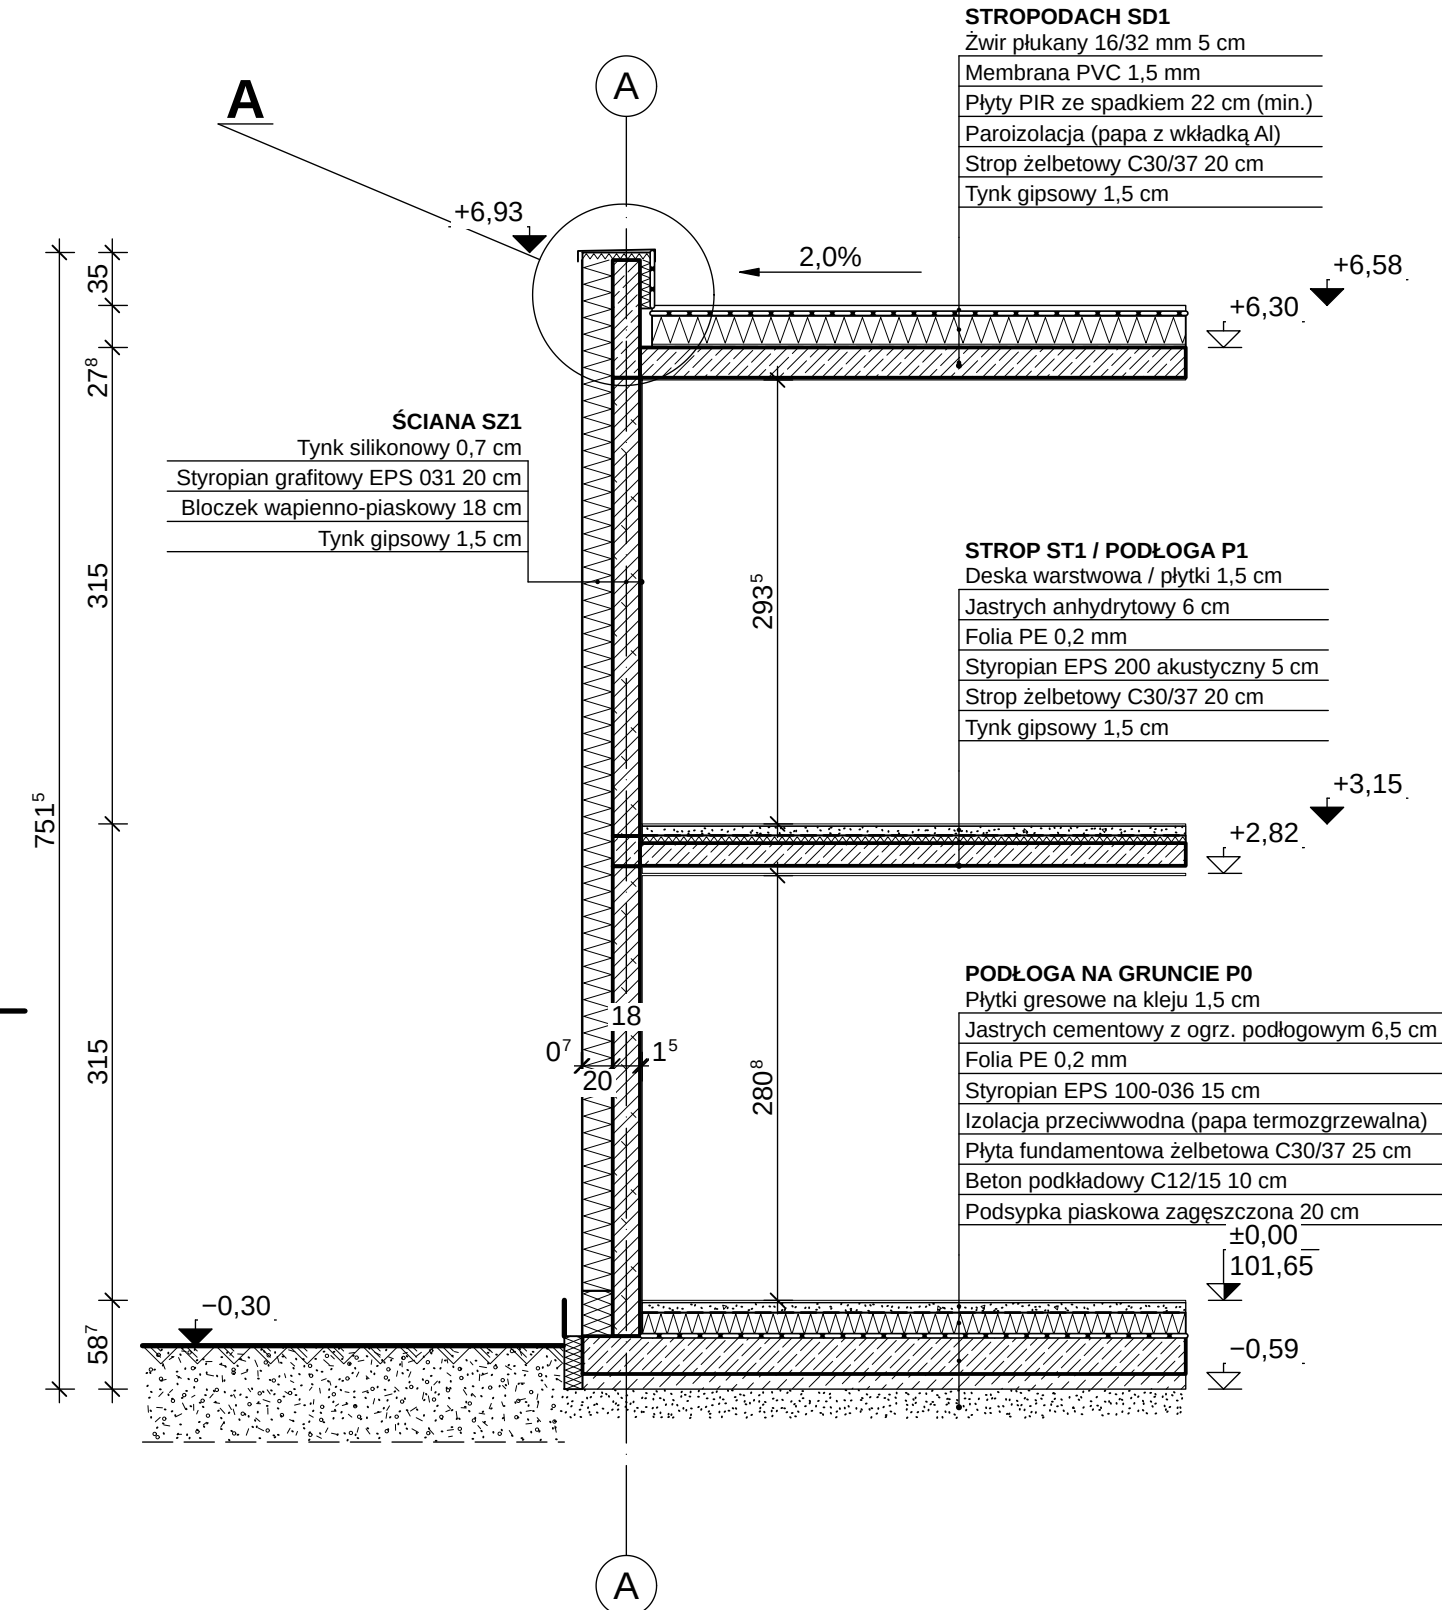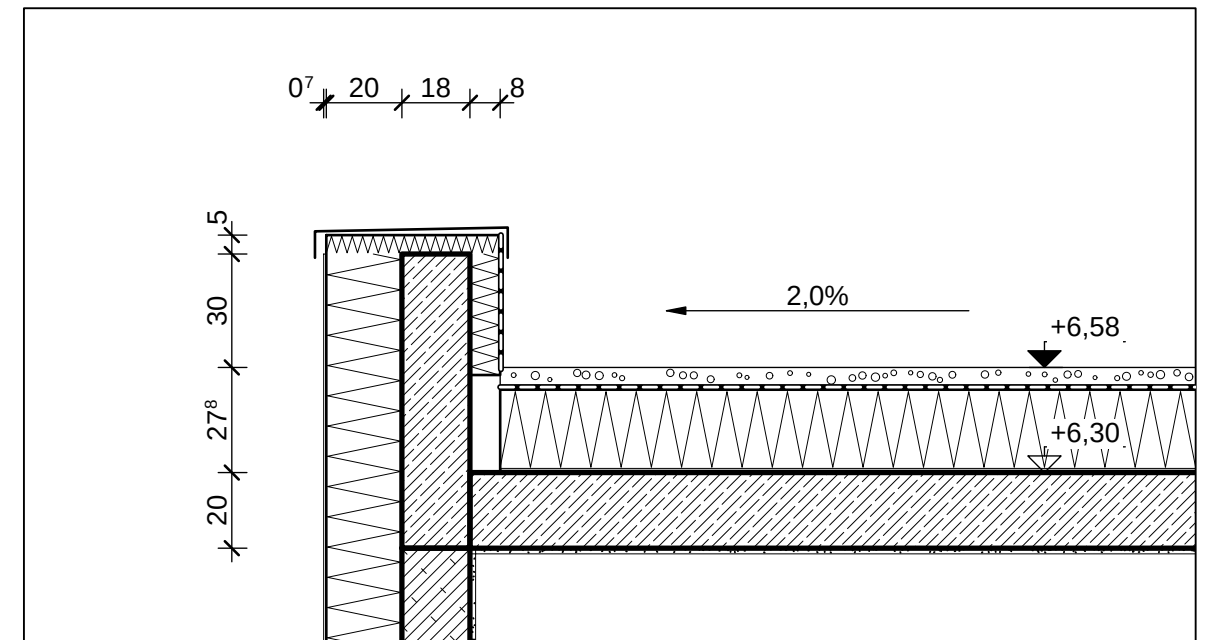**DETAL A — ATTYKA 1:20****UWAGI**

- Rzędne w m względem ±0,00 = 101,65 m n.p.m.; wymiary w cm.
- Trójkąt zaczerpiony — rzędna wykończenia, niezaczerpiony — rzędna konstrukcji, w połowie zaczerpiony — poziom ±0,00 z rzędną bezwzględną.
- Rysunek testowy silnika — dane nie stanowią projektu.

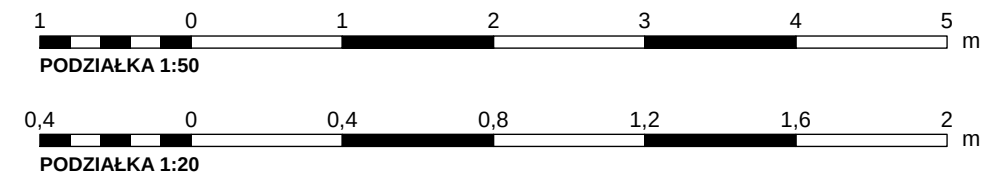

|   |                 |                           |                              |                          |
|---|-----------------|---------------------------|------------------------------|--------------------------|
| PRACOWNIA PROJEKTOWA<br><b>PRACOWNIA PROJEKTOWA — nazwa do uzupełnienia</b><br>adres pracowni do uzupełnienia                                     |                 |                           | STADIUM<br><b>PB</b>         | BRANŻA<br>ARCHITEKTURA   |
| INWESTOR<br>(do uzupełnienia)   |                 |                           |                              |                          |
| OBIEKT / NAZWA ZAMIERZENIA BUDOWLANEGO<br><b>Budynek mieszkalny jednorodzinny „Dom LAMELA” — PRÓBA SILNIKA RYSUNKOWEGO (rysunek testowy)</b>      |                 |                           |                              |                          |
| ADRES / LOKALIZACJA (NR DZIAŁKI, OBRĘB, JEDN. EWIDENCYJNA)<br>dz. nr ewid. 123/4, obręb 0005 Przykładowo, jedn. ewid. Przykładowo (dane fikcyjne) |                 |                           |                              | KAT. OBIEKTU<br><b>I</b> |
| FUNKCJA   | IMIĘ I NAZWISKO | SPECJALNOŚĆ, NR UPRAWNIEN | DATA                         | PODPIS                   |
| Projektant   |                 |                           |                              |                          |
| Projektant (wsp.)   |                 |                           |                              |                          |
| Sprawdzający   |                 |                           |                              |                          |
| Opracował   |                 |                           |                              |                          |
| TYTUŁ RYSUNKU<br><b>PRZEKRÓJ PRÓBNY A-A</b>   |                 |                           |                              |                          |
| SKALA<br><b>1:50, 1:20</b>   | FORMAT<br>A3    | DATA<br>09.2026           | NR RYSUNKU<br><b>DEMO-02</b> | REWIZJA<br><b>0</b>      |

OZNACZENIA MATERIAŁÓW W PRZEKROJACH (PN-B-01030:2000 + oznaczenia przyjęte)

|  |   |  |   |  |                                                                                             |
|--|---|--|---|--|---------------------------------------------------------------------------------------------|
|  | Beton zbrojony (żelbet)<br><i>PN-B-01030:2000 poz. 4</i>                                                    |  | Izolacja termiczna miękka (wełna mineralna) — „wężyk”<br><i>PN-B-01030:2000 poz. 12</i>                    |  | Płyta gipsowo-kartonowa<br><i>oznaczenie przyjęte (odmiana poz. 2)</i>                      |
|  | Beton niezbrojony, kamień<br><i>PN-B-01030:2000 poz. 3</i>                                                  |  | Izolacja termiczna twarda (EPS) — zygzak<br><i>PN-B-01030:2000 poz. 12</i>                                 |  | Jastrych (wylewka) cementowy/anhydrytowy<br><i>oznaczenie przyjęte (zaprawa + kruszywo)</i> |
|  | Beton lekki<br><i>PN-B-01030:2000 poz. 5</i>                                                                |  | Izolacja termiczna twarda (XPS) — zygzak podwójny<br><i>oznaczenie przyjęte (odmiana poz. 12)</i>          |  | Płytki ceramiczne / gres (okładzina)<br><i>oznaczenie przyjęte</i>                          |
|  | Beton komórkowy (autoklawizowany)<br><i>PN-B-01030:2000 poz. 5 (beton lekki)</i>                            |  | Izolacja termiczna twarda (PIR/PUR) — zygzak z okładzinami<br><i>oznaczenie przyjęte (odmiana poz. 12)</i> |  | Grunt rodzimy (powierzchnia gruntu w przekroju)<br><i>PN-B-01030:2000 poz. 1</i>            |
|  | Mur z cegieł i pustaków ceramicznych<br><i>PN-B-01030:2000 poz. 7</i>                                       |  | Izolacja przeciwwodna (papa, membrana) — pas czarno-biały<br><i>PN-B-01030:2000 poz. 13</i>                |  | Nasyp, zasypka (grunt nasypowy)<br><i>oznaczenie przyjęte</i>                               |
|  | Mur z bloczków wapienno-piaskowych (silikatowych)<br><i>oznaczenie przyjęte (odmiana poz. 7 PN-B-01030)</i> |  | Izolacja przeciwwilgociowa — linia pogrubiona praktyka (PN-B-01025:2004)                                   |  | Piasek, podsypka piaskowa<br><i>PN-B-01030:2000 poz. 2 (podsypka)</i>                       |
|  | Drewno — przekrój prostopadły do włókien<br><i>PN-B-01030:2000 poz. 8a</i>                                  |  | Paroizolacja (folia PE) — linia kreskowa<br><i>oznaczenie przyjęte</i>                                     |  | Żwir, tłuczeń<br><i>oznaczenie przyjęte</i>                                                 |
|  | Drewno — przekrój wzdłuż włókien<br><i>PN-B-01030:2000 poz. 8b</i>                                          |  | Membrana paroprzepuszczalna / wiatroizolacja<br><i>oznaczenie przyjęte</i>                                 |  | Pospółka (mieszanka piaskowo-żwirowa)<br><i>oznaczenie przyjęte</i>                         |
|  | Sklejka<br><i>PN-B-01030:2000 poz. 9</i>                                                                    |  | Szkoło i inne materiały przezroczyste<br><i>PN-B-01030:2000 poz. 14</i>                                    |  | Ziemia urodzajna (humus)<br><i>oznaczenie przyjęte</i>                                      |
|  | Płyty drewnopochodne (OSB, MFP, wiórowe)<br><i>PN-B-01030:2000 poz. 10</i>                                  |  | Tworzywa sztuczne<br><i>PN-B-01030:2000 poz. 15</i>                                                        |  |                                                                                             |
|  | Metale (stal, aluminium) — zaczerpnienie<br><i>PN-B-01030:2000 poz. 11</i>                                  |  | Tynk, zaprawa<br><i>PN-B-01030:2000 poz. 2</i>                                                             |  |                                                                                             |

SYMBOLE GRAFICZNE (PN-B-01025, PN-EN 60617, PN-EN ISO 10628, PN-EN ISO 11091)

|                                          |                                           |                                                 |                                        |                                            |                               |                                                |                                       |
|------------------------------------------|-------------------------------------------|-------------------------------------------------|----------------------------------------|--------------------------------------------|-------------------------------|------------------------------------------------|---------------------------------------|
| Strzałka północy<br>                     | Oś konstrukcyjna<br>                      | Oznaczenie przekroju<br>                        | Oznaczenie pomieszczenia<br>           | Symbol stolarki<br>                        | Rzędna — rzut (X / ramka)<br> | Rzędne — przekrój (±0,00 / wyk. / konstr.)<br> | Spadek / pochylnia<br>                |
| Wejście do budynku (±0,00 / poniżej)<br> | Odnośnik szczegółu<br>                    | Wymiar (cm, mm w indeksie)<br>                  | Otwór w stropie / szacht<br>           | Drzwi rozwierane<br>                       | Drzwi przesuwne HS<br>        | Okno (rama, szyba, parapety)<br>               | Schody — bieg z linią cięcia<br>      |
| Gniazdo 1f / 2× / IP44 / 3f<br>          | Łącznik 1-bieg. / 2-bieg. / schodowy<br>  | Oprawa ogólna / kinkiet / ścienna / liniowa<br> | Rozdzielnica / puszka / uziemienie<br> | Czujnik ruchu / dzwonek / wideodomofon<br> | Gniazdo RJ45 / TV / SPD<br>   | Pion / zawór / zawór zwrotny<br>               | Wodomierz / filtr / pompa<br>         |
| Rury: W / C / Cy / K<br>                 | Rozdzielacz / zasobnik / pompa ciepła<br> | Czyszczak / wpust / rewizja<br>                 | Kratka / anemostat N / W<br>           | Czerpnia / wyrzutnia<br>                   | Rekuperator<br>               | Grzejnik / ogrzewanie podłogowe<br>            | Drzewo istn. / proj. / do wycinki<br> |
| Drzewo iglaste / krzew / żywopłot<br>    | Trawnik / kostka / deska<br>              | Słup en. / oświetl. / hydrant / studzienka<br>  | Złącze ZK / skrzynka<br>               | Granica działki, punkty graniczne<br>      | Linia zabudowy<br>            | Warstwie / pkt wysokościowe<br>                | Brama przesuwna / furtka<br>          |

RODZAJE I GRUBOŚCI LINII (PN-EN ISO 128-2, grupy linii wg podziałki)

| Próbka | Rodzaj linii            | Zastosowanie                                                                | 1:20 | 1:50 | 1:100 | 1:500 |
|--------|-------------------------|-----------------------------------------------------------------------------|------|------|-------|-------|
|        | ciągła bardzo gruba     | kontury przekroju bez kreskowania, pręty zbrojeniowe, izolacje przeciwwodne | 1,00 | 0,70 | 0,70  | 0,50  |
|        | ciągła gruba            | kontury elementów konstrukcyjnych w przekroju (z kreskowaniem)              | 0,70 | 0,50 | 0,35  | 0,35  |
|        | ciągła średnia          | warstwy nienośne w przekroju, stolarka, krawędzie widoczne bliskie          | 0,35 | 0,25 | 0,25  | 0,18  |
|        | ciągła cienka           | wymiary, linie pomocnicze, odnośniki, wyposażenie, krawędzie widoczne       | 0,18 | 0,18 | 0,18  | 0,13  |
|        | ciągła bardzo cienka    | kreskowanie materiałów, meble                                               | 0,13 | 0,13 | 0,13  | 0,13  |
|        | kreskowa cienka         | krawędzie niewidoczne, elementy nad płaszczyzną cięcia                      | 0,18 | 0,18 | 0,18  | 0,13  |
|        | punktowa cienka         | osie konstrukcyjne, osie symetrii                                           | 0,18 | 0,18 | 0,18  | 0,13  |
|        | punktowa gruba (krótka) | ślad płaszczyzny przekroju (końce i załamania)                              | 0,70 | 0,50 | 0,35  | 0,35  |
|        | dwupunktowa             | granice działki, elementy usuwane/projektowane, skrajne położenia           | 0,70 | 0,50 | 0,35  | 0,35  |
|        | kropkowa                | elementy pomocnicze, zakres robót                                           | 0,18 | 0,18 | 0,18  | 0,13  |

PISMO (PN-EN ISO 3098; Liberation Sans — metrycznie zgodna z Arial)

h = 1,8 mm    ĄĘŁŃÓŚŹŹ ąęęńńśŹŹ 0123456789 ±0,00 –1,20 24<sup>5</sup>  
h = 2,5 mm    ĄĘŁŃÓŚŹŹ ąęęńńśŹŹ 0123456789 ±0,00 –1,20 24<sup>5</sup>  
h = 3,5 mm    ĄĘŁŃÓŚŹŹ ąęęńńśŹŹ 0123456789 ±0,00 –1,20 24<sup>5</sup>  
h = 5,0 mm    ĄĘŁŃÓŚŹŹ ąęęńńśŹŹ 0123456789 ±0,00 –1,20 24<sup>5</sup>

odcinek kontrolny 100 mm (wydruk 1:1)

|   |                     |                           |                              |                                |                          |
|---|---------------------|---------------------------|------------------------------|--------------------------------|--------------------------|
| PRACOWNIA PROJEKTOWA<br><b>PRACOWNIA PROJEKTOWA</b> — nazwa do uzupełnienia                                                                       |                     | STADIUM<br><b>PB</b>      |                              | BRANŻA<br><b>WIELOBRANŻOWY</b> |                          |
| adres pracowni do uzupełnienia   |                     |                           |                              |                                |                          |
| INWESTOR<br>(do uzupełnienia)   |                     |                           |                              |                                |                          |
| OBIEKT / NAZWA ZAMIERZENIA BUDOWLANEGO<br><b>Budynek mieszkalny jednorodzinny „Dom LAMELA” — PRÓBA SILNIKA RYSUNKOWEGO (rysunek testowy)</b>      |                     |                           |                              |                                |                          |
| ADRES / LOKALIZACJA (NR DZIAŁKI, OBRĘB, JEDN. EWIDENCYJNA)<br>dz. nr ewid. 123/4, obręb 0005 Przykładowo, jedn. ewid. Przykładowo (dane fikcyjne) |                     |                           |                              |                                | KAT. OBIEKTU<br><b>I</b> |
| FUNKCJA   | IMIĘ I NAZWISKO     | SPECJALNOŚĆ, NR UPRAWNIEŃ | DATA                         | PODPIS                         |                          |
| Projektant   |                     |                           |                              |                                |                          |
| Projektant (wsp.)   |                     |                           |                              |                                |                          |
| Sprawdzający   |                     |                           |                              |                                |                          |
| Opracował   |                     |                           |                              |                                |                          |
| TYTUŁ RYSUNKU<br><b>TABLICA OZNACZEŃ: MATERIAŁY I SYMBOLE</b>                                                                                     |                     |                           |                              |                                |                          |
| SKALA<br>—   | FORMAT<br><b>A2</b> | DATA<br>09.2026           | NR RYSUNKU<br><b>DEMO-03</b> | REWIZJA<br><b>0</b>            |                          |