


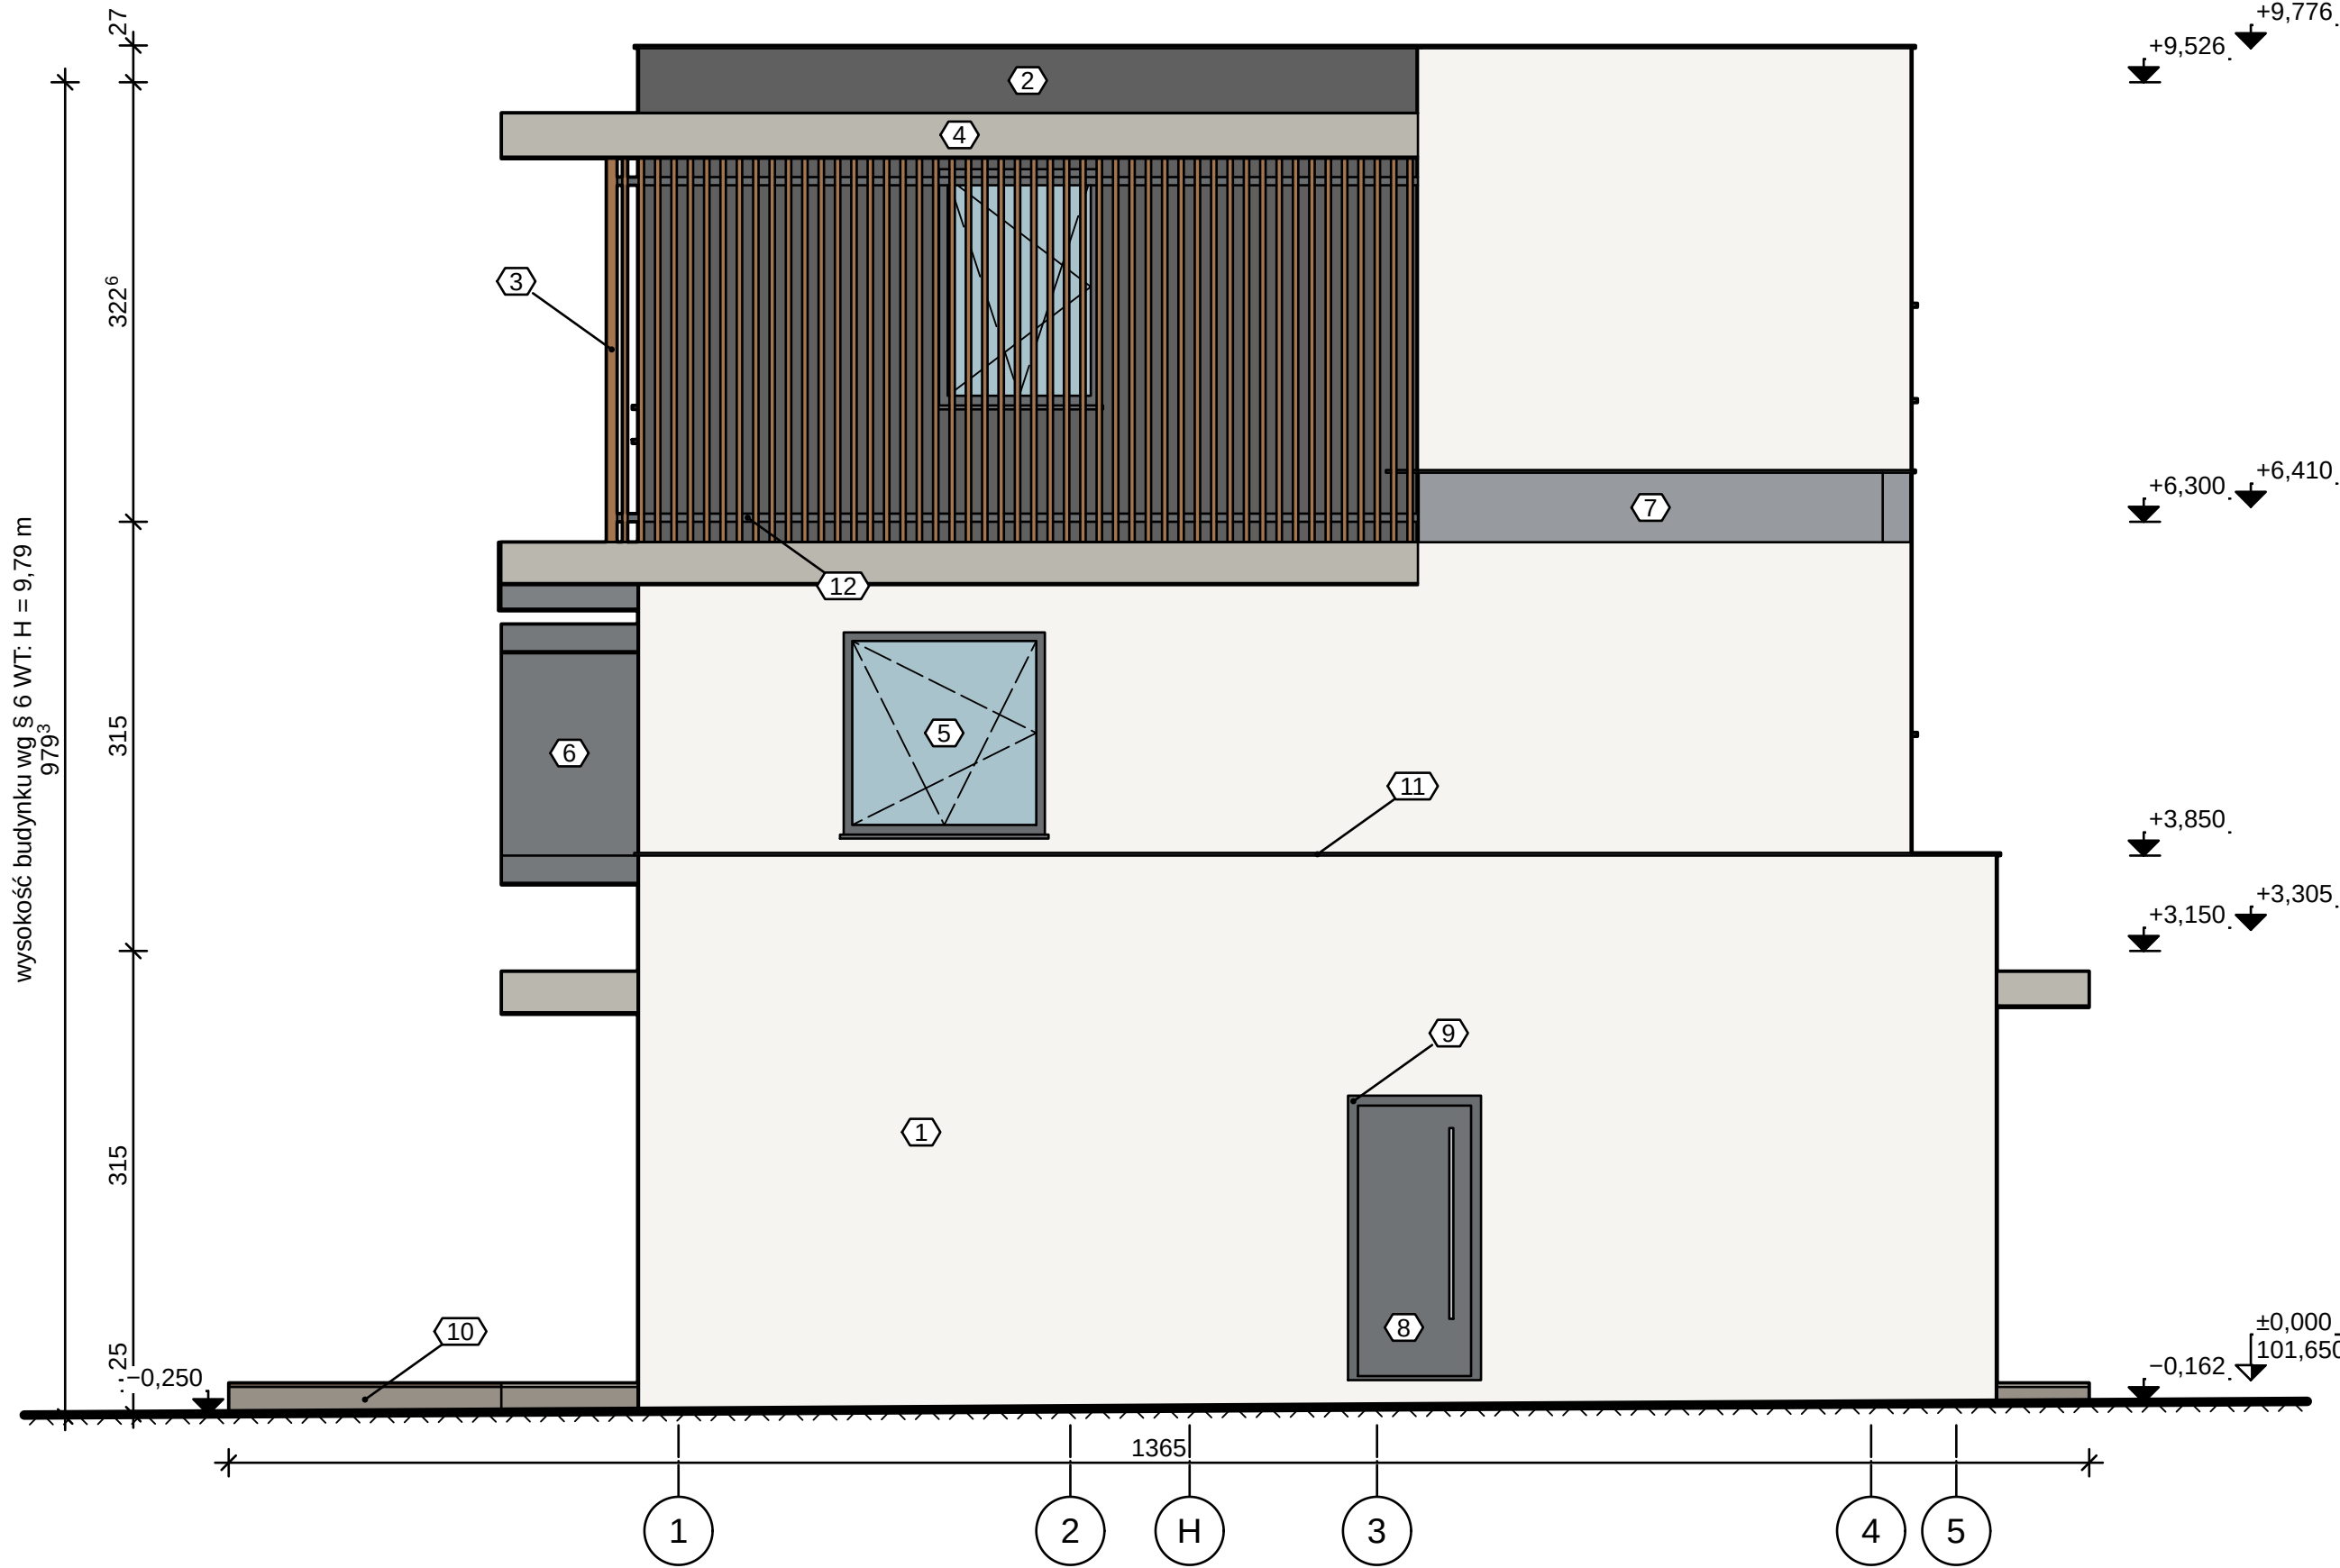


ELEWACJA WSCHODNIA 1:50

KOLORYSTYKA I MATERIAŁY ELEWACJI

1	ETICS: warstwa zbrojona + tynk silikonowy 1,5 mm (biały / jasnoszary NCS S 1500-N) [TYNK_SIL]	#f5f4f0
2	Membrana fasadowa wiatroizolacyjna UV-stabilna, czarna (sd ≈ 0,02 m) [MEMB_WIATR]	#1d1d1d
3	Lamele elewacyjne 40×80 mm, drewno termojesion (klasa 1 trwałości), olejowane [DREWNO_TERMO]	#9b6b41
4	Żelbet C30/37 XC4/XF1 (krawędzie płyt wysuniętych, atyki, belki) [ZB_C30]	#b4b1a9
5	Szkoło (szyby zespolone) [SZKLO]	#a9c3cd
6	Rama boku C: ruszt stalowy ocynkowany w okładzinie z blachy aluminiowej RAL 7016 (pusta w środku) [RAMA_C]	#3b4044
7	Styropian grafitowy EPS 031 (ETICS, NRO w systemie) [EPS031]	#8f9296
8	Drzwi zewnętrzne, płycina aluminiowa [DRZWI_ZEWN]	#34383c
9	Stołarka — profile aluminiowe, antracyt [RAMA_ALU]	#2b2f33
10	Podbudowa nawierzchni (kruszywo) [NAW_PODBUDOWA]	#8d877d
11	Obróbki blacharskie (blacha powlekana) [OBROBKA_BLACH]	#3b3f43
12	Stal malowana proszkowo (balustrady, rygle) [STAL_BAL]	#2c3034

OBJAŚNIENIA I UWAGI

- Wymiary w cm (mm w indeksie górnym, np. 24⁵ = 24,5 cm), rzędne w m względem ±0,000 = 101,650 m n.p.m. (PL-EVRF2007-NH).
- Rzędne: trójkąt zaczerpiony — poziom wykończenia, niezaczerpiony — konstrukcji, w połowie zaczerpiony — poziom ±0,000 z rzędną bezwzględną (PN-B-01025).
- Wysokość budynku wg § 6 WT: od terenu przy najniższym położonym wejściu (−0,267) do wierzchu stropodachu D1 (+9,526) — H = 9,79 m (bez atyki).
- Kolorystyka orientacyjna wg kolorów materiałów w modelu (do potwierdzenia wzornikiem RAL/NCS).
- Rysunek wygenerowany automatycznie z modelu /home/user/aihouse/model/budynek.yaml (wersja 1.0, 2026-09-25) — generatory lamela.views.

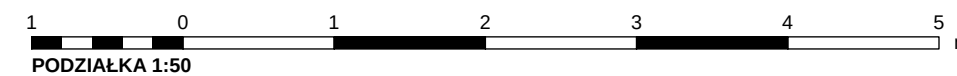

REW.	OPIS ZMIANY			DATA	
0	Wydanie — rysunek wygenerowany z modelu			2026-09-25	
PRACOWNIA PROJEKTOWA PRACOWNIA PROJEKTOWA — nazwa do uzupełnienia adres pracowni do uzupełnienia			STADIUM PB	BRANŻA ARCHITEKTURA (AR)	
INWESTOR (do uzupełnienia)					
OBIEKT / NAZWA ZAMIERZENIA BUDOWLANEGO Budynek mieszkalny jednorodzinny wolnostojący „Dom LAMELA”					
ADRES / LOKALIZACJA (NR DZIAŁKI, OBRĘB, JEDN. EWIDENCYJNA) ul. Lipowa (fikcyjna), dz. nr ewid. 123/4, obręb 0005 Przykładowo, gm. Przykładowo (fikcyjna)				KAT. OBIEKTU I	
FUNKCJA		IMIĘ I NAZWISKO	SPECJALNOŚĆ, NR UPRAWNIEŃ	DATA	PODPIS
Projektant					
Projektant (wsp.)					
Sprawdzający					
Opracował					
TYTUŁ RYSUNKU ELEWACJA WSCHODNIA					
SKALA 1:50	FORMAT A2	DATA WYDANIA 2026-09-25	RODZAJ DOK. elewacja	NR RYSUNKU PB-AR-09	ARKUSZ 9/10
					REW. 0