

TOM RYSUNKÓW ARCHITEKTURY — WIDOKI Z MOD

Lp.	Nr rys.	Tytuł rysunku	Skala	Format
1	PB-AR-01	RZUT PARTERU	1:50	A1
2	PB-AR-02	RZUT I PIĘTRA	1:50	A3×3
3	PB-AR-03	RZUT II PIĘTRA	1:50	A3×3
4	PB-AR-04	RZUT DACHU	1:50	A2×3
5	PB-AR-05	PRZEKRÓJ A-A	1:50	A3×3
6	PB-AR-06	PRZEKRÓJ B-B	1:50	A3×3
7	PB-AR-07	ELEWACJA POŁUDNIOWA (OGRODOWA)	1:50	A3×3
8	PB-AR-08	ELEWACJA PÓŁNOCNA (OD ULICY)	1:50	A3×3
9	PB-AR-09	ELEWACJA WSCHODNIA	1:50	A2
10	PB-AR-10	ELEWACJA ZACHODNIA	1:50	A2

PRACOWNIA PROJEKTOWA PRACOWNIA PROJEKTOWA — nazwa do uzupełnienia		STADIUM PB	BRANŻA ARCHITEKTURA (AR)			
INWESTOR (do uzupełnienia)						
OBIEKT / NAZWA ZAMIERZENIA BUDOWLANEGO Budynek mieszkalny jednorodzinny wolnostojący „Dom LAMELA”						
ADRES / LOKALIZACJA (NR DZIAŁKI, OBRĘB, JEDN. EWIDENCYJNA) ul. Lipowa (fikcyjna), dz. nr ewid. 123/4, obręb 0005 Przykładowo, gm. Przykładowo (fikcyjna)				KAT. OBIEKTU I		
FUNKCJA	IMIĘ I NAZWISKO	SPECJALNOŚĆ, NR UPRAWNIEŃ	DATA	PODPIS		
Projektant						
Projektant (wsp.)						
Sprawdzający						
Opracował						
TYTUŁ RYSUNKU SPIS RYSUNKÓW						
SKALA —	FORMAT A4	DATA WYDANIA 2026-09-25	RODZAJ DOK. spis	NR RYSUNKU PB-AR-00	ARKUSZ —	REW.


odcinek kontury 100 mm (wydruk 1:1)

RZUT PARTERU 1:50

REW.	OPIS ZMIANY			DATA	
0	Wydanie — rysunek wygenerowany z modelu			2026-09-25	
PRACOWNIA PROJEKTOWA PRACOWNIA PROJEKTOWA — nazwa do uzupełnienia adres pracowni do uzupełnienia				STADIUM PB	BRANŻA ARCHITEKTURA (AR)
INWESTOR (do uzupełnienia)					
OBJEKT / NAZWA ZAMIERZENIA BUDOWLANEGO Budynek mieszkalny jednorodzinny wolnostojący „Dom LAMELA”					
ADRES / LOKALIZACJA (NR DZIAŁKI, OBRĘB, JEDN. EWIDENCYJNA) ul. Lipowa (fikcyjna), dz. nr ewid. 1234, obręb 0005 Przykładowo, gm. Przykładowo (fikcyjna)					KAT. OBJEKTU I
FUNKCJA	IMIĘ I NAZWISKO	SPECJALNOŚĆ, NR UPRAWNIEN		DATA	PODPIS
Projektant					
Projektant (wsp.)					
Sprawdzający					
Opracował					
TYTUŁ RYSUNKU					
RZUT PARTERU					
SKALA 1:50	FORMAT A1	DATA WYDANIA 2026-09-25	RODZAJ DOK. 1ZUT	NR RYSUNKU PB-AR-01	ARKUSZ 1/10
					REW. 0

OBJAŚNIENIA I UWAGI

- Wymiary w cm (mm w indeksie górnym, np. 24⁵ = 24,5 cm), rzędne w m względem ±0,000 = 101,650 m n.p.m. (PL-EVRF2007-NH).
- Rzuty: płaszczyzna cięcia +1,10 m nad posadzką kondygnacji. Linia kreskowa — elementy nad płaszczyznę cięcia (obrysy płyt i wsporników, brył wyższych kondygnacji, otwory w stropie nad, belki); linia cienka — elementy poniżej (widok).
- Otwory: licznik — szerokość, mianownik — wysokość w świetle muru, w nawiasie wysokość parapetu; symbol stolarki wg zestawienia stolarki.
- Numeracja pomieszczeń wg PN-B-01025 / PN-EN ISO 4157-2: <nr kondygnacji> (parter = 1) > <nr> identyfikator w modelu: <kond> <nr> (parter = 0).
- Drzwi: strona otwierania (lewej/prawej) wg modelu — patrzeć od strony, w którą otwiera się skrzydło.
- Rysunek wygenerowany automatycznie z modelu /modeluser/aihouse/model/budynek.yamł (wersja 1.0, 2026-09-25) — generatory lamela.views.

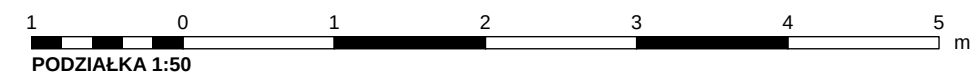

ZESTAWIENIE POMIESZCZEŃ

Nr	Nazwa pomieszczenia	Posadzka	Kat.	Wys. [m]	Pow. [m²]
1.06	Salon + jadalnia + kuchnia	Deska warstwowa dębowa 15 mm, klejona	podst.	2,77	54,44
1.13	Garaż 2-stanowiskowy	Posadzka żywiczna epoksydowa antypoślizgowa	podst. (garaż)	2,76	37,42
1.10	Pokój gościnny / gabinet	Deska warstwowa dębowa 15 mm, klejona	podst.	2,77	12,52
1.12	Pomieszczenie techniczne	Płytki gresowe 60×120 na kleju C2TE S1 techn.	podst.	2,76	8,85
1.11	Przedśrodek gospodarczy	Płytki gresowe 60×120 na kleju C2TE S1 ruchu	podst.	2,76	7,18
1.02	Hol	Płytki gresowe 60×120 na kleju C2TE S1 ruchu	podst.	2,77	4,44
1.01	Wiatrołap	Płytki gresowe 60×120 na kleju C2TE S1 ruchu	podst.	2,77	3,89
1.09	Łazienka gościnna (natrysk)	Płytki gresowe 60×120 na kleju C2TE S1 pomoc.	podst.	2,77	3,86
1.07	Pas komunikacyjny przy schodach	Deska warstwowa dębowa 15 mm, klejona	ruchu	2,77	3,51
1.16	Schowek pod spocznikiem (h < 1,40)	Płytki gresowe 60×120 na kleju C2TE S1 pomoc.	podst.	1,37	2,91
1.04	Klatka schodowa	Deska warstwowa dębowa 15 mm, klejona	ruchu	2,77	2,78
1.03	WC gościnne	Płytki gresowe 60×120 na kleju C2TE S1 pomoc.	podst.	2,77	2,32
1.08	Przedpokój gościnny	Deska warstwowa dębowa 15 mm, klejona	ruchu	2,77	1,46
1.15	Schowek pod schodami (h 1,40-2,20)	Płytki gresowe 60×120 na kleju C2TE S1 pomoc.	podst.	1,80	1,45
1.05	Śpiżarnia	Płytki gresowe 60×120 na kleju C2TE S1 pomoc.	podst.	2,77	1,02
1.14	Szacht instalacyjny SI		techn.	2,77	0,45
RAZEM powierzchnia netto					148,49
w tym użytkowa (podst. + pomoc.)					115,93

OZNACZENIA MATERIAŁÓW (PN-B-01030 + przyjęte)

	Wełna mineralna 035 (szkielet, docieplenia, ściana dom-garaż) — meander „UUU”		Stal konstrukcyjna S355 (słupy RK, rama boksu C), cynkowana ognioowo + malowana proszkowo RAL 7016 — zabezpieczenie
	Styropian grafitylowy EPS 031 (ETICS, NRO w systemie) — zrygawk „VVV”		Ścianka szklana VSG 2 × 8 mm w ramie aluminiowej (wiatrołap / hol)
	Bloczek wapniowo-piaskowy 12 cm, kl. 15 (ścianki działowe, licowy w klatce); Bloczek wapniowo-piaskowy (silikat) 18 cm, kl. 20, gr. 1, na zaprawie cienkowarstwowej — kratka ukłosa 45°/135°		Żelbet C25/30, B500SP (stropy, płyta fundamentowa, ściany) — 45° na przemienną cięgłą i przerywaną

OZNACZENIA LINII

- elementy nad płaszczyznę cięcia (obrysy płyt, wsporników, brył wyższych kondygnacji)
- elementy poniżej płaszczyzny cięcia (widok z góry)
- osie konstrukcyjne; linia punktowa z pogrubionymi końcami — ślad przekroju

odcinek konteiny 100 mm (wydruk 1:1)

RZUT I PIĘTRA 1:50

ZESTAWIENIE POMIESZCZEŃ

Nr	Nazwa pomieszczenia	Posadzka	Kat.	Wys. [m]	Pow. [m²]
2.02	Pokój rodzinny / biblioteka (boks C)	Deska warstwowa dębowa 15 mm, klejona	podst.	2,77	28,36
2.01	Hol	Deska warstwowa dębowa 15 mm, klejona	naruchu	2,77	14,09
2.03	Pokój dziecka 1	Deska warstwowa dębowa 15 mm, klejona	podst.	2,77	13,19
2.04	Pokój dziecka 2	Deska warstwowa dębowa 15 mm, klejona	podst.	2,77	12,52
2.08	Pralnia z suszarnią	Płytki gresowe 60×120 na kleju C2TE \$1	pomoc.	2,77	6,64
2.05	Łazienka dzieci (wanna)	Płytki gresowe 60×120 na kleju C2TE \$1	pomoc.	2,77	5,50
2.07	WC z natryskiem	Płytki gresowe 60×120 na kleju C2TE \$1	pomoc.	2,77	4,08
2.06	Klatka schodowa	Deska warstwowa dębowa 15 mm, klejona	naruchu	2,77	0,49
2.09	Szacht instalacyjny SI		techn.	2,77	0,45
RAZEM powierzchnia netto					85,33
w tym użytkowa (podst. + pomoc.)					70,30

OZNACZENIA MATERIAŁÓW (PN-B-01030 + przyjęte)


	Wełna mineralna 035 (szkielet, docieplenia, ściana dom-garaż)		Rama boksu C: ruszt stalowy ocynkowany w okładzinie z blachy aluminiowej RAL 7016 (pusta w środku); Stal konstrukcyjna S355 (skrupy RK, rama boksu C); cynikowana ogniowo + malowana proszkowo RAL 7016 — zacczernienie
	Styropian grafitowy EPS 031 (ETICS, NRO w systemie) — żygżak „VVV”		Żelbet C25/30, B500SP (stropy, płyta fundamentowa, ściany) — 45° na przemiern ciągle i przerywane
	Bloczek wapniowo-piaskowy 12 cm, kl. 15 (ścianki działowe, licowy w klatce); Bloczek wapniowo-piaskowy (slikat) 18 cm, kl. 20, gr. 1, na zaprawie cienkowarstwowej — kratka ukośna 45°/135°		

OZNACZENIA LINII


- elementy nad płaszczyzną cięcia (obrys płyt, wsporników, brył wyższych kondygnacji)
- elementy poniżej płaszczyzny cięcia (widok z góry)
- osie konstrukcyjne; linia punktowa z pogrubionymi końcami — ślad przekroju

OBJAŚNIENIA I UWAGI

- Wymiary w cm (mm w indeksie górnym, np. 24⁵ = 24,5 cm), rzędne w m względem ±0,000 = 101,650 m n.p.m. (PL-EVRF2007-NH).
- Rzuty: płaszczyzna cięcia +1,10 m nad posadzką kondygnacji. Linia kreskową — elementy nad płaszczyzną cięcia (obrys płyt i wsporników, brył wyższych kondygnacji, otwory w stropie nad, belki); linia cieniłą — elementy poniżej (widok).
- Otwory: licznik — szerokość, mianownik — wysokość w świetle muru, w nawiasie wysokość parapetu; symbol stolarki wg zestawienia stolarki.
- Numeracja pomieszczeń wg PN-B-01025 / PN-EN ISO 4157-2: <nr kondygnacji (parter = 1)>, <nr>; identyfikator w modelu: <kond>.<nr> (parter = 0).
- Drzwi: strona otwierania (lewe/prawe) wg modelu — patrząc od strony, w którą otwiera się skrzydło.
- Rysunek wygenerowany automatycznie z modelu /home/user/aihouse/model/budynek.yamł (wersja 1.0, 2026-09-25) — generatory lamela.views.

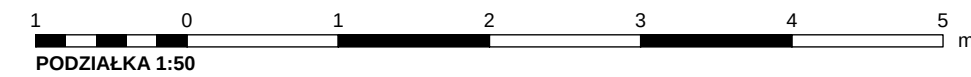

REW.	OPIS ZMIANY	DATA
0	Wydanie — rysunek wygenerowany z modelu	2026-09-25
PRACOWNIA PROJEKTOWA PRACOWNIA PROJEKTOWA — nazwa do uzupełnienia		STADIUM PB
adres pracowni do uzupełnienia		BRANŻA ARCHITEKTURA (AR)
INWESTOR (do uzupełnienia)		
OBIEKT / NAZWA ZAMIERZENIA BUDOWLANEGO Budynek mieszkalny jednorodzinny wolnostojący „Dom LAMELA”		
ADRES / LOKALIZACJA (NR DZIAŁKI, OBRĘB, JEDN. EWIDENCYJNA) ul. Lipowa (fikcyjna), dz. nr ewid. 123/4, obręb 0005 Przykładowo, gm. Przykładowo (fikcyjna)		KAT. OBIEKTU I
FUNKCJA	IMIĘ I NAZWISKO	SPECJALNOŚĆ, NR UPRAWNIENI
Projektant		DATA
Projektant (wsp.)		PODPIS
Sprawdzający		
Opracował		
TYTUŁ RYSUNKU RZUT I PIĘTRA		
SKALA 1:50	FORMAT A3×3	DATA WYDANIA 2026-09-25
RODZAJ DOK. rzut	NR RYSUNKU PB-AR-02	ARKUSZ 2/10
REW. 0		

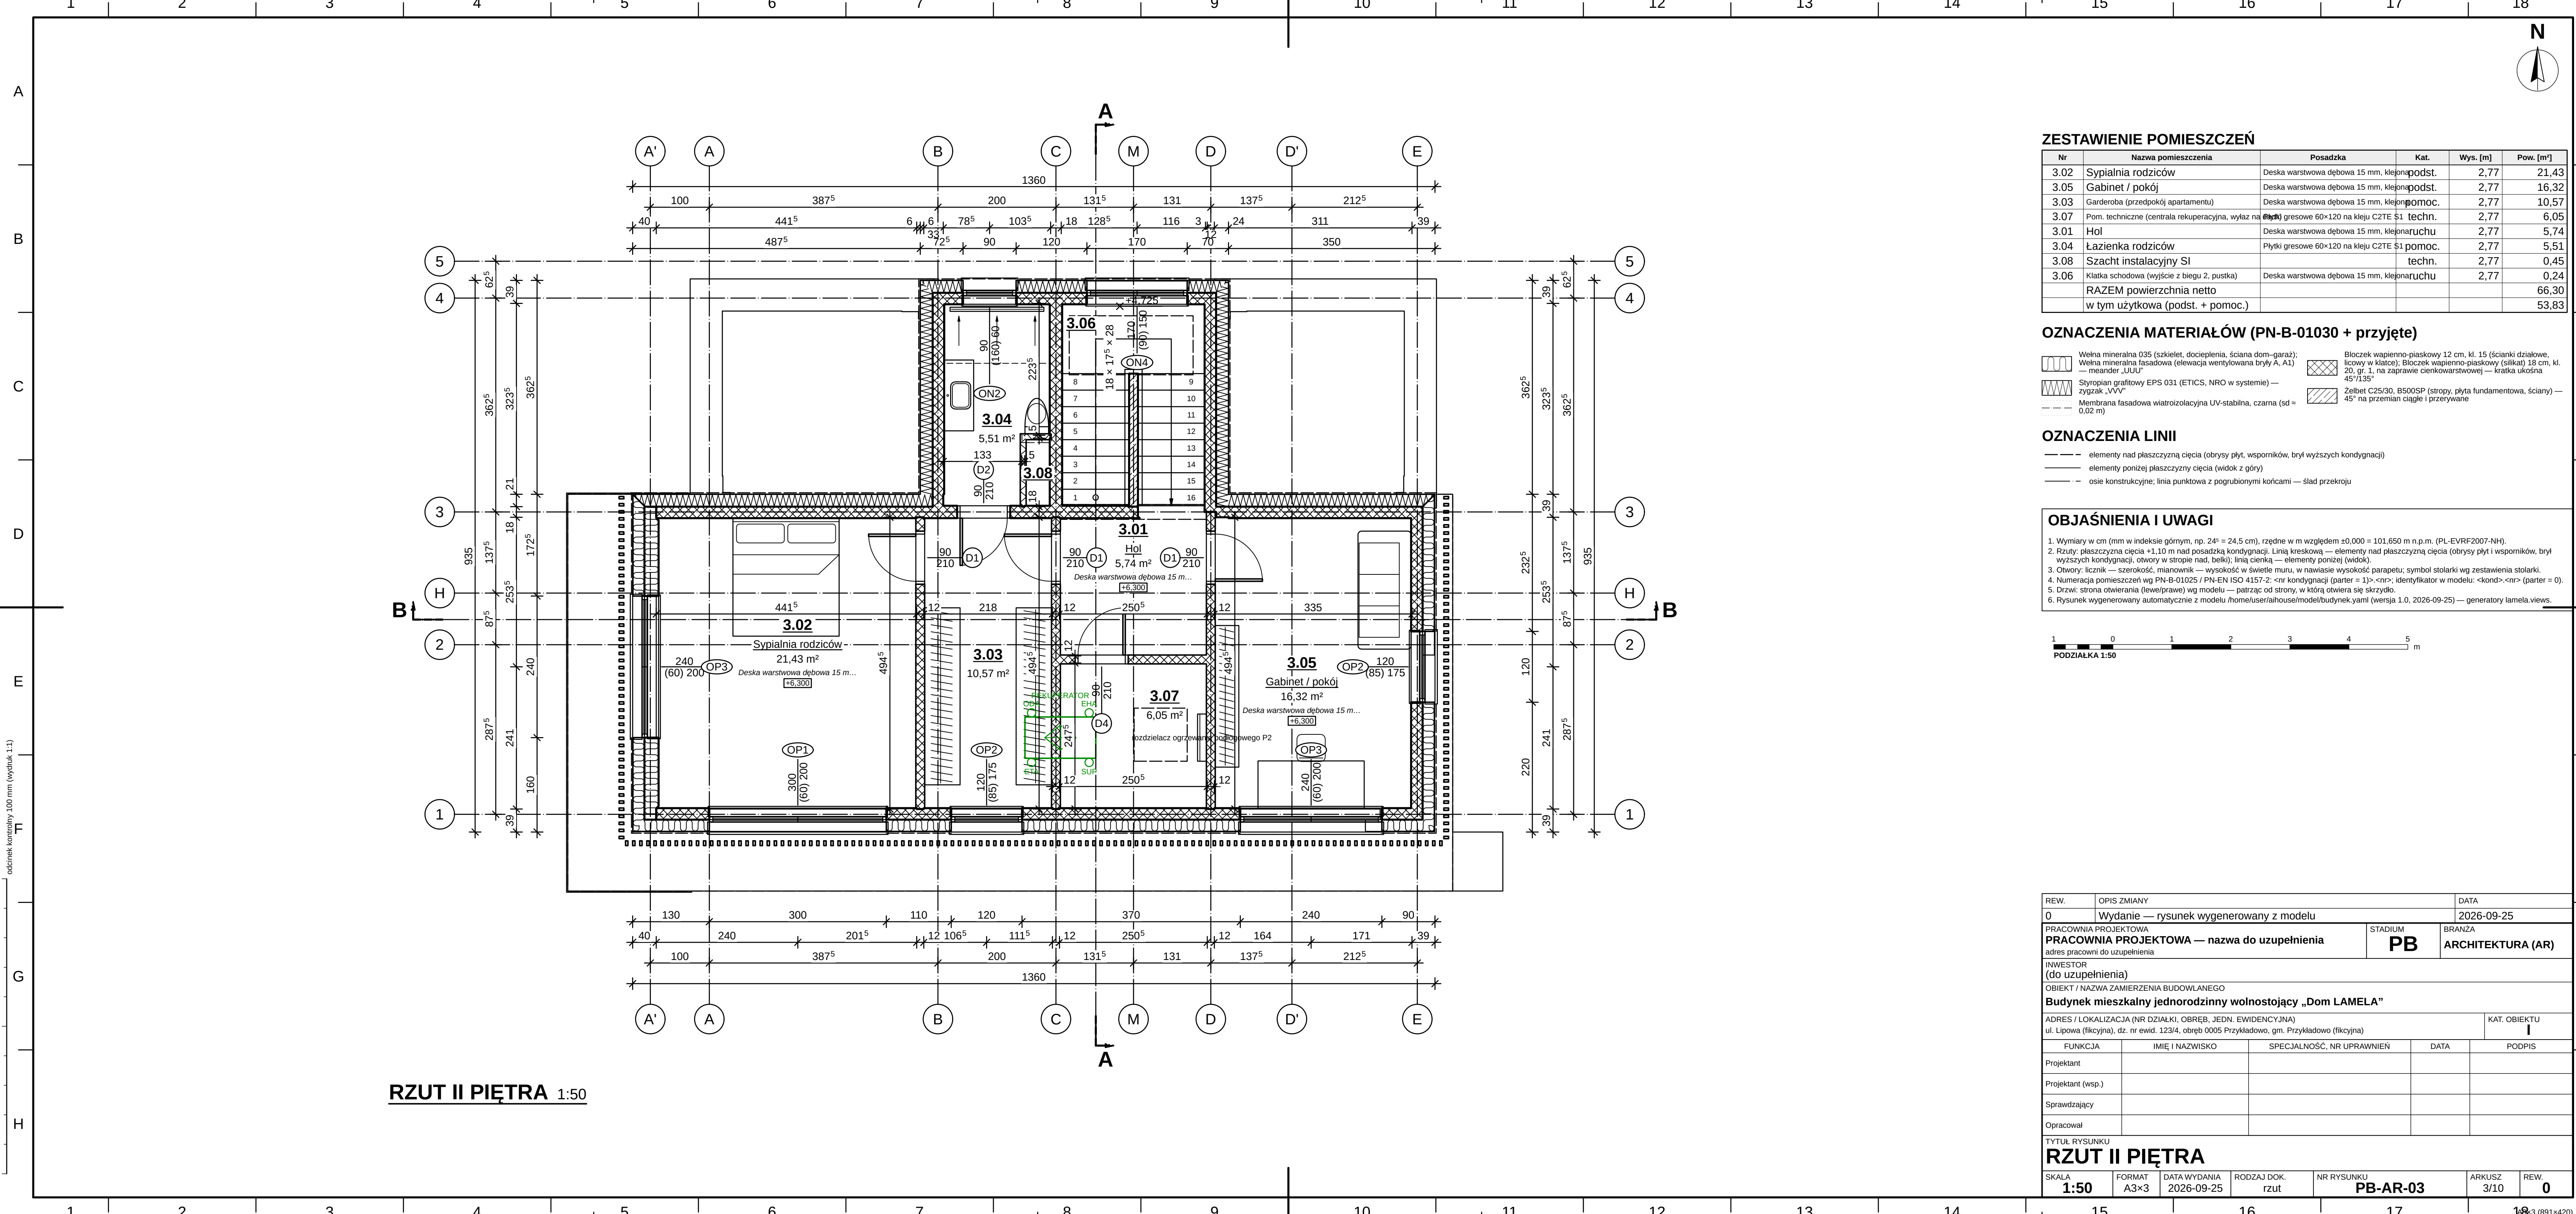

ZESTAWIENIE POMIESZCZEŃ

Nr	Nazwa pomieszczenia	Posadzka	Kat.	Wys. [m]	Pow. [m²]
3.02	Sypialnia rodziców	Deska warstwowa dębowa 15 mm, klejona	podst.	2,77	21,43
3.05	Gabinet / pokój	Deska warstwowa dębowa 15 mm, klejona	podst.	2,77	16,32
3.03	Garderoba (przedpokój apartamentu)	Deska warstwowa dębowa 15 mm, klejona	pomoc.	2,77	10,57
3.07	Pom. techniczne (centrala rekuperacyjna, wylaz na dach)	Płytki gresowe 60x120 na kleju C2TE \$1	techn.	2,77	6,05
3.01	Hol	Deska warstwowa dębowa 15 mm, klejona	aruchu	2,77	5,74
3.04	Łazienka rodziców	Płytki gresowe 60x120 na kleju C2TE \$1	pomoc.	2,77	5,51
3.08	Szacht instalacyjny SI		techn.	2,77	0,45
3.06	Klatka schodowa (wyjście z biegu 2, pustka)	Deska warstwowa dębowa 15 mm, klejona	aruchu	2,77	0,24
RAZEM powierzchnia netto					66,30
w tym użytkowa (podst. + pomoc.)					53,83

OZNACZENIA MATERIAŁÓW (PN-B-01030 + przyjęte)


	Wetna mineralna 035 (szkielet, docieplenia, ściana dom-garaż); Wetna mineralna fasadowa (elewacja wentylowana bryły A, A1) — meander „JU”		Bloczek wapienno-piaskowy 12 cm, kl. 15 (ścianki działowe, licowy w klatce); Bloczek wapienno-piaskowy (słikat) 18 cm, kl. 20, gr. 1, na zaprawie cienkowarstwowej — klatka ukosna 45°/135°
	Styropian gąbłowy EPS 031 (ETICS, NRO w systemie) — zygzak „VVV”		Żelbet C25/30, B500SP (stropy, płyta fundamentowa, ściany) — 45° na przemienną ciągłą i przerywaną
	Membrana fasadowa wiatroizolacyjna UV-stabilna, czarna (sd = 0,02 m)		

OZNACZENIA LINII

- elementy nad płaszczyzną cięcia (obryszy płyt, wsporników, brył wyższych kondygnacji)
- elementy poniżej płaszczyzny cięcia (widok z góry)
- osie konstrukcyjne; linia punktowa z pogrubionymi końcami — ślad przekroju

OBJAŚNIENIA I UWAGI

- Wymiary w cm (mm w indeksie górnym, np. 24^o = 24,5 cm), rzędne w m względem ±0,000 = 101,650 m n.p.m. (PL-EVRF2007-NH).
- Rzuty: płaszczyzna cięcia +1,10 m nad posadzką kondygnacji. Linia kreskowa — elementy nad płaszczyzną cięcia (obryszy płyt i wsporników, brył wyższych kondygnacji, otwory w stropie nad, belki); linia cienka — elementy poniżej cięcia (obryszy płyt i wsporników).
- Otwory: licznik — szerokość, mianownik — wysokość w świetle muru, w nawiasie wysokość parapetu; symbol stolarki wg zestawienia stolarki.
- Numeracja pomieszczeń wg PN-B-01025 / PN-EN ISO 4157-2: <nr kondygnacji (parter = 1)>.<nr>; identyfikator w modelu: <kond>.<nr> (parter = 0).
- Drzwi: strona otwierania (lewe/prawe) wg modelu — patrząc od strony, w którą otwiera się skrzydło.
- Rysunek wygenerowany automatycznie z modelu /home/user/aihouse/model/budynek.yaml (wersja 1.0, 2026-09-25) — generatory lamela.views.

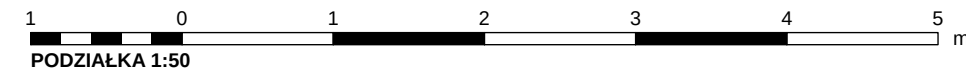



REW.	OPIS ZMIANY			DATA
0	Wydanie — rysunek wygenerowany z modelu			2026-09-25
PRACOWNIA PROJEKTOWA PRACOWNIA PROJEKTOWA — nazwa do uzupełnienia adres pracowni do uzupełnienia			STADIUM PB	BRANŻA ARCHITEKTURA (AR)
INWESTOR (do uzupełnienia)				
OBIEKT / NAZWA ZAMIERZENIA BUDOWLANEGO Budynek mieszkalny jednorodzinny wolnostojący „Dom LAMELA”				
ADRES / LOKALIZACJA (NR DZIAŁKI, OBRĘB, JEDN. EWIDENCYJNA) ul. Lipowa (fikcyjna), dz. nr ewid. 123/4, obręb 0005 Przykładowo, gm. Przykładowo (fikcyjna)				KAT. OBIEKTU I
FUNKCJA	IMIĘ I NAZWISKO	SPECJALNOŚĆ, NR UPRAWNIENI	DATA	PODPIS
Projektant				
Projektant (wsp.)				
Sprawdzający				
Opracował				
TYTUŁ RYSUNKU RZUT II PIĘTRA				
SKALA 1:50	FORMAT A3×3	DATA WYDANIA 2026-09-25	RODZAJ DOK. rzut	NR RYSUNKU PB-AR-03
ARKUSZ 3/10		REW. 0		

OZNACZENIA LINII

- elementy nad płaszczyznę cięcia (obryszy płyt, wspomników, brył wyższych kondygracji)
--- elementy poniżej płaszczyzny cięcia (wielok z góry)
--- osie konstrukcyjne; linia punktowa z pogrubionymi końcami --- ślad przekroju

OBJAŚNIENIA I UWAGI


1. Wymiary w cm (mm w indeksie górnym, np. 24⁵ = 24,5 cm), rzędy w m względem s.0.000 ± 101.650 m n.p.m. (PL-EVRP2007-NH).
2. Rysunek wygenerowany automatycznie z modelu /home/user/housemodel/budynek-yam1 (wersja 1.0, 2026-09-25) --- generatory lamela.views.

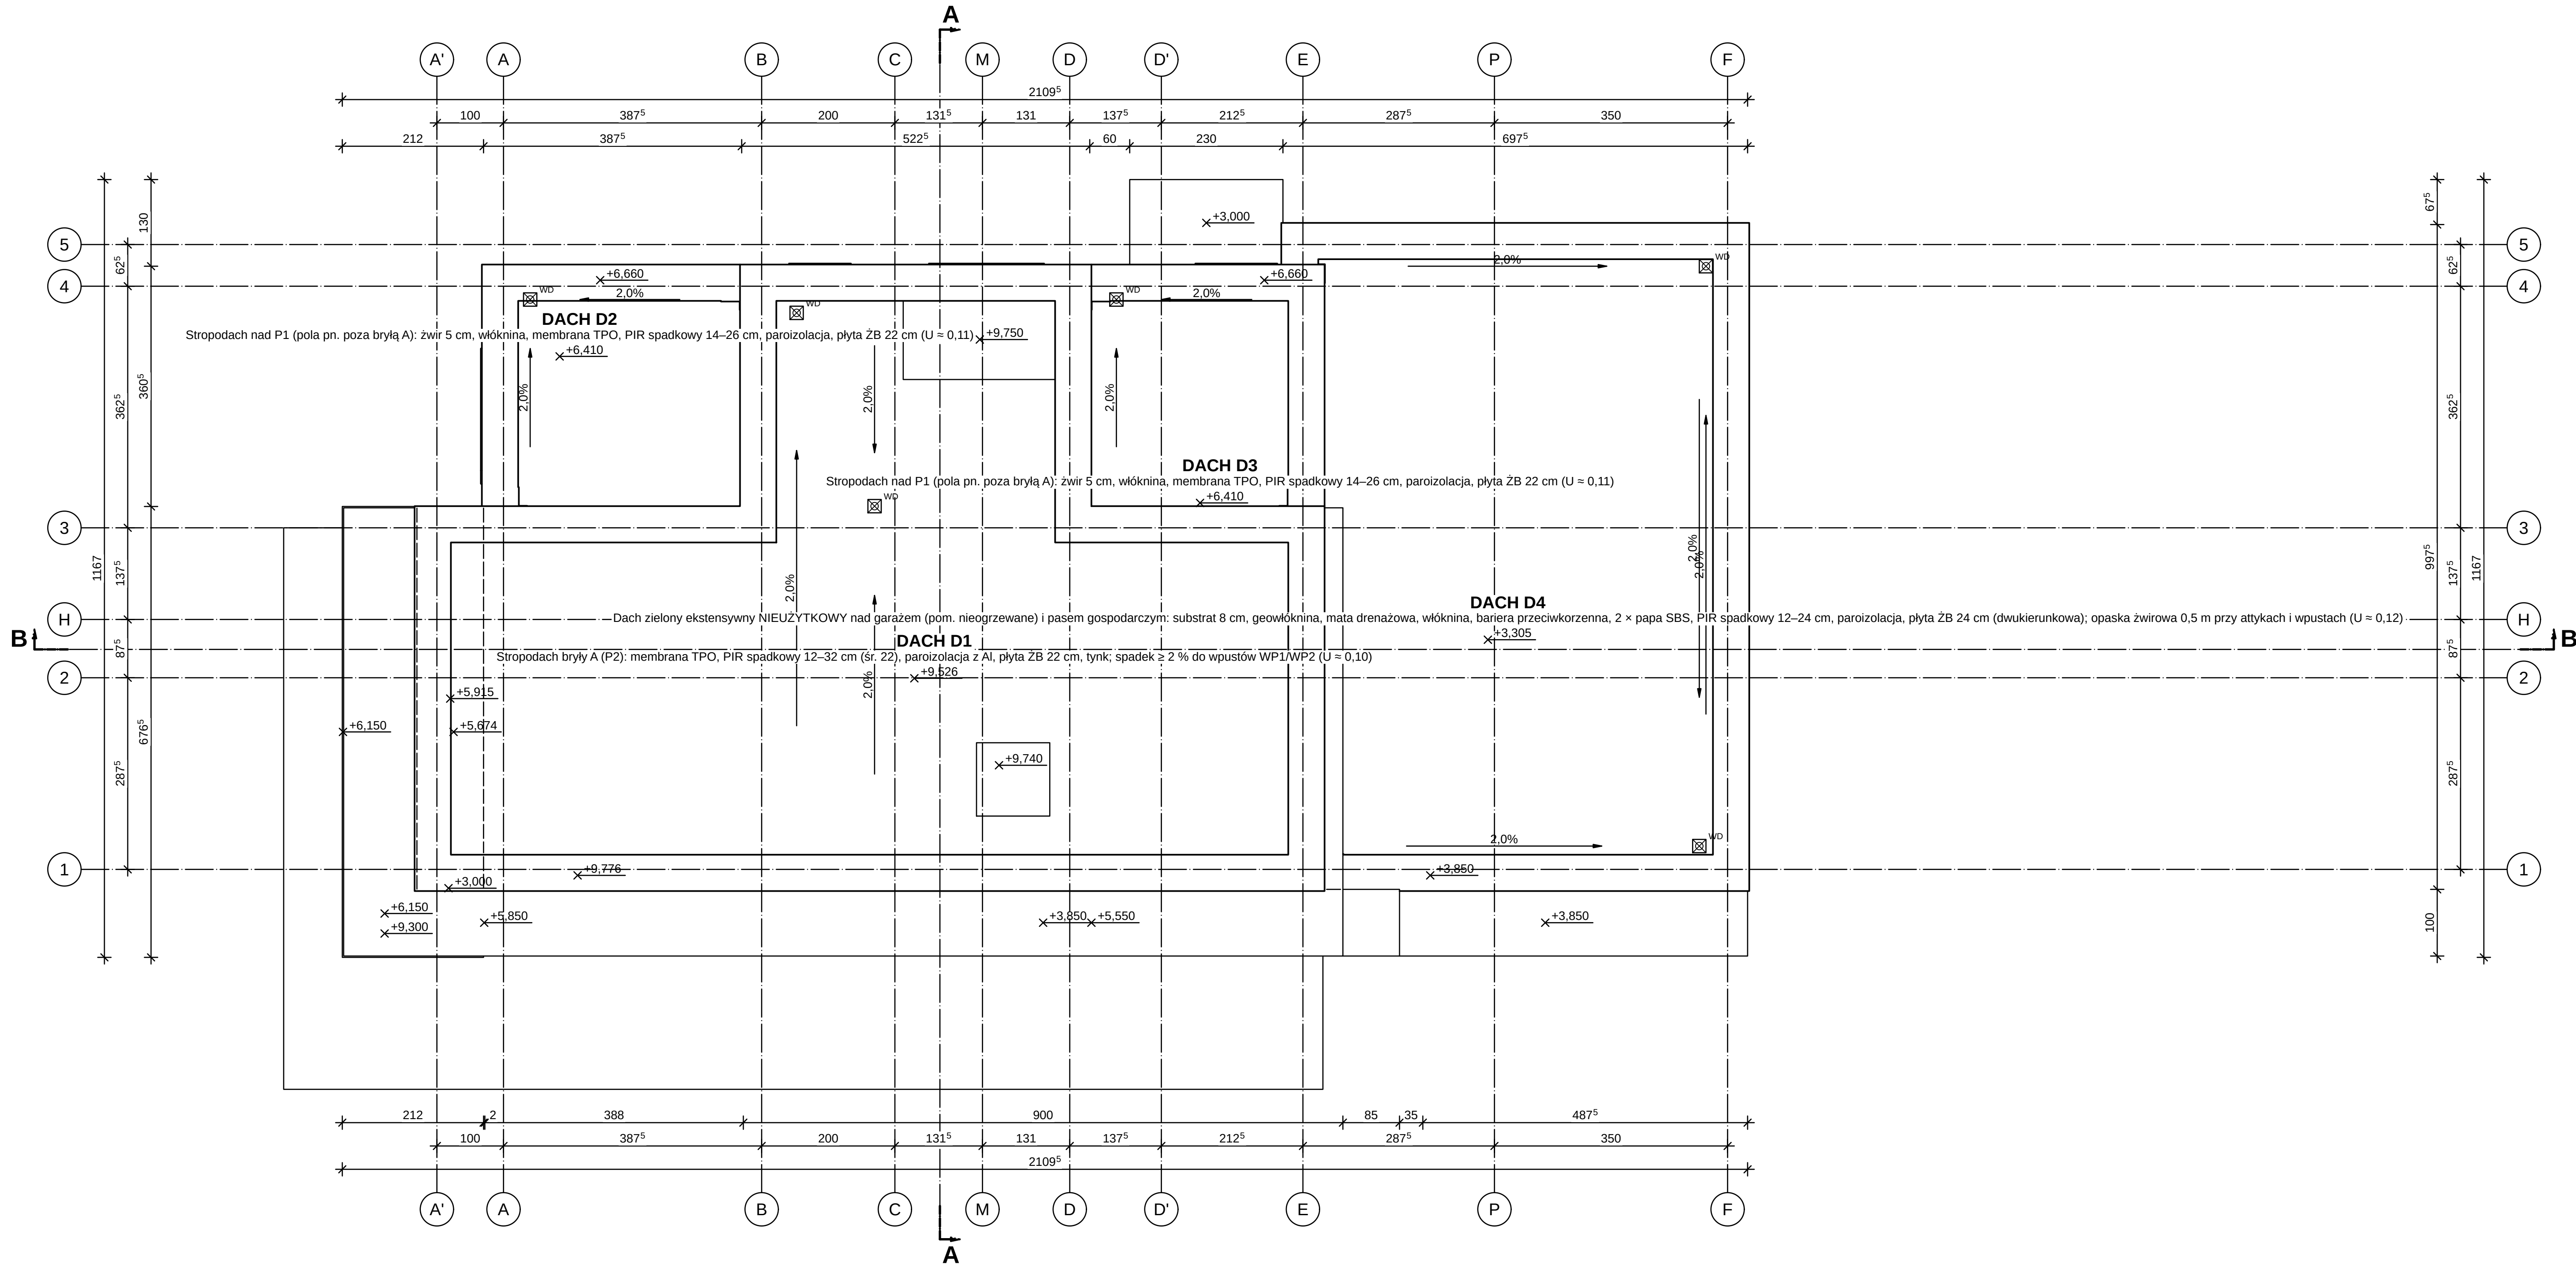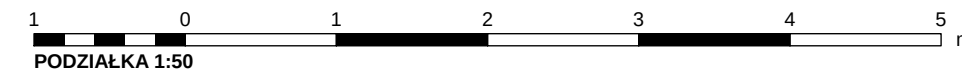

RZUT DACHU 1:50

REW.	OPIS ZMIANY			DATA	
0	Wydanie — rysunek wygenerowany z modelu			2026-09-25	
PRACOWNIA PROJEKTOWA			STADIUM	BRANŻA	
PRACOWNIA PROJEKTOWA — nazwa do uzupełnienia			PB	ARCHITEKTURA (AR)	
adres pracowni do uzupełnienia					
INWESTOR					
(do uzupełnienia)					
OBIEKT / NAZWA ZAMIERZENIA BUDOWLANEGO					
Budynek mieszkalny jednorodzinny wolnostojący „Dom LAMELA”					
ADRES / LOKALIZACJA (NR DZIAŁKI, OBRĘB, JEDN. EVIDENCYJNA)					KAT. OBIEKTU
ul. Lipowa (Racjonal), dz. nr ewid. 1234, obręb 0005 Przykładowo, gm. Przykładowo (Racjonal)					I
FUNKCJA		IMIĘ I NAZWISKO	SPECJALNOŚĆ, NR UPRAWNIEN	DATA	PODPIŚ
Projektant					
Projektant (wsp.)					
Sprawdzający					
Opracował					
TYTUŁ RYSUNKU					
RZUT DACHU					
SKALA	FORMAT	DATA WYDANIA	RODZAJ DOK.	NR RYSUNKU	ARKUSZ
1:50	A2x3	2026-09-25	rzut	PB-AR-04	4/10
					REW.
					0

PRZEKRÓJ A-A 1:50

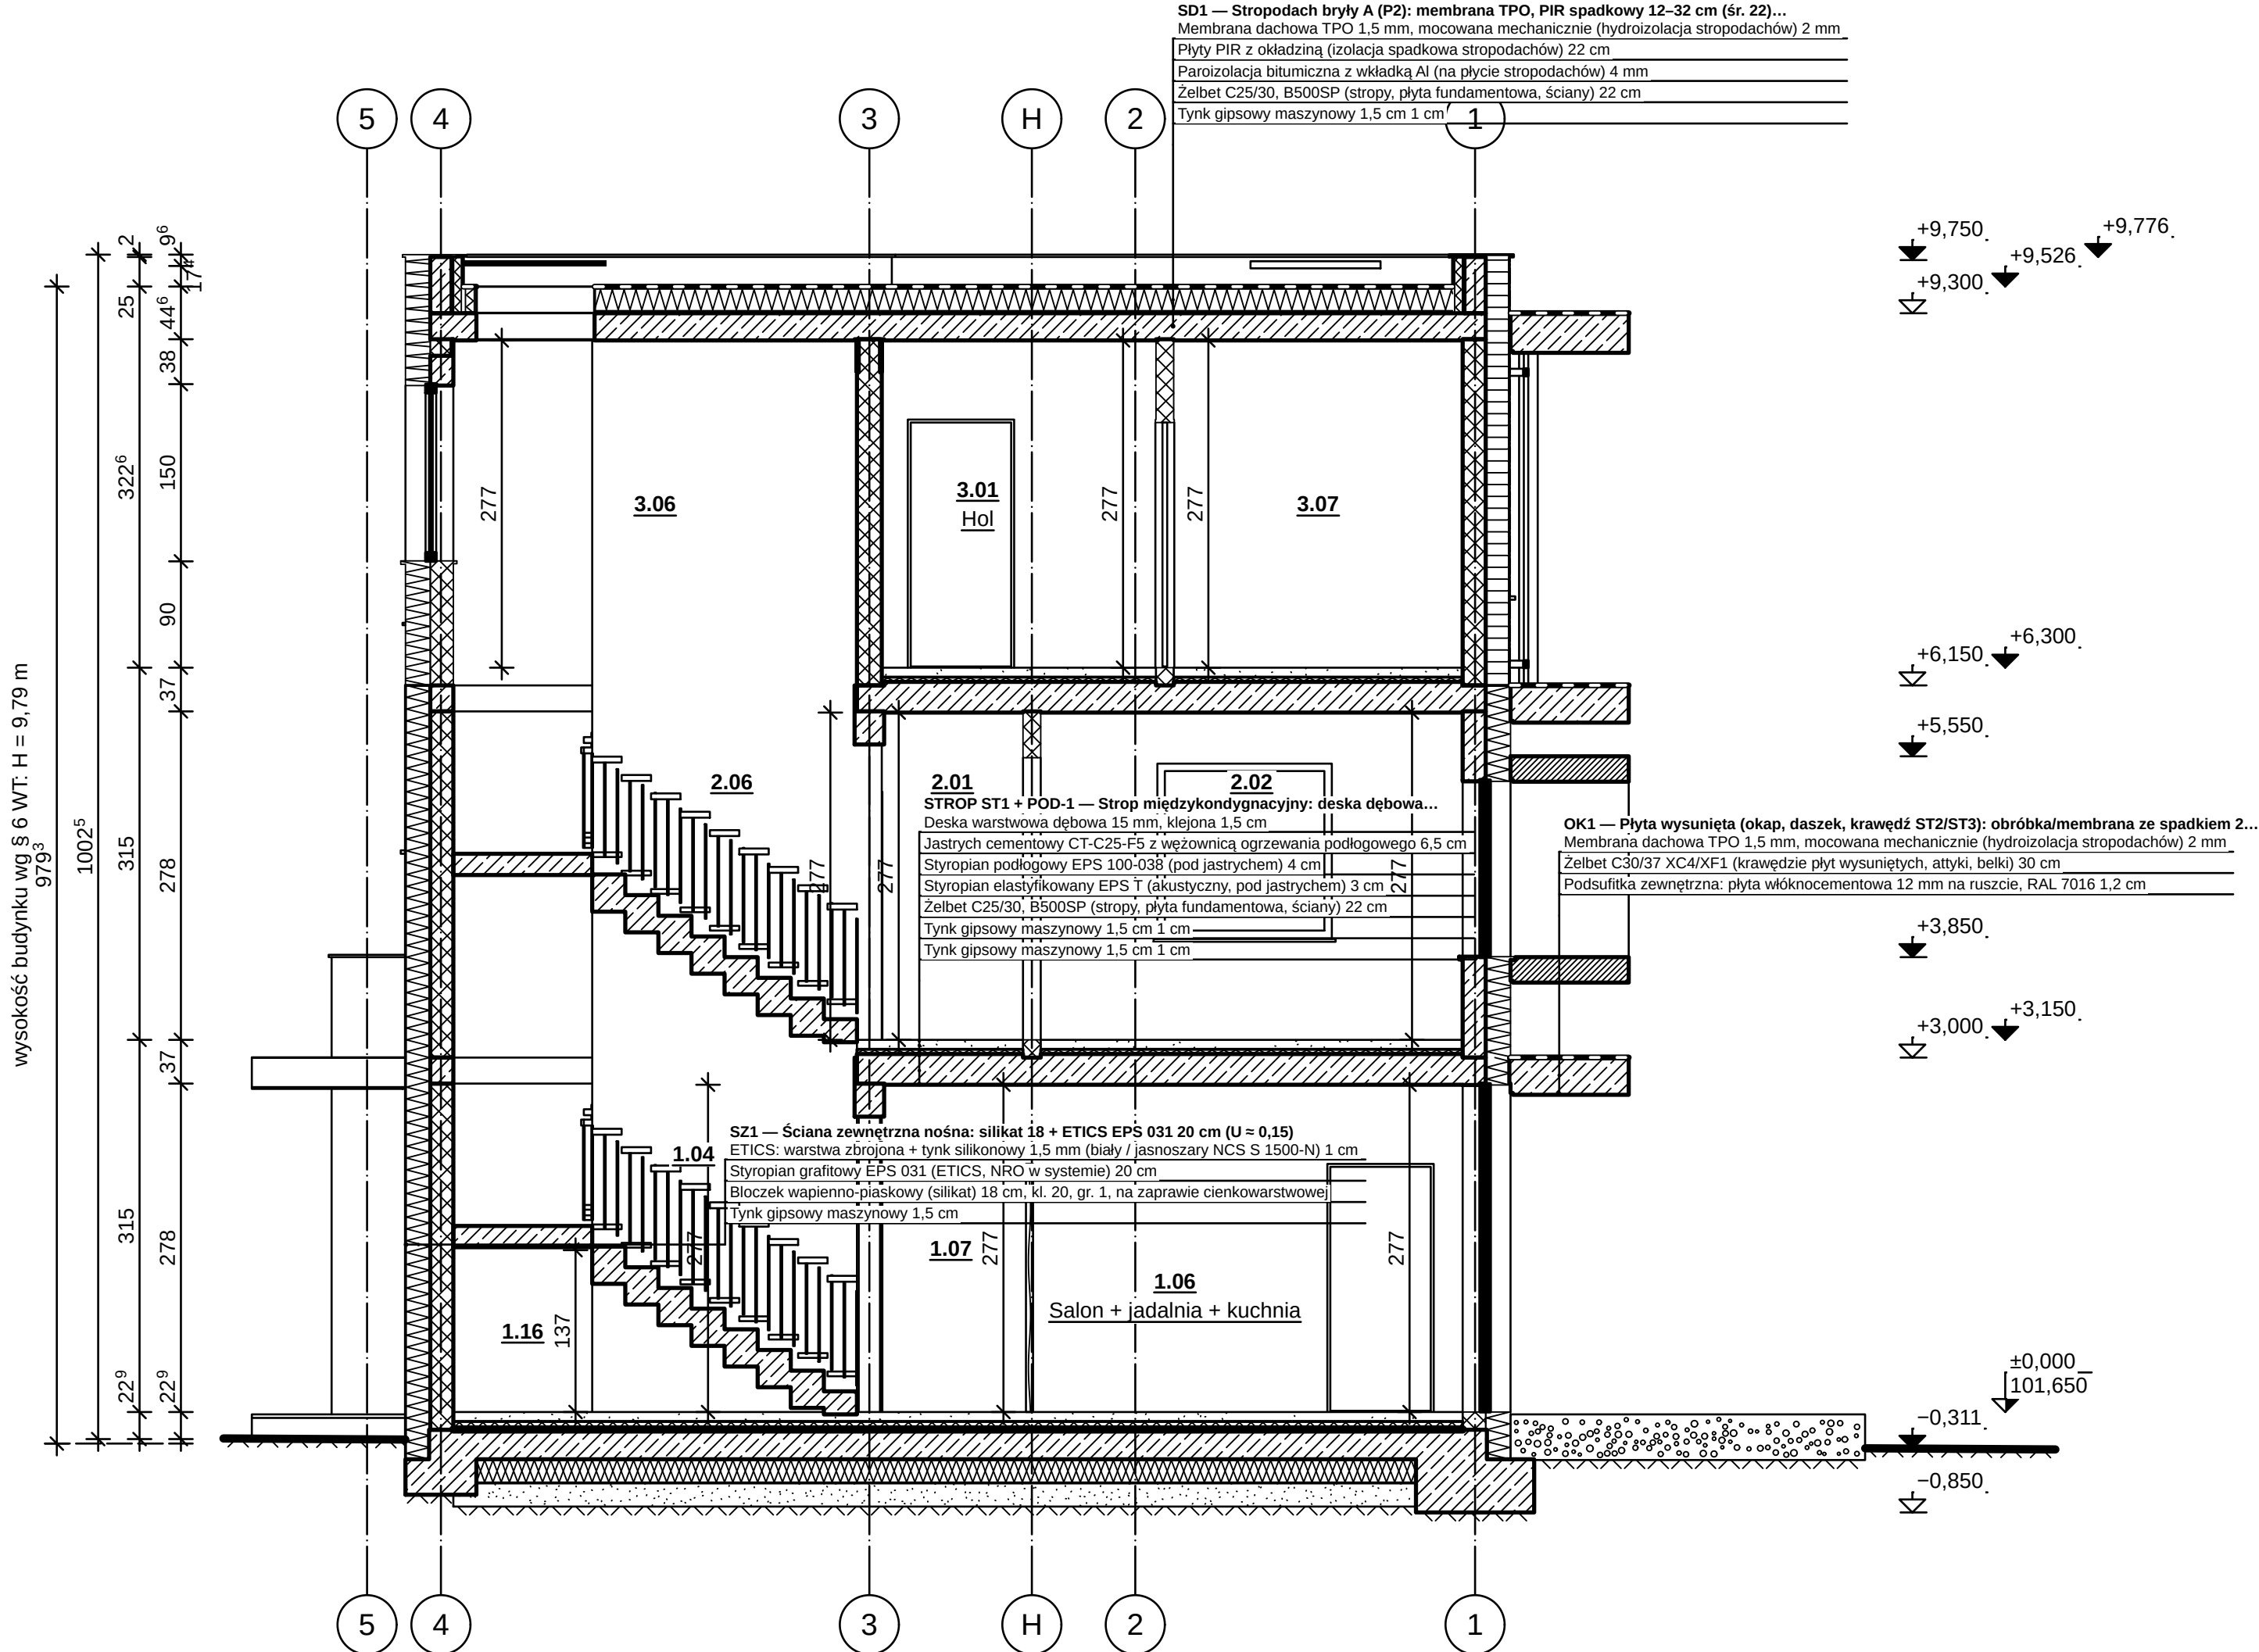

OZNACZENIA MATERIAŁÓW (PN-B-01030 + przyjęte)

	Lamele dębowe 30x60 mm (ekran komunikacji P0, h 2,10 m); Deska warstwowo dębowa 15 mm, klejona — przekrój wzdłuż włókien		Membrana fasadowa wiatroizolacyjna UV-stabilna, czarna (sd = 0,02 m)
	grunt rodzimy		Bloczek wapienno-piaskowy 12 cm, kl. 15 (ścianki działowe, licowy w kładce); Bloczek wapienno-piaskowy (silikat) 18 cm, kl. 20, gr. 1, na zaprawie cienkowarstwowej — kładka ukośna 45°/135°
	Włna mineralna fasadowa (elewacja wentylowana bryły A, A1) — meander „UUU”		Paroizolacja bitumiczna z wkładką Al (na płycie stropodachów) — linia kreskowa cienka 3/1 po ciepłej stronie
	Płyty PIR z okładziną (izolacja spadkowa stropodachów) — zygzak z okładziną		Podosypka piaskowa zagęszczona (l_s ≥ 0,98)
	Izolacja przeciwwilgociowa i przeciwdrońowa: membrana SBS 4 mm na płycie fundamentowej — linia bardzo gruba		Obróbki blacharskie (blacha powlekana); Stalarka — profile aluminiowe, antracyt; Rama boku C: ruszt stalowy ocynkowany w okładzinie z blachy aluminiowej RAL 7016 (pusta w środku); Stal malowana proszkowo (balustrady, rygle) — zacierzenie
	Membrana dachowa TPO 1,5 mm, mocowana mechanicznie (hydroizolacja stropodachów) — pas czarno-biały		Szkło (szyby zespolone); Ścianka szklana VSG 2 × 8 mm w ramie aluminiowej (wiatrolap / hol)
	Styropian grafitowy EPS 031 (ETICS, NRO w systemie); Styropian podłogowy EPS 100-038 (pod jastrychem); Styropian elastykowany EPS T (akustyczny, pod jastrychem) — zygzak „VVV”		Żelbet C25/30, B500SP (stropy, płyta fundamentowa, ściany); Żelbet C30/37 XC4/XF1 (krawędzie płyt wysuniętych, attyki, belki) — 45° na przemian ciągle i przerywane
	Polistyren ekstrudowany XPS 300 (pod płytą fundamentową, cokół, izolacja obwodowa) — zygzak podwójny		Podbudowa nawierzchni (kruszywo)
	Jastrych cementowy CT-C25-F5 z węzownicą ogrzewania podłogowego — kropki		

OBJAŚNIENIA I UWAGI

- Wymiary w cm (mm w indeksie górnym, np. 24³ = 24,5 cm), rzędne w m względem ±0,000 = 101,650 m n.p.m. (PL-EVRF2007-NH).
- Rzędne: trójkąt zacierzony — poziom wykończenia, niezacierzony — konstrukcji, w połowie zacierzony — poziom ±0,000 z rzędną bezwzględną (PN-B-01025).
- Wysokość budynku wg § 6 WT: H = 9,79 m.
- Opisy warstw: kod i nazwa przegrody z modelu, materiały i grubości wg modelu (od góry / od lewej).
- Opisy warstw pominięte na rysunku (brak miejsca w podziale 1:50): POD-0, STROP ST2 + POD-1 — układ warstw wg zestawienia przegród w części opisowej / przekroju 1:50.
- Rysunek wygenerowany automatycznie z modelu /home/user/aihouse/model/budynek.yaml (wersja 1.0, 2026-09-25) — generatory lamela.views.




REW.		OPIS ZMIANY		DATA		
0		Wydanie — rysunek wygenerowany z modelu		2026-09-25		
PRACOWNIA PROJEKTOWA PRACOWNIA PROJEKTOWA — nazwa do uzupełnienia adres pracowni do uzupełnienia			STADIUM PB	BRANZA ARCHITEKTURA (AR)		
INWESTOR (do uzupełnienia)						
OBIEKT / NAZWA ZAMIERZENIA BUDOWLANEGO Budynek mieszkalny jednorodzinny wolnostojący „Dom LAMELA”						
ADRES / LOKALIZACJA (NR DZIAŁKI, OBRĘB, JEDN. EWIDENCYJNA) ul. Lipowa (fikcyjna), dz. nr ewid. 123/4, obręb 0005 Przykładowo, gm. Przykładowo (fikcyjna)				KAT. OBIEKTU I		
FUNKCJA		IMIĘ I NAZWISKO		SPECJALNOŚĆ, NR UPRAWNIEN	DATA	PODPIS
Projektant						
Projektant (wsp.)						
Sprawdzający						
Opracował						
TYTUŁ RYSUNKU PRZEKRÓJ A-A						
SKALA 1:50	FORMAT A3x3	DATA WYDANIA 2026-09-25	RODZAJ DOK. przekrój	NR RYSUNKU PB-AR-05	ARKUSZ 5/10	REW. 0

PRZEKRÓJ B-B 1:50

wysokość budynku wg § 6 WT: H = 9,79 m
9/79³

odcinek kantylajny 100 mm (wydruk 1:1)

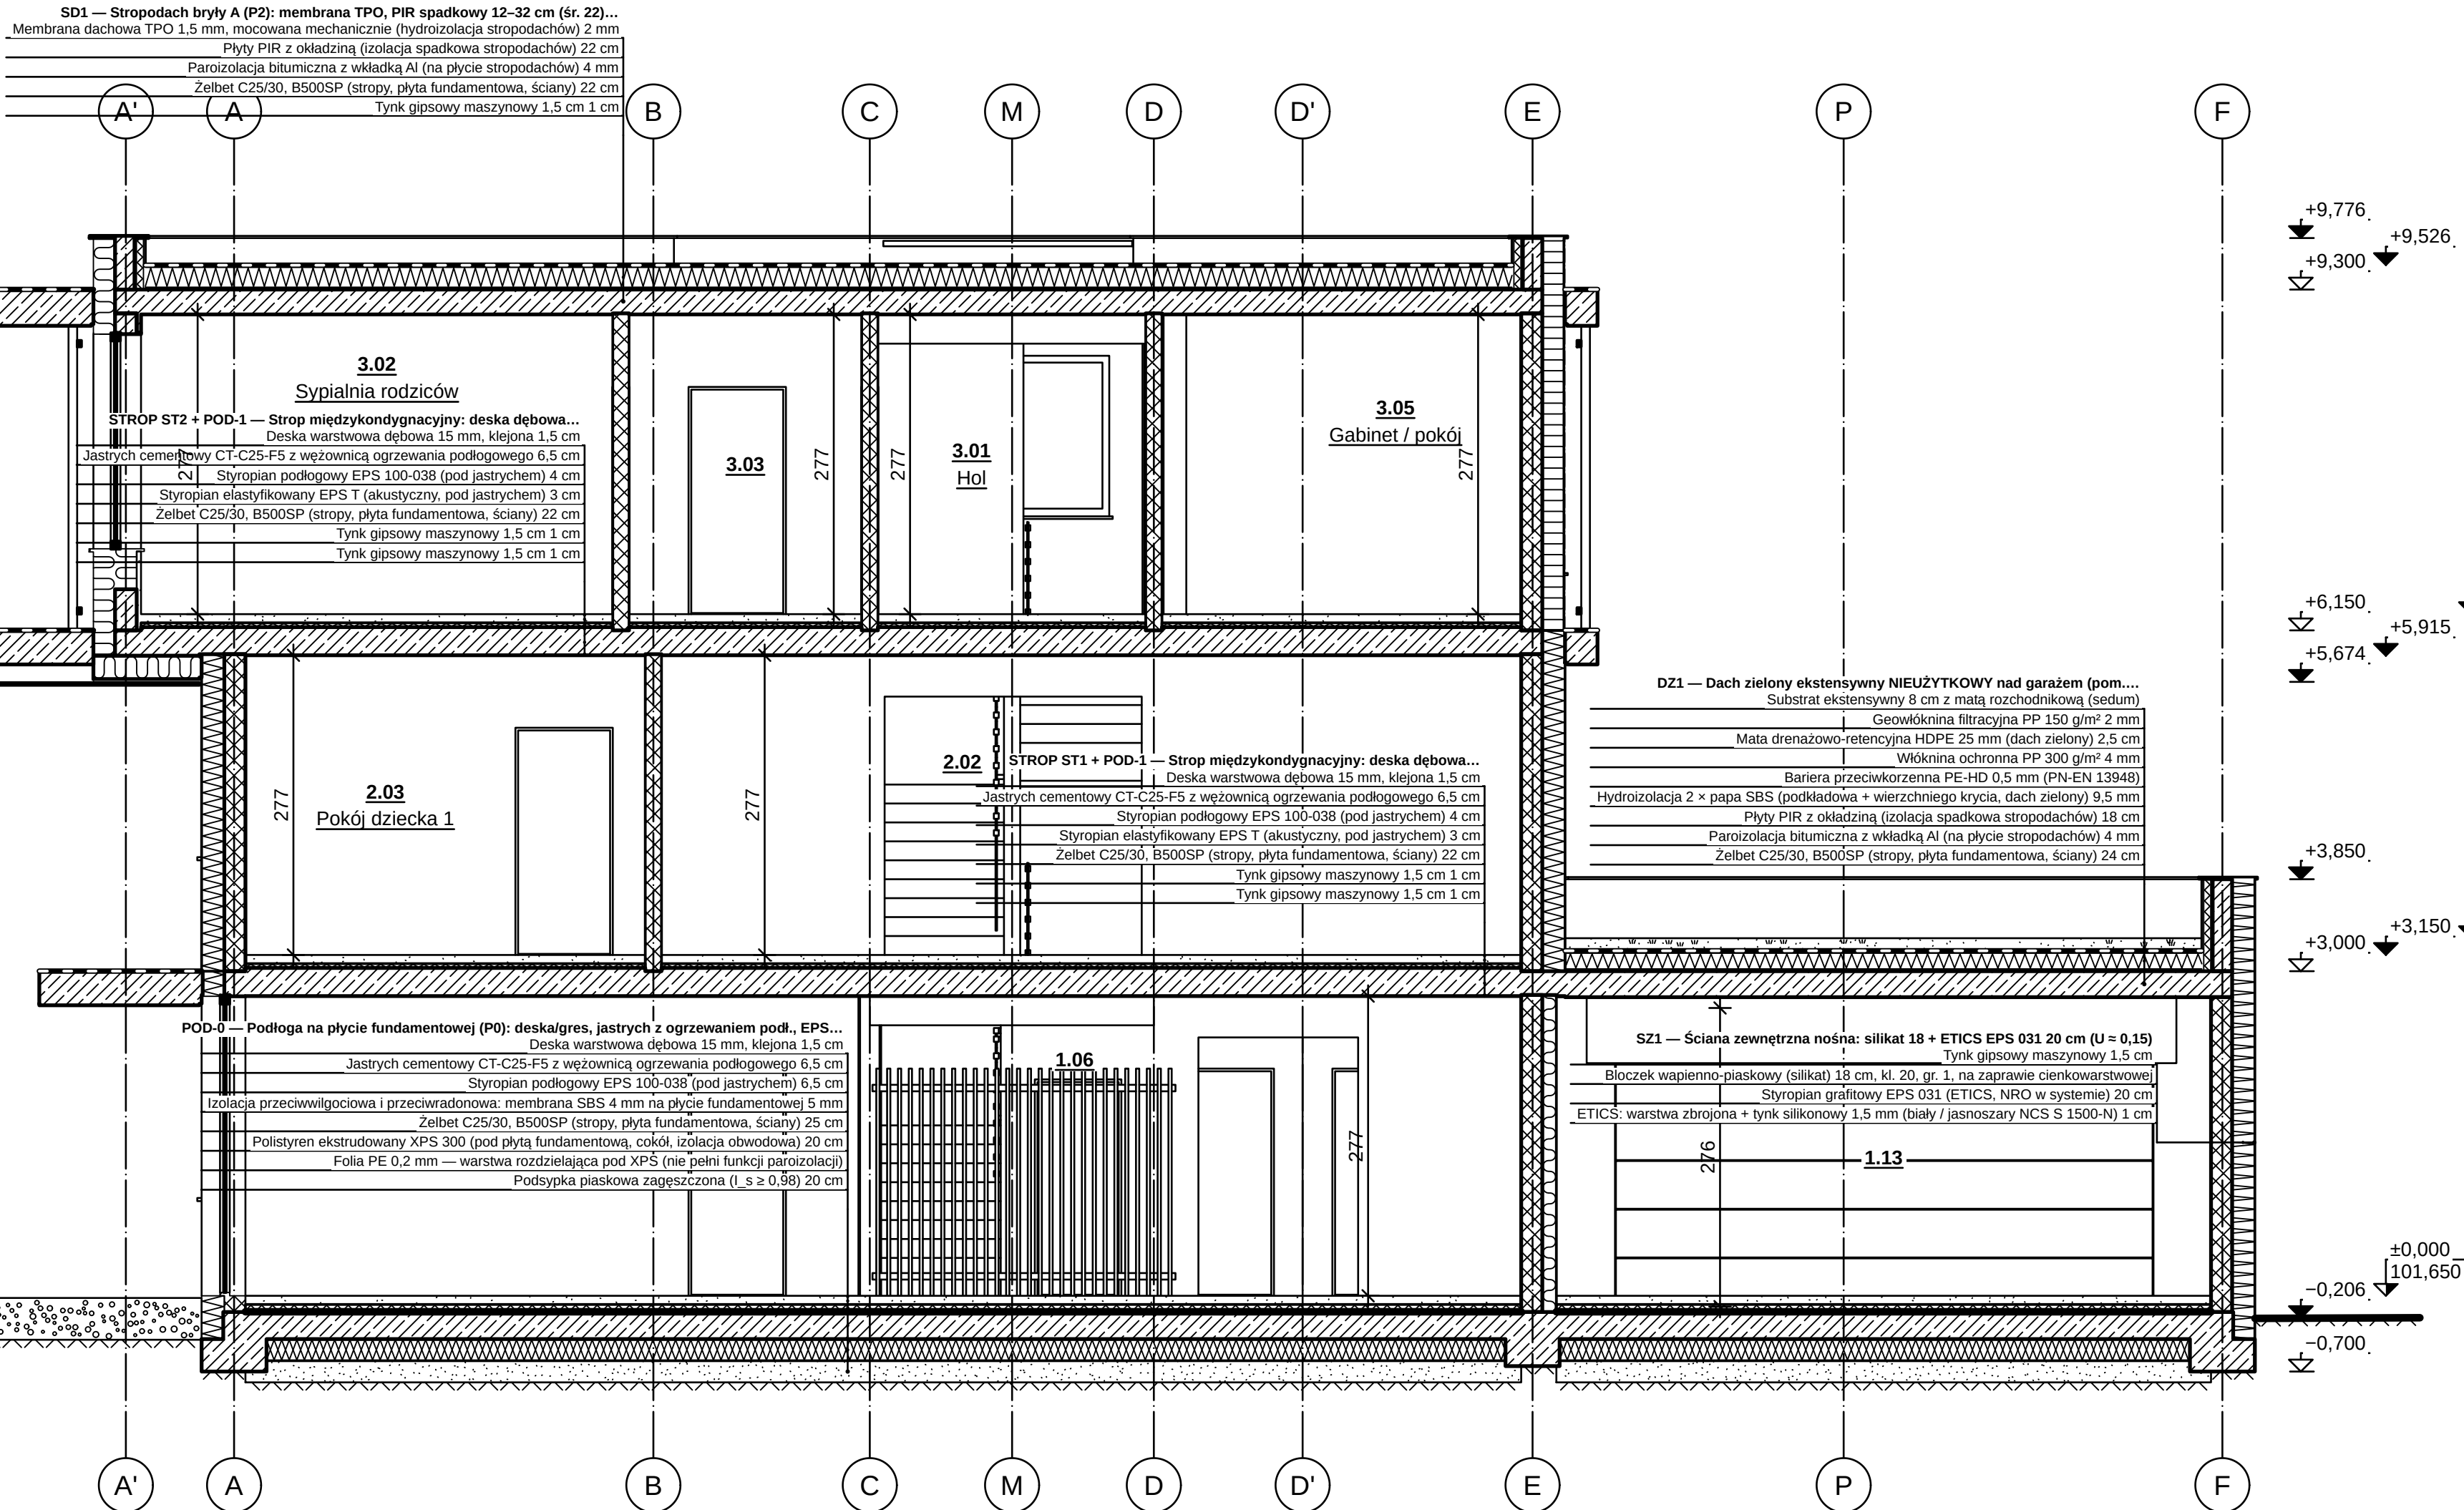


OZNACZENIA MATERIAŁÓW (PN-B-01030 + przyjęte)

	grunt rodzimy		Membrana fasadowa wiatroizolacyjna UV-stabilna, czarna (sd = 0,02 m)
	Substrat ekstensywny 8 cm z matą rozchodnikową (sedum)		Błoczek wapienno-piaskowy 12 cm, kl. 15 (ścianki działowe, licowy w kładce); Błoczek wapienno-piaskowy (silikat) 18 cm, kl. 20, gr. 1, na zaprawie cienkowarstwowej — krętka ułożona 45°/135°
	Welna mineralna 035 (szkielet, docieplenia, ściana dom-garaż); Welna mineralna fasadowa (elewacja wentylowana bryły A, A1) — meander „UUU”		Paroizolacja bitumiczna z wkładką Al (na płycie stropodachów) — linia kreskowa cienka 3/1 po ciepłej stronie
	Płyty PIR z okładziną (izolacja spadkowa stropodachów) — zygzak z okładzinami		Podsypka piaskowa zagęszczona (l _s ≥ 0,98)
	Izolacja przeciwwilgociowa i przeciwdrańowa: membrana SBS 4 mm na płycie fundamentowej — linia bardzo gruba		Płyta gipsowo-kartonowa 12,5 mm (GKB / GKBI w łazienkach); Podosufłoka zewnętrzna: płyta włóknocementowa 12 mm na ruszcie, RAL 7016
	Membrana dachowa TPO 1,5 mm, mocowana mechanicznie (hydroizolacja stropodachów); Hydroizolacja 2 × papa SBS (podkładowa + wierzchniego krycia, dach zielony) — pas czarno-biały		Obróbki blacharskie (blacha powlekana); Stalarka — profile aluminiowe, antracyt; Stal malowana proszkowo (balustrady, rygle) — zaczerpnienie
	Styropian grafitowy EPS 031 (ETICS, NRO w systemie); Styropian podłogowy EPS 100-038 (pod jastrychem); Styropian elastykowany EPS T (akustyczny, pod jastrychem) — zygzak „VVV”		Żelbet C25/30, B500SP (stropy, płyta fundamentowa, ściany); Żelbet C30/37 XC4/XF1 (krawędzie płyt wysuniętych, atyki, belki) — 45° na przemian ciągłe i przerywane
	Polistyren ekstrudowany XPS 300 (pod płytą fundamentową, cokół, izolacja obwodowa) — zygzak podwójny		Podbudowa nawierzchni (kruszywo)
	Jastrych cementowy CT-C25-F5 z węzownicą ogrzewania podłogowego — kropki		

OBJAŚNIENIA I UWAGI

- Wymiary w cm (mm w indeksie górnym, np. 24⁵ = 24,5 cm), rzędne w m względem ±0,000 = 101,650 m n.p.m. (PL-EVRF2007-NH).
- Rzędne: trójkąt zaczerpiony — poziom wykończenia, niezaczerpiony — konstrukcji, w pokoiwie zaczerpiony — poziom ±0,000 z rzędną bezwzględną (PN-B-01025).
- Wysokość budynku wg § 6 WT: od terenu przy najniższym wejściu (-0,267) do wierzchu stropodachu D1 (+9,526) — H = 9,79 m (bez atyki).
- Opisy warstw: kod i nazwa przegrody z modelu, materiały i grubości wg modelu (od góry / od lewej).
- Opisy warstw pominięte na rysunku (brak miejsca w podziale 1:50): STROP ST22 + POD-1, OK1 — układ warstw wg zestawienia przegród w części opisowej / przekroju 1:50.
- Rysunek wygenerowany automatycznie z modelu /home/user/aihouse/model/budynek.yaml (wersja 1.0, 2026-09-25) — generatory lamela.views.

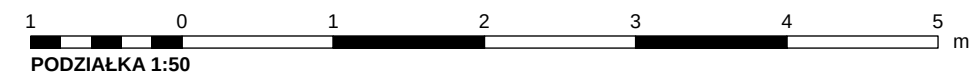

REW.	OPIS ZMIANY	DATA
0	Wydanie — rysunek wygenerowany z modelu	2026-09-25
PRACOWNIA PROJEKTOWA PRACOWNIA PROJEKTOWA — nazwa do uzupełnienia		STADIUM PB
adres pracowni do uzupełnienia		BRANZA ARCHITEKTURA (AR)
INWESTOR (do uzupełnienia)		
OBIEKT / NAZWA ZAMIERZENIA BUDOWLANEGO Budynek mieszkalny jednorodzinny wolnostojący „Dom LAMELA”		
ADRES / LOKALIZACJA (NR DZIAŁKI, OBRĘB, JEDN. EWIDENCYJNA) ul. Lipowa (fikcyjna), dz. nr ewid. 123/4, obręb 0005 Przykładowo, gm. Przykładowo (fikcyjna)		KAT. OBIEKTU I
FUNKCJA	IMIĘ I NAZWISKO	SPECJALNOŚĆ, NR UPRAWNIENI
Projektant		DATA
Projektant (wsp.)		PODPIS
Sprawdzający		
Opracował		
TYTUŁ RYSUNKU PRZEKRÓJ B-B		
SKALA 1:50	FORMAT A3×3	DATA WYDANIA 2026-09-25
RODZAJ DOK. przekrój	NR RYSUNKU PB-AR-06	ARKUSZ 6/10
REW. 0		




ELEWACJA POŁUDNIOWA 1:50

KOLORYSTYKA I MATERIAŁY ELEWACJI


1	ETICS: warstwa zbrojona + tynk silikonowy 1,5 mm (biały / jasnoszary NCS S 1500-N) [TYNK_SIL]	#f5f4f0
2	Szko (szyby zespolone) [SZKLO]	#a9c3cd
3	Membrana fasadowa wiatroizolacyjna UV-stabilna, czarna (sd = 0,02 m) [MEMB_WIATR]	#1d1d1d
4	Lamele elewacyjne 40×80 mm, drewno termojesion (klasa 1 trwałości), olejowane [DREWNO_TERMIO]	#9b6b41
5	Żelbet C30/37 XC4/XF1 (krawędzie płyt wysuniętych, atyki, belki) [ZB_C30]	#b4b1a9
6	Stolarka — profile aluminiowe, antracyt [RAMA_ALU]	#2b2f33
7	Rama boku C: ruszt stalowy ocynkowany w okładzinie z blachy aluminiowej RAL 7016 (pusta w środku) [RAMA_C]	#3b4044
8	Podbudowa nawierzchni (kruszywo) [NAW_PODBUDOWA]	#8d877d
9	Drzwi zewnętrzne, płycina aluminiowa [DRZWI_ZEWN]	#34383c
10	Stal malowana proszkowo (balustrady, rygle) [STAL_BAL]	#2c3034
11	Podsufitka zewnętrzna: płyta włóknocementowa 12 mm na ruszcie, RAL 7016 [PODSUF]	#474b4f
12	Obróbki blacharskie (blacha powlekana) [OBROBKA_BLACH]	#3b3f43
13	Deska tarasowa [NAW_DESKA]	#6d5847

OBJAŚNIENIA I UWAGI


- Wymiary w cm (mm w indeksie górnym, np. 24² = 24,5 cm), rzędne w m względem ±0,000 = 101,650 m n.p.m. (PL-EVRF2007-NH).
- Rzędne: trójkąt zaczerniony — poziom wykończenia, niezaczerniony — konstrukcji, w pokłowie zaczerniony — poziom ±0,000 z rzędną bezwzględną (PN-B-01025).
- Wysokość budynku wg § 6 WT: od terenu przy najniżej położonym wejściu (−0,267) do wierzchu stropodachu D1 (+9,526) — H = 9,79 m (bez attyk).
- Kolorystyka orientacyjna wg kolorów materiałów w modelu (do potwierdzenia wzornikiem RAL/NCS).
- Rysunek wygenerowany automatycznie z modelu /home/user/aihouse/model/budynek.yaml (wersja 1.0, 2026-09-25) — generatory lamela.views.

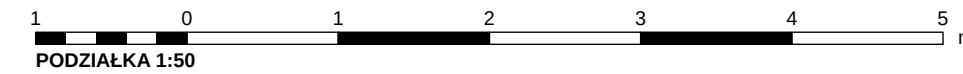

REW.	OPIS ZMIANY				DATA
0	Wydanie — rysunek wygenerowany z modelu				2026-09-25
PRACOWNIA PROJEKTOWA				STADIUM	BRANZA
PRACOWNIA PROJEKTOWA — nazwa do uzupełnienia				PB	ARCHITEKTURA (AR)
adres pracowni do uzupełnienia					
INWESTOR					
(do uzupełnienia)					
OBIEKT / NAZWA ZAMIERZENIA BUDOWLANEGO					
Budynek mieszkalny jednorodzinny wolnostojący „Dom LAMELA”					
ADRES / LOKALIZACJA (NR DZIAŁKI, OBREB, JEDN. EWIDENCYJNA)					KAT. OBIEKTU
ul. Lipowa (fikcyjna), dz. nr ewid. 123/4, obręb 0005 Przykładowo, gm. Przykładowo (fikcyjna)					I
FUNKCJA	IMIĘ I NAZWISKO		SPECJALNOŚĆ, NR UPRAWNIENI	DATA	PODPIS
Projektant					
Projektant (wsp.)					
Sprawdzający					
Opracował					
TYTUŁ RYSUNKU					
ELEWACJA POŁUDNIOWA (OGRODOWA)					
SKALA	FORMAT	DATA WYDANIA	RODZAJ DOK.	NR RYSUNKU	ARKUSZ
1:50	A3x3	2026-09-25	elewacja	PB-AR-07	7/10
					REW.
					0

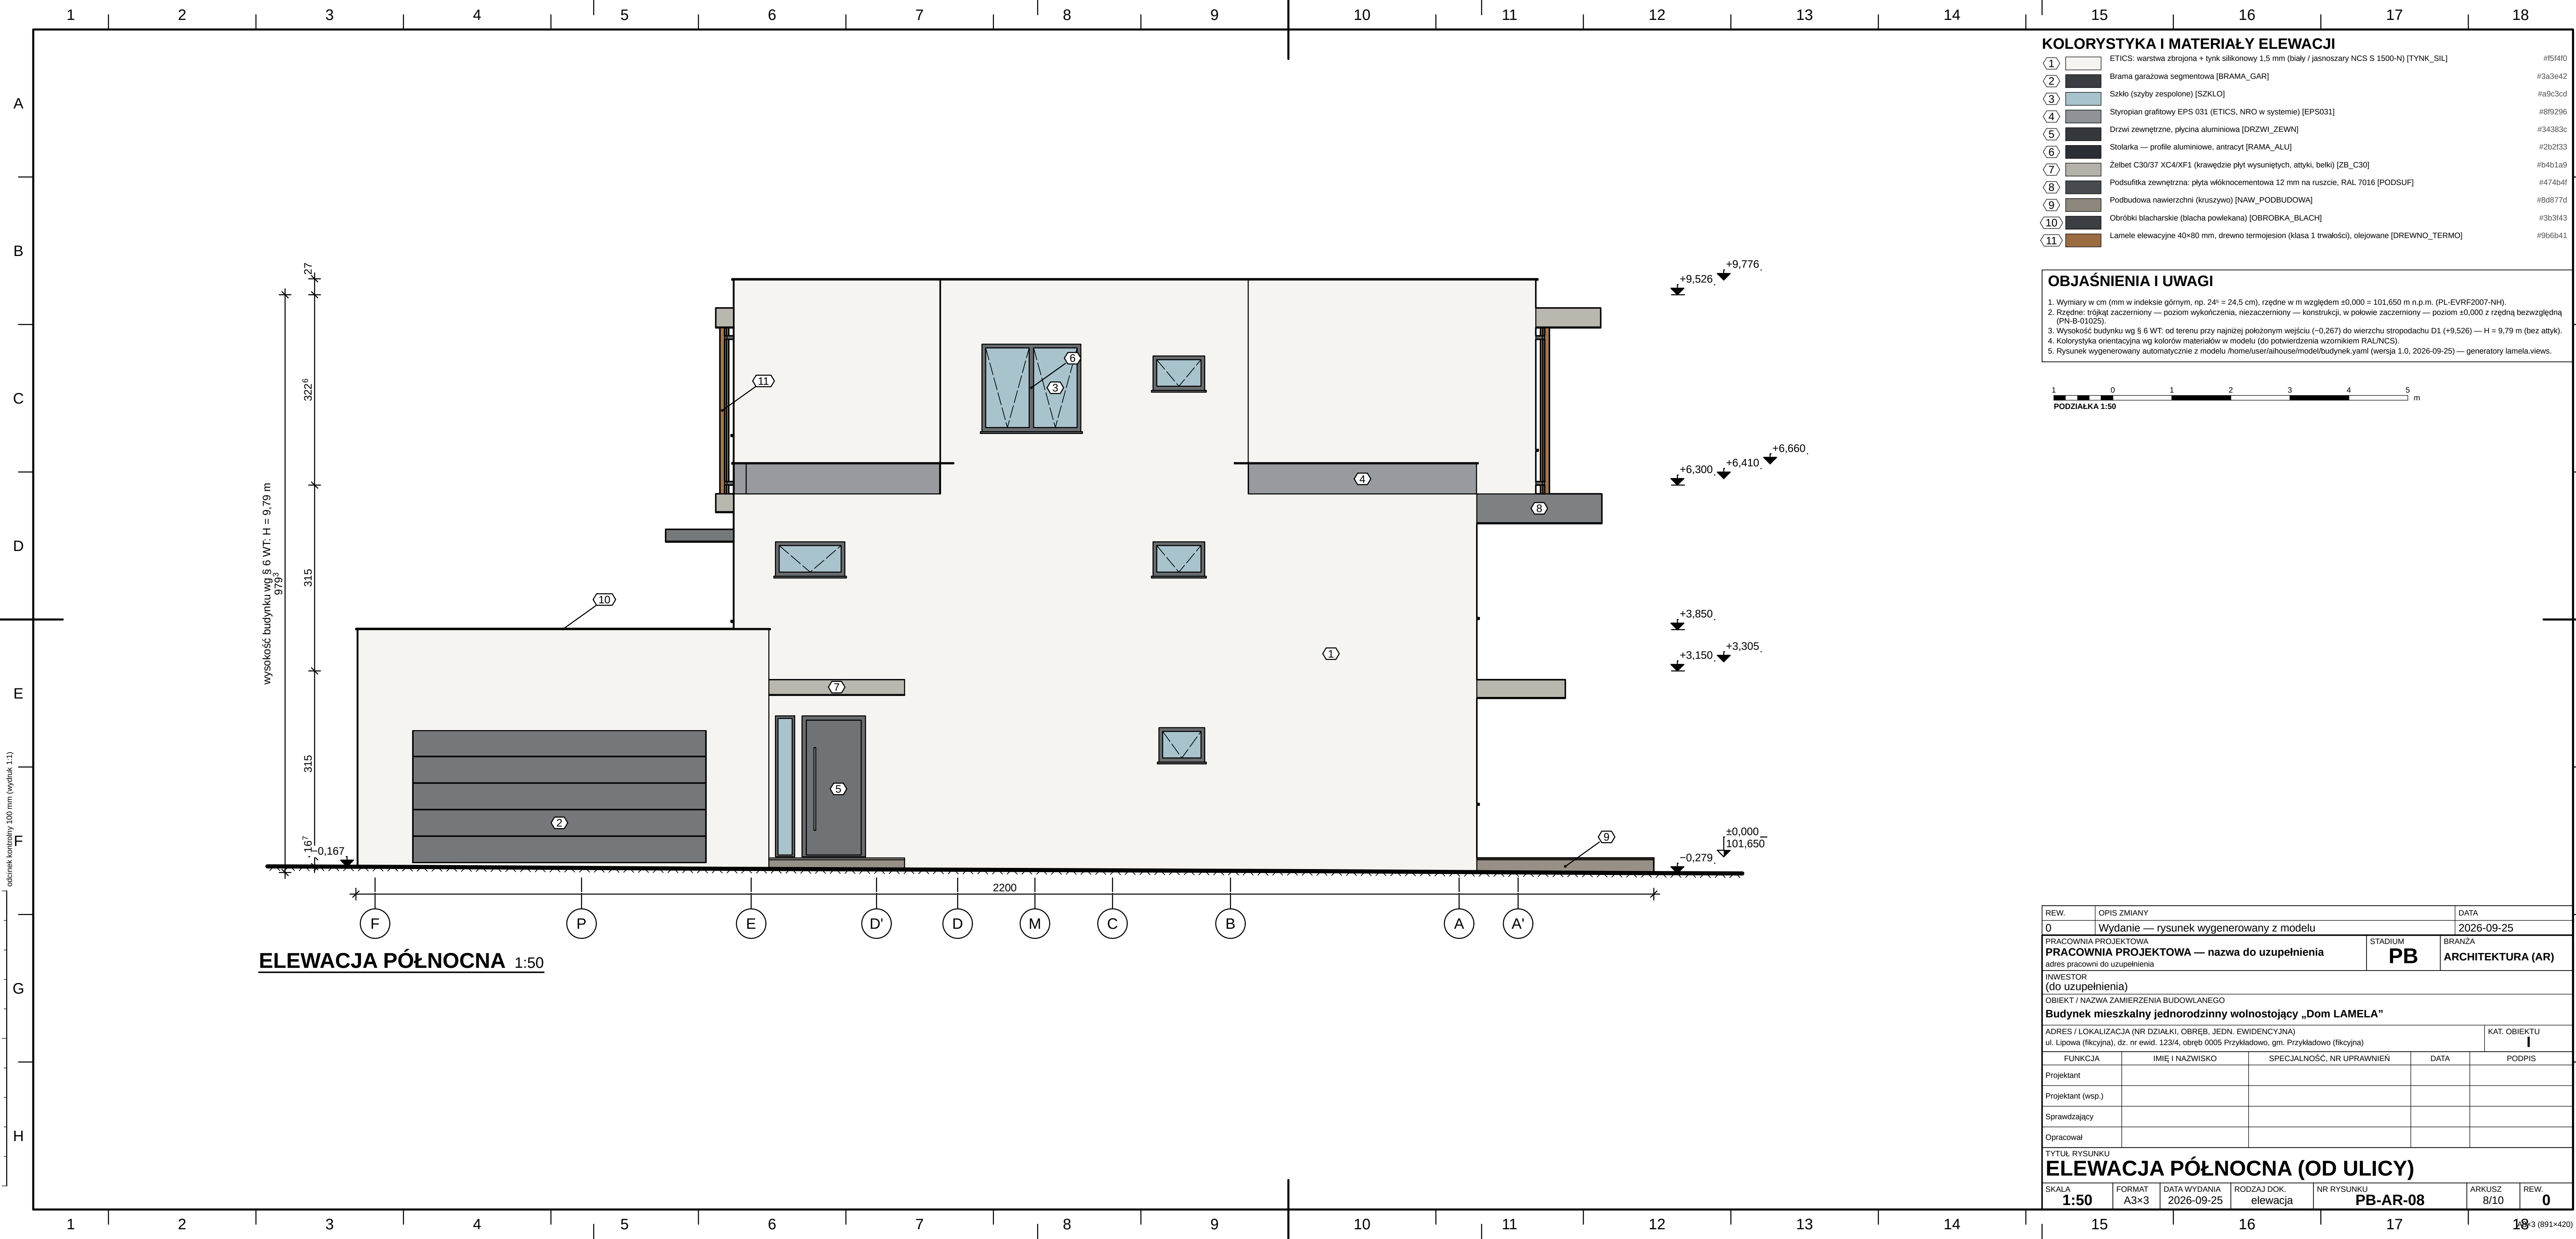

REW.	OPIS ZMIANY				DATA	
0	Wydanie — rysunek wygenerowany z modelu				2026-09-25	
PRACOWNIA PROJEKTOWA PRACOWNIA PROJEKTOWA — nazwa do uzupełnienia adres pracowni do uzupełnienia					STADIUM PB	BRANŻA ARCHITEKTURA (AR)
INWESTOR (do uzupełnienia)						
OBJEKT / NAZWA ZAMIERZENIA BUDOWLANEGO						
Budynek mieszkalny jednorodzinny wolnostojący „Dom LAMELA”						
ADRES / LOKALIZACJA (NR DZIAŁKI, OBRĘB, JEDN. EWIDENCYJNA) ul. Lipowa (fikcyjna), dz. nr ewid. 123/4, obręb 0005 Przykładowo, gm. Przykładowo (fikcyjna)					KAT. OBIEKTU I	
FUNKCJA	IMIĘ I NAZWISKO		SPECJALNOŚĆ, NR UPRAWNIENI		DATA	PODPIS
Projektant						
Projektant (wsp.)						
Sprawdzający						
Opracował						
TYTUŁ RYSUNKU						
ELEWACJA PÓŁNOCNA (OD ULICY)						
SKALA	FORMAT	DATA WYDANIA	RODZAJ DOK.	NR RYSUNKU	ARKUSZ	REW.
1:50	A3×3	2026-09-25	elewacja	PB-AR-08	8/10	0

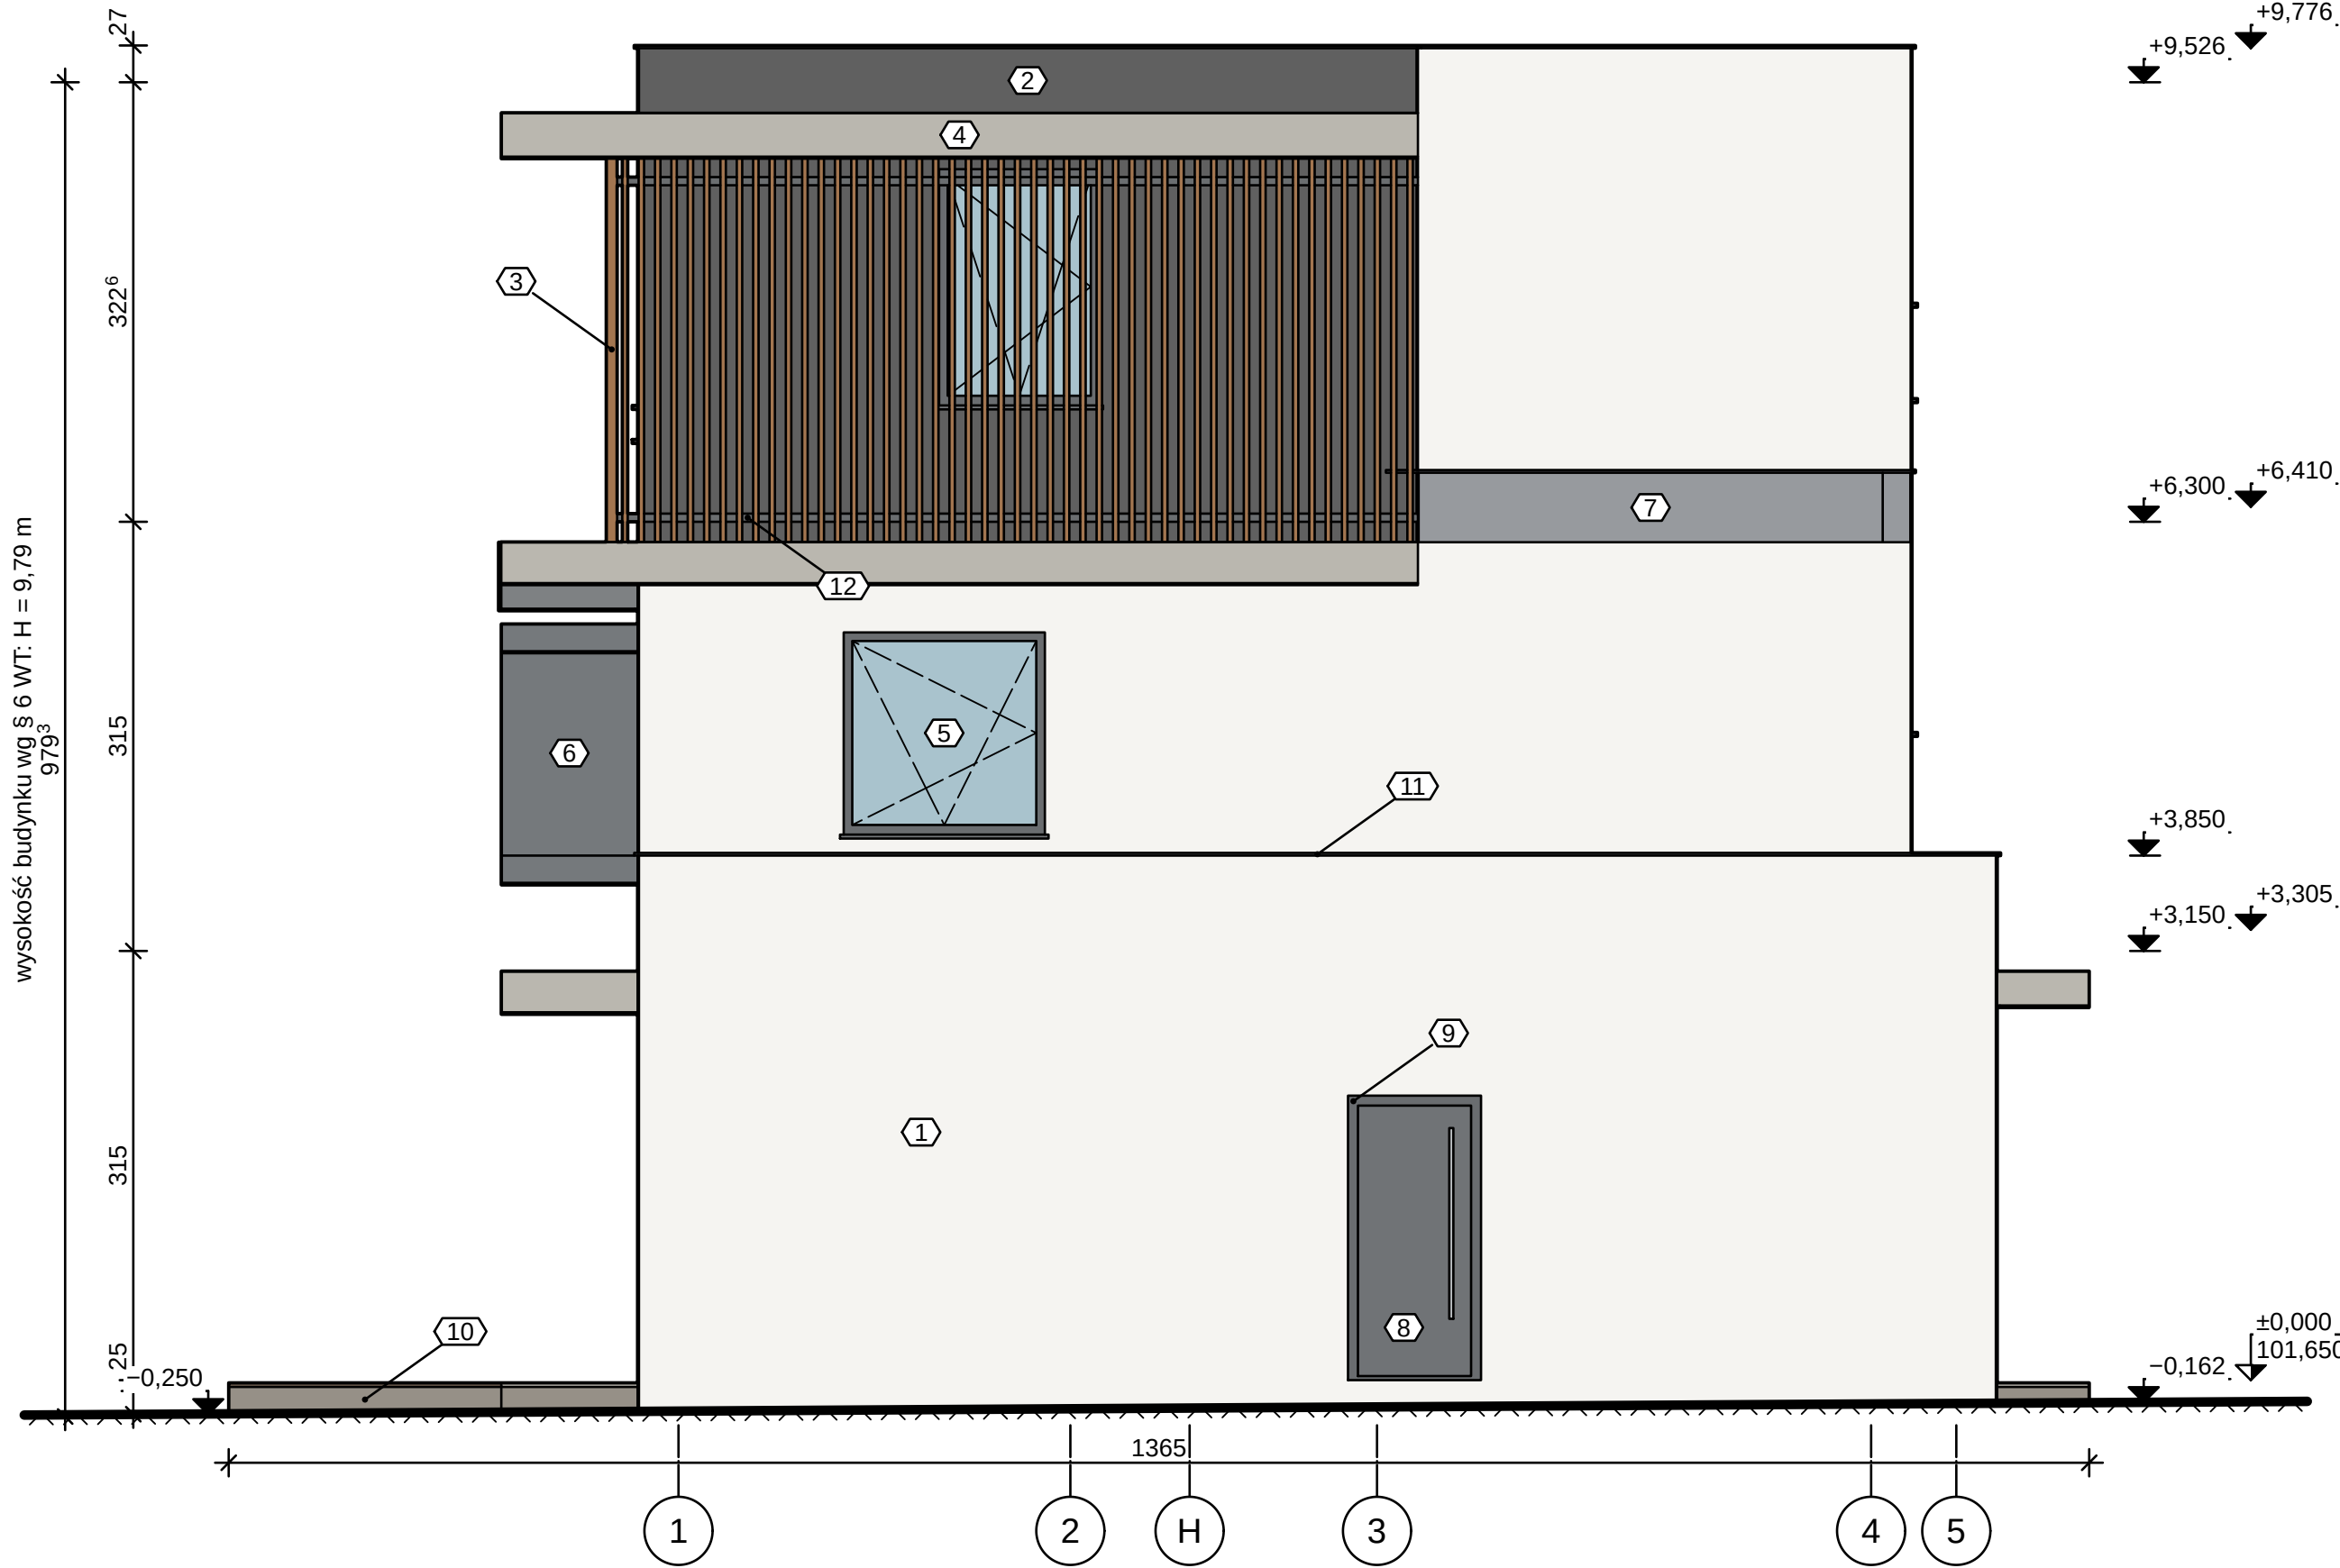


ELEWACJA WSCHODNIA 1:50

KOLORYSTYKA I MATERIAŁY ELEWACJI


1	ETICS: warstwa zbrojona + tynk silikonowy 1,5 mm (biały / jasnoszary NCS S 1500-N) [TYNK_SIL]	#f5f4f0
2	Membrana fasadowa wiatroizolacyjna UV-stabilna, czarna (sd ≈ 0,02 m) [MEMB_WIATR]	#1d1d1d
3	Lamele elewacyjne 40×80 mm, drewno termojesion (klasa 1 trwałości), olejowane [DREWNO_TERMO]	#9b6b41
4	Żelbet C30/37 XC4/XF1 (krawędzie płyt wysuniętych, atyki, belki) [ZB_C30]	#b4b1a9
5	Szkoło (szyby zespolone) [SZKLO]	#a9c3cd
6	Rama boku C: ruszt stalowy ocynkowany w okładzinie z blachy aluminiowej RAL 7016 (pusta w środku) [RAMA_C]	#3b4044
7	Styropian grafitowy EPS 031 (ETICS, NRO w systemie) [EPS031]	#8f9296
8	Drzwi zewnętrzne, płycina aluminiowa [DRZWI_ZEWN]	#34383c
9	Stołarka — profile aluminiowe, antracyt [RAMA_ALU]	#2b2f33
10	Podbudowa nawierzchni (kruszywo) [NAW_PODBUDOWA]	#8d877d
11	Obróbki blacharskie (blacha powlekana) [OBROBKA_BLACH]	#3b3f43
12	Stal malowana proszkowo (balustrady, rygle) [STAL_BAL]	#2c3034

OBJAŚNIENIA I UWAGI

- Wymiary w cm (mm w indeksie górnym, np. 24⁵ = 24,5 cm), rzędne w m względem ±0,000 = 101,650 m n.p.m. (PL-EVRF2007-NH).
- Rzędne: trójkąt zaczerwiony — poziom wykończenia, niezaczerwiony — konstrukcji, w połowie zaczerwiony — poziom ±0,000 z rzędną bezwzględną (PN-B-01025).
- Wysokość budynku wg § 6 WT: od terenu przy najniższym położonym wejściu (−0,267) do wierzchu stropodachu D1 (+9,526) — H = 9,79 m (bez atyki).
- Kolorystyka orientacyjna wg kolorów materiałów w modelu (do potwierdzenia wzornikiem RAL/NCS).
- Rysunek wygenerowany automatycznie z modelu /home/user/aihouse/model/budynek.yaml (wersja 1.0, 2026-09-25) — generatory lamela.views.

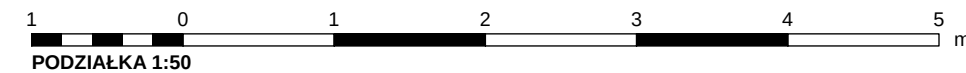

REW.	OPIS ZMIANY			DATA	
0	Wydanie — rysunek wygenerowany z modelu			2026-09-25	
PRACOWNIA PROJEKTOWA PRACOWNIA PROJEKTOWA — nazwa do uzupełnienia adres pracowni do uzupełnienia			STADIUM PB	BRANŻA ARCHITEKTURA (AR)	
INWESTOR (do uzupełnienia)					
OBIEKT / NAZWA ZAMIERZENIA BUDOWLANEGO Budynek mieszkalny jednorodzinny wolnostojący „Dom LAMELA”					
ADRES / LOKALIZACJA (NR DZIAŁKI, OBRĘB, JEDN. EWIDENCYJNA) ul. Lipowa (fikcyjna), dz. nr ewid. 123/4, obręb 0005 Przykładowo, gm. Przykładowo (fikcyjna)				KAT. OBIEKTU I	
FUNKCJA	IMIĘ I NAZWISKO		SPECJALNOŚĆ, NR UPRAWNIEŃ	DATA	PODPIS
Projektant					
Projektant (wsp.)					
Sprawdzający					
Opracował					
TYTUŁ RYSUNKU ELEWACJA WSCHODNIA					
SKALA 1:50	FORMAT A2	DATA WYDANIA 2026-09-25	RODZAJ DOK. elewacja	NR RYSUNKU PB-AR-09	ARKUSZ 9/10
					REW. 0

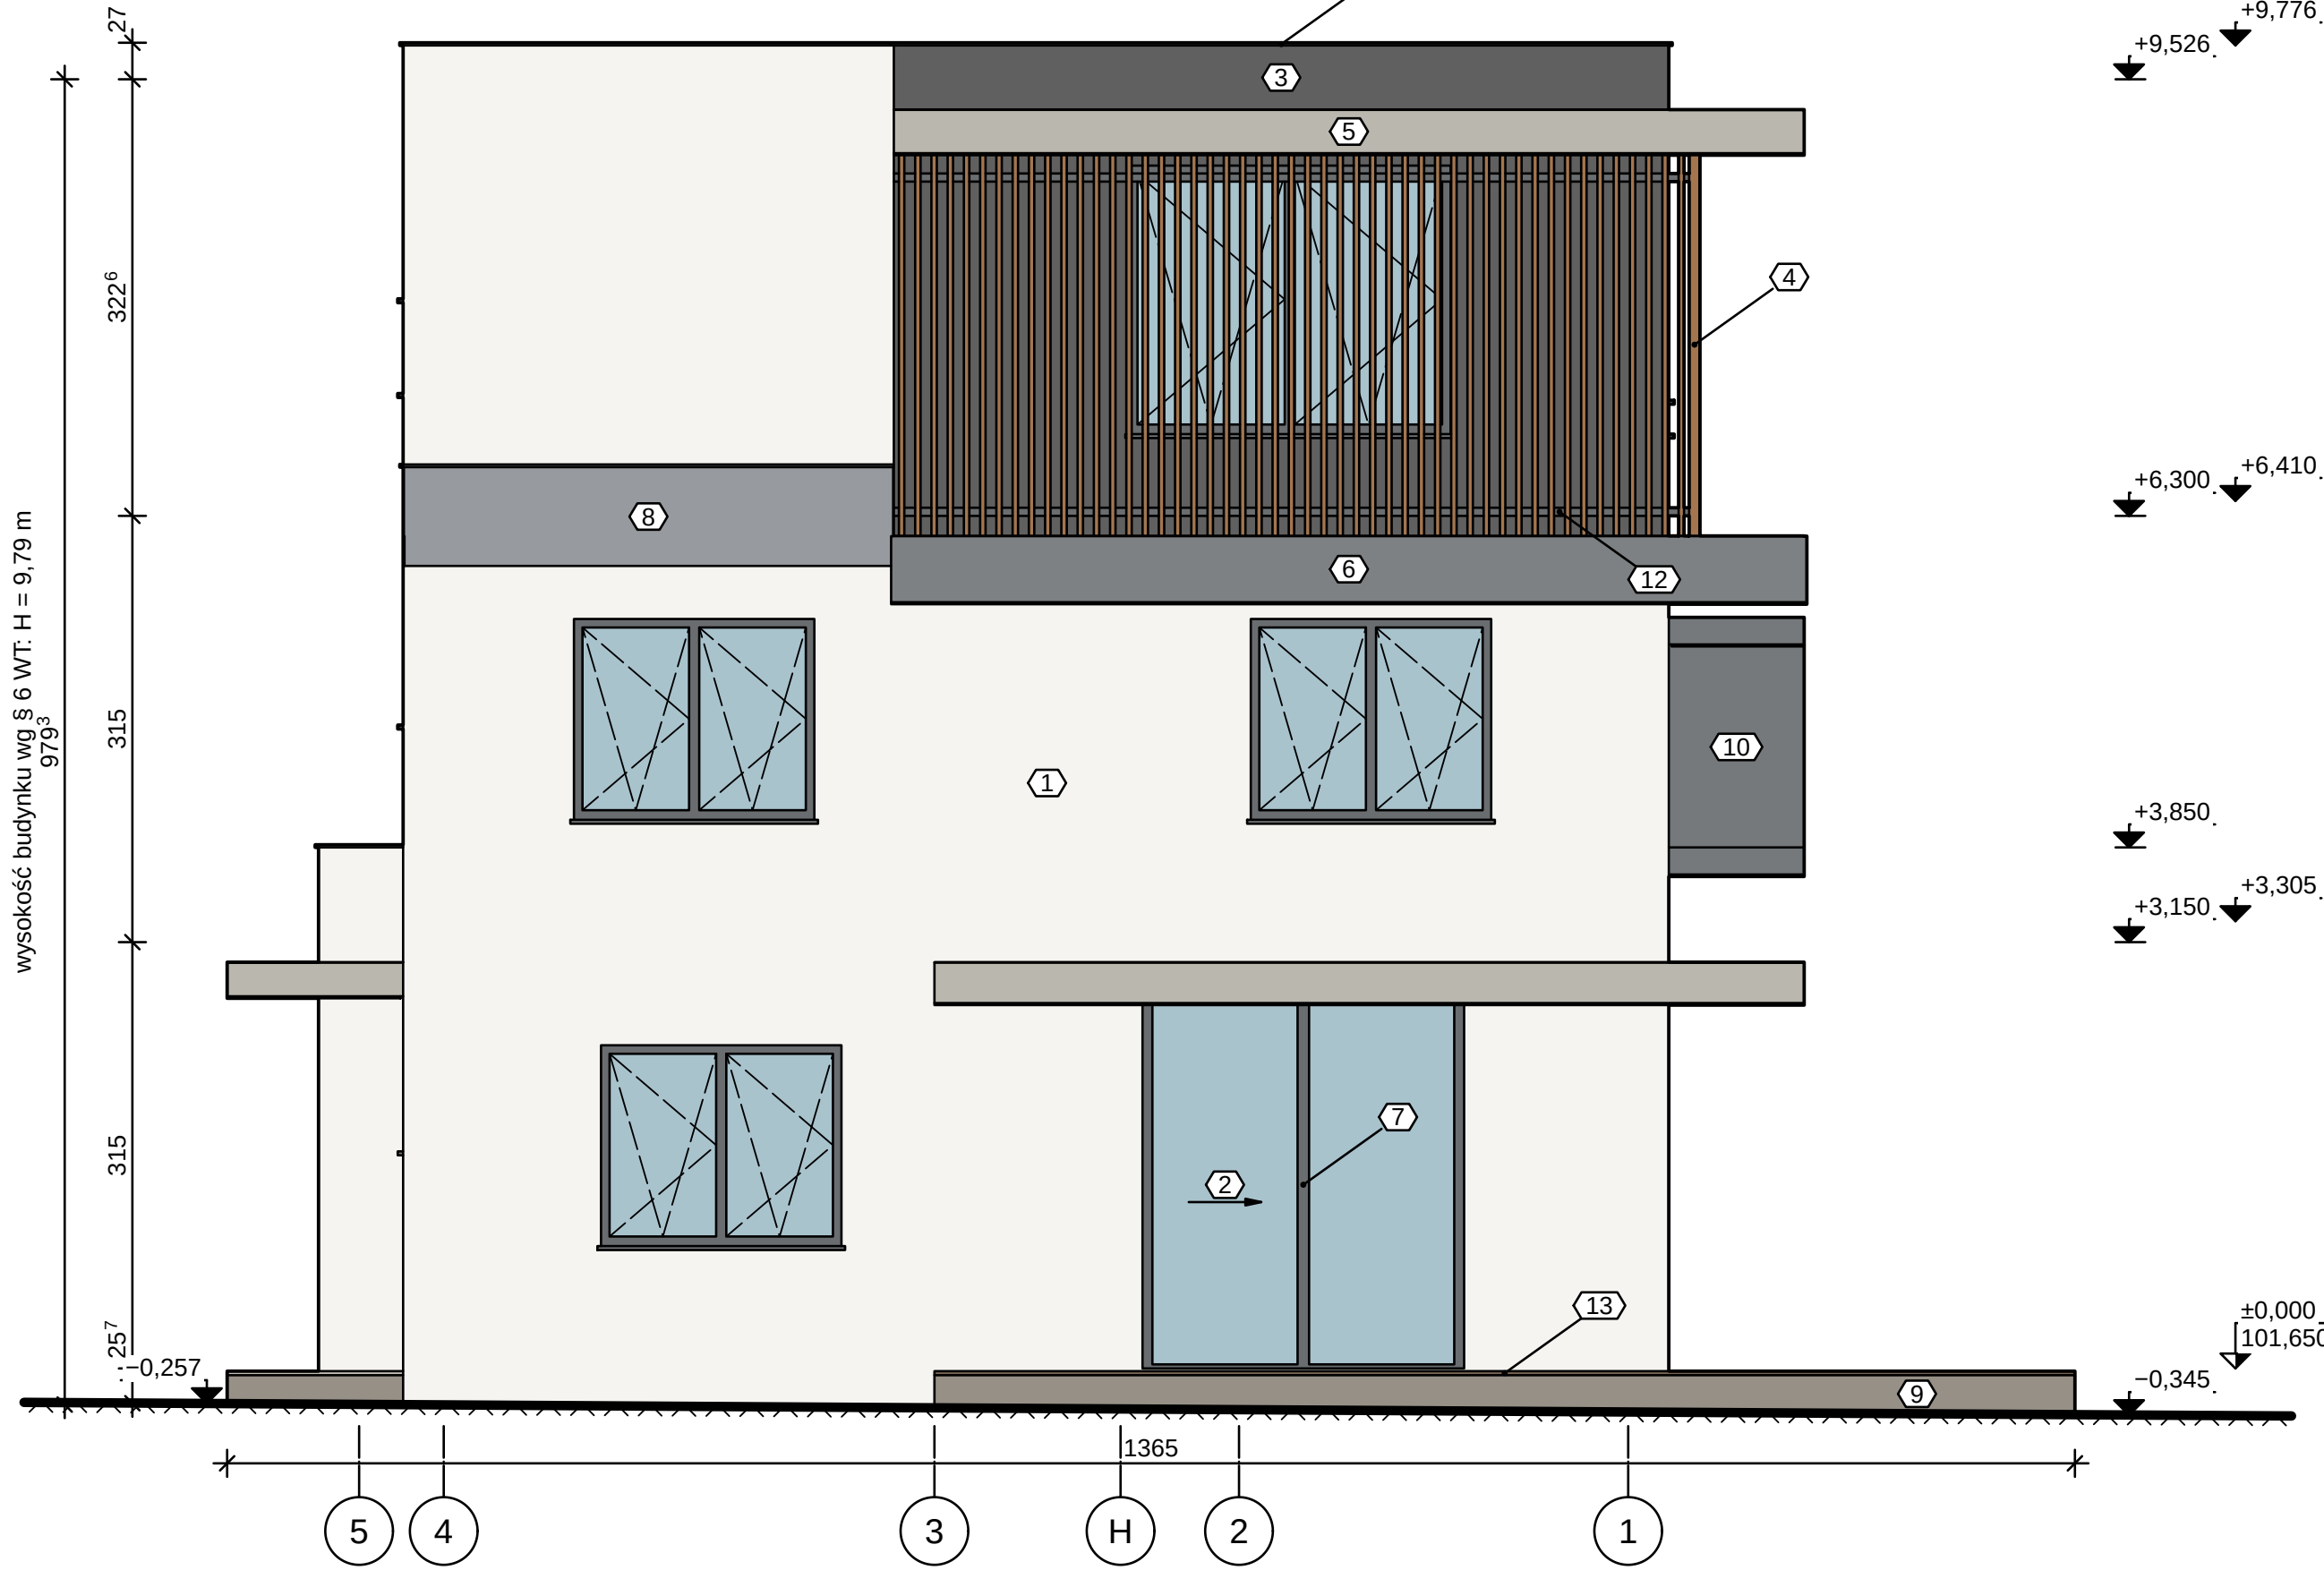


ELEWACJA ZACHODNIA 1:50

KOLORYSTYKA I MATERIAŁY ELEWACJI

1	ETICS: warstwa zbrojona + tynk silikonowy 1,5 mm (biały / jasnoszary NCS S 1500-N) [TYNK_SIL]	#f5f4f0
2	Szkoło (szyby zespolone) [SZKŁO]	#a9c3cd
3	Membrana fasadowa wiatroizolacyjna UV-stabilna, czarna (sd ≈ 0,02 m) [MEMB_WIATR]	#1d1d1d
4	Lamele elewacyjne 40×80 mm, drewno termojesion (klasa 1 trwałości), olejowane [DREWNO_TERMO]	#9b6b41
5	Żelbet C30/37 XC4/XF1 (krawędzie płyt wysuniętych, atyki, belki) [ZB_C30]	#b4b1a9
6	Podsufitka zewnętrzna: płyta włóknocementowa 12 mm na ruszcie, RAL 7016 [PODSUF]	#474b4f
7	Stołarka — profile aluminiowe, antracyt [RAMA_ALU]	#2b2f33
8	Styropian grafitowy EPS 031 (ETICS, NRO w systemie) [EPS031]	#8f9296
9	Podbudowa nawierzchni (kruszywo) [NAW_PODBUDOWA]	#8d877d
10	Rama boksu C: ruszt stalowy ocynkowany w okładzinie z blachy aluminiowej RAL 7016 (pusta w środku) [RAMA_C]	#3b4044
11	Obróbki blacharskie (blacha powlekana) [OBROBKA_BLACH]	#3b3f43
12	Stal malowana proszkowo (balustrady, rygle) [STAL_BAL]	#2c3034
13	Deska tarasowa [NAW_DESKA]	#6d5847

OBJAŚNIENIA I UWAGI

- Wymiary w cm (mm w indeksie górnym, np. 24⁵ = 24,5 cm), rzędne w m względem ±0,000 = 101,650 m n.p.m. (PL-EVRF2007-NH).
- Rzędne: trójkąt zaczerwiony — poziom wykończenia, niezaczerwiony — konstrukcji, w połowie zaczerwiony — poziom ±0,000 z rzędną bezwzględną (PN-B-01025).
- Wysokość budynku wg § 6 WT: od terenu przy najniższym położonym wejściu (-0,267) do wierzchu stropodachu D1 (+9,526) — H = 9,79 m (bez attyk).
- Kolorystyka orientacyjna wg kolorów materiałów w modelu (do potwierdzenia wzornikiem RAL/NCS).
- Rysunek wygenerowany automatycznie z modelu /home/user/aihouse/model/budynek.yaml (wersja 1.0, 2026-09-25) — generatory lamela.views.

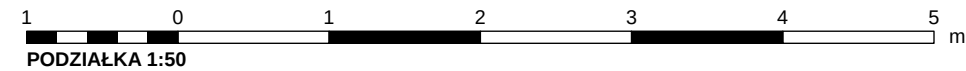

REW.	OPIS ZMIANY			DATA	
0	Wydanie — rysunek wygenerowany z modelu			2026-09-25	
PRACOWNIA PROJEKTOWA PRACOWNIA PROJEKTOWA — nazwa do uzupełnienia adres pracowni do uzupełnienia			STADIUM PB	BRANŻA ARCHITEKTURA (AR)	
INWESTOR (do uzupełnienia)					
OBIEKT / NAZWA ZAMIERZENIA BUDOWLANEGO Budynek mieszkalny jednorodzinny wolnostojący „Dom LAMELA”					
ADRES / LOKALIZACJA (NR DZIAŁKI, OBREB, JEDN. EWIDENCYJNA) ul. Lipowa (fikcyjna), dz. nr ewid. 123/4, obręb 0005 Przykładowo, gm. Przykładowo (fikcyjna)				KAT. OBIEKTU I	
FUNKCJA		IMIĘ I NAZWISKO	SPECJALNOŚĆ, NR UPRAWNIEŃ	DATA	PODPIS
Projektant					
Projektant (wsp.)					
Sprawdzający					
Opracował					
TYTUŁ RYSUNKU ELEWACJA ZACHODNIA					
SKALA 1:50	FORMAT A2	DATA WYDANIA 2026-09-25	RODZAJ DOK. elewacja	NR RYSUNKU PB-AR-10	ARKUSZ 10/10
					REW. 0