


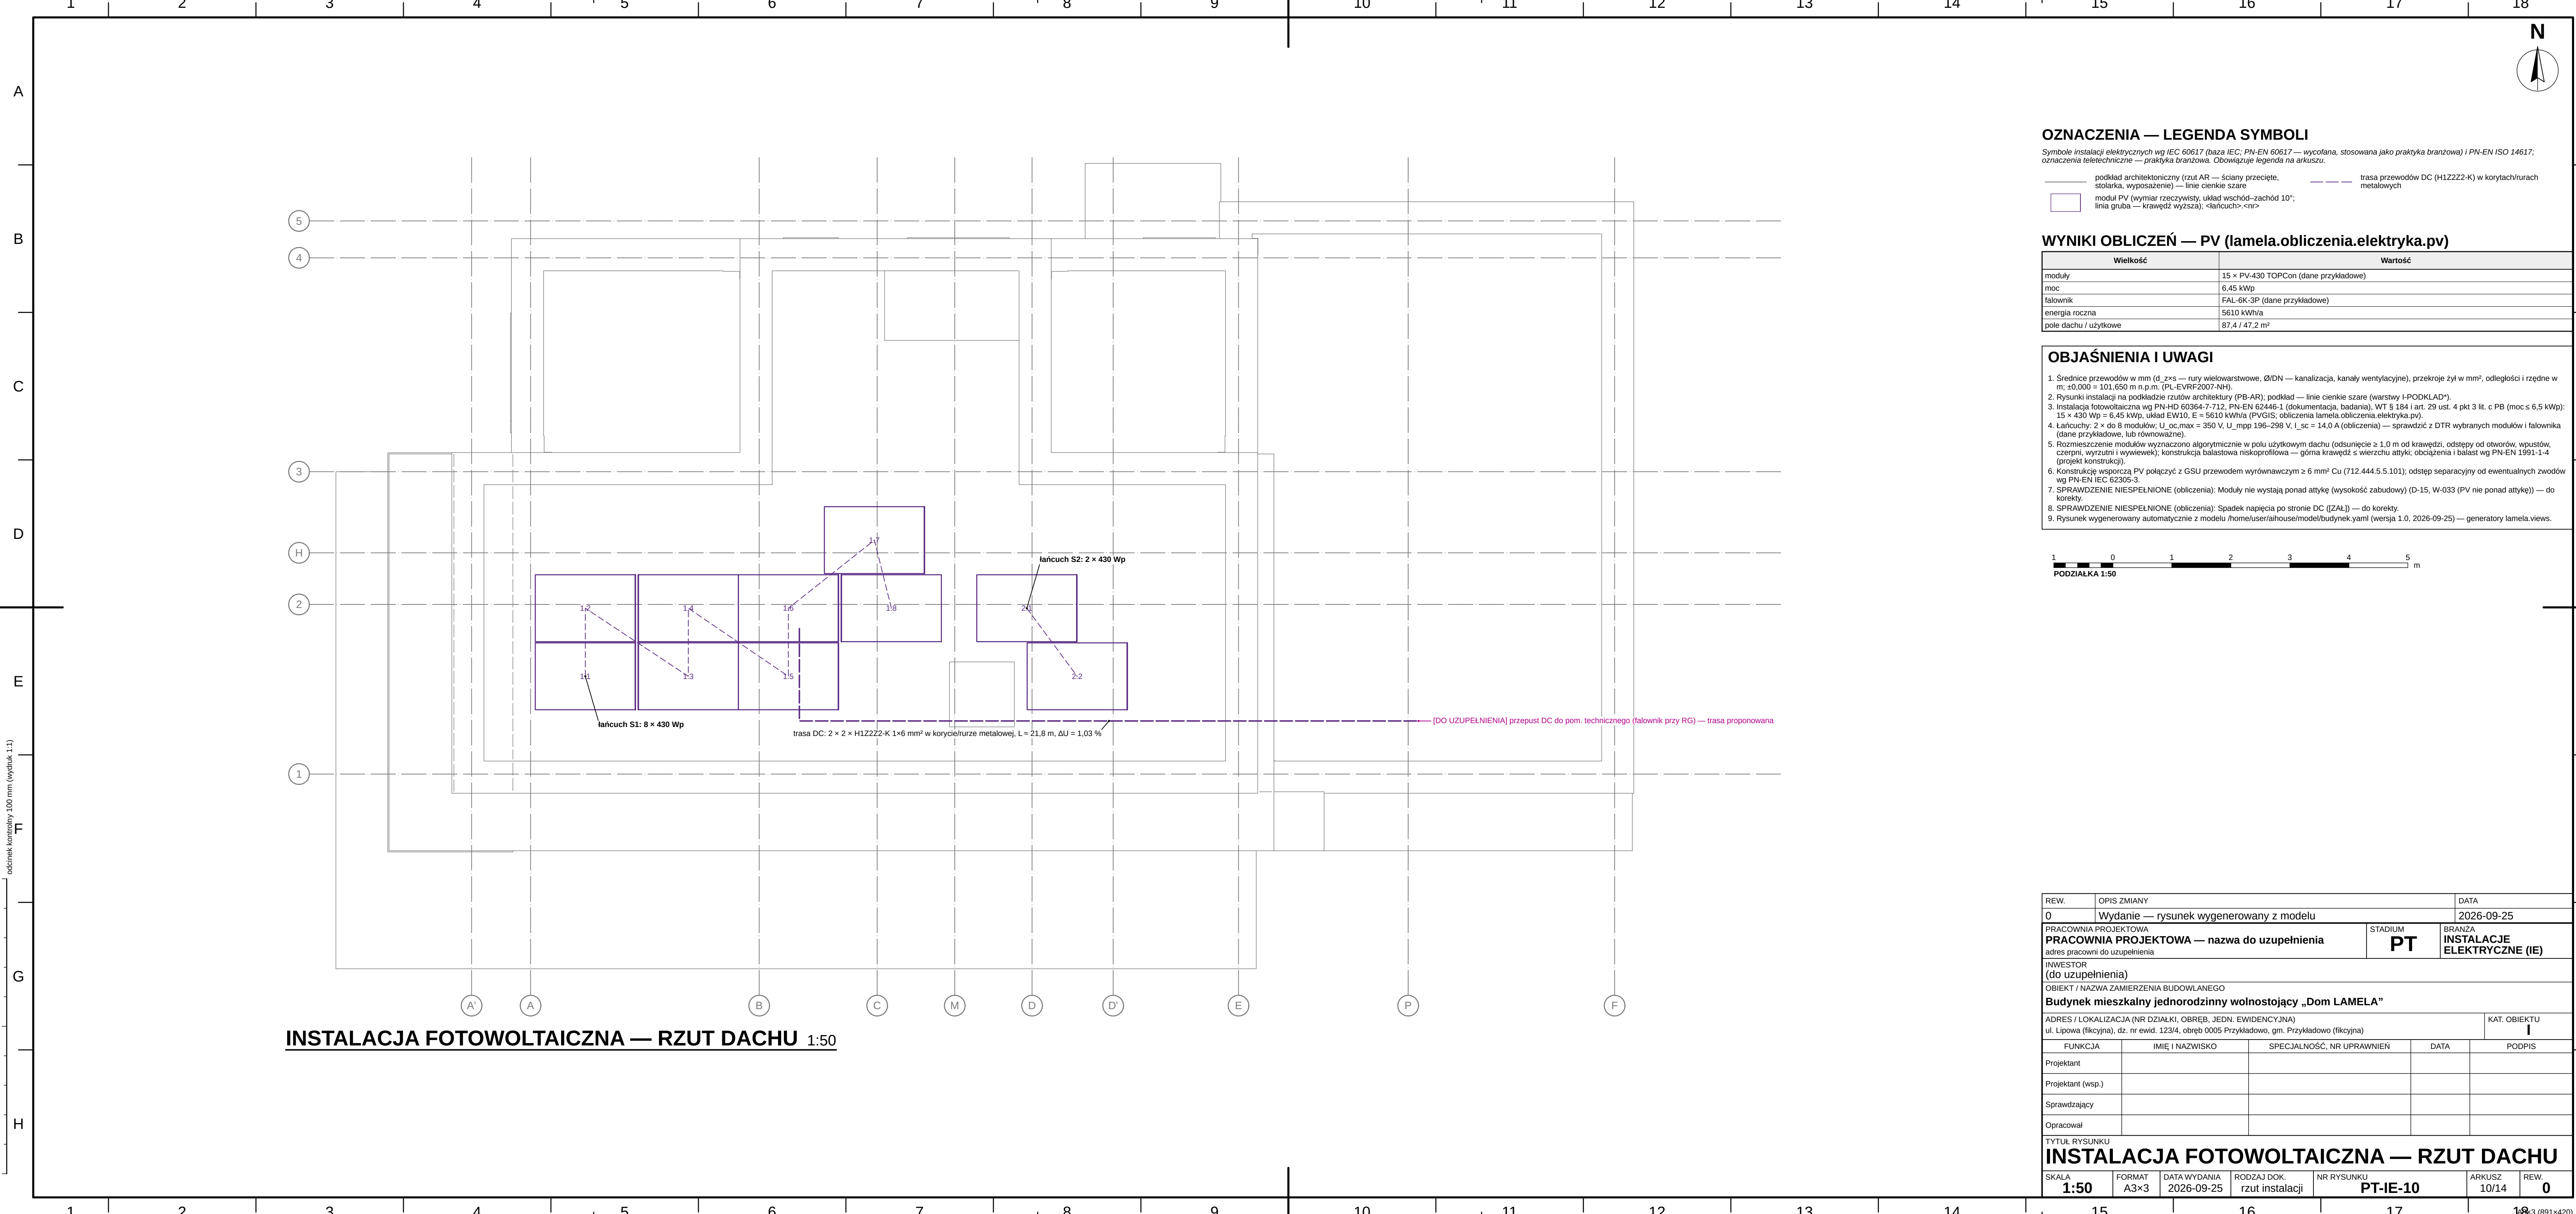

INSTALACJA FOTOWOLTAICZNA — RZUT DACHU 1:50

OZNACZENIA — LEGENDA SYMBOLI

Symboly instalacji elektrycznych wg IEC 60617 (baza IEC; PN-EN 60617 — wycofana, stosowana jako praktyka branżowa) i PN-EN ISO 14617; oznaczenia teletechniczne — praktyka branżowa. Obowiązuje legenda na arkuszu.


	podkład architektoniczny (rzut AR — ściany przecięcie, stolarka, wyposażenie)		trasa przewodów DC (H1ZZZ2-K) w korytach/rurach metalowych
	moduł PV (wymiar rzeczywisty, układ wschód–zachód 10°; linia gruba — krawędź wyższa); <łańcuch>.<nr>		

WYNIKI OBLICZEŃ — PV (lamela.obliczenia.elektryka.pv)

Wielkość	Wartość
moduły	15 × PV-430 TOPCon (dane przykładowe)
moc	6,45 kWp
falownik	FAL-6K-3P (dane przykładowe)
energia roczna	5610 kWh/a
pole dachu / użytkowe	87,4 / 47,2 m²

OBJAŚNIENIA I UWAGI

- Srednice przewodów w mm (d_z×s — rury wielowarstwowe, Ø/DN — kanalizacja, kanały wentylacyjne), przekroje żył w mm², odległości i rzędne w m; ±0,000 = 101,650 m n.p.m. (PL-EVRF2007-NH).
- Rysunki instalacji na podkładzie rzutów architektury (PB-AR); podkład — linie cienkie szare (warstwy I-PODKLAD*).
- Instalacja fotowoltaiczna wg PN-HD 60364-7-712, PN-EN 62446-1 (dokumentacja, badania), WT § 184 i art. 29 ust. 4 pkt 3 lit. c PB (moc ≤ 6,5 kWp); 15 × 430 Wp = 6,45 kWp, układ EW10, E = 5610 kWh/a (PVGIS; obliczenia lamela.obliczenia.elektryka.pv).
- Łańcuchy: 2 × do 8 modułów; U_oc,max = 350 V, U_mpp 196–298 V, I_sc = 14,0 A (obliczenia) — sprawdzić z DTR wybranych modułów i falownika (dane przykładowe, lub równoważne).
- Rozmieszczenie modułów wyznaczono algorytmicznie w polu użytkowym dachu (odsunięcie ≥ 1,0 m od krawędzi, odstęp od otworów, wypustów, czerpni, wyrzutni i wystawek); konstrukcja balastowa niskoprofilowa — górna krawędź s wierzchu attyki; obciążenia i balast wg PN-EN 1991-1-4 (projekt konstrukcji).
- Konstrukcję wsporcza PV połączyć z GSU przewodem wyrównawczym ≥ 6 mm² Cu (712.444.5.5.101); odstęp separacyjny od ewentualnych zwodów wg PN-EN IEC 62305-3.
- SPRAWDZENIE NIESPEŁNIONE (obliczenia): Moduły nie wystają ponad attykę (wysokość zabudowy) (D-15, W-033 (PV nie ponad attykę)) — do korekty.
- SPRAWDZENIE NIESPEŁNIONE (obliczenia): Spadek napięcia po stronie DC (IZAL) — do korekty.
- Rysunek wygenerowany automatycznie z modelu /home/user/ai/house/model/budynek.yaml (wersja 1.0, 2026-09-25) — generatory lamela.views.

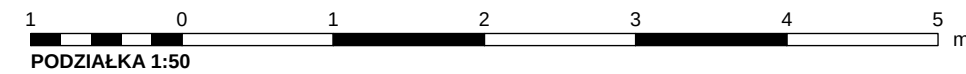

REW.		OPIS ZMIANY		DATA	
0		Wydanie — rysunek wygenerowany z modelu		2026-09-25	
PRACOWNIA PROJEKTOWA PRACOWNIA PROJEKTOWA — nazwa do uzupełnienia adres pracowni do uzupełnienia			STADIUM PT	BRANŻA INSTALACJE ELEKTRYCZNE (IE)	
INWESTOR (do uzupełnienia)					
OBIEKT / NAZWA ZAMIERZENIA BUDOWLANEGO Budynek mieszkalny jednorodzinny wolnostojący „Dom LAMELA”					
ADRES / LOKALIZACJA (NR DZIAŁKI, OBRĘB, JEDN. EWIDENCYJNA) ul. Lipowa (fikcyjna), dz. nr ewid. 123/4, obręb 0005 Przykładowo, gm. Przykładowo (fikcyjna)				KAT. OBIEKTU I	
FUNKCJA		IMIĘ I NAZWISKO		SPECJALNOŚĆ, NR UPRAWNIENI	DATA
Projektant					
Projektant (wsp.)					
Sprawdzający					
Opracował					
TYTUŁ RYSUNKU INSTALACJA FOTOWOLTAICZNA — RZUT DACHU					
SKALA 1:50	FORMAT A3×3	DATA WYDANIA 2026-09-25	RODZAJ DOK. rzut instalacji	NR RYSUNKU PT-IE-10	ARKUSZ 10/14
					REW. 0