


odcinek kontrolny 100 mm (wydruk 1:1)

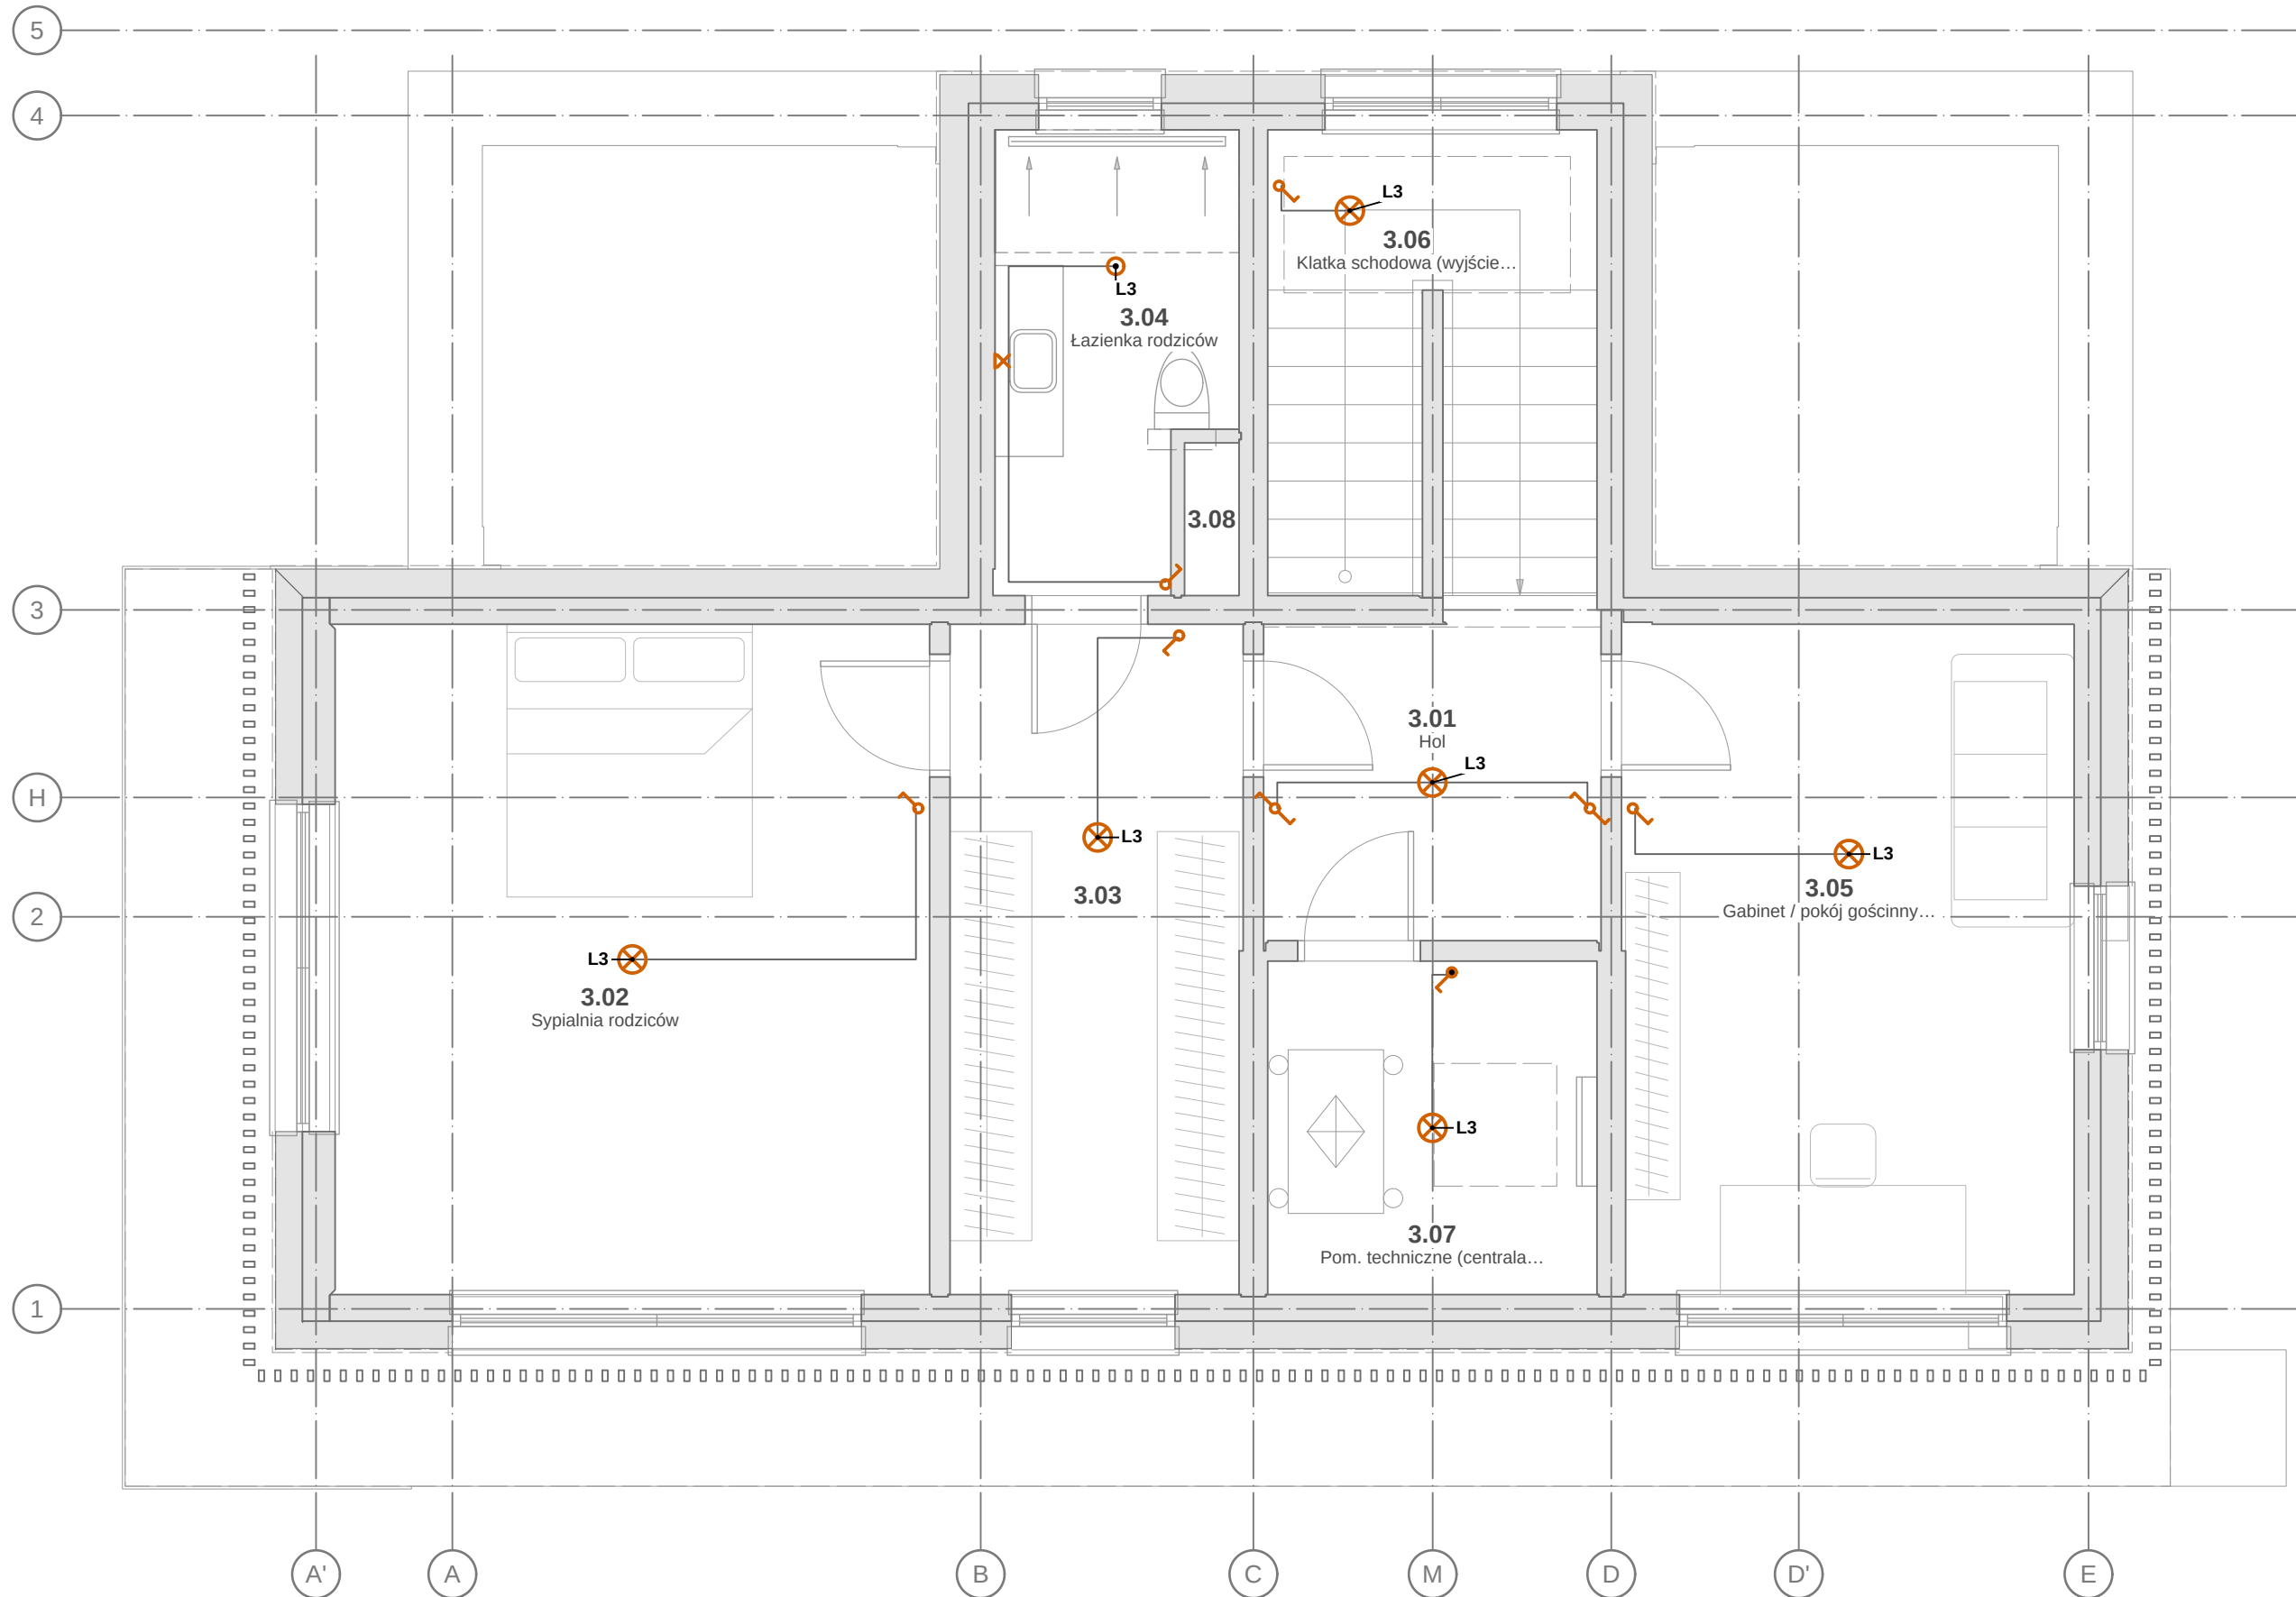

INSTALACJA OŚWIETLENIA — RZUT II PIĘTRA 1:50

OZNACZENIA — LEGENDA SYMBOLI

Symboly instalacji elektrycznych wg IEC 60617 (baza IEC; PN-EN 60617 — wycofana, stosowana jako praktyka branżowa) i PN-EN ISO 14617; oznaczenia teletechniczne — praktyka branżowa. Obowiązuje legenda na arkuszu.



	podkład architektoniczny (rzut AR — ściany przecięte, stolarka, wyposażenie) — linie cienkie szare		łącznik schodowy (przełącznik dwukierunkowy)
	przewody obwodów oświetlenia YDYp 3x1,5 / 4x1,5 (w tynku, w stropie) — połączenia punktów (przebieg schematyczny)		oprawa wpuszczana (downlight) IP44 — strefy łazienek wg PN-HD 60364-7-701
	oprawa oświetleniowa sufitowa (PN-EN 60617-11-15)		wypust / oprawa ścienna (kinkiet), nad lustrem IP44
	łącznik jednobiegunowy, h = 1,10 m (IP44 — zaczerniony)		

OBWODY NA ARKUSZU (lamela.obliczenia.elektryka.obwody)

Obw.	Odbiorniki	Zab.	Przewód	L [m]	ΔU [%]	Faza	RCD
L3	Oświetlenie P2	B10	YDYp 3x1,5	27,8	0,81	L3	RCBO typ A 30 mA

OBJAŚNIENIA I UWAGI

- Średnice przewodów w mm (d_zxs — rury wielowarstwowe, Ø/DN — kanalizacja, kanały wentylacyjne), przekroje żył w mm², odległości i rzędne w m; ±0,000 = 101,650 m n.p.m. (PL-EVRF2007-NH).
- Rysunki instalacji na podkładzie rzutów architektury (PB-AR); podkład — linie cienkie szare (warstwy I-PODKŁAD*).
- Instalacja oświetlenia wg PN-HD 60364 (seria), WT § 180–186 i § 64 (oświetlenie wejścia); natężenie oświetlenia wg PN-EN 12464-1 (wartości zalecane); obwody i zabezpieczenia z obliczeń (lamela.obliczenia.elektryka); wyłączniki nadprądowe B10, RCBO/RCD 30 mA.
- Rozmieszczenie opraw i łączników wyznaczono algorytmicznie (model nie zawiera punktów elektrycznych): oprawy w siatce ok. 3 m w obsrysie pomieszczenia, łączniki przy drzwiach od strony klamki 0,15 m od ościeżnicy na h = 1,10 m; typy opraw — do uzgodnienia z Inwestorem (projekt oświetlenia wnętrz).
- Przewody YDYp 3x1,5 (4x1,5 łączniki schodowe/świecznikowe) w tynku i w warstwach stropu, w strefach instalacyjnych; w łazienkach osprzęt poza strefami 0–1 wg PN-HD 60364-7-701, IP44 w strefie 2.
- Rysunek wygenerowany automatycznie z modelu model/budynek.yaml (wersja 1.0, 2026-09-25) — generatory lamela.views.

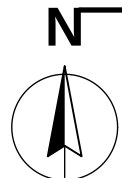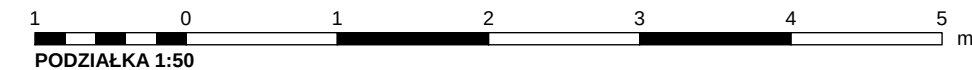

REW.	OPIS ZMIANY				DATA
0	Wydanie — rysunek wygenerowany z modelu				2026-09-25
PRACOWNIA PROJEKTOWA PRACOWNIA PROJEKTOWA — nazwa do uzupełnienia adres pracowni do uzupełnienia			STADIUM PT	BRANŻA INSTALACJE ELEKTRYCZNE (IE)	
INWESTOR (do uzupełnienia)					
OBIEKT / NAZWA ZAMIERZENIA BUDOWLANEGO Budynek mieszkalny jednorodzinny wolnostojący „Dom LAMELA”					
ADRES / LOKALIZACJA (NR DZIAŁKI, OBRĘB, JEDN. EWIDENCYJNA) ul. Lipowa (fikcyjna), dz. nr ewid. 123/4, obręb 0005 Przykładowo, gm. Przykładowo (fikcyjna)					KAT. OBIEKTU I
FUNKCJA	IMIĘ I NAZWISKO		SPECJALNOŚĆ, NR UPRAWNIEN	DATA	PODPIS
Projektant	[DO UZUPEŁNIENIA]		[DO UZUPEŁNIENIA]		
Projektant (wsp.)	[DO UZUPEŁNIENIA]		[DO UZUPEŁNIENIA]		
Sprawdzający	nie dotyczy (art. 20 ust. 3 pkt 2 PB)		—		
Opracował	[DO UZUPEŁNIENIA]		[DO UZUPEŁNIENIA]		
TYTUŁ RYSUNKU INSTALACJA OŚWIETLENIA — RZUT II PIĘTRA					
SKALA 1:50	FORMAT 690×297	DATA WYDANIA 2026-09-25	RODZAJ DOK. rzut instalacji	NR RYSUNKU PT-IE-03	ARKUSZ 3/14
					REW. 0