


TOM RYSUNKÓW ARCHITEKTURY — WIDOKI Z MOD

Lp.	Nr rys.	Tytuł rysunku	Skala	Format
1	PB-AR-01	RZUT PARTERU	1:50	630×594
2	PB-AR-02	RZUT I PIĘTRA	1:50	770×420
3	PB-AR-03	RZUT II PIĘTRA I RZUT DACHU	1:50	590×891
4	PB-AR-04	PRZEKROJE A-A I B-B	1:50	1130×420
5	PB-AR-05	ELEWACJE	1:50	2050×297

PRACOWNIA PROJEKTOWA PRACOWNIA PROJEKTOWA — nazwa do uzupełnienia		STADIUM PB	BRANŻA ARCHITEKTURA (AR)			
INWESTOR (do uzupełnienia)						
OBIEKT / NAZWA ZAMIERZENIA BUDOWLANEGO Budynek mieszkalny jednorodzinny wolnostojący „Dom LAMELA”						
ADRES / LOKALIZACJA (NR DZIAŁKI, OBRĘB, JEDN. EWIDENCYJNA) ul. Lipowa (fikcyjna), dz. nr ewid. 123/4, obręb 0005 Przykładowo, gm. Przykładowo (fikcyjna)				KAT. OBIEKTU I		
FUNKCJA	IMIĘ I NAZWISKO	SPECJALNOŚĆ, NR UPRAWNIENI	DATA	PODPIS		
Projektant						
Projektant (wsp.)						
Sprawdzający						
Opracował						
TYTUŁ RYSUNKU SPIS RYSUNKÓW						
SKALA —	FORMAT A4	DATA WYDANIA 2026-09-25	RODZAJ DOK. spis	NR RYSUNKU PB-AR-00	ARKUSZ —	REW.

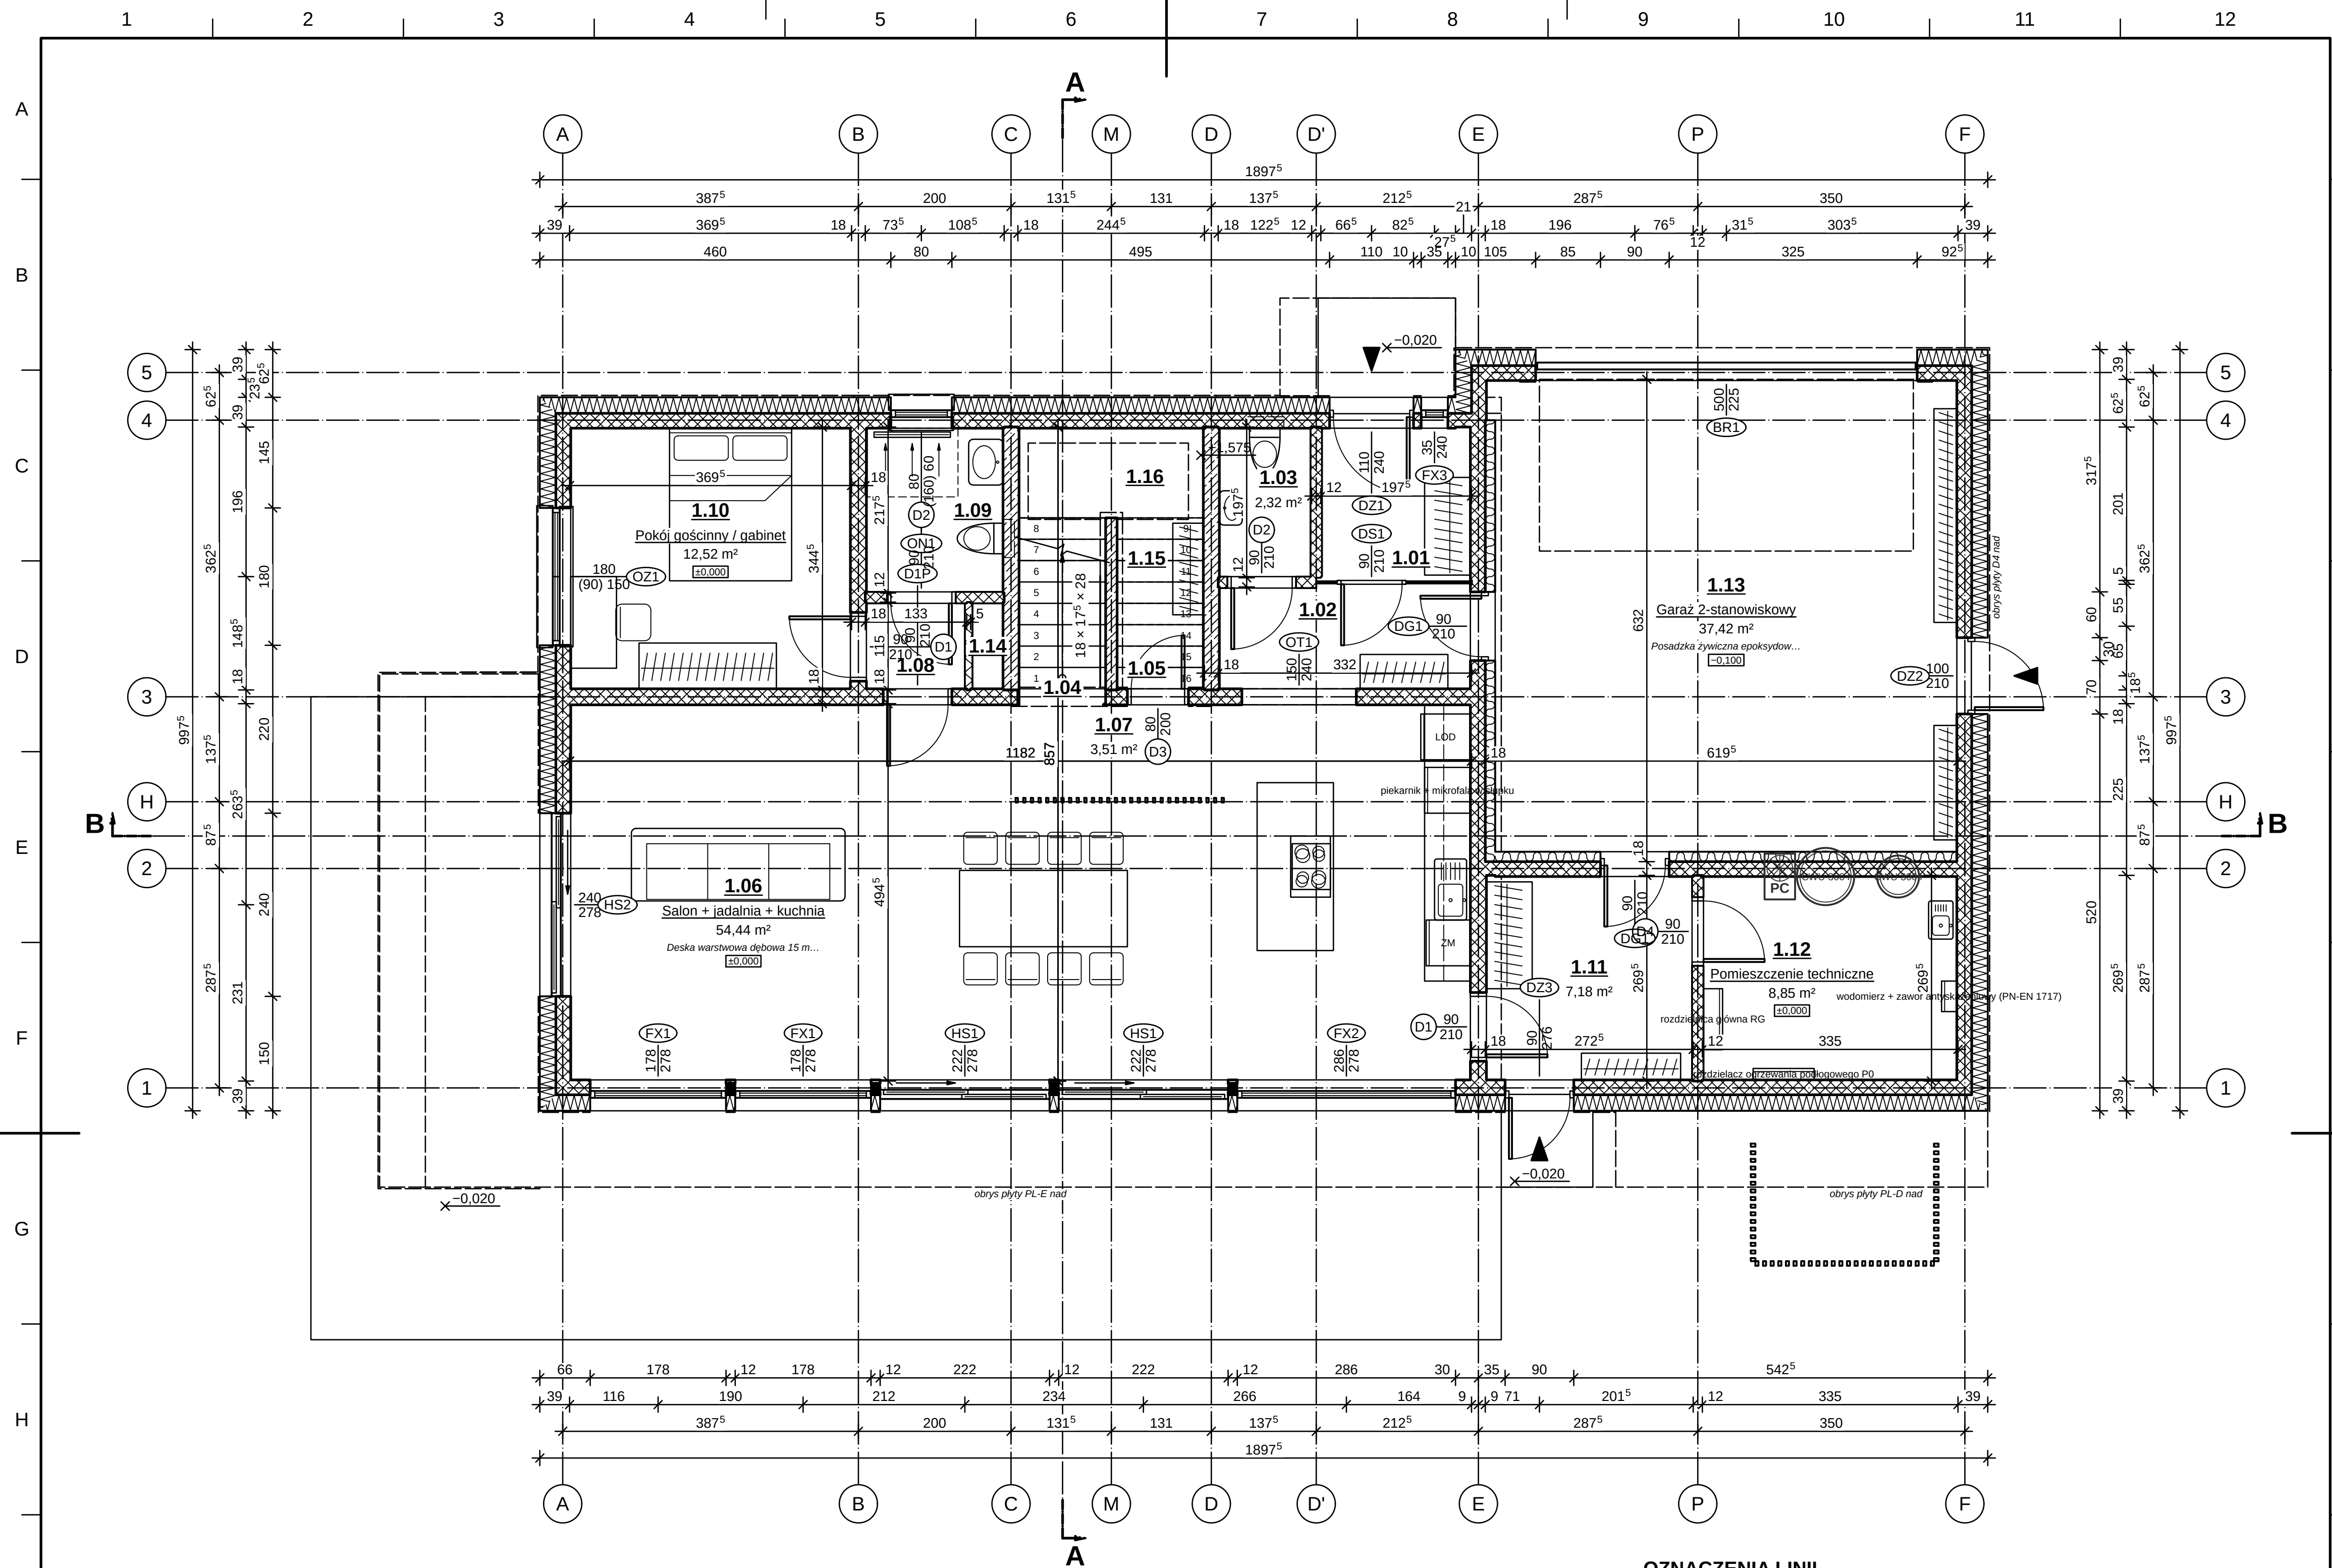

RZUT PARTERU 1:50

- OBJAŚNIENIA I UWAGI**
- Wymiary w cm (mm w indeksie górnym, np. 24⁵ = 24,5 cm), rzędne w m względem ±0,000 = 101,650 m n.p.m. (PL-EVREF2007-NH).
 - Rzuty: płaszczyzna cięcia +1,10 m nad posadzką kondygnacji. Linia kreskową — elementy nad płaszczyzną cięcia (obrysy płyt i wsporników, brył wyższych kondygnacji), otwory w stropie nad, belki); linią cieniłą — elementy poniżej (widok).
 - Otwory: licznik — szerokość, mianownik — wysokość w świetle muru, w nawiasie wysokość parapetu; symbol stolarki wg zestawienia stolarki.
 - Numeracja pomieszczeń wg PN-B-01025 / PN-EN ISO 4157-2: <nr kondygnacji (parter = 1)> <nr>; identyfikator w modelu: <kond> <nr> (parter = 0).
 - Drzwi: strona otwierania (lewe/prawe) wg modelu — patrząc od strony, w którą otwiera się skrzydło.
 - Rysunek wygenerowany automatycznie z modelu modelbudynek.yamli (wersja 1.0, 2026-09-25) — generatory lamela.views.

ZESTAWIENIE POMIESZCZEŃ



Nr	Nazwa pomieszczenia	Posadzka	Kat.	Wys. [m]	Pow. [m²]
1.06	Salon + jadalnia + kuchnia	Deska warstwowa dębowa 15 mm, klejona	podst.	2,77	54,44
1.13	Garaż 2-stanowiskowy	Posadzka żywiczna epoksydowa antypoślizgowa (garaż)	2,76	37,42	
1.10	Pokój gościnny / gabinet	Deska warstwowa dębowa 15 mm, klejona	podst.	2,77	12,52
1.12	Pomieszczenie techniczne	Płytki gresowe 60x120 na kleju C2TE \$1 techn.	2,76	8,85	
1.11	Przedśionek gospodarczy	Płytki gresowe 60x120 na kleju C2TE \$1	ruchu	2,76	7,18
1.02	Hol	Płytki gresowe 60x120 na kleju C2TE \$1	ruchu	2,77	4,44
1.01	Wiatrołap	Płytki gresowe 60x120 na kleju C2TE \$1	ruchu	2,77	3,89
1.09	Łazienka gościnna (natrysk)	Płytki gresowe 60x120 na kleju C2TE \$1	pomoc.	2,77	3,84
1.07	Pas komunikacyjny przy schodach	Deska warstwowa dębowa 15 mm, klejona	ruchu	2,77	3,51
1.16	Schówek pod spocznikiem (h < 1,40)	Płytki gresowe 60x120 na kleju C2TE \$1	pomoc.	1,37	2,91
1.04	Klatka schodowa	Deska warstwowa dębowa 15 mm, klejona	ruchu	2,77	2,78
1.03	WC gościnne	Płytki gresowe 60x120 na kleju C2TE \$1	pomoc.	2,77	2,32
1.15	Schówek pod schodami (h 1,40-2,20)	Płytki gresowe 60x120 na kleju C2TE \$1	pomoc.	1,80	1,45
1.08	Przedpokój gościnny	Deska warstwowa dębowa 15 mm, klejona	ruchu	2,77	1,44
1.05	Spizarnia	Płytki gresowe 60x120 na kleju C2TE \$1	pomoc.	2,77	1,02
1.14	Szacht instalacyjny SI		techn.	2,77	0,45
RAZEM powierzchnia netto					148,45
w tym użytkowa (podst. + pomoc.)					115,91

OZNACZENIA MATERIAŁÓW (PN-B-01030 + przyjęte)


- Włna mineralna 035 (szkielet, docieplenia, ściana dom-garaż)
- Stal konstrukcyjna S355 (słupy RK, rama boksu C), cynkowana ogniowo + malowana proszkowo RAL 7016 — zaczemienie
- Ścianka szklana VSG 2 × 8 mm w ramie aluminiowej (wiatrołap / hol)
- Żelbet C25/30, B500SP (stropy, płyta fundamentowa, ściany) — 45° na przemian ciągle i przerywane

OZNACZENIA LINII

- elementy nad płaszczyzną cięcia (obrysy płyt, wsporników, brył wyższych kondygnacji)
- elementy poniżej płaszczyzny cięcia (widok z góry)
- osie konstrukcyjne; linia punktowa z pogrubionymi końcami — ślad przekroju

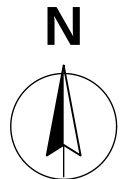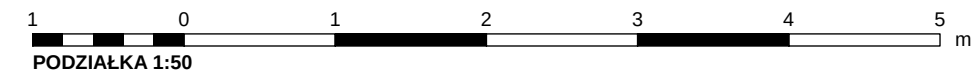

REW.	OPIS ZMIANY	DATA		
0	Wydanie — rysunek wygenerowany z modelu	2026-09-25		
PRACOWNIA PROJEKTOWA PRACOWNIA PROJEKTOWA — nazwa do uzupełnienia		BRANZA ARCHITEKTURA (AR)		
adres pracowni do uzupełnienia				
INWESTOR (do uzupełnienia)				
OBIEKT / NAZWA ZAMIERZENIA BUDOWLANEGO Budynek mieszkalny jednorodzinny wolnostojący „Dom LAMELA”				
ADRES / LOKALIZACJA (NR DZIAŁKI, OBRĘB, JEDN. EWIDENCYJNA) ul. Lipowa (fikcyjna), dz. nr ewid. 123/4, obręb 0005 Przykładowo, gm. Przykładowo (fikcyjna)		KAT. OBIEKTU I		
FUNKCJA	IMIĘ I NAZWISKO	SPECJALNOŚĆ, NR UPRAWNIENI	DATA	PODPIS
Projektant				
Projektant (wsp.)				
Sprawdzający				
Opracował				
TYTUŁ RYSUNKU RZUT PARTERU				
SKALA 1:50	FORMAT 630×594	DATA WYDANIA 2026-09-25	RODZAJ DOK. rzut	NR RYSUNKU PB-AR-01
ARKUSZ 1/5	REW. 0			

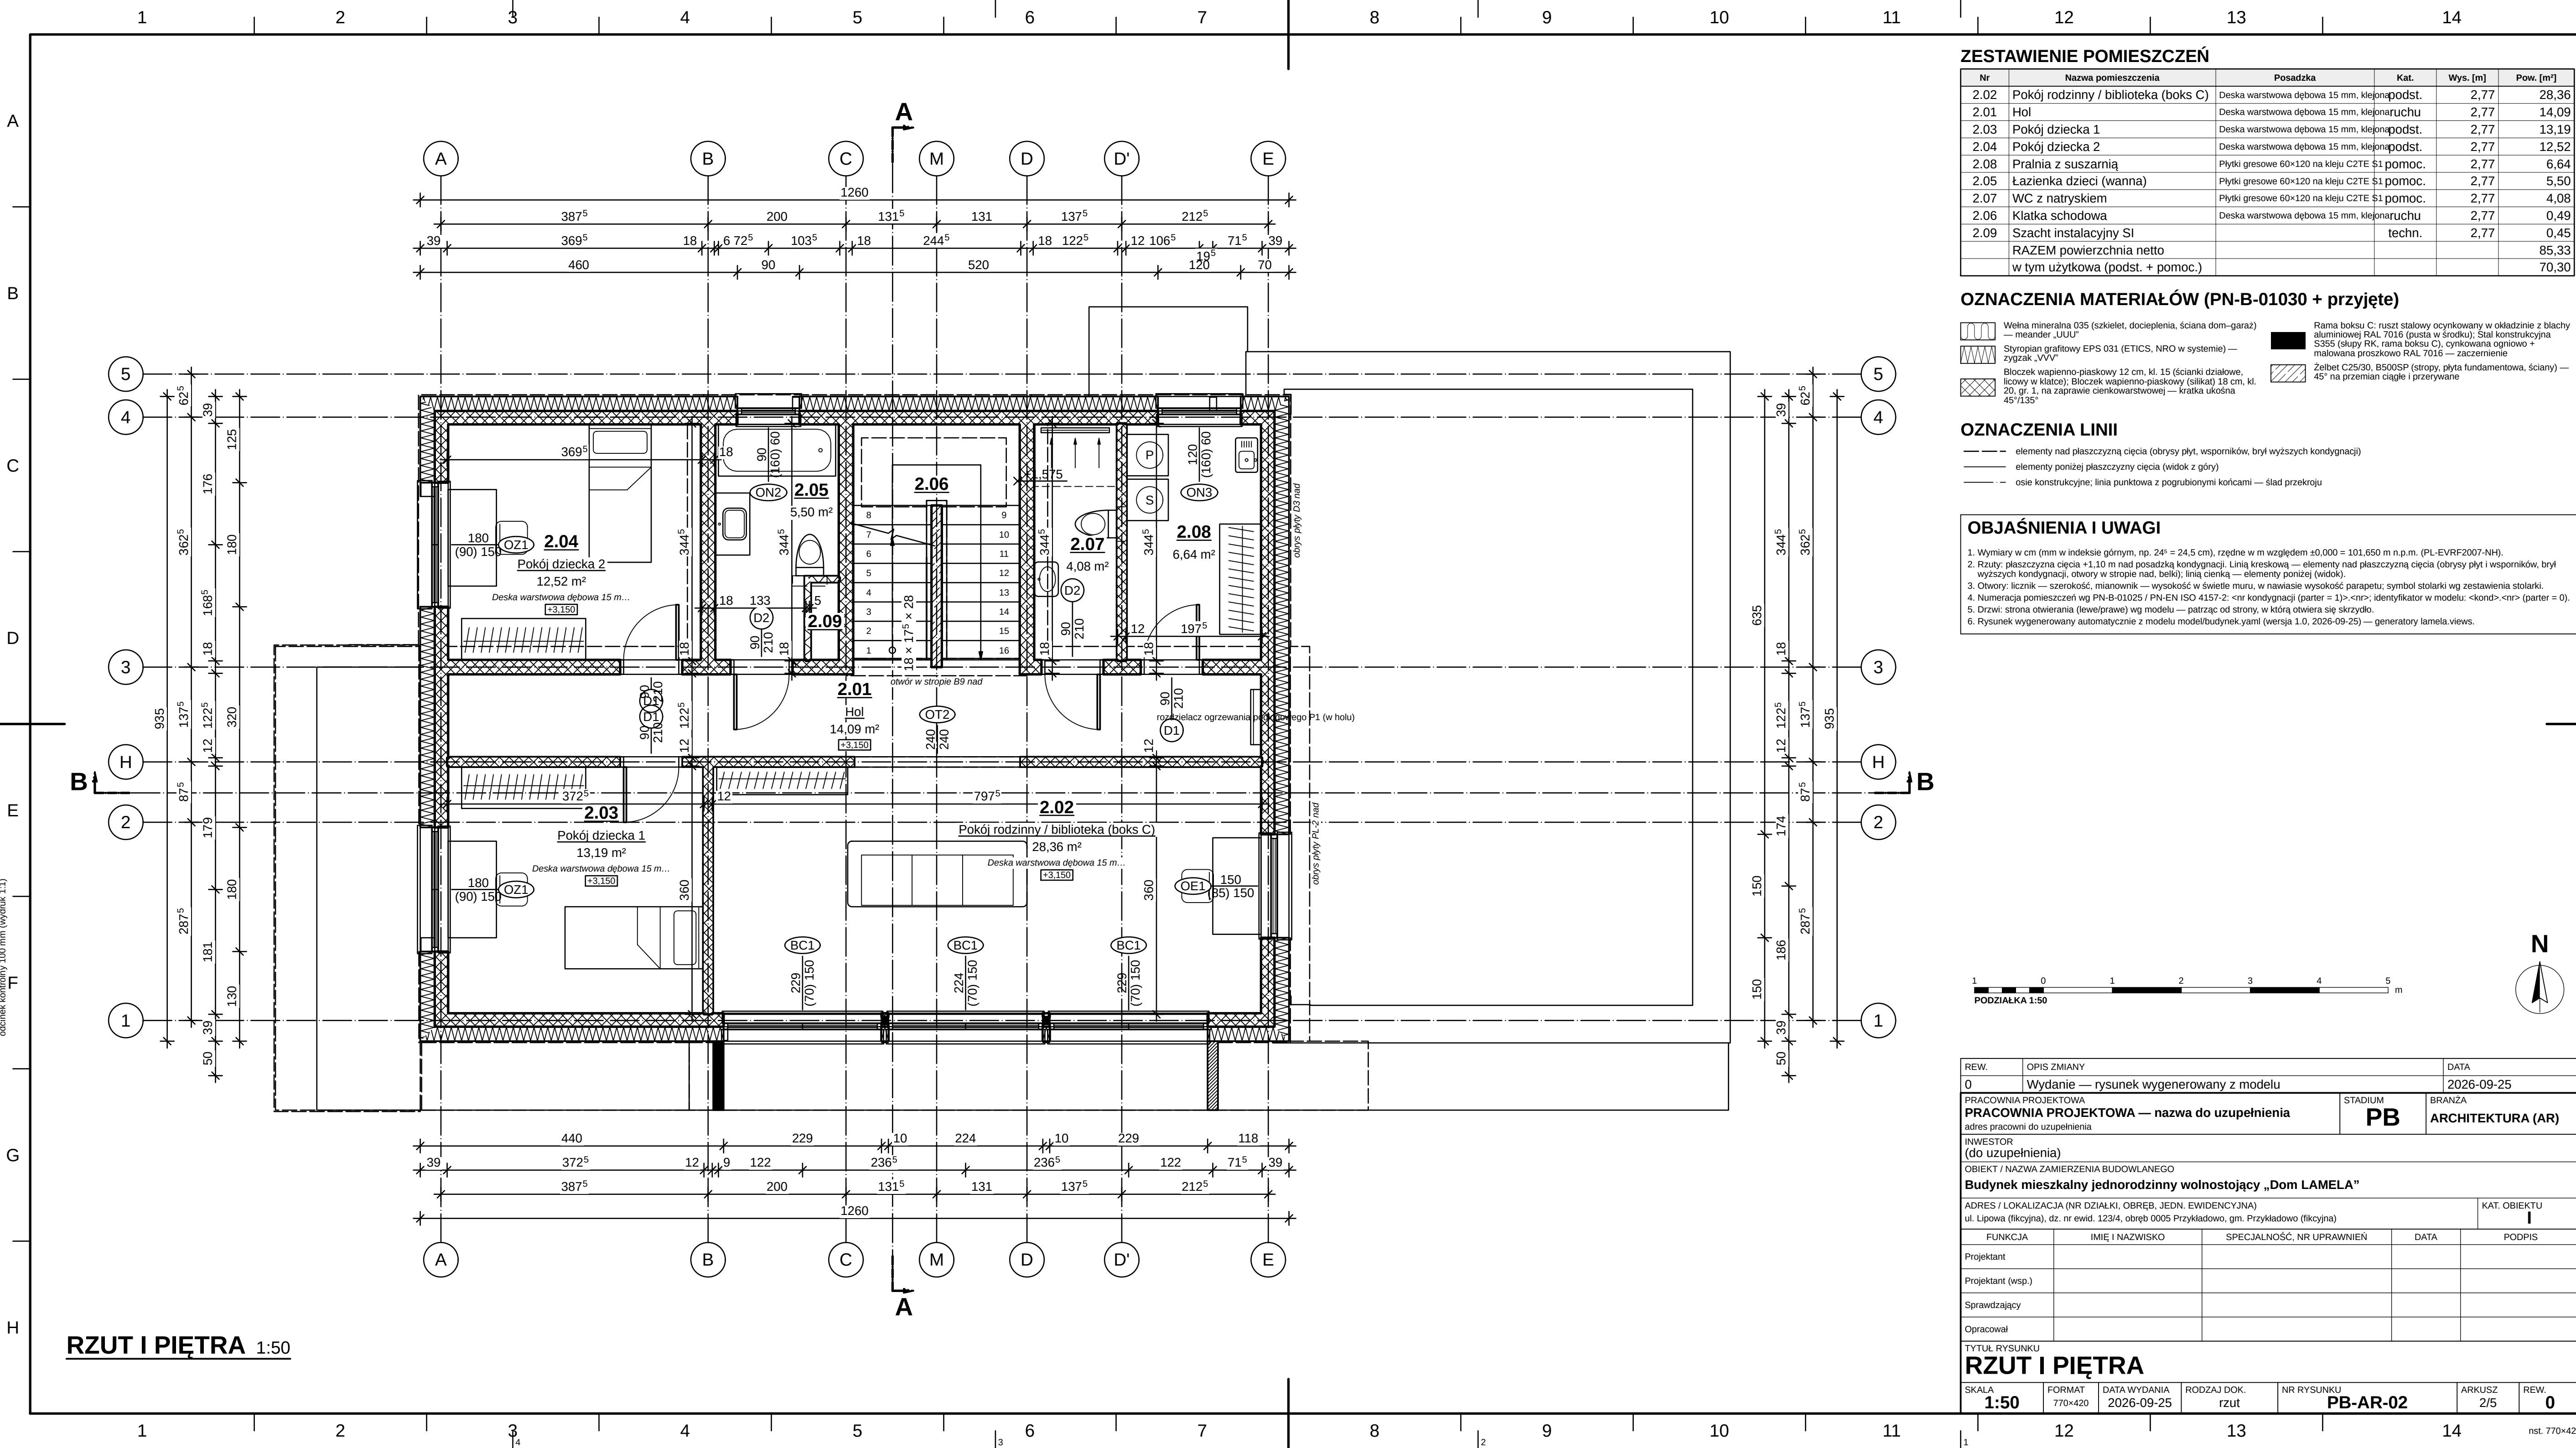

ZESTAWIENIE POMIESZCZEŃ

Nr	Nazwa pomieszczenia	Posadzka	Kat.	Wys. [m]	Pow. [m²]
2.02	Pokój rodzinny / biblioteka (boks C)	Deska warstwowa dębowa 15 mm, klejona	podst.	2,77	28,36
2.01	Hol	Deska warstwowa dębowa 15 mm, klejona	podst.	2,77	14,09
2.03	Pokój dziecka 1	Deska warstwowa dębowa 15 mm, klejona	podst.	2,77	13,19
2.04	Pokój dziecka 2	Deska warstwowa dębowa 15 mm, klejona	podst.	2,77	12,52
2.08	Pralnia z suszarnią	Płytki gresowe 60×120 na kleju C2TE S1	podm.	2,77	6,64
2.05	Łazienka dzieci (wanna)	Płytki gresowe 60×120 na kleju C2TE S1	podm.	2,77	5,50
2.07	WC z natryskiem	Płytki gresowe 60×120 na kleju C2TE S1	podm.	2,77	4,08
2.06	Klatka schodowa	Deska warstwowa dębowa 15 mm, klejona	podst.	2,77	0,49
2.09	Szacht instalacyjny SI		techn.	2,77	0,45
RAZEM powierzchnia netto					85,33
w tym użytkowa (podst. + pomoc.)					70,30

OZNACZENIA MATERIAŁÓW (PN-B-01030 + przyjęte)

	Włna mineralna 035 (szkielet, docieplenia, ściana dom-garaż) — meander „UUU”		Rama boksu C: ruszt stalowy ocynkowany w zakładzinie z blachy aluminiowej RAL 7016 (pusta w środku). Stal konstrukcyjna S355 (słupy RK, rama boksu C), cynkowana ognioowo + malowana proszkowo RAL 7016 — zaczernienie
	Styropian gniałowy EPS 031 (ETICS, NRO w systemie) — zygzak „VVV”		Żelbet C25/30, B500SP (stropy, płyta fundamentowa, ściany) — 45° na przemian ciagle i przerywane
	Błoczek wapienno-piaskowy 12 cm, kl. 15 (ścianki działowe, lico w klatce); Błoczek wapienno-piaskowy (silikat) 18 cm, kl. 20, gr. 1, na zaprawie cienkowarstwowej — kratka ukośna 45°/135°		

OZNACZENIA LINII

	elementy nad płaszczyznę cięcia (obrysy płyt, wsporników, brył wyższych kondygnacji)
	elementy poniżej płaszczyzny cięcia (widok z góry)
	osie konstrukcyjne; linia punktowa z pogrubionymi końcami — ślad przekroju

OBJAŚNIENIA I UWAGI

- Wymiary w cm (mm w indeksie górnym, np. 24⁵ = 24,5 cm), rzędne w m względem ±0,000 = 101,650 m n.p.m. (PL-EVRF2007-NH).
- Rzuty: płaszczyzna cięcia +1,10 m nad posadzką kondygnacji. Linia kreskową — elementy nad płaszczyznę cięcia (obrysy płyt i wsporników, brył wyższych kondygnacji, otwory w stropie nad, belki); linią cienką — elementy poniżej (widok).
- Otwory: licznik — szerokość, mianownik — wysokość w świetle muru, w nawiasie wysokość parapetu; symbol stolarki wg zestawienia stolarki.
- Numeracja pomieszczeń wg PN-B-01025 / PN-EN ISO 4157-2: <nr kondygnacji (parter = 1)> <nr> <identyfikator w modelu: <kond> <nr> (parter = 0).
- Drzwi: strona otwierania (lewe/prawe) wg modelu — patrz: od strony, w którą otwiera się skrzydło.
- Rysunek wygenerowany automatycznie z modelu model/budynek.yaml (wersja 1.0, 2026-09-25) — generatory lamela.views.




REW.	OPIS ZMIANY	DATA		
0	Wydanie — rysunek wygenerowany z modelu	2026-09-25		
PRACOWNIA PROJEKTOWA PRACOWNIA PROJEKTOWA — nazwa do uzupełnienia adres pracowni do uzupełnienia		STADIUM PB	BRANŻA ARCHITEKTURA (AR)	
INWESTOR (do uzupełnienia)				
OBIEKT / NAZWA ZAMIERZENIA BUDOWLANEGO Budynek mieszkalny jednorodzinny wolnostojący „Dom LAMELA”				
ADRES / LOKALIZACJA (NR DZIAŁKI, OBRĘB, JEDN. EWIDENCYJNA) ul. Lipowa (fikcyjna), dz. nr ewid. 123/4, obręb 0005 Przykładowo, gm. Przykładowo (fikcyjna)			KAT. OBIEKTU I	
FUNKCJA	IMIĘ I NAZWISKO	SPECJALNOŚĆ, NR UPRAWNIENI	DATA	PODPIS
Projektant				
Projektant (wsp.)				
Sprawdzający				
Opracował				
TYTUŁ RYSUNKU RZUT I PIĘTRA				
SKALA 1:50	FORMAT 770x420	DATA WYDANIA 2026-09-25	RODZAJ DOK. rzut	NR RYSUNKU PB-AR-02
ARKUSZ 2/5			REW. 0	

RZUT II PIĘTRA 1:50

OZNACZENIA LINII

- elementy nad płaszczyzną cięcia (obrysy płyt, wsporników, brył wyższych kondygnacji)
--- elementy poniżej płaszczyzny cięcia (widok z góry)
--- osie konstrukcyjne; linia punktowa z pogrubionymi końcami — ślad przebiegu

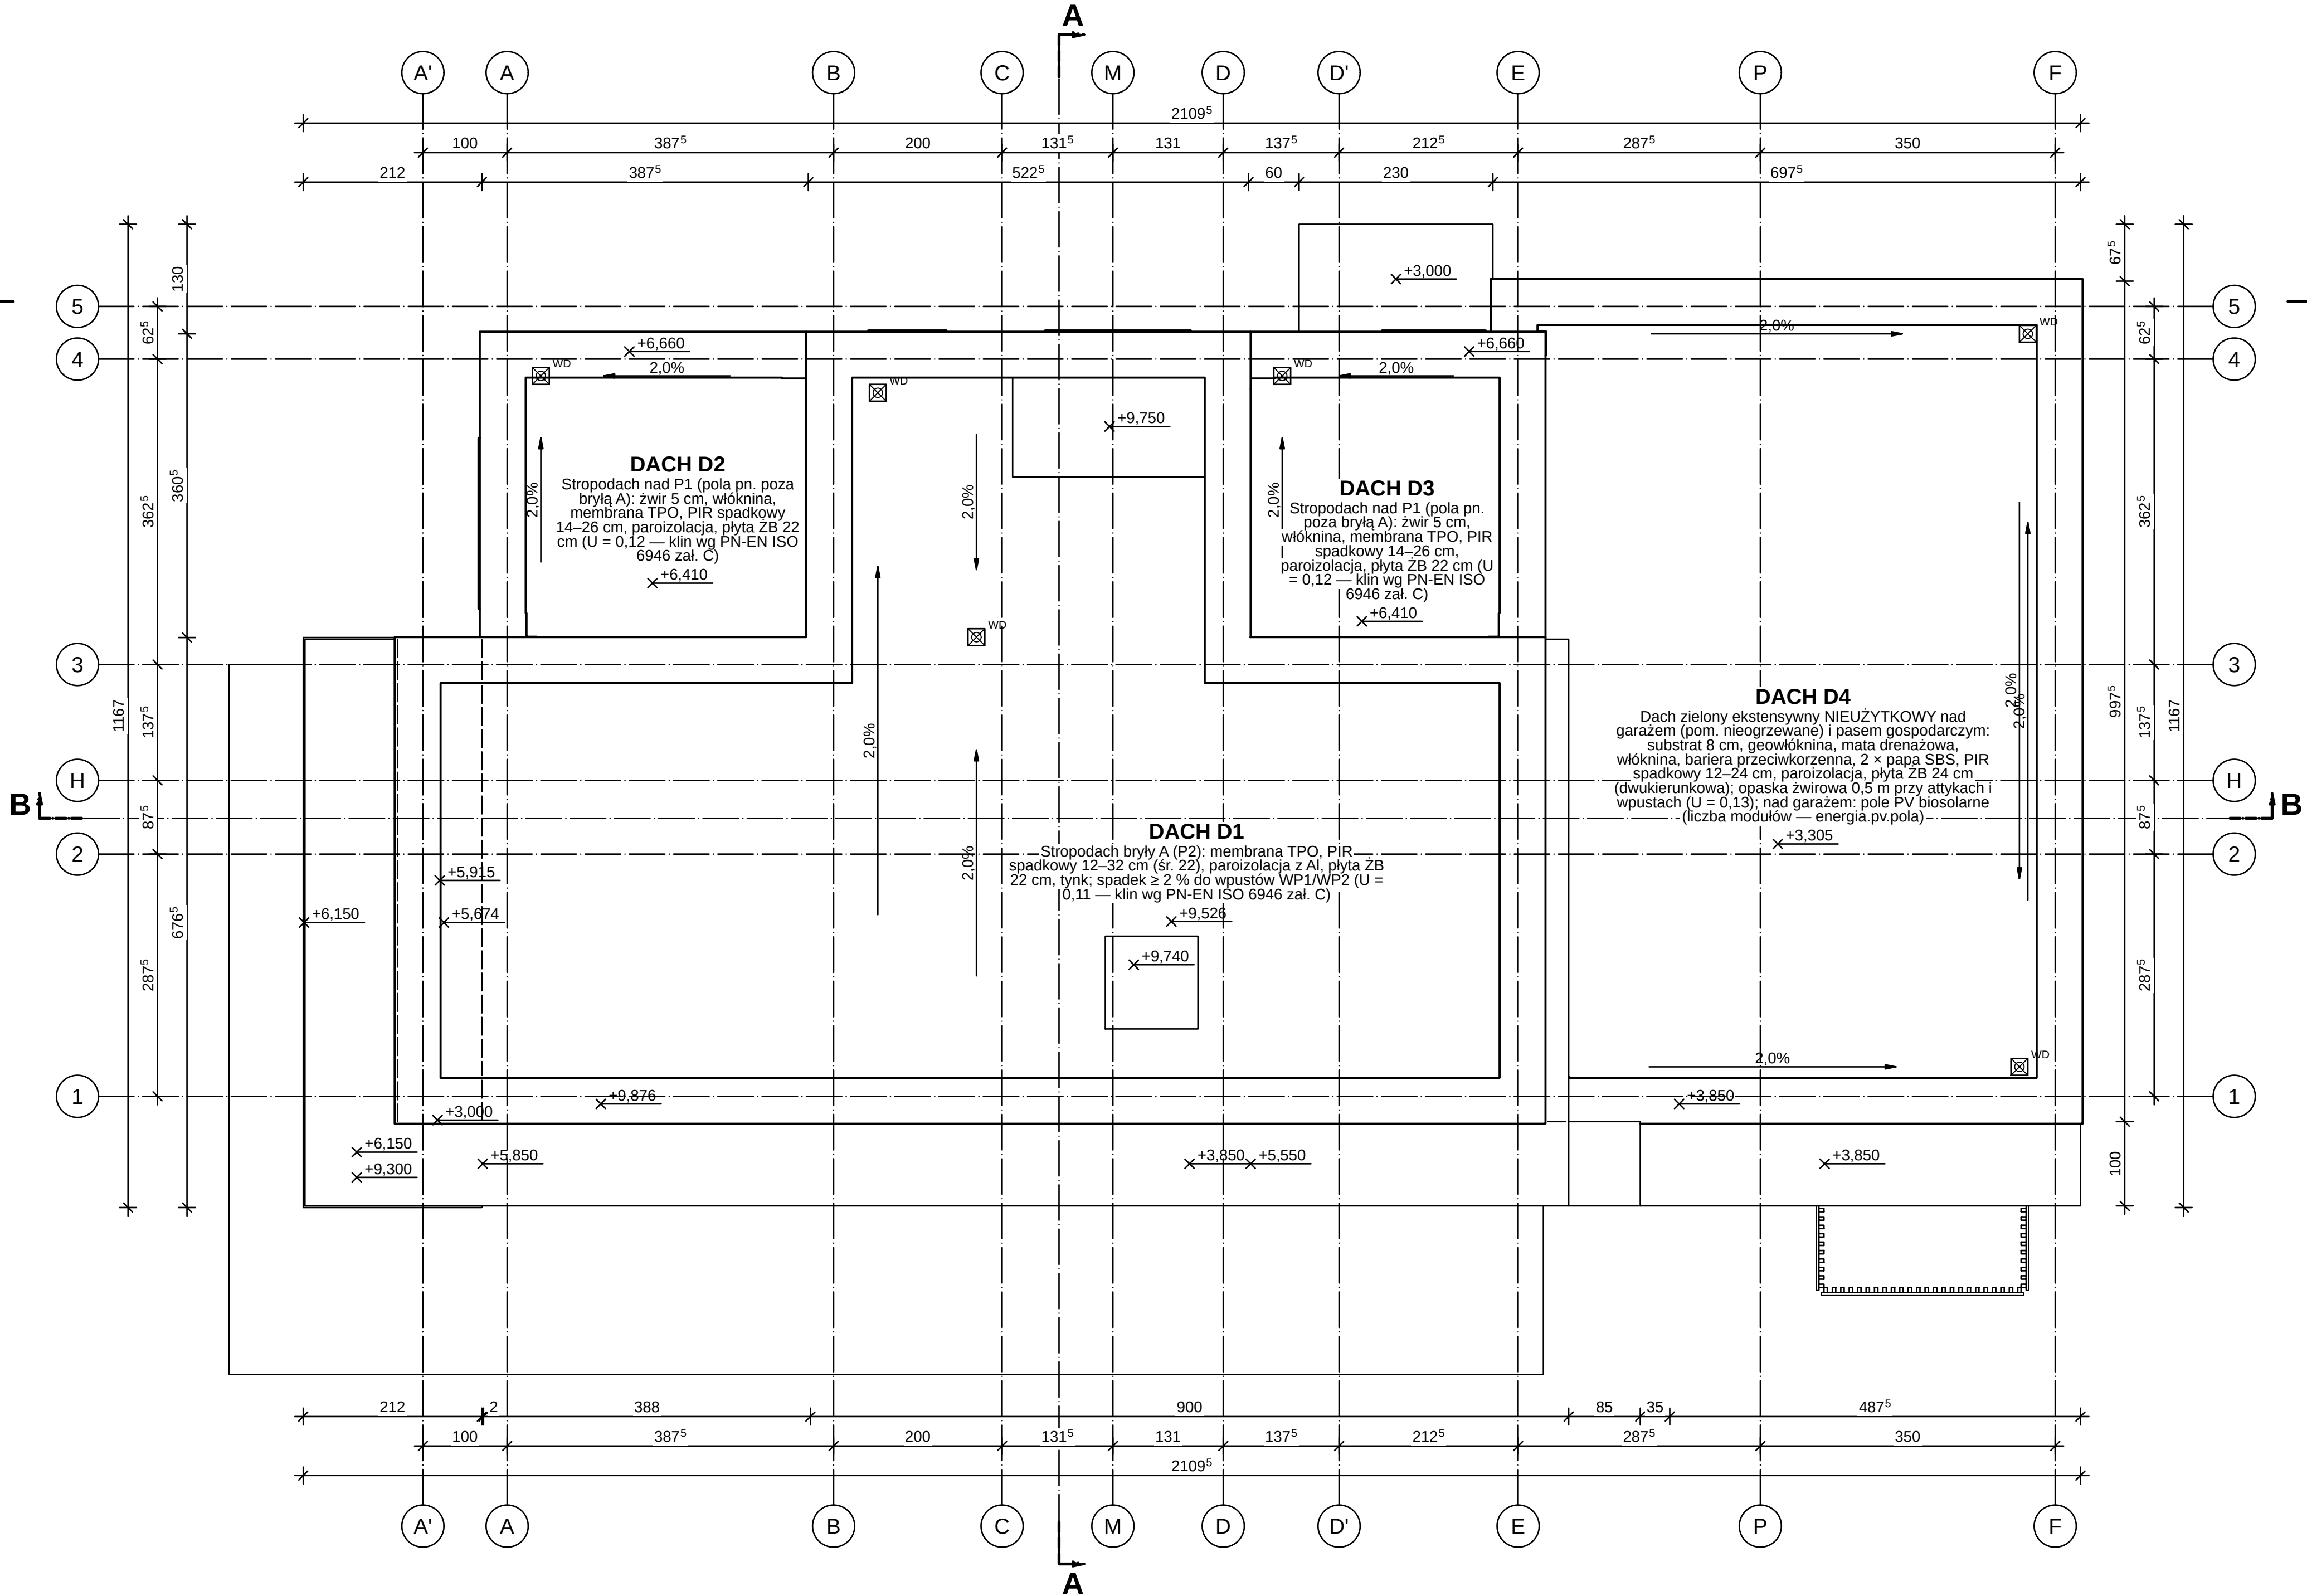

RZUT DACHU 1:50

OZNACZENIA MATERIAŁÓW (PN-B-01030 + przyjęte)

- Włna mineralna 035 (szkielet, docieplenia, ściana dom-garaz);
Wełna mineralna fasadowa (elewacja wentylowana bryły A, A1)
--- meander, UUU
Styropian grafitowy EPS 031 (ETICS, NRO w systemie) —
zgracek „VUV”
--- Membrana fasadowa wiatroizolacyjna UV-stabilna, czarna (sd = 0,02 m)
Błoczek wapniowo-piaskowy 12 cm, kl. 15 (ścianki działowe, boczny w klatce); Błoczek wapniowo-piaskowy (silikat) 18 cm, kl. 20, gr. 1, na zaprawie cienkowarstwowej — krawka ukośna 45°/135°
Żelbet C25/30, B500SP (stropy, płyta fundamentowa, ściany) —
45° na przemiian cięgie i przerywane

OBJAŚNIENIA I UWAGI

1. Wymiary w cm (mm w indeksie górnym, np. 24° = 24,5 cm), rzędne w m względem ±0,000 = 101,650 m n.p.m. (PL-EVRF2007-NH).
2. Rzut: płaszczyzna cięcia +1,10 m nad posadzką kondygnacji. Linia krekowa — elementy nad płaszczyzną cięcia (obrysy płyt i wsporników, brył wyższych kondygnacji, otwory w stropie nad, belki); linia ciągła — elementy poniżej (widok).
3. Otwory: licznik — szerokość, mianownik — wysokość w świetle muru, w nawiasie wysokość parapetu; symbol stolarki wg zestawienia stolarki.
4. Numeracja pomieszczeń wg PN-B-01025 / PN-EN ISO 4157-2: <nr> kondygnacji (parter = 1) <nr>; identyfikator w modelu: <kond> <nr> (parter = 0).
5. Dzw: strona otwierania (lewo/prawo) wg modelu — patrz: od strony, w którą otwiera się skrzydło.
6. Rysunek wygenerowany automatycznie z modelu modelBudynek.yamf (wersja 1.0, 2026-09-25) — generatory lamela.views.


1 0 1 2 3 4 5 m
PODZIAŁKA 1:50

ZESTAWIENIE POMIESZCZEŃ


Nr	Nazwa pomieszczenia	Posadzka	Kat.	Wys. [m]	Pow. [m²]
3.02	Sypialnia rodziców	Deska warstwowa dębowa 15 mm, klejona podst.	2,77	21,43	
3.05	Gabinet / pokój gościnny okazjonalny	Deska warstwowa dębowa 15 mm, klejona podst.	2,77	16,25	
3.03	Garderoba (przedpokój apartamentu)	Deska warstwowa dębowa 15 mm, klejona pomoc.	2,77	10,49	
3.07	Pom. techniczne (centrala rekuperacyjna, wylaz na dach)	Płytki gresowe 60x120 na kleju CZTE \$1 techn.	2,77	5,90	
3.01	Hol	Deska warstwowa dębowa 15 mm, klejona podst.	2,77	5,74	
3.04	Łazienka rodziców	Płytki gresowe 60x120 na kleju CZTE \$1 pomoc.	2,77	5,51	
3.08	Szacht instalacyjny SI	techn.	2,77	0,45	
3.06	Klatka schodowa (wyjście z biegu 2, pustka)	Deska warstwowa dębowa 15 mm, klejona podst.	2,77	0,24	
RAZEM powierzchnia netto					66,01
w tym użytkowa (podst. + pomoc.)					53,67

REW.	OPIS ZMIANY	DATA
0	Wydanie — rysunek wygenerowany z modelu	2026-09-25
PRACOWNIA PROJEKTOWA — nazwa do uzupełnienia		STADIUM
ul. Lipowa (fikcyjna), dz. nr ewid. 123/4, obręb 0005 Przykładowo, gm. Przykładowo (fikcyjna)		BRANŻA
INWESTOR (do uzupełnienia)		ARCHITEKTURA (AR)
OBIEKT / NAZWA ZAMIERZENIA BUDOWLANEGO		
Budynek mieszkalny jednorodzinny wolnostojący „Dom LAMELA”		
ADRES / LOKALIZACJA (NR DZIAŁKI, OBRĘB, JEDN. EWIDENCYJNA)		KAT. OBIEKTU
ul. Lipowa (fikcyjna), dz. nr ewid. 123/4, obręb 0005 Przykładowo, gm. Przykładowo (fikcyjna)		I
FUNKCJA	IMIĘ I NAZWISKO	SPECJALNOŚĆ, NR UPRAWNIENI
Projektant		DATA
Projektant (wsp.)		PODPIS
Sprawdzający		
Opracował		
TYTUŁ RYSUNKU		
RZUT II PIĘTRA I RZUT DACHU		
SKALA	FORMAT	DATA WYDANIA
1:50	S90x891	2026-09-25
RODZAJ DOK.	RZUT	NR RYSUNKU
		PB-AR-03
ARKUSZ	3/5	REW.
		0

PRZĘKRÓJ A-A 1:50

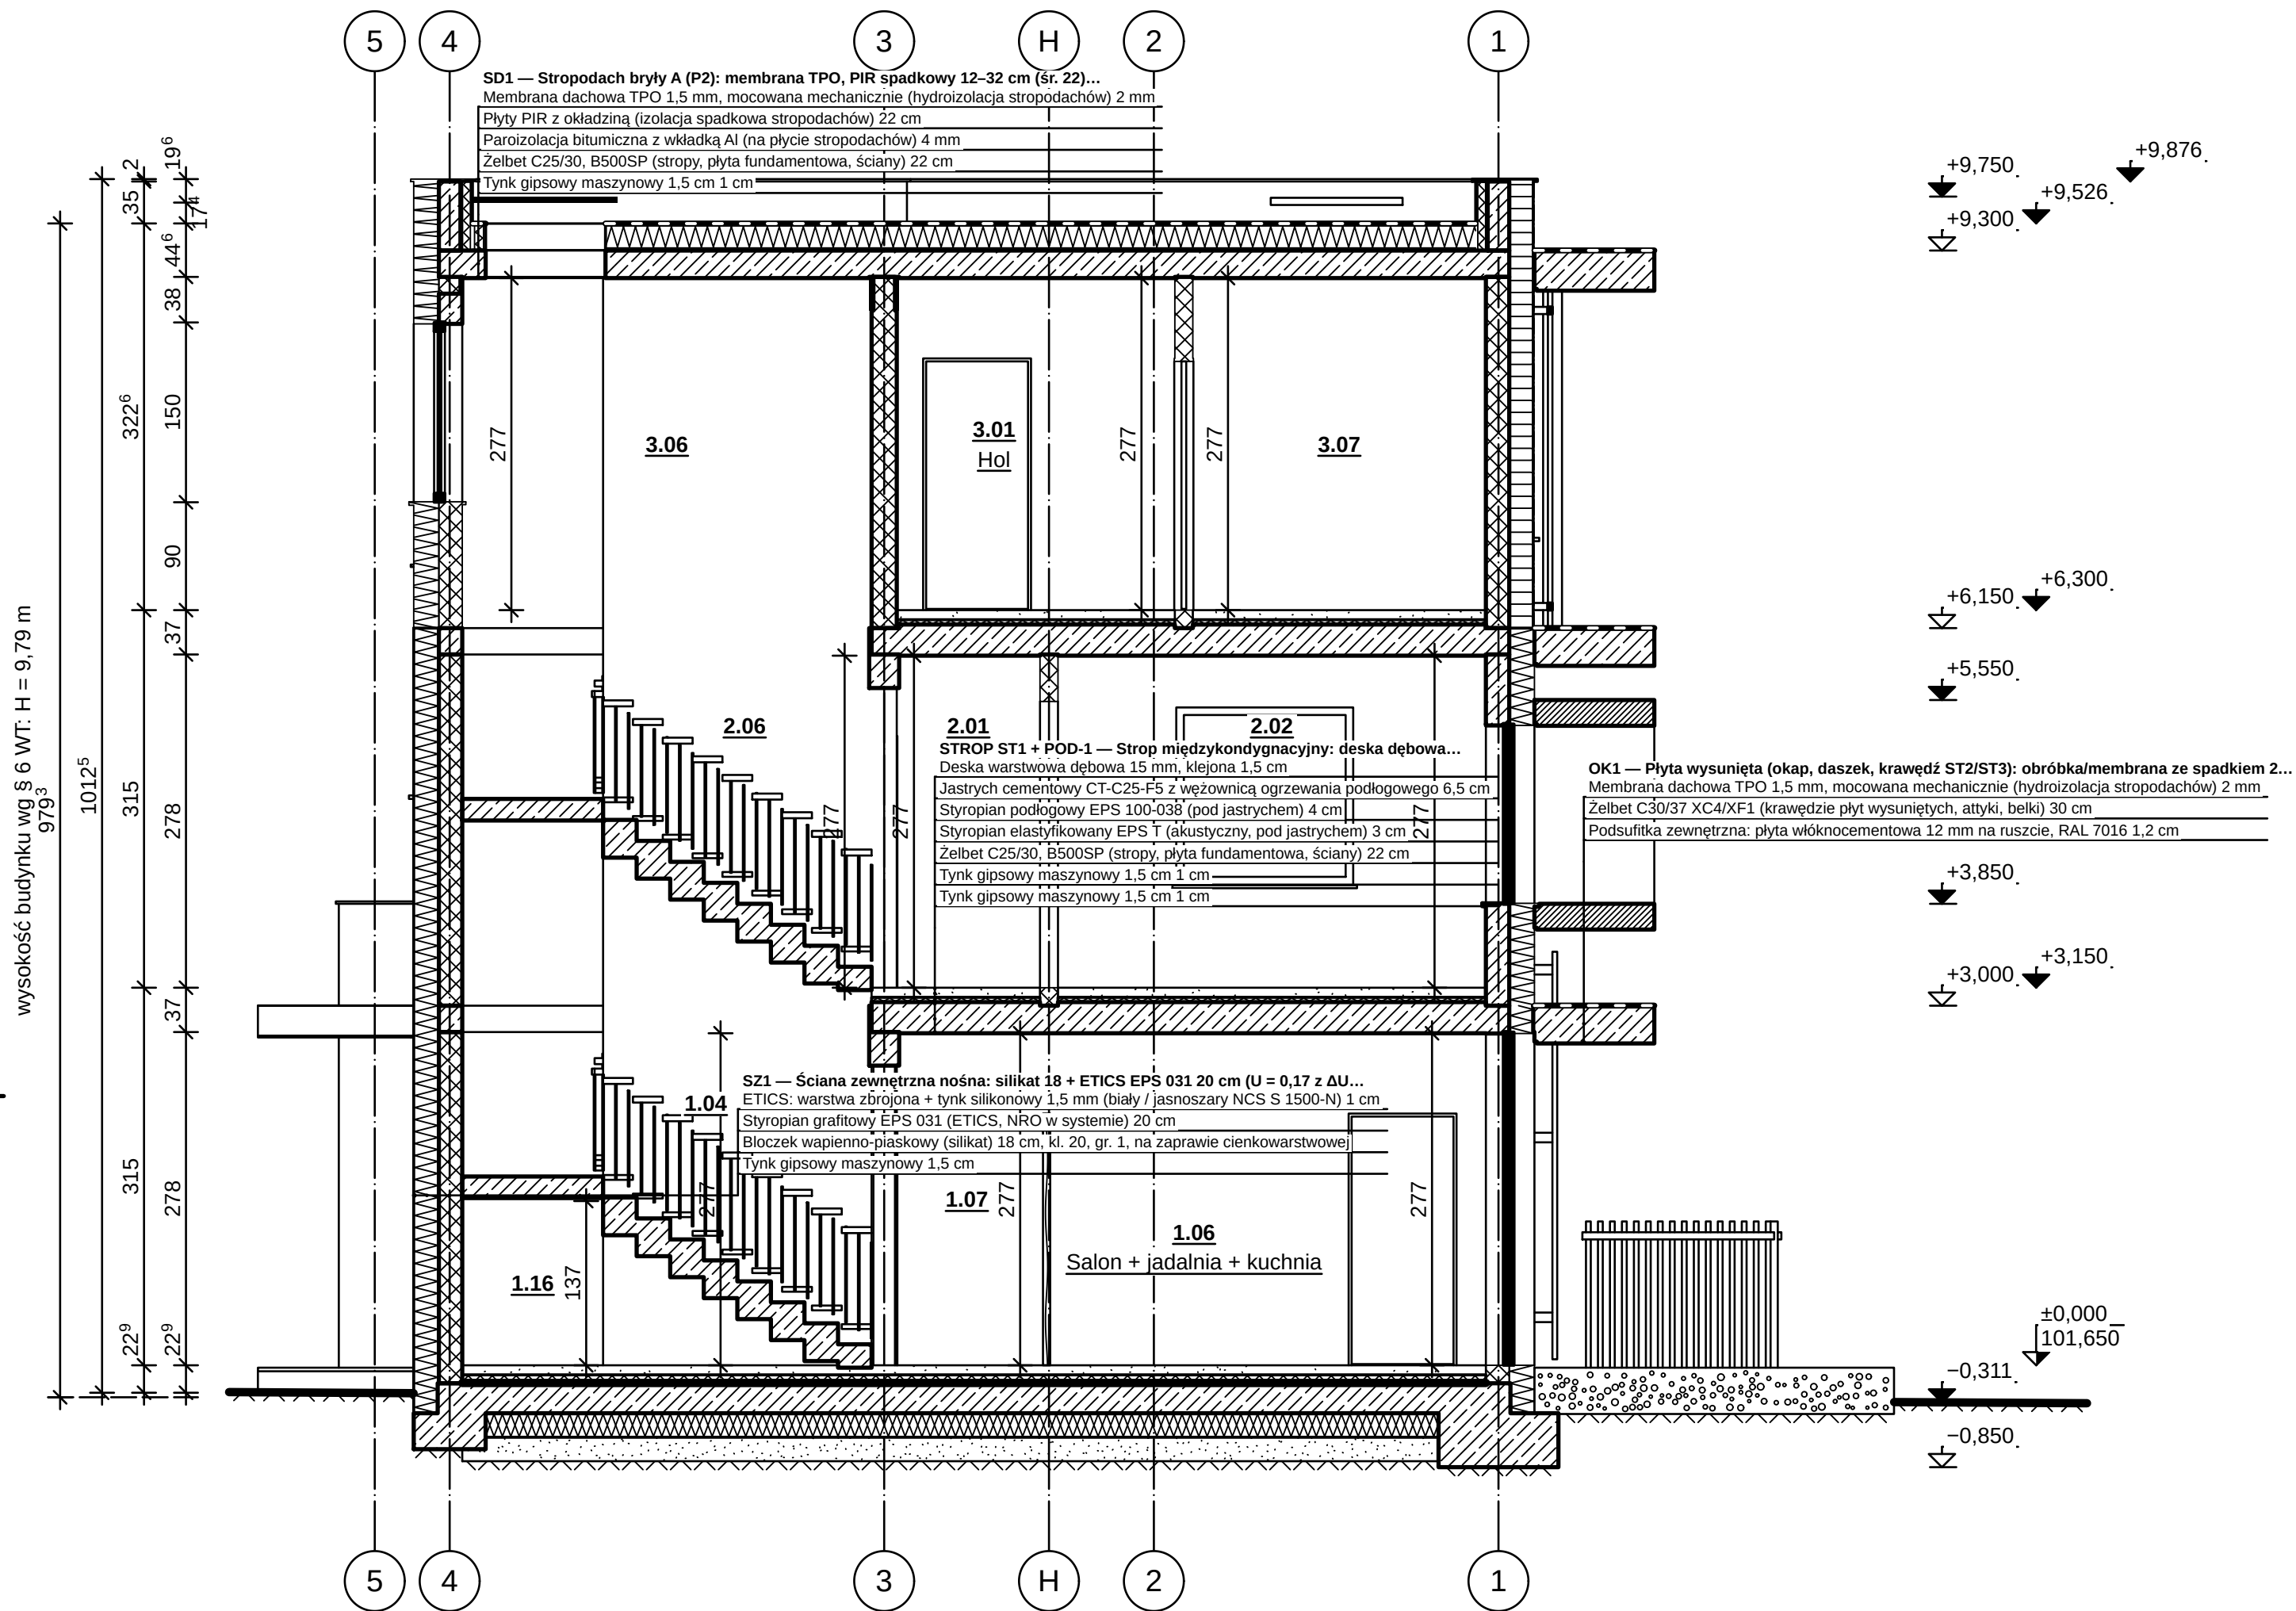

PRZĘKRÓJ B-B 1:50

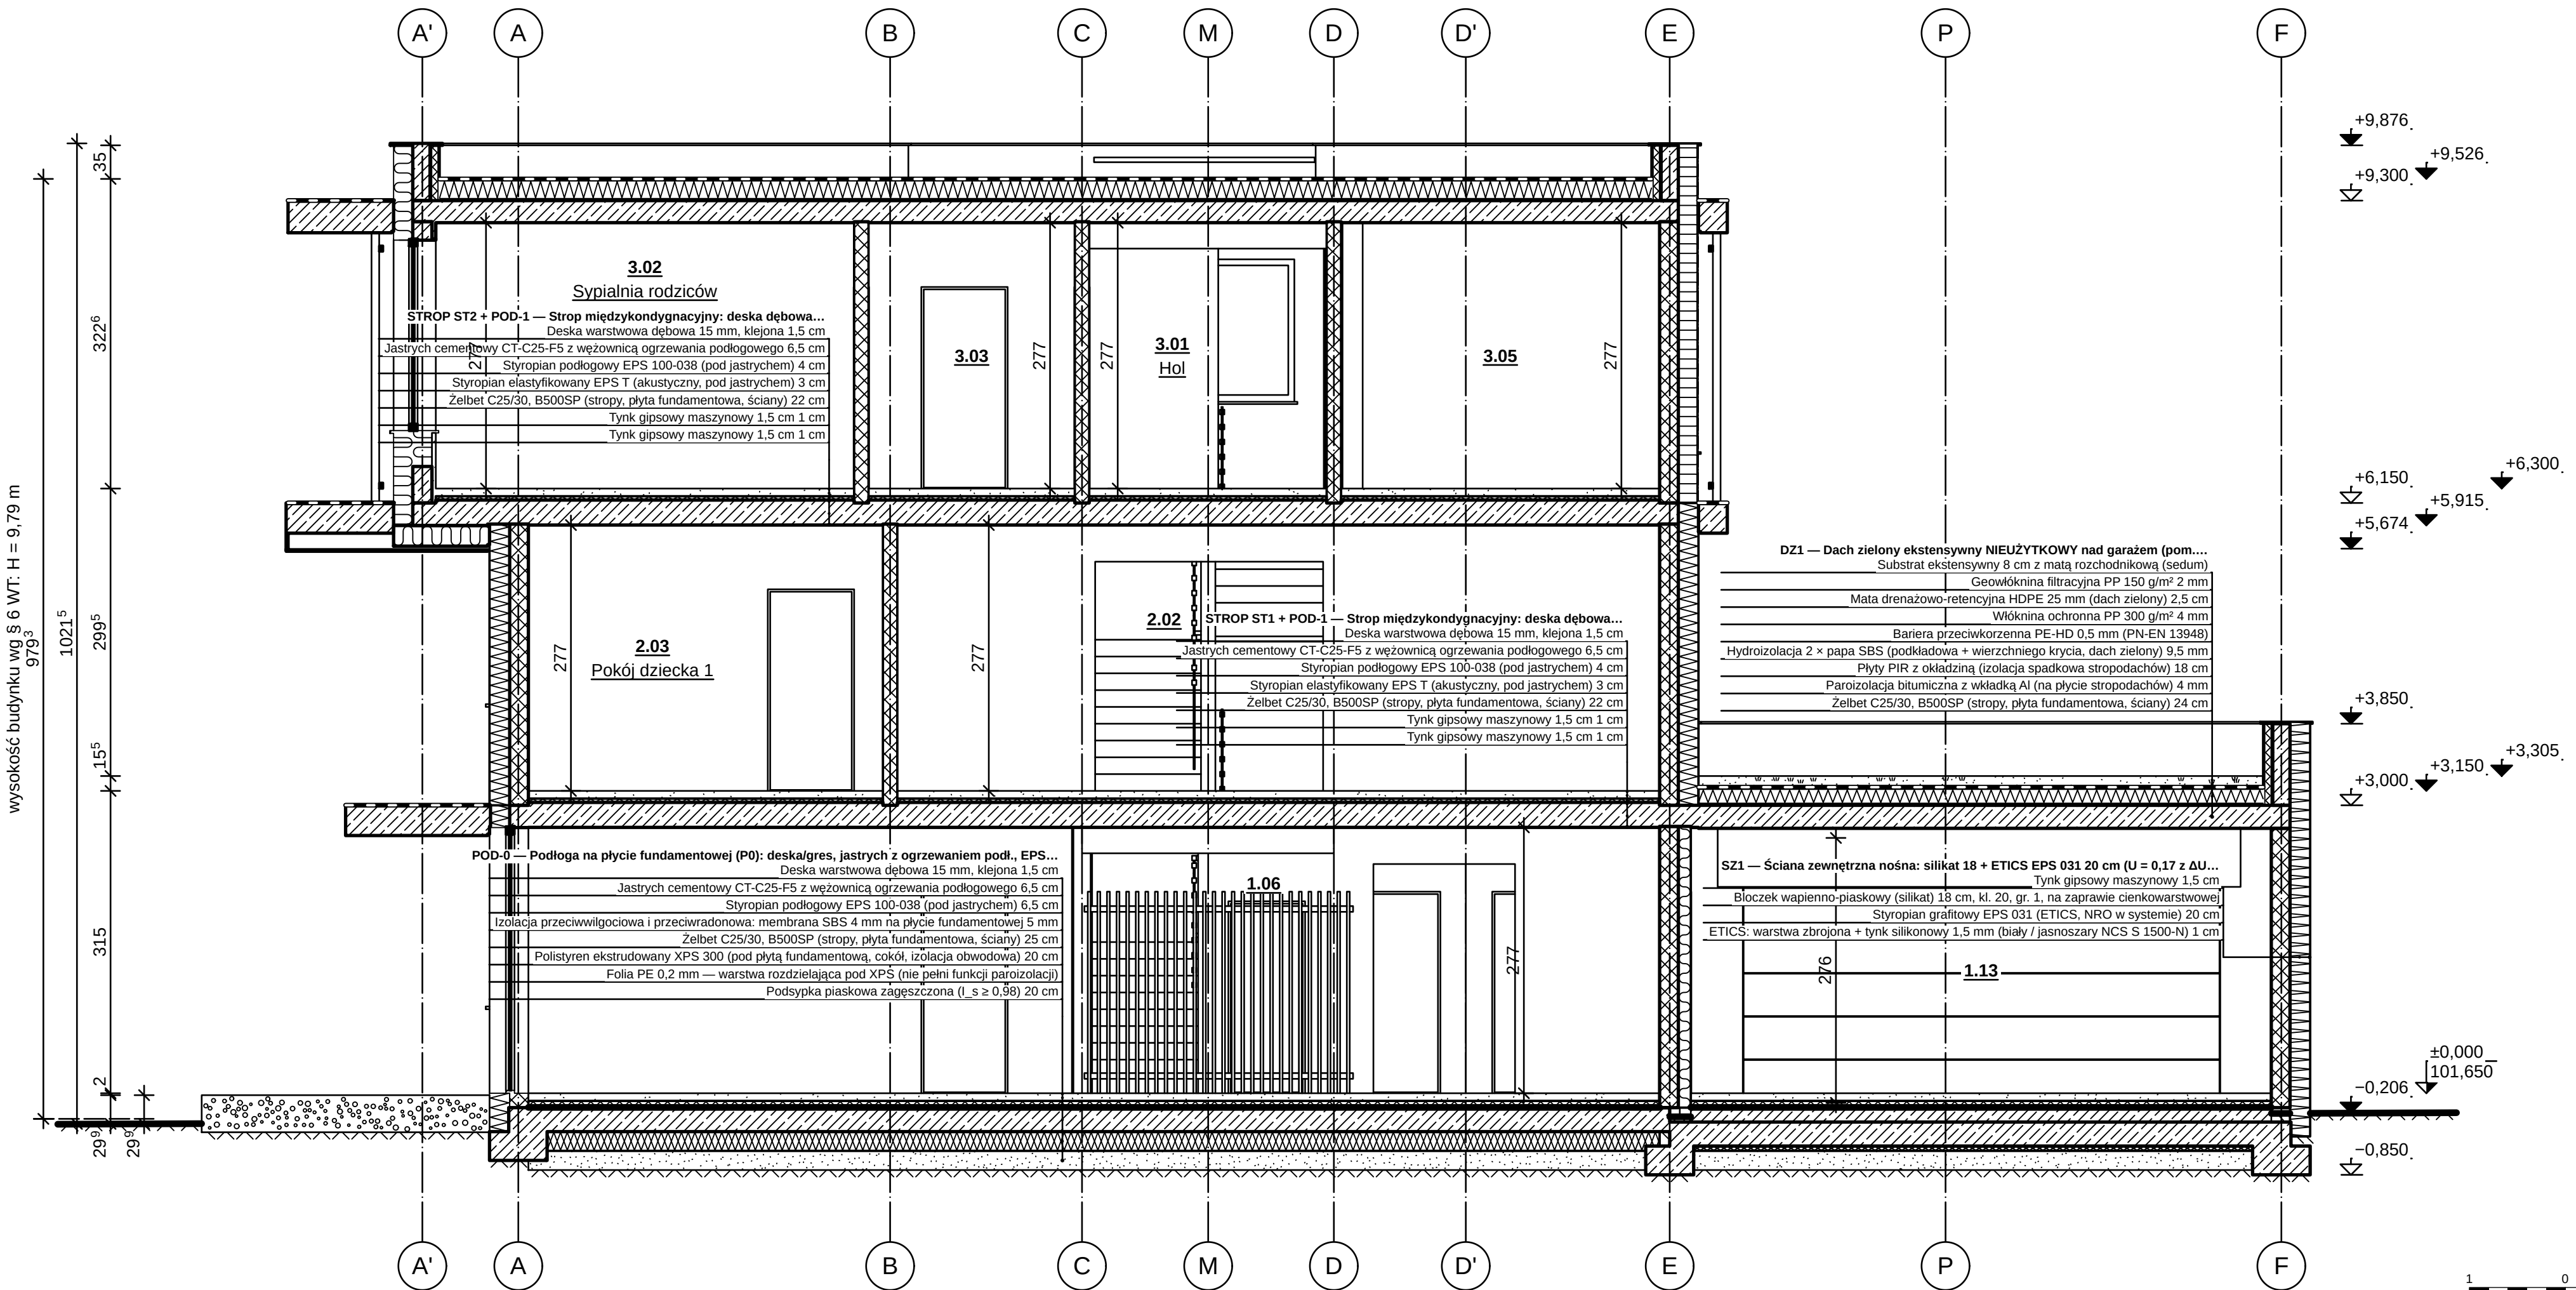


OBJAŚNIENIA I UWAGI

- Wymiary w cm (mm w indeksie górnym, np. 24" = 24,5 cm), rzędne w m względem ±0,000 = 101,650 m n.p.m. (PL-EVRF2007-NH).
- Rzędne: trójkąt zacementowany — poziom wykończenia, niezacementowany — konstrukcji, w połowie zacementowany — poziom ±0,000 z rzędną bezwzględną (PN-B-01025).
- Wysokość budynku wg § 6 WT: od terenu przy najniższej podłożonej wejściu (-0,267) do wierzchu stropodachu D1 (+9,526) — H = 9,79 m (bez attyki).
- Opisy warstw: kod i nazwa przegrody z modelu, materiały i grubości wg modelu (od góry / od lewej).
- Przekrój A-A: opisy warstw pominięte na rysunku (brak miejsca w podziale 1:50): POD-0, STROP ST2 + POD-1 — układ warstw wg zestawienia przegród w części opisowej / przekroju 1:50.
- Przekrój B-B: opisy warstw pominięte na rysunku (brak miejsca w podziale 1:50): STROP ST2Z + POD-1, SD1, OK1 — układ warstw wg zestawienia przegród w części opisowej / przekroju 1:50.
- Rysunek wygenerowany automatycznie z modelu modelbudynki.yamli (wersja 1.0, 2026-09-25) — generatory lamela.views.


OZNACZENIA MATERIAŁÓW (PN-B-01030 + przyjęte)

- Lamele dębowe 30×60 mm (ekran komunikacji P0, h 2,10 m; 0,02 m).
- Deska warstwowa dębowa 15 mm, klejona — przekrój wzdłuż włókien
- grunt rodzimy
- Substrat ekstensywny 8 cm z małą rozchodnikową (sedum)
- Wełna mineralna fasadowa (elewacja wentylowana bryły A, A1); Wełna mineralna OSB (szkielet, docieplenia, ściana dom-garaz) — meander „UUU”
- Płyty PIR z okładziną (izolacja spadkowa stropodachów) — zygzak z okładzinami
- Izolacja przeciwwilgociowa i przeciwdrażna: membrana SBS 4 mm na płycie fundamentowej — linia bardzo gruba
- Membrana dachowa TPO 1,5 mm, mocowana mechanicznie (hydroizolacja stropodachów); Hydroizolacja 2 × papa SBS (podkładowa + wierzchniego krycia, dach zielony) — pas czarno-biały
- Syroplan gąbrowy EPS 031 (ETICS, NRO w systemie); Syroplan podłogowy EPS 100-038 (pod jastrychem); Syroplan elastyczny EPS T (akustyczny, pod jastrychem) — zygzak „VVV”
- Polistyren ekstrudowany XPS 300 (pod płytą fundamentową, cokoł, izolacja obwodowa) — zygzak podwójny
- Jasnych cementowy CT-C25-F5 z wężownicą ogrzewania podłogowego — kropki
- Membrana fasadowa wiatroizolacyjna UV-stabilna, czarna (sd = 0,02 m)
- Błoczek wapienno-piaskowy 12 cm, kl. 15 (ścianki działowe, licowy w klatce); Błoczek wapienno-piaskowy (silikat) 18 cm, kl. 20, gr. 1, na zaprawie cienkowarstwowej — kratka ukośna 45°/135°
- Paroizolacja bitumiczna z wkładką Al (na płycie stropodachów) — linia kreskowa cienka 3/1 po ciepłej stronie
- Podsyłka piaskowa zagęszczona (L s ≥ 0,98)
- Płyta gipsowo-kartonowa 12,5 mm (GKB / GKB) w łazienkach; Podsyłka zewnętrzna: płyta włóknocementowa 12 mm na ruszcie, RAL 7016
- Obróbki blacharskie (blacha powlekana); Stalarka — profile aluminiowe, antracyt; Rama boksu C; ruszt stalowy ocynkowany w okładzinie z blachy aluminiowej RAL 7016 (pushta w środku); Stal malowana proszkowo (balustrady, rygle) — zaczerpienie
- Szkło (szyby zespolone); Ścianka szklana VSG 2 × 8 mm w ramie aluminiowej (wiatrąpek / hoi)
- Żelbet C25/30, B500SP (stropy, płyta fundamentowa, ściany); Żelbet C30/37 XC4/XF1 (krawędzie płyt wysuniętych, attyki, belki) — 45° na przemian ciągłe i przerywane
- Podbudowa nawierzchni (kruszywo)

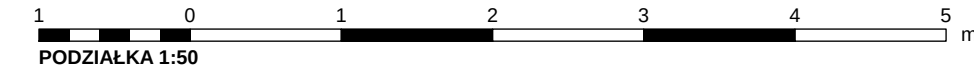

REW.		OPIS ZMIANY		DATA	
0		Wydanie — rysunek wygenerowany z modelu		2026-09-25	
PRACOWNIA PROJEKTOWA PRACOWNIA PROJEKTOWA — nazwa do uzupełnienia				STADIUM PB	BRANŻA ARCHITEKTURA (AR)
adres pracowni do uzupełnienia					
INWESTOR (do uzupełnienia)					
OBJEKT / NAZWA ZAMIERZENIA BUDOWLANEGO Budynek mieszkalny jednorodzinny wolnostojący „Dom LAMELA”					
ADRES / LOKALIZACJA (NR DZIAŁKI, OBRĘB, JEDN. EWIDENCYJNA) ul. Lipowa (fikcyjna), dz. nr ewid. 1234, obręb 0005 Przykładowo, gm. Przykładowo (fikcyjna)					KAT. OBJEKTU I
FUNKCJA		IMIĘ I NAZWISKO		SPECJALNOŚĆ, NR UPRAWNIENI	DATA
Podpis		Podpis		Podpis	Podpis
Projektant					
Projektant (wsp.)					
Sprawdzający					
Opracował					
TYTUŁ RYSUNKU					
PRZĘKROJE A-A I B-B					
SKALA	FORMAT	DATA WYDANIA	RODZAJ DOK.	NR RYSUNKU	ARKUSZ
1:50	1130x420	2026-09-25	przekrój	PB-AR-04	4/5
					REW.
					0

A
B
C
D
E
F

 

- KOLORYSTYKA I MATERIAŁY ELEWACJI**
- 1 ETICS: warstwa zbrojona + tynk silikonowy 1,5 mm (biały) / jasnoszary NCS S 1500-N [TYNK_SIL]
 - 2 Szkło (szyby zespolone) [SZKŁO]
 - 3 Membrana fasadowa wiatrozłocząca UV-stabilna, czarna (sd = 0,02 m) [MEMB_WIATR]
 - 4 Lamelle elewacyjne 40x80 mm, drewno termooferowane (klasa 1 trwałości), olejowane [DREWNO_TERMO]
 - 5 Żelbet C30/37 XC4/FX1 (krawędzie płyty wysuniętych, atyki, belki) [ZB_C30]
 - 6 Stalarka — profile aluminiowe, antracyt [RAMA_ALU]
 - 7 Rama boku C: ruszt stalowy ocynkowany w okładzinie z blachy aluminiowej RAL 7016 (pusta w środku) [RAMA_C]
 - 8 Podbudowa nawierzchni (rusztywo) [NAW_PODBUDOWA]
 - 9 Drzwi zewnętrzne, płycina aluminiowa [DRZWI_ZEWNI]
 - 10 Stal S235 ocynkowana ogniochronna, malowana proszkowo RAL 7016 — kratownica przycięta (pręty E12 w siatce 0,30 m; ramię 40x40) [STAL_OCYNK]
 - 11 Stal malowana proszkowo (balustrady, rylce) [STAL_BAL]
 - 12 Podsiłka zewnętrzna: płyta włóknocementowa 12 mm na ruszcie, RAL 7016 [PODSUF]
 - 13 Obróbki blacharskie (blacha powlekana) [OBRÓBKA_BLACH]
 - 14 Deska tarasowa [NAW_DESKA]
 - 15 Styropian grafitowy EPS 031 (ETICS, NRO w systemie) [EPS031]
 - 16 Brama garażowa segmentowa [BRAMA_GAR]

OBJAŚNIENIA I UWAGI

1. Wymiary w cm (mm w indeksie górnym, np. 24" = 24,5 cm), rzędne w m względem ±0,000 = 101,650 m n.p.m. (PL-EVRF2007-NH).

2. Różnice: różnica zaczerpniętych — poziom wykończony, niezaczerpnięty — poziom wykończony — poziom ±0,000 z rzędnej bezwzględnej (PN-B-01025).

3. Wysokość budynku wg § 6 WT: od terenu przy najniższym położonym wejściu (-0,267) do wierzchołka strzypochy D1 (+9,526) — H = 9,79 m (bez atyki).

4. Kolorystyka orientacyjna wg kolorów materiałów w modelu (dla powiększenia wzornikiem RAL/NCS).

5. Rysunek wygenerowany automatycznie z modelu model/budynki.yaml (wersja 1.0, 2026-09-25) — generatory lamela.views.

<				
--	--	--	--	--