


odcinek kontury 100 mm (wydruk 1:1)

RZUT PARTERU 1:50

REW.	OPIS ZMIANY			DATA	
0	Wydanie — rysunek wygenerowany z modelu			2026-09-25	
PRACOWNIA PROJEKTOWA PRACOWNIA PROJEKTOWA — nazwa do uzupełnienia adres pracowni do uzupełnienia				STADIUM PB	BRANŻA ARCHITEKTURA (AR)
INWESTOR (do uzupełnienia)					
OBJEKT / NAZWA ZAMIERZENIA BUDOWLANEGO Budynek mieszkalny jednorodzinny wolnostojący „Dom LAMELA”					
ADRES / LOKALIZACJA (NR DZIAŁKI, OBRĘB, JEDN. EWIDENCYJNA) ul. Lipowa (fikcyjna), dz. nr ewid. 1234, obręb 0005 Przykładowo, gm. Przykładowo (fikcyjna)					KAT. OBJEKTU I
FUNKCJA	IMIĘ I NAZWISKO	SPECJALNOŚĆ, NR UPRAWNIEN	DATA	PODPIS	
Projektant					
Projektant (wsp.)					
Sprawdzający					
Opracował					
TYTUŁ RYSUNKU					
RZUT PARTERU					
SKALA 1:50	FORMAT A1	DATA WYDANIA 2026-09-25	RODZAJ DOK. Izot.	NR RYSUNKU PB-AR-01	ARKUSZ 1/10
					REW. 0

OBJAŚNIENIA I UWAGI

- Wymiary w cm (mm w indeksie górnym, np. 24⁵ = 24,5 cm), rzędne w m względem ±0,000 = 101,650 m n.p.m. (PL-EVRF2007-NH).
- Rzuty: płaszczyzna cięcia +1,10 m nad posadzką kondygnacji. Linia kreskowa — elementy nad płaszczyznę cięcia (obrysy płyt i wsporników, brył wyższych kondygnacji, otwory w stropie nad, belki); linia cienka — elementy poniżej (widok).
- Otwory: licznik — szerokość, mianownik — wysokość w świetle muru, w nawiasie wysokość parapetu; symbol stolarki wg zestawienia stolarki.
- Numeracja pomieszczeń wg PN-B-01025 / PN-EN ISO 4157-2: <nr kondygnacji> (parter = 1) > <nr> identyfikator w modelu: <kond> <nr> (parter = 0).
- Drzwi: strona otwierania (lewej/prawej) wg modelu — patrzeć od strony, w którą otwiera się skrzydło.
- Rysunek wygenerowany automatycznie z modelu /modeluser/aihouse/model/budynek.yamł (wersja 1.0, 2026-09-25) — generatory lamela.views.

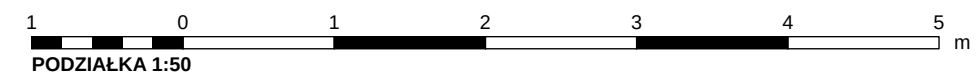

ZESTAWIENIE POMIESZCZEŃ

Nr	Nazwa pomieszczenia	Posadzka	Kat.	Wys. [m]	Pow. [m²]
1.06	Salon + jadalnia + kuchnia	Deska warstwowa dębowa 15 mm, klejona	podst.	2,77	54,44
1.13	Garaż 2-stanowiskowy	Posadzka żywiczna epoksydowa antypoślizgowa	podst.	2,76	37,42
1.10	Pokój gościnny / gabinet	Deska warstwowa dębowa 15 mm, klejona	podst.	2,77	12,52
1.12	Pomieszczenie techniczne	Płytki gresowe 60×120 na kleju C2TE S1 techn.	podst.	2,76	8,85
1.11	Przedśrodek gospodarczy	Płytki gresowe 60×120 na kleju C2TE S1 ruchu	podst.	2,76	7,18
1.02	Hol	Płytki gresowe 60×120 na kleju C2TE S1 ruchu	podst.	2,77	4,44
1.01	Wiatrołap	Płytki gresowe 60×120 na kleju C2TE S1 ruchu	podst.	2,77	3,89
1.09	Łazienka gościnna (natrysk)	Płytki gresowe 60×120 na kleju C2TE S1 pomoc.	podst.	2,77	3,86
1.07	Pas komunikacyjny przy schodach	Deska warstwowa dębowa 15 mm, klejona	podst.	2,77	3,51
1.16	Schowek pod spocznikiem (h < 1,40)	Płytki gresowe 60×120 na kleju C2TE S1 pomoc.	podst.	1,37	2,91
1.04	Klatka schodowa	Deska warstwowa dębowa 15 mm, klejona	podst.	2,77	2,78
1.03	WC gościnne	Płytki gresowe 60×120 na kleju C2TE S1 pomoc.	podst.	2,77	2,32
1.08	Przedpokój gościnny	Deska warstwowa dębowa 15 mm, klejona	podst.	2,77	1,46
1.15	Schowek pod schodami (h 1,40-2,20)	Płytki gresowe 60×120 na kleju C2TE S1 pomoc.	podst.	1,80	1,45
1.05	Śpiżarnia	Płytki gresowe 60×120 na kleju C2TE S1 pomoc.	podst.	2,77	1,02
1.14	Szacht instalacyjny SI		techn.	2,77	0,45
RAZEM powierzchnia netto					148,49
w tym użytkowa (podst. + pomoc.)					115,93

OZNACZENIA MATERIAŁÓW (PN-B-01030 + przyjęte)

	Wełna mineralna 035 (szkielet, docieplenia, ściana dom-garaż) — meander „UUU”		Stal konstrukcyjna S355 (słupy RK, rama boksu C), cynkowana ognioowo + malowana proszkowo RAL 7016 — zabezpieczenie
	Styropian grafitylowy EPS 031 (ETICS, NRO w systemie) — zrygawk „VVV”		Ścianka szklana VSG 2 × 8 mm w ramie aluminiowej (wiatrołap / hol)
	Bloczek wapniowo-piaskowy 12 cm, kl. 15 (ścianki działowe, licowy w klatce); Bloczek wapniowo-piaskowy (silikat) 18 cm, kl. 20, gr. 1, na zaprawie cienkowarstwowej — kratka ukośna 45°/135°		Żelbet C25/30, B500SP (stropy, płyta fundamentowa, ściany) — 45° na przemienną cięgę i przerywane

OZNACZENIA LINII

- elementy nad płaszczyznę cięcia (obrysy płyt, wsporników, brył wyższych kondygnacji)
- elementy poniżej płaszczyzny cięcia (widok z góry)
- osie konstrukcyjne; linia punktowa z pogrubionymi końcami — ślad przekroju

