


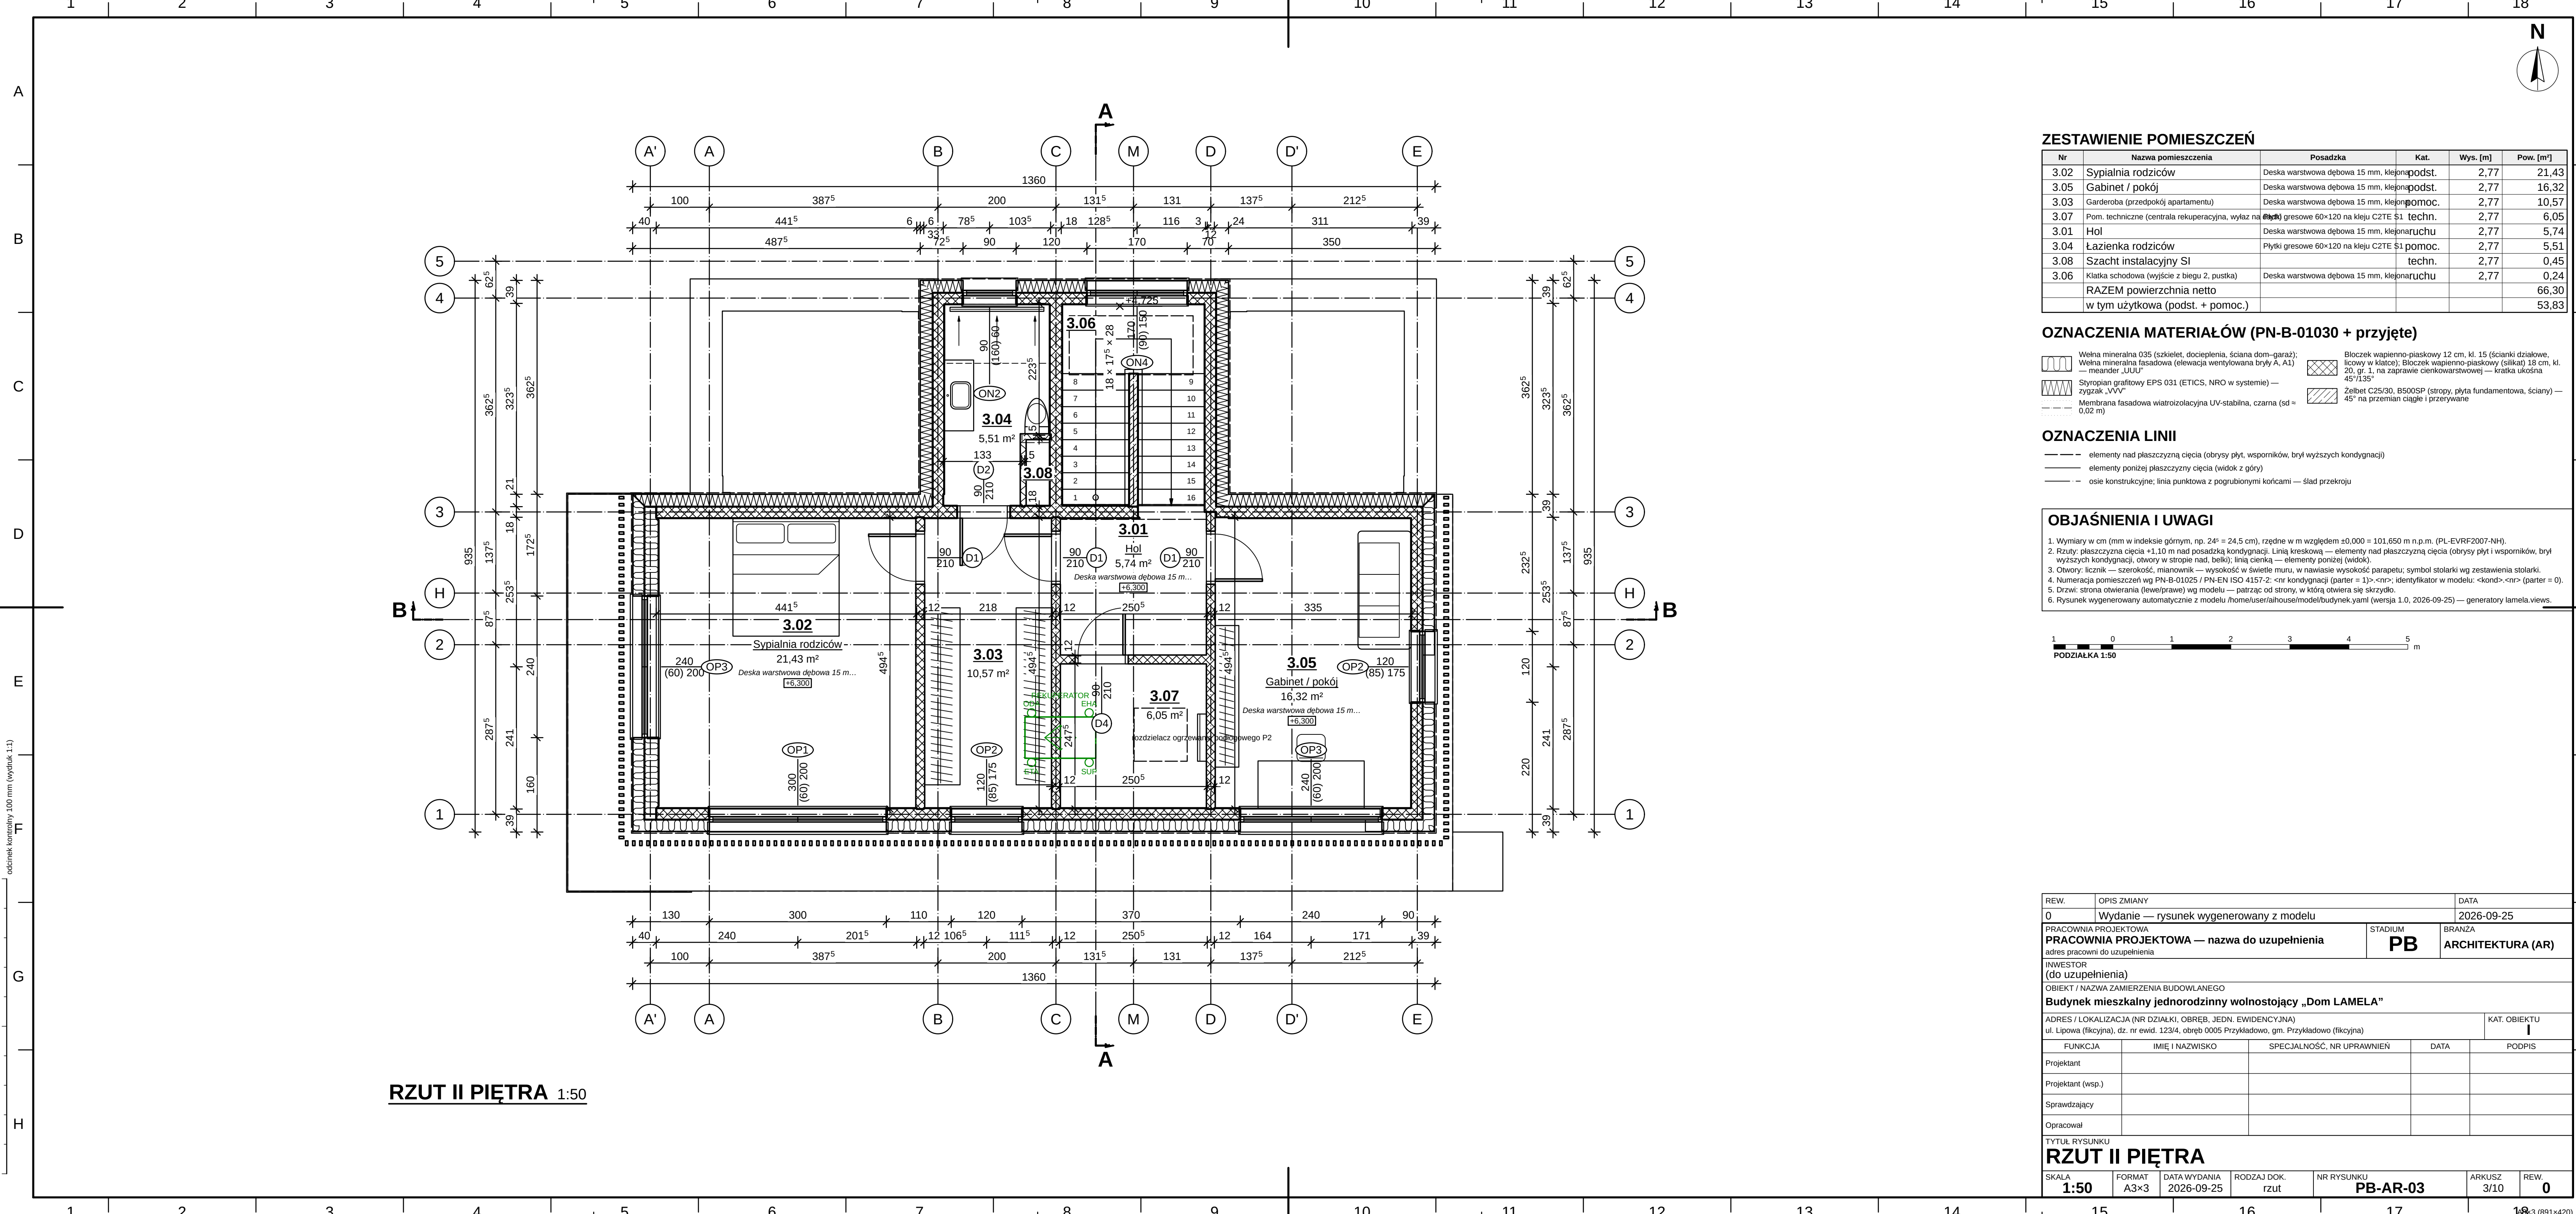

RZUT II PIĘTRA 1:50

ZESTAWIENIE POMIESZCZEŃ

Nr	Nazwa pomieszczenia	Posadzka	Kat.	Wys. [m]	Pow. [m²]
3.02	Sypialnia rodziców	Deska warstwowo-dębowa 15 mm, klejona	podst.	2,77	21,43
3.05	Gabinet / pokój	Deska warstwowo-dębowa 15 mm, klejona	podst.	2,77	16,32
3.03	Garderoba (przedpokój apartamentu)	Deska warstwowo-dębowa 15 mm, klejona	pomoc.	2,77	10,57
3.07	Pom. techniczne (centrala rekuperacyjna, wylaz na dach)	Płyty gresowe 60x120 na kleju C2TE \$1	techn.	2,77	6,05
3.01	Hol	Deska warstwowo-dębowa 15 mm, klejona	aruchu	2,77	5,74
3.04	Łazienka rodziców	Płytki gresowe 60x120 na kleju C2TE \$1	pomoc.	2,77	5,51
3.08	Szacht instalacyjny SI		techn.	2,77	0,45
3.06	Klatka schodowa (wyjście z biegu 2, pustka)	Deska warstwowo-dębowa 15 mm, klejona	aruchu	2,77	0,24
RAZEM powierzchnia netto					66,30
w tym użytkowa (podst. + pomoc.)					53,83

OZNACZENIA MATERIAŁÓW (PN-B-01030 + przyjęte)


	Wetna mineralna 035 (szkielet, docieplenia, ściana dom-garaż); Wetna mineralna fasadowa (elewacja wentylowana bryły A, A1) — meander „JU”		Blotek wapienno-piaskowy 12 cm, kl. 15 (ścianki działowe, łicowy w klatce); Blotek wapienno-piaskowy (słikat) 18 cm, kl. 20, gr. 1, na zaprawie cienkowarstwowej — klatka ukosna 45°/135°
	Styropian gąbłowy EPS 031 (ETICS, NRO w systemie) — zygzak „VVV”		Żelbet C25/30, B500SP (stropy, płyta fundamentowa, ściany) — 45° na przemienną ciągłą i przerywaną
	Membrana fasadowa wiatroizolacyjna UV-stabilna, czarna (sd = 0,02 m)		

OZNACZENIA LINII

- elementy nad płaszczyzną cięcia (obryszy płyt, wsporników, brył wyższych kondygnacji)
- elementy poniżej płaszczyzny cięcia (widok z góry)
- osie konstrukcyjne; linia punktowa z pogrubionymi końcami — ślad przekroju

OBJAŚNIENIA I UWAGI

- Wymiary w cm (mm w indeksie górnym, np. 24^o = 24,5 cm), rzędne w m względem ±0,000 = 101,650 m n.p.m. (PL-EVRF2007-NH).
- Rzuty: płaszczyzna cięcia +1,10 m nad posadzką kondygnacji. Linia kreskowa — elementy nad płaszczyzną cięcia (obryszy płyt i wsporników, brył wyższych kondygnacji, otwory w stropie nad, belki); linia cienka — elementy poniżej cięcia (obryszy płyt i wsporników, brył niższych kondygnacji).
- Otwory: licznik — szerokość, mianownik — wysokość w świetle muru, w nawiasie wysokość parapetu; symbol stolarki wg zestawienia stolarki.
- Numeracja pomieszczeń wg PN-B-01025 / PN-EN ISO 4157-2: <nr kondygnacji (parter = 1)>.<nr>; identyfikator w modelu: <kond>.<nr> (parter = 0).
- Drzwi: strona otwierania (lewe/prawe) wg modelu — patrząc od strony, w którą otwiera się skrzydło.
- Rysunek wygenerowany automatycznie z modelu /home/user/aihouse/model/budynek.yaml (wersja 1.0, 2026-09-25) — generatory lamela.views.

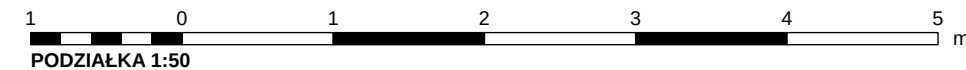

REW.	OPIS ZMIANY			DATA	
0	Wydanie — rysunek wygenerowany z modelu			2026-09-25	
PRACOWNIA PROJEKTOWA				STADIUM	BRANŻA
PRACOWNIA PROJEKTOWA — nazwa do uzupełnienia				PB	ARCHITEKTURA (AR)
adres pracowni do uzupełnienia					
INWESTOR					
(do uzupełnienia)					
OBIEKT / NAZWA ZAMIERZENIA BUDOWLANEGO					
Budynek mieszkalny jednorodzinny wolnostojący „Dom LAMELA”					
ADRES / LOKALIZACJA (NR DZIAŁKI, OBRĘB, JEDN. EWIDENCYJNA)					KAT. OBIEKTU
ul. Lipowa (fikcyjna), dz. nr ewid. 123/4, obręb 0005 Przykładowo, gm. Przykładowo (fikcyjna)					I
FUNKCJA	IMIĘ I NAZWISKO	SPECJALNOŚĆ, NR UPRAWNIENI	DATA	PODPIS	
Projektant					
Projektant (wsp.)					
Sprawdzający					
Opracował					
TYTUŁ RYSUNKU					
RZUT II PIĘTRA					
SKALA	FORMAT	DATA WYDANIA	RODZAJ DOK.	NR RYSUNKU	ARKUSZ
1:50	A3x3	2026-09-25	rzut	PB-AR-03	3/10
					REW.
					0