


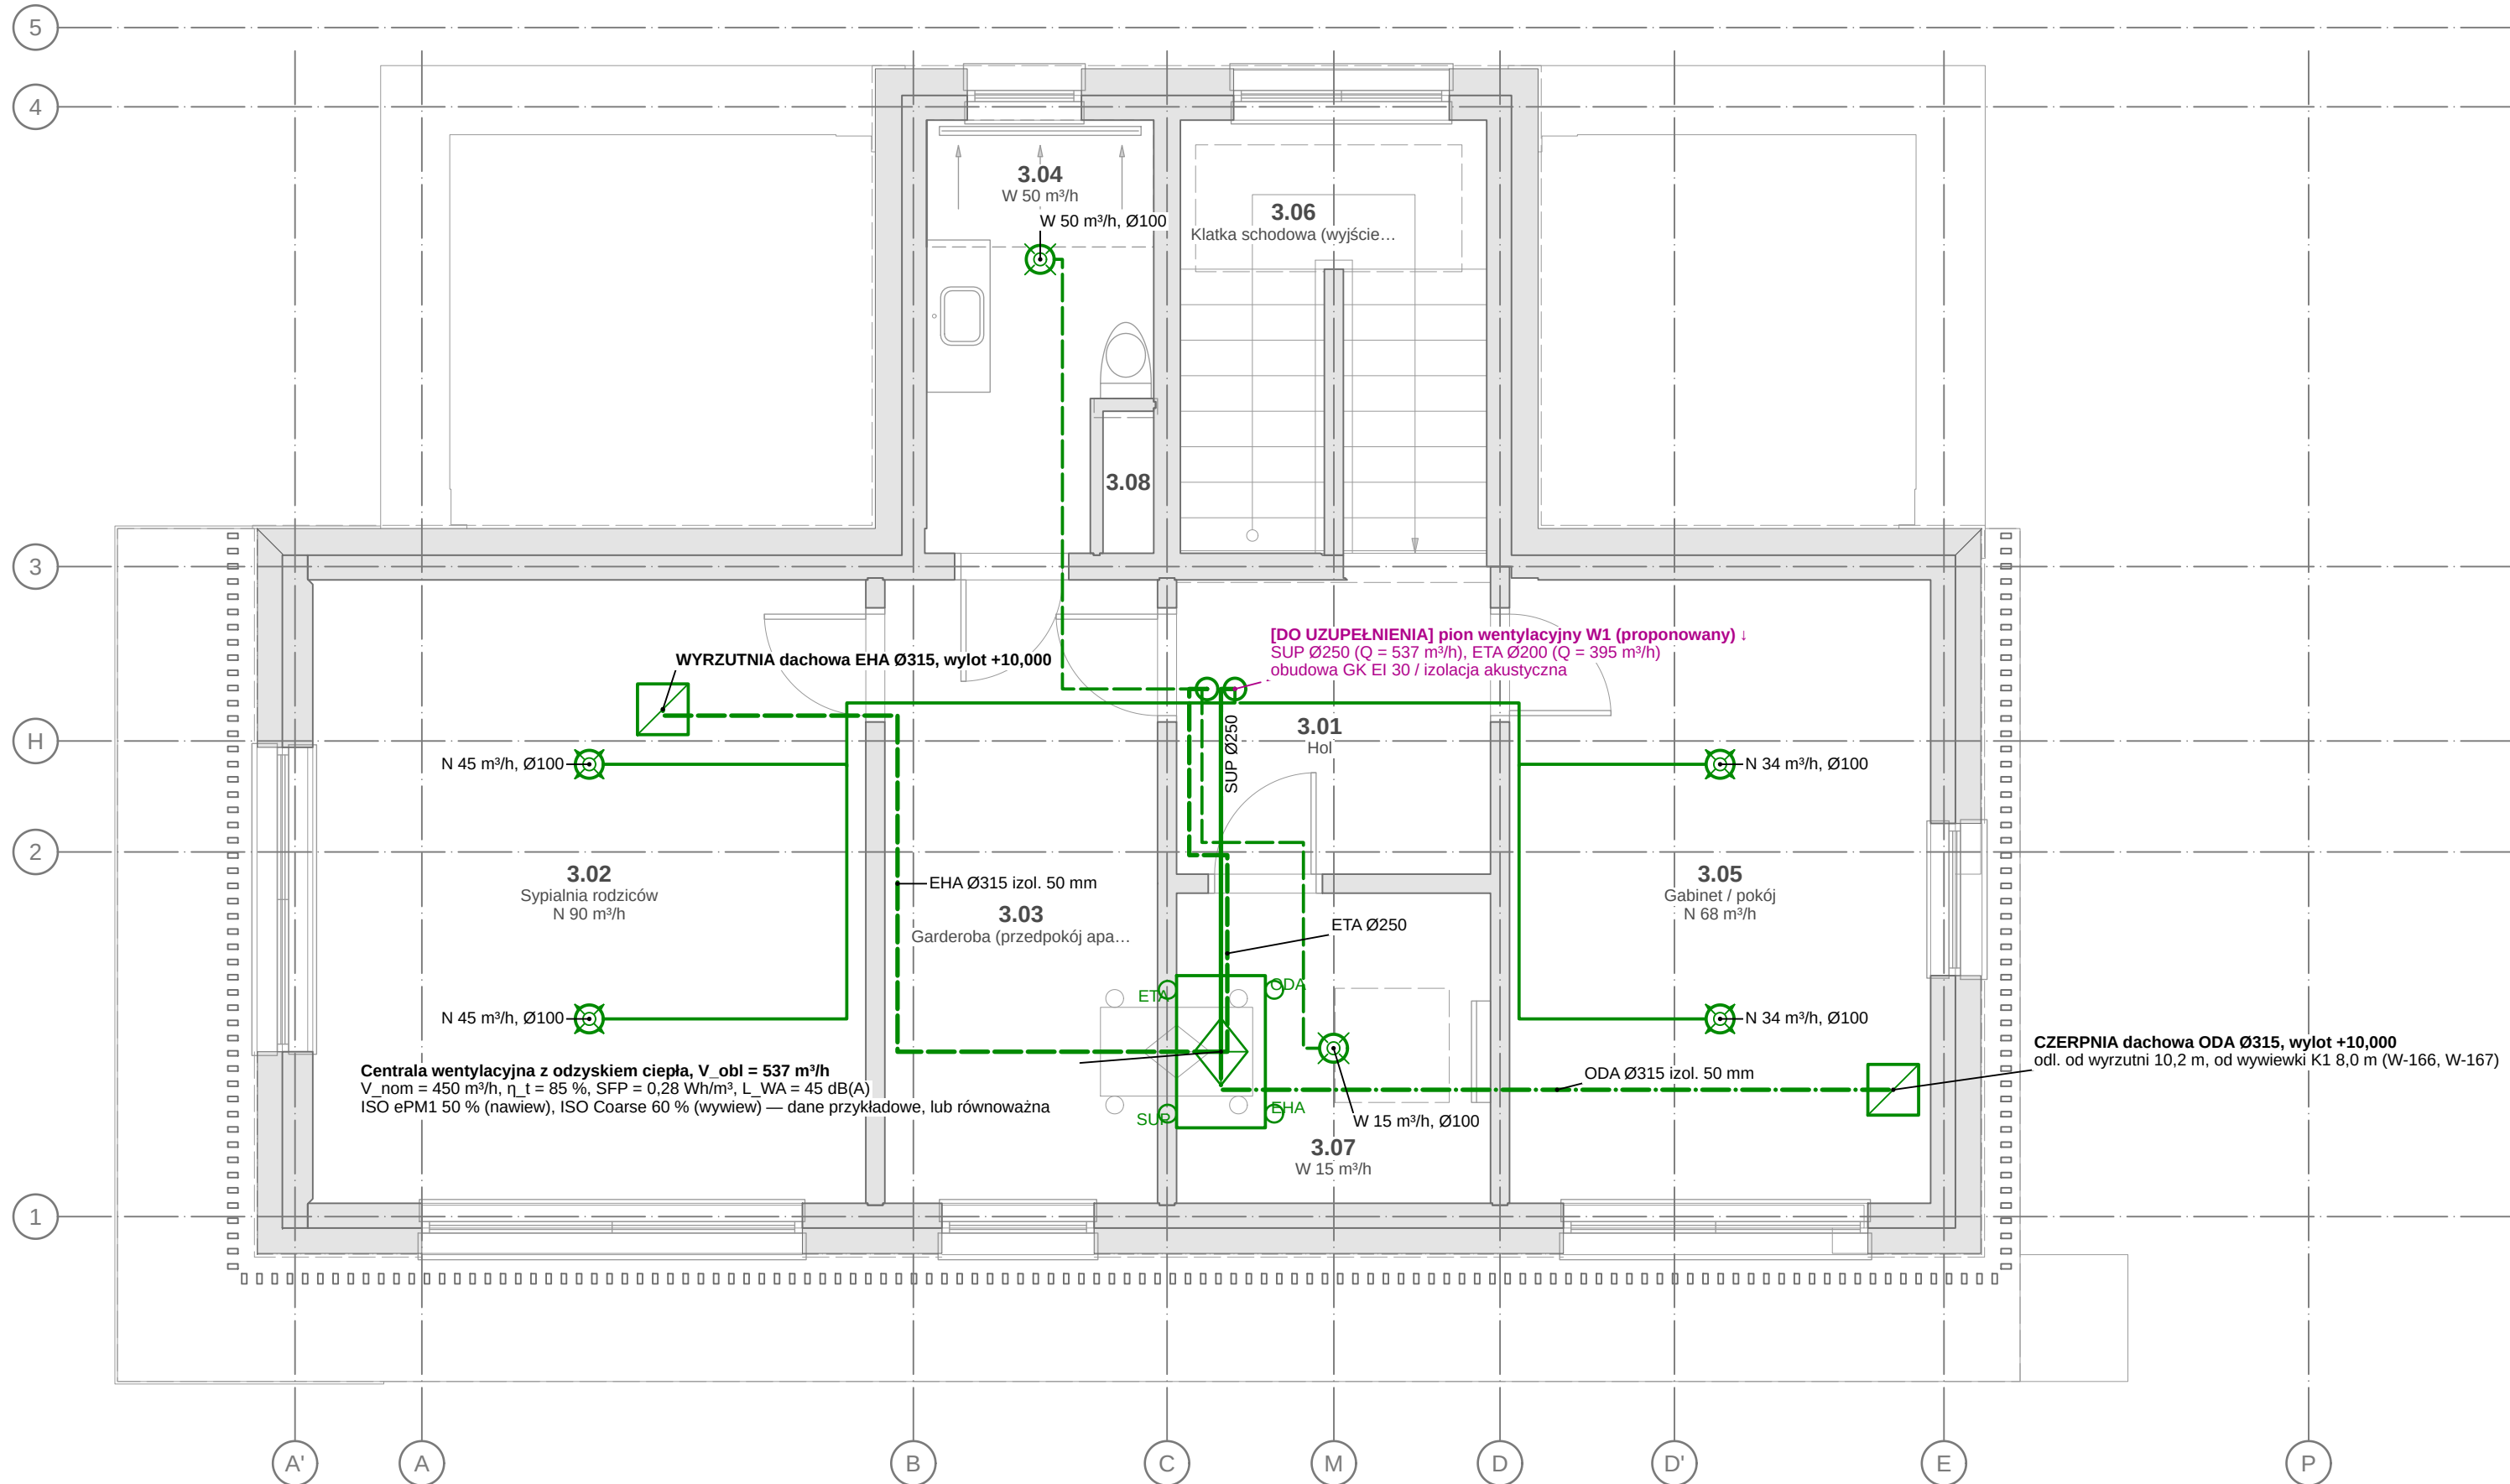

WENTYLACJA MECHANICZNA — RZUT II PIĘTRA 1:50

OZNACZENIA — LEGENDA SYMBOLI

Oznaczenia instalacji sanitarnych — praktyka branżowa (PN-B-01410, PN-B-01411, PN-B-01430 — normy wycofane, bez następcy); amatura i urządzenia wg PN-EN ISO 10628-2 / PN-EN ISO 14617; rodzaje powietrza wg PN-EN 16798-3 (ODA, SUP, ETA, EHA). Obowiązuje legenda na arkuszu.


—	podkład architektoniczny (rzut AR — ściany przecięte, stolarka, wyposażenie) — linie cienkie szare	⊗	wywieńnik (zawór wywieńnikowy) — W, wydatek [m³/h]
—	SUP — powietrze nawiewane (kanały okrągłe, izolowane w przestrzeniach nieogrzewanych)	⊙	⊙ pion wentylacyjny (kanał pionowy SUP/ETA)
—	ETA — powietrze wywiewane	⊙	ODA — powietrze zewnętrzne (czerpane), EHA — wyrzutowe; kanały izolowane paroszczelnie
⊗	nawiewnik (anemostat/zawór nawiewny) — N, wydatek [m³/h], średnica przyłącza	⊙	ODA — powietrze zewnętrzne (czerpane), EHA — wyrzutowe; kanały izolowane paroszczelnie

STRUMIENIE POWIETRZA — P2 [m³/h]

Pom.	Nazwa	Nawiew	Wywiew
2.02	Sypialnia rodziców	90	—
2.04	Łazienka rodziców	—	50
2.05	Gabinet / pokój	68	—
2.07	Pom. techniczne (centrala reku	—	15

OBJAŚNIENIA I UWAGI

- Średnice przewodów w mm (d, 2xS — rury wielowarstwowe, Ø/DN — kanalizacja, kanały wentylacyjne), przekroje żył w mm², odległości i rzędne w m; ±0,000 = 101,650 m n.p.m. (PL-EVRF2007-NH).
- Rysunki instalacji na podkładzie rzutów architektury (PB-AR); podkład — linie cienkie szare (warstwy I-PODKŁAD).
- Wentylacja mechaniczna nawiewno-wywiewna z odzyskiem ciepła wg WT § 147–150 i PN-EN 16798-3 (oznaczenia ODA/SUP/ETA/EHA); strumienie powietrza z bilansu wentylacji (lamela.obliczenia.energia.wentylacja, PN-B-03430/Az3 powołana w WT § 149) — nawiew do pokoi, wywiew z kuchni, łazienek, WC, pralni, sypialni.
- Średnice kanałów dobrane dla v ≤ 2,5 m/s (przyłącza) i ≤ 3,5 m/s (pnie); kanały okrągłe stalowe ocynkowane (typu spiro) lub system rozdzielaczy z przewodami elastycznymi (lub równoważne), z tłumikami akustycznymi za centralą; przepływ powietrza między pomieszczeniami przez podcięcie drzwi ≥ 1 cm (przepływ transferowy).
- Trasy kanałów i lokalizację pionu wyznaczono algorytmicznie (ortogonalnie, w przestrzeni sufitów podwieszanych/stropów) — do koordynacji z konstrukcją i architekturą (sufity SUP, GK).
- Kanały ODA i EHA w obrębie budynku — izolacja paroszczelna ≥ 50 mm; kanały SUP/ETA w przestrzeniach nieogrzewanych — izolacja ≥ 50 mm. Okap kuchenny — z recyrkulacją (filtr węglowy).
- Bilans na rysunkach: Σ nawiew = 537 m³/h, Σ wywiew = 395 m³/h — strumienie = max(model, bilans modułu energii; bilans projektowy (minima PN-B3B-03430/Az3 + nawiew 20 m³/h-os., rozdział nawiewu proporcjonalnie do powierzchni pokoi, min. 20 m³/h na pokój)); nastawy regulacyjne nawiewników wywiewać do bilansu zrównoważonego przy rozruchu (PN-EN 12599).
- Rysunek wygenerowany automatycznie z modelu /home/user/aihouse/model/budynek.yaml (wersja 1.0, 2026-09-25) — generatory lamela.views.

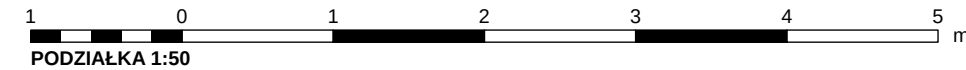

REW.	OPIS ZMIANY	DATA
0	Wydanie — rysunek wygenerowany z modelu	2026-09-25
PRACOWNIA PROJEKTOWA PRACOWNIA PROJEKTOWA — nazwa do uzupełnienia	STADIUM PT	BRANZA INSTALACJE SANITARNE (IS)
adres pracowni do uzupełnienia	INWESTOR (do uzupełnienia)	
OBIEKT / NAZWA ZAMIERZENIA BUDOWLANEGO Budynek mieszkalny jednorodzinny wolnostojący „Dom LAMELA”		
ADRES / LOKALIZACJA (NR DZIAŁKI, OBRĘB, JEDN. EWIDENCYJNA) ul. Lipowa (fikcyjna), dz. nr ewid. 123/4, obręb 0005 Przykładowo, gm. Przykładowo (fikcyjna)	KAT. OBIEKTU I	
FUNKCJA	IMIĘ I NAZWISKO	SPECJALNOŚĆ, NR UPRAWNIENI
Projektant		DATA
Projektant (wsp.)		PODPIS
Sprawdzający		
Opracował		
TYTUŁ RYSUNKU WENTYLACJA MECHANICZNA — RZUT II PIĘTRA		
SKALA 1:50	FORMAT A3x3	DATA WYDANIA 2026-09-25
RODZAJ DOK. rzut instalacji	NR RYSUNKU PT-IS-14	ARKUSZ 14/17
REW. 0		