



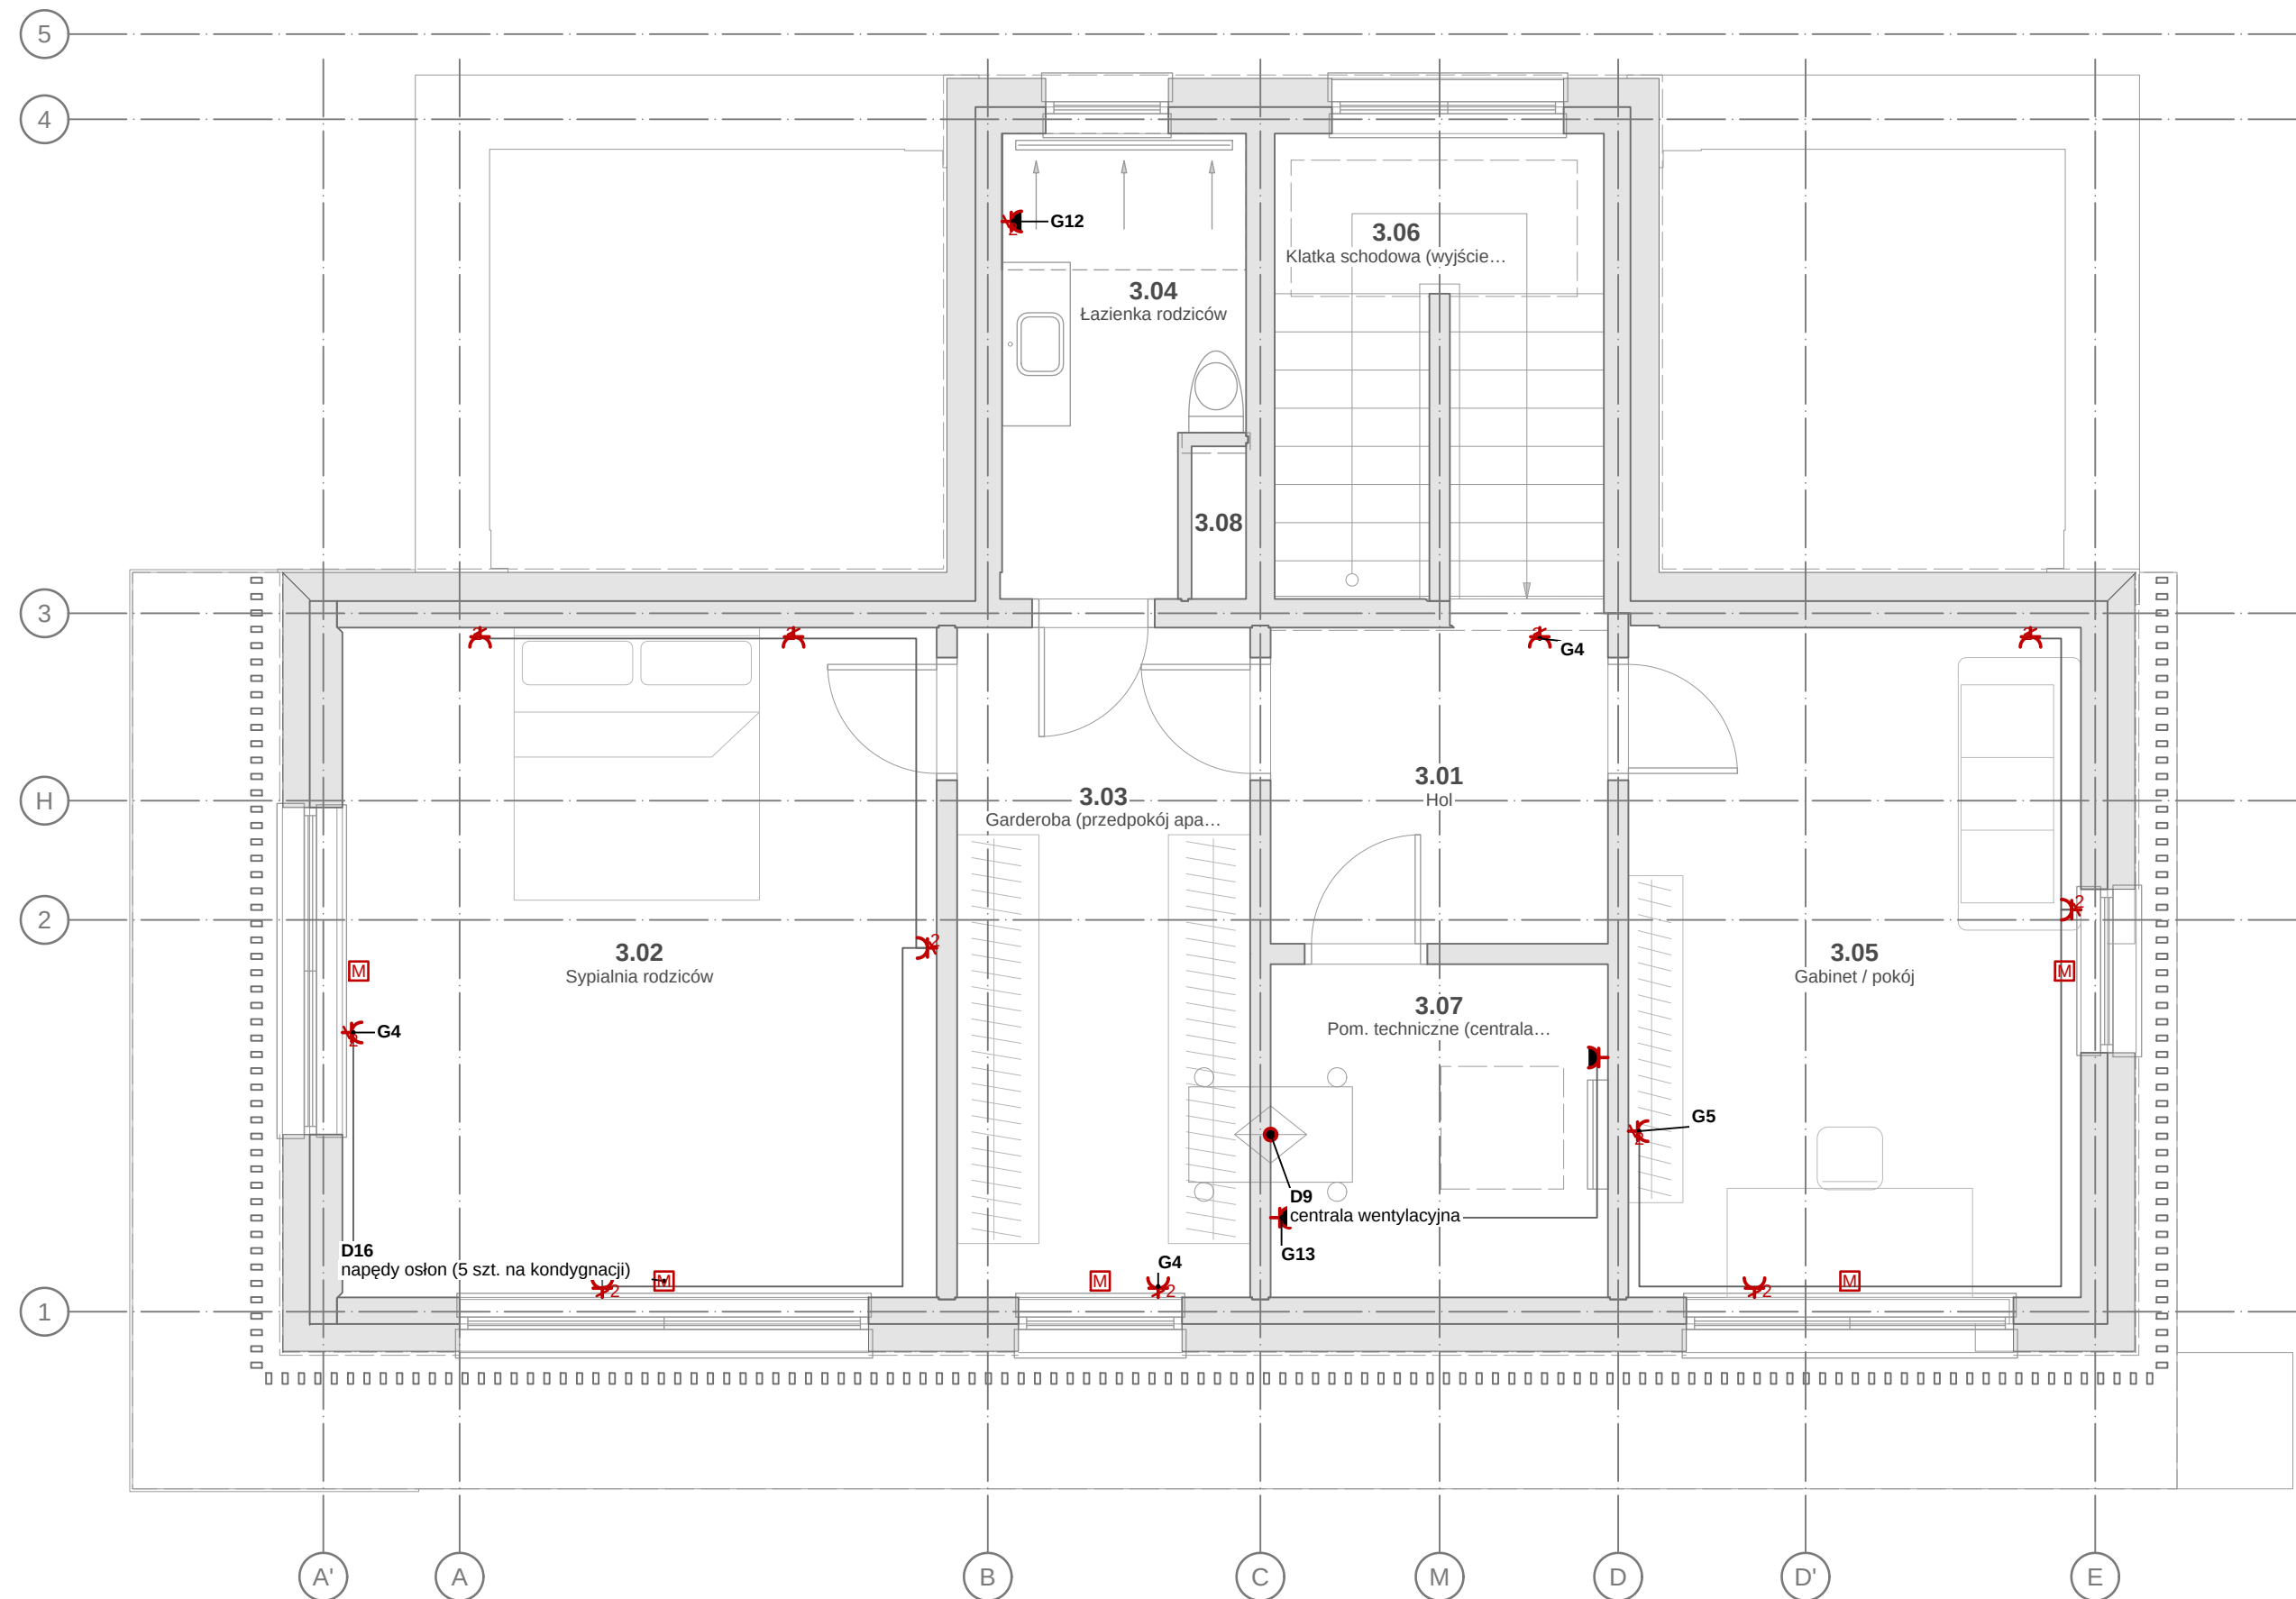

INSTALACJA GNIAZD WTYCZKOWYCH I ZASILANIA URZĄDZEŃ — RZUT II PIĘTRA 1:50

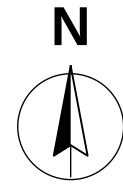

OZNACZENIA — LEGENDA SYMBOLI

Symbole instalacji elektrycznych wg IEC 60617 (baza IEC; PN-EN 60617 — wycofana, stosowana jako praktyka branżowa) i PN-EN ISO 14617; oznaczenia teletechniczne — praktyka branżowa. Obowiązuje legenda na arkuszu.


podłak architektoniczny (złut AR — ściany przeście, stolarka, wyposażenie) — linie ciemne szare przewody obwodów gniazdw YDYP 3x2,5 (5x2,5 — 3f) — połączenia punktów (przebieg schematów w trybie i w poszczególnych) gniazda wtyczkowe podwójne ze stykiem ochronnym, h = 0,30 m (kuchnia nad blatem 1,10 m)	gniazdo bytowsko-europejskie IP44 (zaznaki h = 1,20 m, garaż, pom. techniczne, zewnętrzne) wypust / puszka przyłączeniowa urządzenia zasilanego na stałe (opis: obwod, urządzenie, moc) M — zasilanie napędu osłony przeciwoświecennej (zasilanie/screen) przy oknie
---	---

OBWODY NA ARKUSZU (lamela.obliczenia.elektryka.obwody)

Obw.	Odbiorniki	Zab.	Przewód	L [m]	ΔU [%]	Faza	RCD
G4	Gniazda P2: 2,02 Sympialni rodziców, 2,03 Garderoba	B16	YDyp 3x4	22,3	2,16	L2	RCBO typ A 30 mA
G5	Gniazda P2: 2,05 Gabinet / pokój	B16	YDyp 3x2,5	17,1	2,59	L3	RCBO typ A 30 mA
G12	Gniazda łazienki (2,04 Łazienka rodziców)	B16	YDyp 3x4	29,0	2,63	L3	RCBO typ A 30 mA
G13	Gniazda garażu / pom. technicznego (IP44)	B16	YDyp 3x2,5	5,5	1,25	L1	RCBO typ A 30 mA
D9	Rekuperator (V = 437 m³/h)	B10	YDyp 3x1,5	20,7	0,82	L3	RCBO typ A 30 mA
D16	Napędy osłon przysłoniwczych (19 szt.)	B10	YDyp 3x1,5	3,0	0,89	L1	RCBO typ A 30 mA

OBJAŚNIENIA I UWAGI

1. Średnice przewodów (m m, d zxs — rury wielowarstwowe, Ø/DN — kanalizacja, kanały wentylacyjne), przekroje żył w mm², odległości i rzędne w m; ±0,00 = 101,650 m n.p.m. (P-EVRF2007-NH).
2. Rysunki instalacji na podkładzie rzutu architektury (PB-AR); podkład — linie cienkie szare (warstwy I-PODKŁAD).
3. Instalacja gniazd wtyczkowych i zasilania urządzeń przy PN-HD 60364-5-52 (samoczynny wyłącznik różnicowy, RCD 30 mA dla gniazd ≤ 32 A — p. 411.3.3), PN-HD 60364-5-52 (przewody), PN 60364-7-701 (zazienki), PN-HD 60364-7-722 (dowodzenie EV), p. 170 i 180—(obwody gniazd oddzielnie od oświetlenia, gniazda ze systemem ochronnym).
4. Bilans mocy (lamela obliczenia, elektryczna bilans): P_{inst} = 73,4 kW, P_{szczyt} z DLM = 26,3 kW, P_{szczyt} z MW_{prz} = 27 kW, zabezpieczenie przedlicznikiem 40 A.
5. Liczbie i rozmieszczenie urządzeń wyznaczono algorytmicznie (praktyka branżowa, DIN 18015-2): przy łóżkach, biurkach, sofach, nad blatem kuchennym co ok. 1,1 m, przy umywalkach (poza strefą 0-2), pozostałe równomiernie wzdłuż garażu bez otworów; urządzenia stałe — wypoził gniazda dla długich obwodów D.
6. Wysokości montażu (od posadzki): gniazda 0,30 m; nad blatem 1,20 m; łazienki 1,20 m (P4); garaż, pom. techniczne 1,10 m (P4); łazienki 1,10 m.
7. Rysunek wygenerowany automatycznie z modelu /home/user/aihouse/model/budnek.yaml (wersja 1.0, 2026-09-25) — generatory lamela.views.

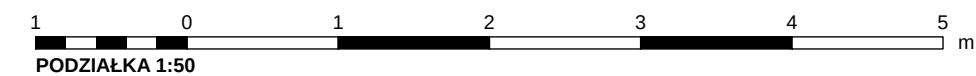

REW.	OPIS ZMIANY				DATA	
0	Wydanie — rysunek wygenerowany z modelu				2026-09-25	
PRACOWNIA PROJEKTOWA PRACOWNIA PROJEKTOWA — nazwa do uzupełnienia adres pracowni do uzupełnienia					STADIUM PT	BRANŻA INSTALACJE ELEKTRYCZNE (IE)
INWESTOR (do uzupełnienia)						
OBJEKT / NAZWA ZAMIERZENIA BUDOWLANEGO						
Budynek mieszkalny jednorodzinny wolnostojący „Dom LAMELA”						
ADRES / LOKALIZACJA (NR DZIAŁKI, OBRĘB, JEDN. EWIDENCYJNA) ul. Lipowa (fikcyjna), dz. nr ewid. 123/4, obręb 0005 Przykładowo, gm. Przykładowo (fikcyjna)						KAT. OBJEKTU I
FUNKCJA	IMIĘ I NAZWISKO		SPECJALNOŚĆ, NR UPRAWNIENI		DATA	PODPIS
Projektant						
Projektant (wsp.)						
Sprawdzający						
Opracował						
TYTUŁ RYSUNKU						
GNIAZDA I ZASILANIE URZĄDZEŃ — RZUT II PIĘTRA						
SKALA 1:50	FORMAT A3×3	DATA WYDANIA 2026-09-25	RODZAJ DOK. rzut instalacji	NR RYSUNKU PT-IE-06	ARKUSZ 6/14	REW. 0