



PRZĘKRÓJ A-A 1:50

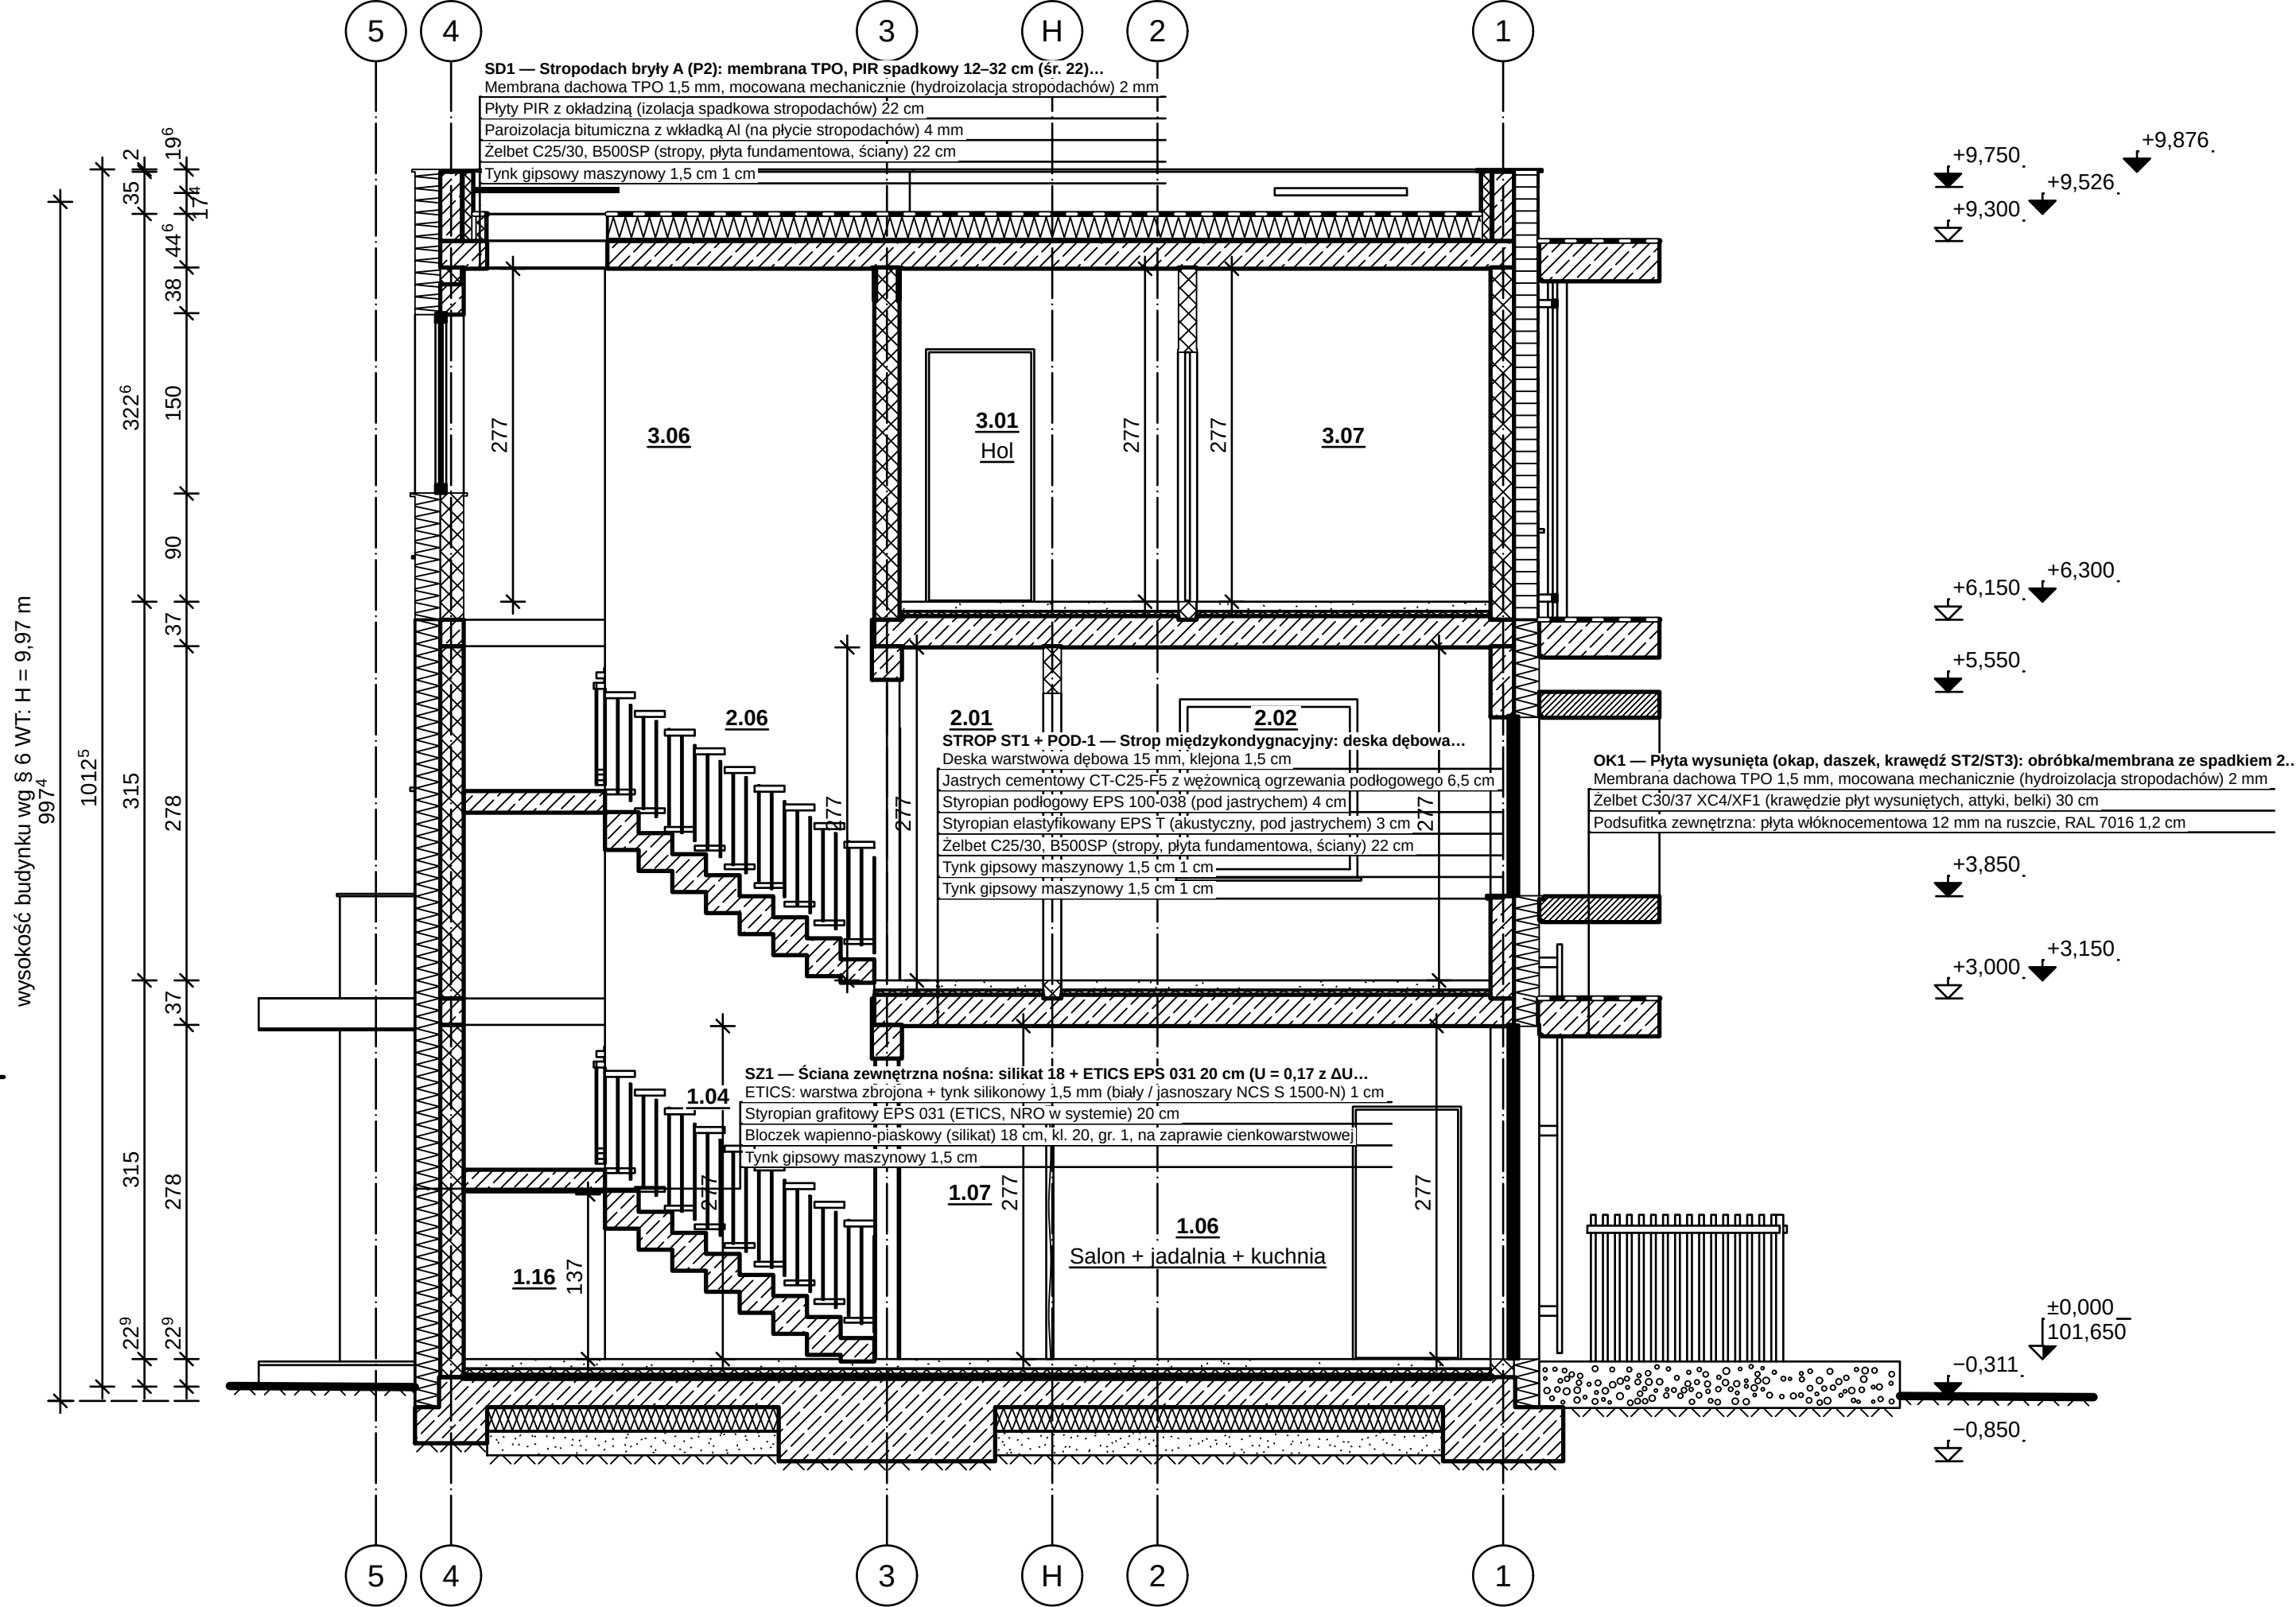

PRZĘKRÓJ B-B 1:50

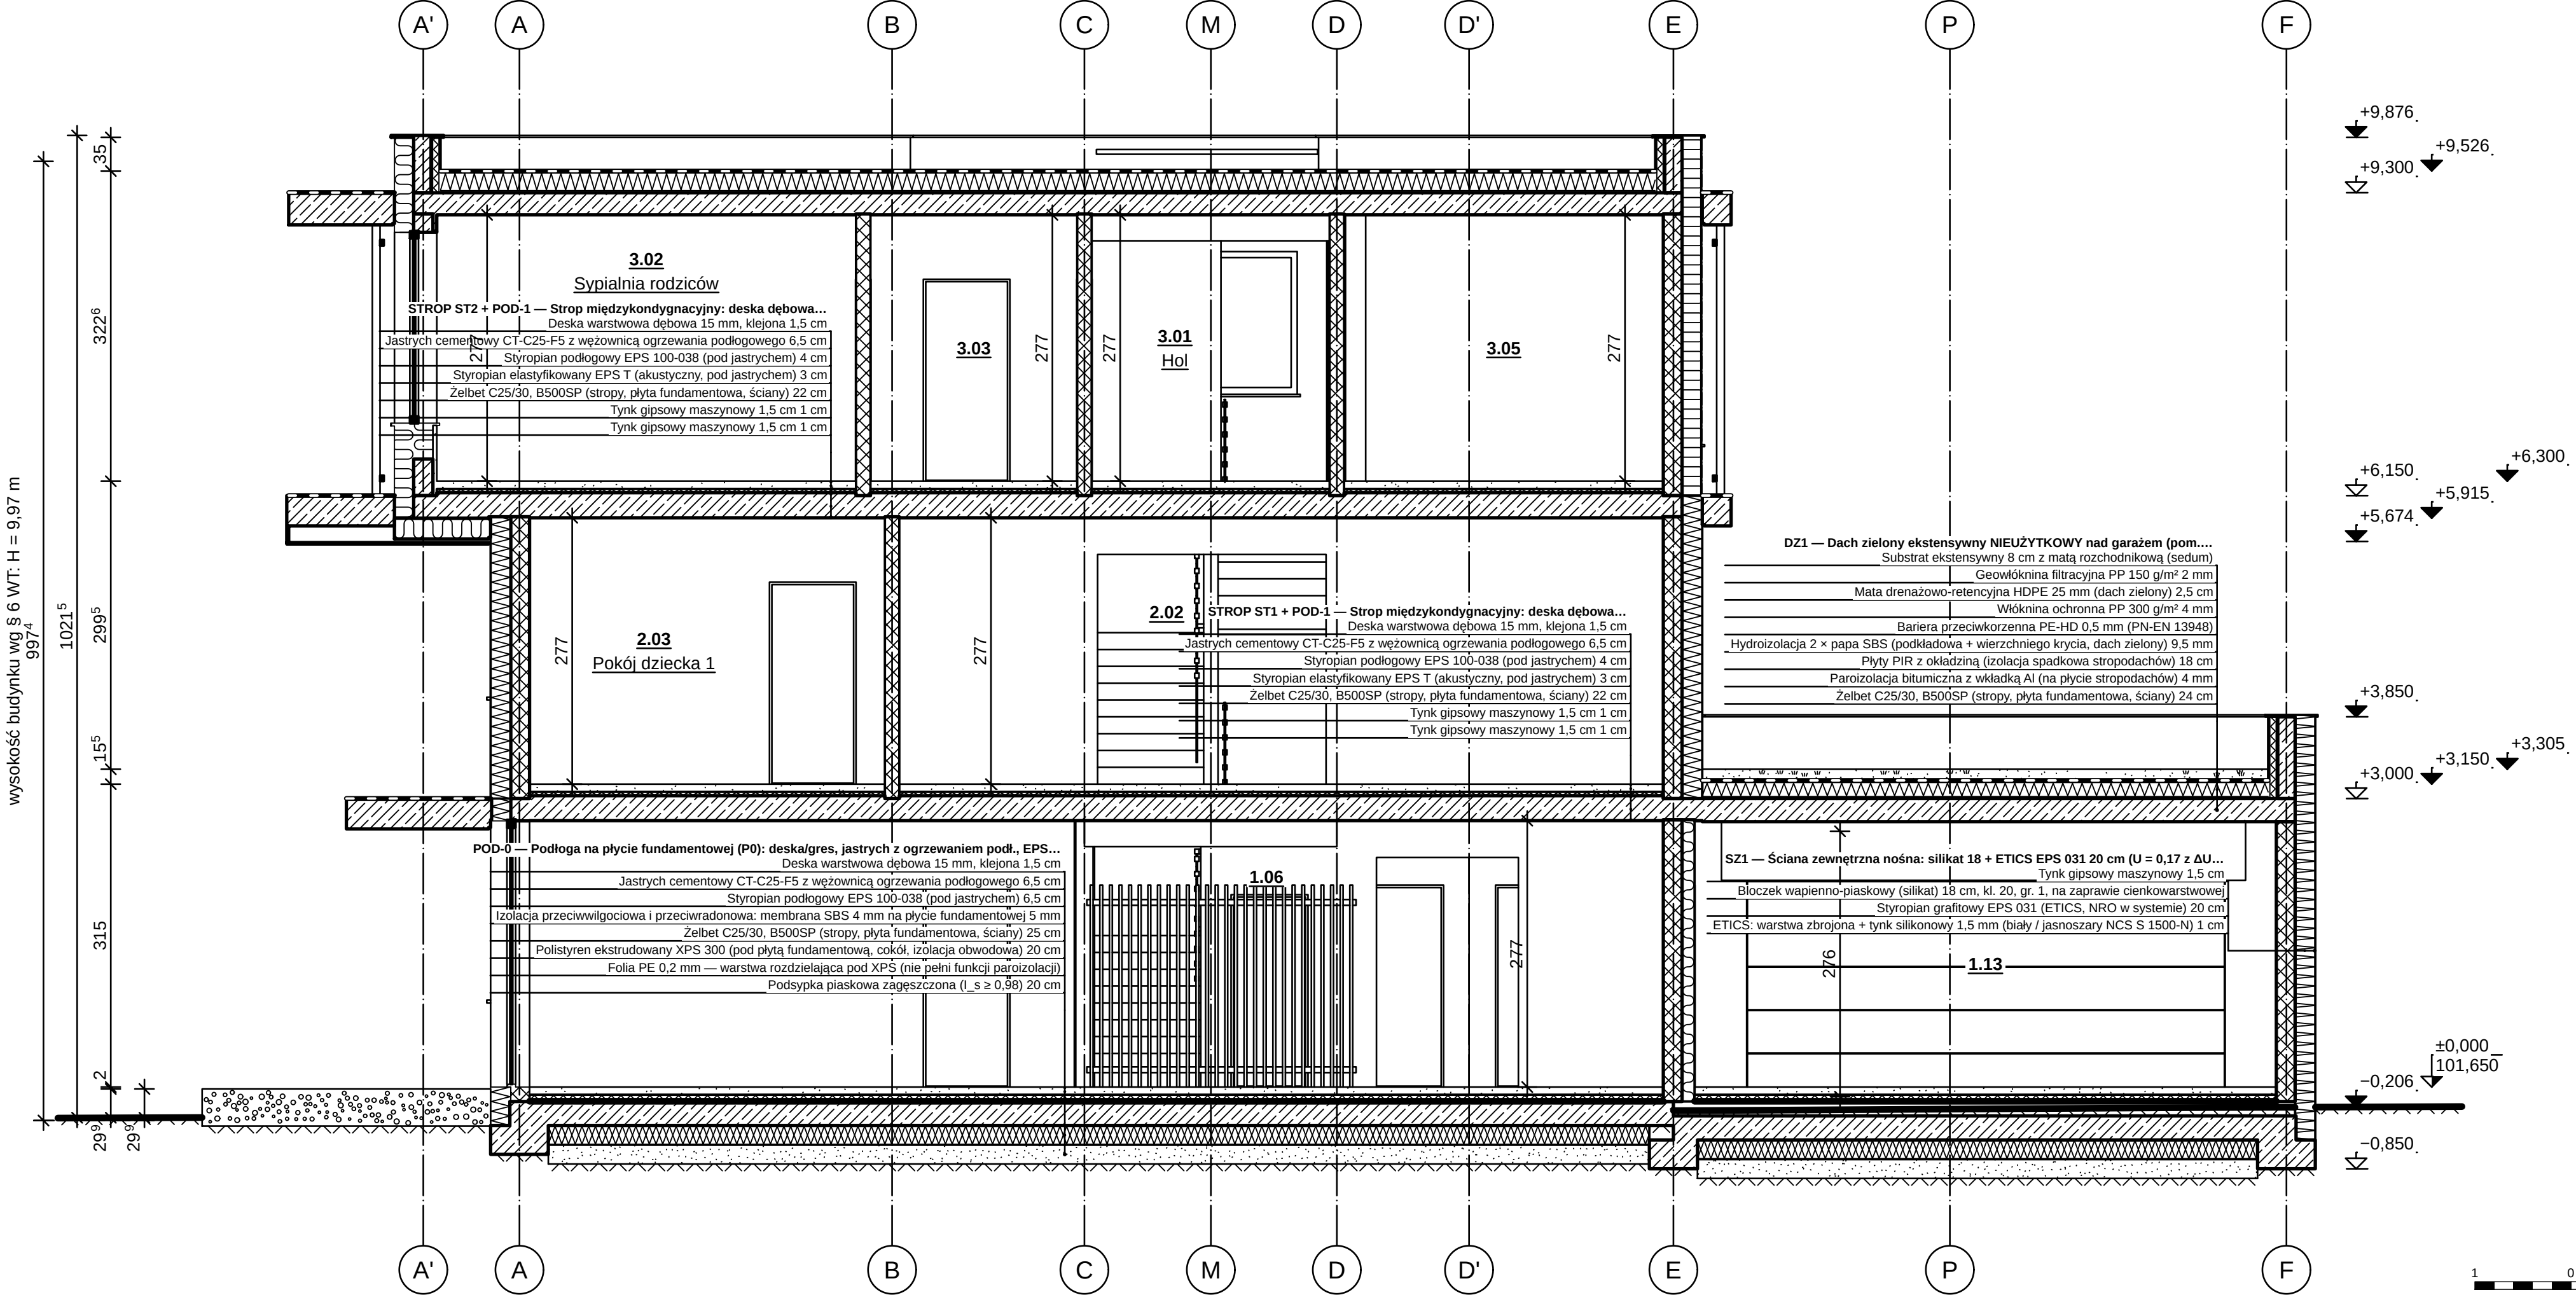


OZNACZENIA MATERIAŁÓW (PN-B-01030 + przyjęte)

- Lamele dębowe 30x60 mm (ekran komunikacji P0, h 2,10 m); Deska warstwowa dębowa 15 mm, klejona — przekrój wzdluż włókien
- grunt rodzimy
- Substrat ekstensywny 8 cm z matą rozchodnikową (sedum)
- Wełna mineralna fasadowa (elewacja wentylowana bryły A, A1); Wełna mineralna 035 (szkielet, docieplenia, ściana dom-garaz) — meander „U”/”
- Płyty PIR z okładziną (izolacja spadkowa stropodachów) — zrygask z okładzinami
- Izolacja przeciwwilgociowa i przeciwradowana: membrana SBS 4 mm na płycie fundamentowej — linia bardzo gruba
- Membrana dachowa TPO 1,5 mm, mocowana mechanicznie (hydroizolacja stropodachów); Hydroizolacja 2 x papa SBS (podkładowa + wierzchniego krycia, dach zielony) — pas czarno-biały
- Szyroplan grafitowy EPS 031 (ETICS, NRO w systemie); Szyroplan podłogowy EPS 100-038 (pod jaskrychem); Szyroplan elastyfikowany EPS T (akustyczny, pod jaskrychem) — zrygask „V”/”
- Polistyren ekstrudowany XPS 300 (pod płytą fundamentową, cokoł, izolacja obwodowa) — zrygask podkowy
- Jaskrychemy cementowy CT-C25-F5 z węzłownicą ogrzewania podłogowego — kropki
- Membrana fasadowa wiatroizolacyjna UV-stabilna, czarna (sd = 0,02 m)
- Błoczek wapienno-piaskowy 12 cm, kl. 15 (ściana działowa, lico w klatce); Błoczek wapienno-piaskowy (silikat) 18 cm, kl. 20, gr. 1, na zaprawie cienkowarstwowej — kratka ukośna 45°/135°
- Paroizolacja bitumiczna z wkładką Al (na płycie stropodachów) — linia kreskowa cienka 3/1 po ciepłej stronie
- Podsyłka piaskowa zagęszczona (l.s ≥ 0,98)
- Płyta gipsowo-kartonowa 12,5 mm (GKB / GKB1 w łazienkach); Podsyłka zewnętrzna: płyta włóknocementowa 12 mm na ruszcie, RAL 7016
- Opórki blacharskie (blacha powlekana); Stalarka — profile aluminiowe, antrycyt; Rama boksu C: ruszt stalowy ocynkowany w okładzinie z blachy aluminiowej RAL 7016 (pusta w środku); Stal malowana proszkowo (balustrady, ryle) — zacementowanie
- Szkoło (szyby zespolone); Ścianka szklana VSG 2 x 8 mm w ramie aluminiowej (wiatrak / hol)
- Zelbet C25/30, B500SP (stropy, płyta fundamentowa, ściany); Zelbet C30/37 XC4/XF1 (krawędzie płyt wysuniętych, atyki, belki) — 45° na przemięcie ciagle i przerywane
- Podbudowa nawierzchni (kruszywo)

OBJAŚNIENIA I UWAGI

- Wymiary w cm (mm w indeksie górnym, np. 24" = 24,5 cm), rzędne w m względem ±0,000 = 101,650 m n.p.m. (PL-EVRF-2007-144).
- Rzędne: trójką zaznaczony — poziom wykonczenia, niezaznaczony — konstrukcji, w połowie zaznaczony — poziom ±0,000 z rzędnią bezwzględna (PN-B-01025).
- Wysokość budynku wg § 6 WT: od terenu przy najniższym wejściu (-0,348) do wierzchu stropodachu D1 (+9,626) — H = 9,97 m (bez atyki).
- Opisy warstw: kod i nazwa przegrody z modelu, materiały i grubości wg modelu (od góry / od lewej).
- Przekrój A-A: opisy warstw pominięte na rysunku (brak miejsca w podziałce 1:50); POD-0, STROP ST2 + POD-1 — układ warstw wg zestawienia przegrod w części opisowej / przekroju 1:50.
- Przekrój B-B: opisy warstw pominięte na rysunku (brak miejsca w podziałce 1:50); STROP ST2Z + POD-1, SD1, OK1 — układ warstw wg zestawienia przegrod w części opisowej / przekroju 1:50.
- Rysunek wygenerowany automatycznie z modelu model/budynek.yaml (wersja 1.0, 2026-09-25) — generator lamela.views.

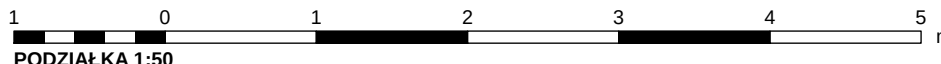

REW. 0		OPIS ZMIANY Wydanie — rysunek wygenerowany z modelu		DATA 2026-09-25	
PRACOWNIA PROJEKTOWA PRACOWNIA PROJEKTOWA — nazwa do uzupełnienia				STADIUM PB	BRANŻA ARCHITEKTURA (AR)
INWESTOR (do uzupełnienia)					
OBJEKT / NAZWA ZAMIERZENIA BUDOWLANEGO Budynek mieszkalny jednorodzinny wolnostojący „Dom LAMELA”					
ADRES / LOKALIZACJA (NR DZIAŁKI, OBRĘB, JEDN. EWIDENCYJNA) ul. Lipowa (fikcyjna), dz. nr ewid. 1234, obręb 0005 Przykładowo, gm. Przykładowo (fikcyjna)					KAT. OBJEKTU I
FUNKCJA	IMIĘ I NAZWISKO		SPECJALNOŚĆ, NR UPRAWNIENI	DATA	PODPIS
Projektant	[DO UZUPEŁNIENIA]		[DO UZUPEŁNIENIA]		
Projektant (wsp.)	[DO UZUPEŁNIENIA]		[DO UZUPEŁNIENIA]		
Sprawdzający	nie dotyczy (art. 20 ust. 3 pkt 2 PB)		—		
Opracował	[DO UZUPEŁNIENIA]		[DO UZUPEŁNIENIA]		
TYTUŁ RYSUNKU PRZĘKROJE A-A I B-B					
SKALA 1:50	FORMAT 1130x420	DATA WYDANIA 2026-09-25	RODZAJ DOK. przekrój	NR RYSUNKU PB-AR-04	ARKUSZ 4/5
				REW. 0	