


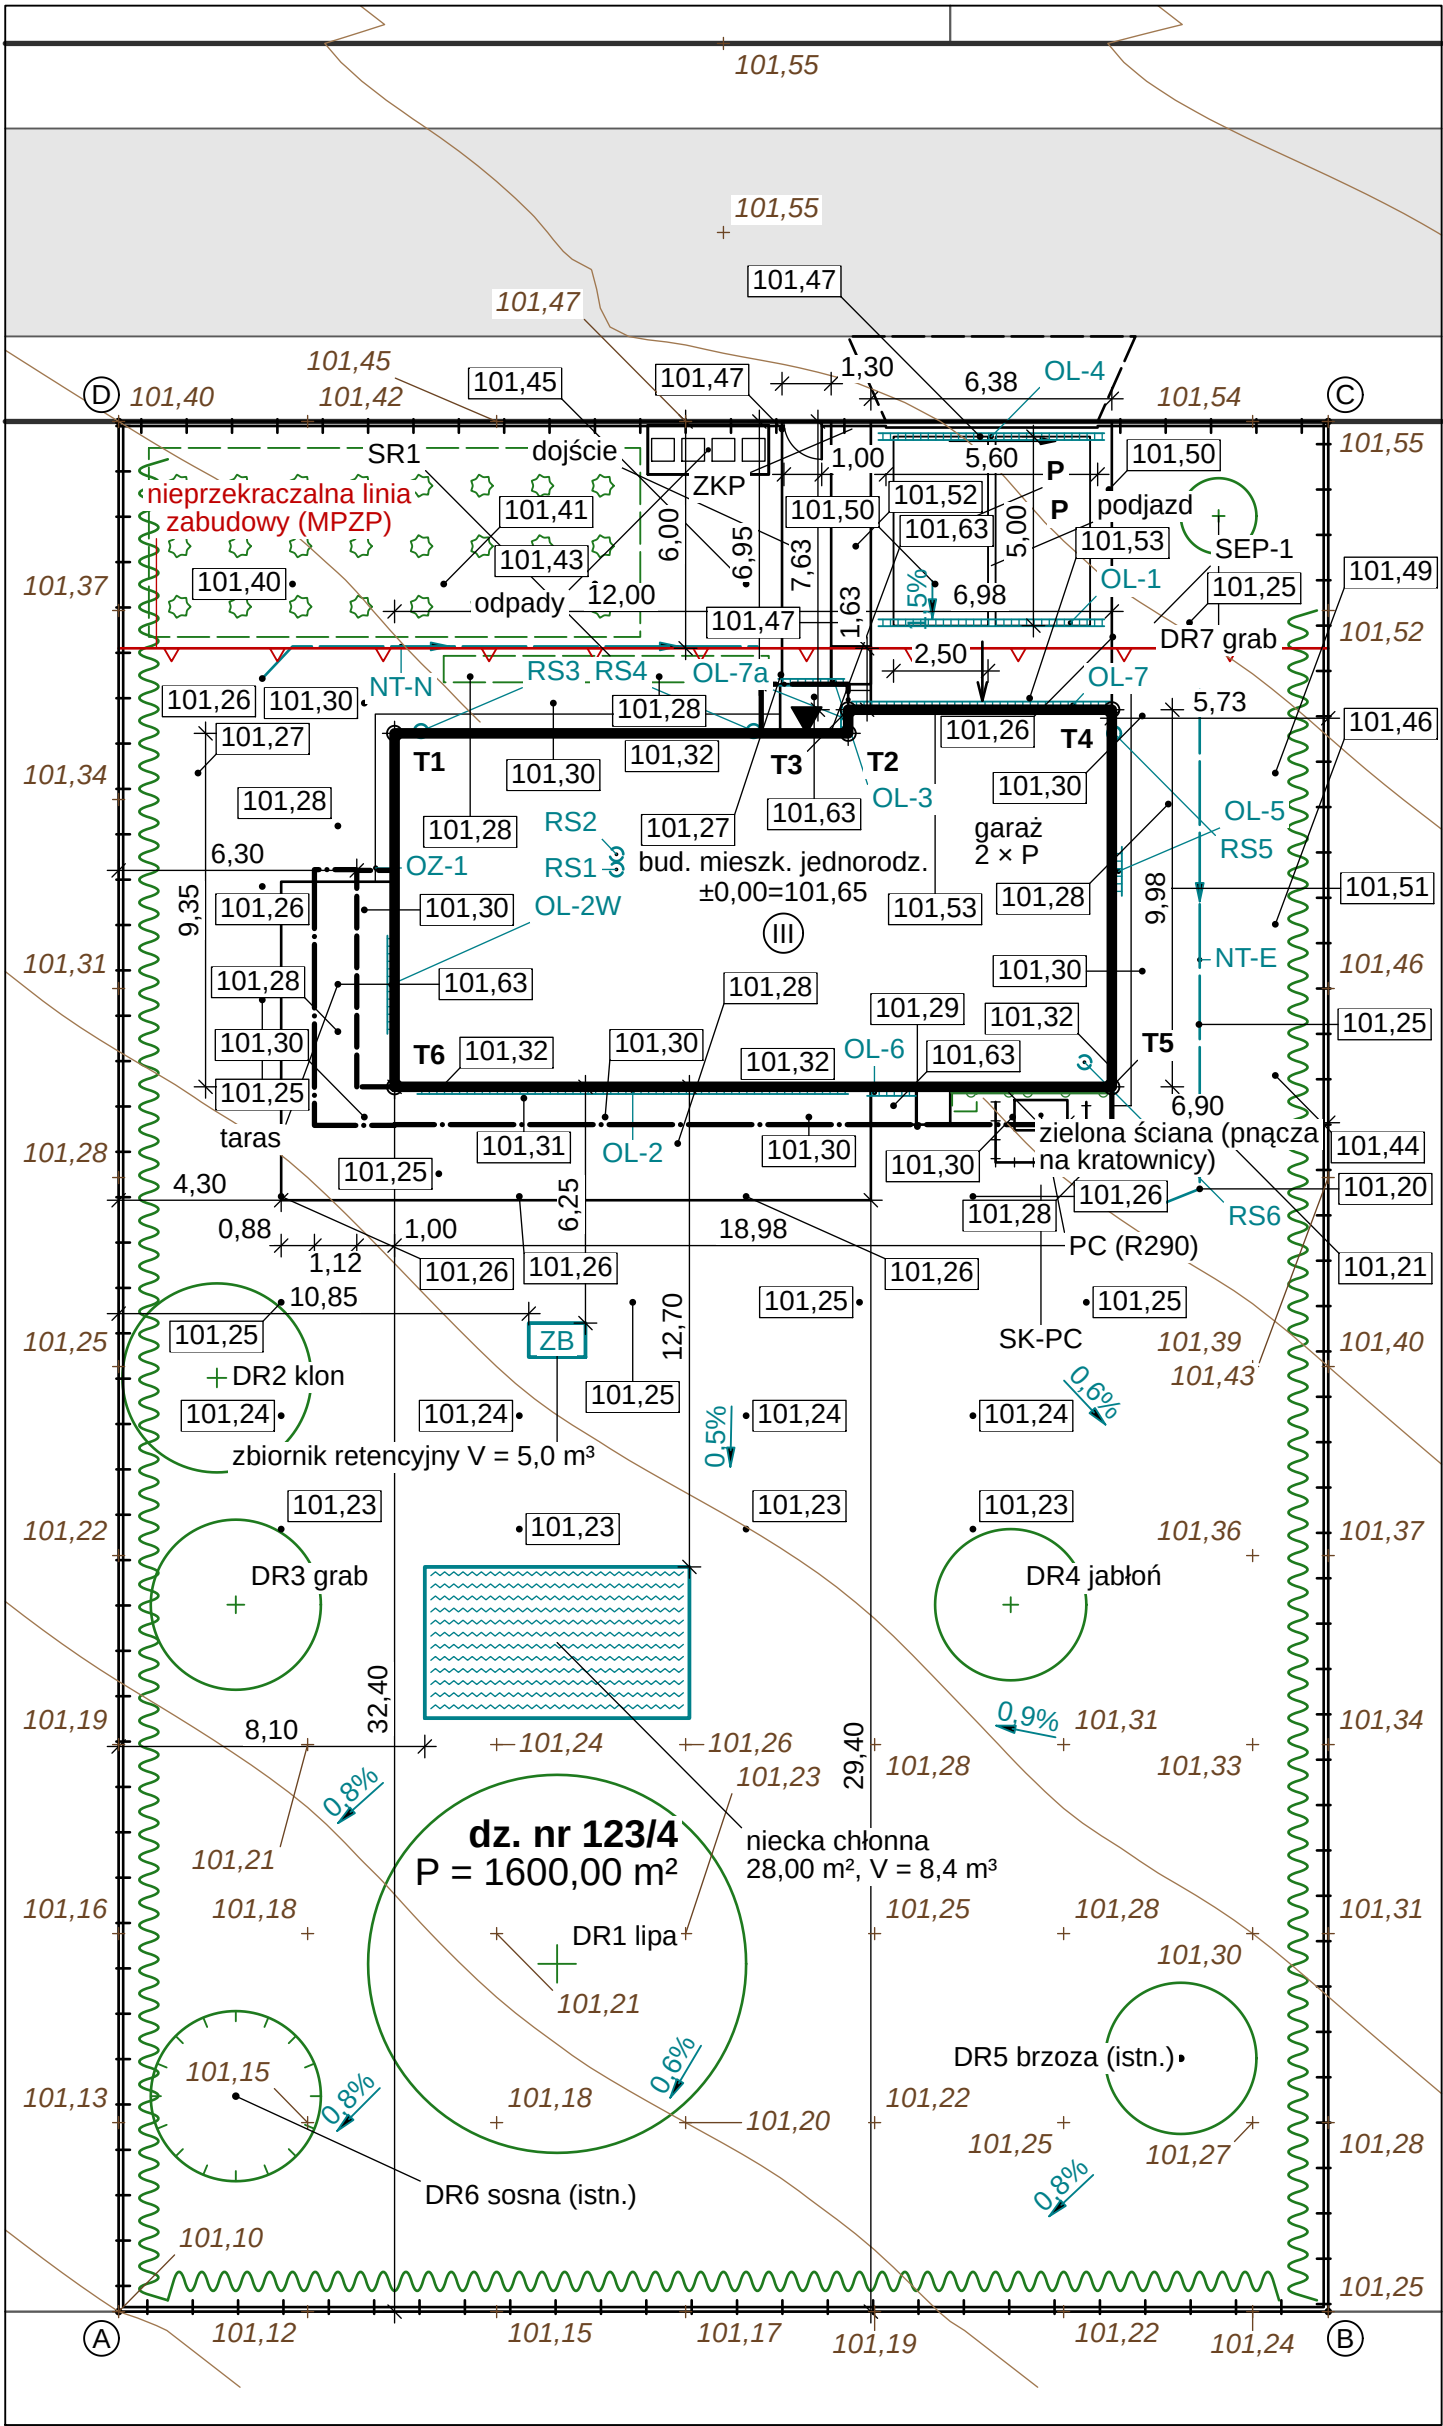

PLAN SZCZEGÓŁOWY — WYMIARY I RZĘDNE 1:200

LEGENDA

- granica działki budowlanej, punkt graniczny, narożnik (PN-B-01027 poz. 2.7)
- linia rozgraniczająca drogi publicznej (PN-B-01027 poz. 2.5)
- jezdnia drogi publicznej (wg mapy)
- nieprzekraczalna linia zabudowy wg MPZP (PN-B-01027 poz. 2.2)
- budynek projektowany — obrys ścian parteru 1,0 m nad terenem (poz. 1.1)
- obrys wyższych kondygnacji poza obrysem parteru (poz. 1.6 d)
- obrys płyt wspornikowych, okapów i daszku — przewieszenia (poz. 1.6 c)
- ±0,00=101,65
- rzędna ±0,00 (posadzka parteru) w m n.p.m.; w kółku liczba kondygnacji nadziemnych
- ▶ wejście główne do budynku (poz. 1.7)
- wjazd do garażu
- zjazd z drogi publicznej — wg zezwolenia zarządcy drogi [DO UZUPEŁNIENIA]
- nawierzchnia z kostki betonowej (poz. 7.10)
- nawierzchnia z płyt betonowych (poz. 7.11)
- płyty w trawie (ażur) — poza PBC
- taras naziemny — deska kompozytowa na legarach
- opaska żwirowa 16/32 na geowłókninie
- stanowisko postojowe 2,50 × 5,00 m (WT § 21)
- osłona pojemników na odpady — segregacja (WT § 22)
- rabata z krzewami
- żywopłot projektowany (poz. 7.6)
- drzewo liściaste projektowane (poz. 7.1)
- drzewo istniejące — zachowane (poz. 7.2)
- ogrodzenie projektowane (poz. 2.8; na granicy — odsunięte graficznie)
- brama przesuwna (poz. 2.9)
- furтка otwierana do wewnątrz działki (WT § 42)
- ażurowa osłona z lamel jednostki PC (bez dachu, prześwit przy terenie)
- zielona ściana — pnącza na kratownicy stalowej odsuniętej od elewacji
- ZB zbiornik retencyjny szczelny (ZB)
- niecka chłonna — ogród deszczowy (przelew zbiornika)
- odwodnienie liniowe
- niecka trawiasta — grot w kierunku spływu
- rura spustowa: zewnętrzna / w szachcie (RS)
- warstwa terenu istniejącego (PN-B-01027 poz. 5.2)
- rzędna terenu istniejącego [m n.p.m.]
- rzędna terenu projektowanego [m n.p.m.]
- spadek nawierzchni [%] — grot w kierunku spadku
- kierunek spływu wód opadowych, spadek terenu [%]
- wymiar / odległość w m z dokładnością 0,01 m
- punkt tyczenia (narożnik obrysu parteru) — wykaz współrzędnych

OBJAŚNIENIA I UWAGI

- Wymiary i odległości w m (dokładność 0,01 m), rzędne w m n.p.m. (PL-EVRF2007-NH).
- Wymiary obrysu — lico zewnętrzne ścian parteru (1,0 m nad terenem); odległości od granic w miejscu najmniejszego oddalenia (WT § 9), z dokładnością 0,01 m (RPB § 15 ust. 3 w brzmieniu Dz.U. 2026 poz. 597, od 5.11.2026 — stosowane).
- Rzędne terenu istniejącego — z mapy (przykładowe); projektowanego — z modelu (działka.yaml: teren.punkty_projectowane); spadki nawierzchni wg modelu, kierunek wg terenu projektowanego; kierunki spływu na trawnikach — wg spadku terenu projektowanego (interpolacja).
- Wody opadowe z nawierzchni i dachów — na teren własny, do niecek i zbiornika (WT § 28 ust. 2); zakaz zmiany spływu w kierunku działek sąsiednich (WT § 29) i odprowadzania na drogi (u.d.p. art. 39).
- Punkty tyczenia — narożniki obrysu zewnętrznego ścian parteru; współrzędne w wykazie obok rysunku.
- Zjazd — geometria zastępcza [DO UZUPEŁNIENIA] (wg zezwolenia zarządcy drogi).
- Braki danych modelu oznaczono [DO UZUPEŁNIENIA]; wykaz: projekt/02_PZT/BRAKI_DANYCH.md.
- Rysunek wygenerowany automatycznie z modelu model/budynek.yaml (wersja 1.0, 2026-09-25) — generator lamela.views.

WYKAZ PUNKTÓW TYCZENIA I GRANICZNYCH

Pkt	x [m]	y [m]	Opis
T1	7,30	41,75	narożnik obrysu parteru
T2	19,30	41,75	narożnik obrysu parteru
T3	19,30	42,38	narożnik obrysu parteru
T4	26,28	42,38	narożnik obrysu parteru
T5	26,28	32,40	narożnik obrysu parteru
T6	7,30	32,40	narożnik obrysu parteru
A	0,00	0,00	punkt graniczny działki
B	32,00	0,00	punkt graniczny działki
C	32,00	50,00	punkt graniczny działki
D	0,00	50,00	punkt graniczny działki

Układ lokalny działki: początek — narożnik A, x → wschód, y → północ. W projekcie rzeczywistym współrzędne w układzie PL-2000 (X — północ, Y — wschód) z mapy do celów projektowych; tyczenie — geodeta uprawniony (PB art. 43 ust. 1).

RZĘDNE CHARAKTERYSTYCZNE [m n.p.m.]

Poziom	Rzędna
±0,00 — posadzka parteru	101,65
T1 — deska kompozytowa...	101,63
T2 — płyty betonowe 60...	101,63
T3 — płyty betonowe 60...	101,63
teren proj. przy wejściu głównym	101,62
teren na obwodzie ścian — min.	101,29
teren na obwodzie ścian — maks.	101,48
najwyższy punkt budynku	111,85
zwierciadło wody gruntowej (ZWG)	97,60

Rzędne projektowane terenu: spadek ≥ 2 % od budynku; na granicach działki rzędne istniejące (bez zmiany spływu na działki sąsiednie — WT § 29, PW art. 234).

ODWODNIENIE POWIERZCHNIOWE

Ozn.	Typ	Wymiar	Spadek	Odbiornik
OL-1	liniowe	L = 5,98 m	0,5 %	SEP-1 → NT-E
OL-2	liniowe	L = 11,40 m	0,5 %	opaska / KD-W
OL-2W	liniowe	L = 2,60 m	0,5 %	KD-W
OL-3	liniowe	L = 1,75 m	0,5 %	KD-W
OL-7	liniowe	L = 6,88 m	0,5 %	SEP-1 → NT-E
OL-7a	liniowe	L = 0,70 m	0,5 %	OL-7 → SEP-1
OL-4	liniowe	L = 5,98 m	0,5 %	SEP-1 → NT-E
OZ-1	opaska żwir.	b = 0,50 m	—	—
NT-N	niecka	L = 13,47 m	0,5 %	pas zach. → ogród p...
NT-E	niecka	L = 14,28 m	0,5 %	ogród pd.
OL-5	liniowe	L = 1,30 m	0,5 %	KD-E
OL-6	liniowe	L = 1,30 m	0,5 %	RS8 → KD-E
NCH-1	niecka	A = 28,00 m²	—	grunt (piaski, ZWG...

DR-0: NIE PROJEKTUJE SIĘ — piaski przepuszczalne, ZWG ≈ 3,8 m p.p.t., posadowienie ≈ 0,5 m p.p.t. (W-285); ochrona płyty: XPS + membrana SBS, opaska żwirowa i spadki terenu

NAWIERZCHNIE UTWARDZONE I TARASY

Ozn.	Nawierzchnia	Pow.	Spadek
U1	podjazd	48,61 m²	1,5 %
U2	dojście	9,04 m²	2,0 %
U3	łącznik dojście–podjazd	1,05 m²	2,0 %
U4	stanowisko pojemników	4,16 m²	2,0 %
U5	fundament jednostki zewn....	1,12 m²	—
U6	ścieżka gospodarcza	0,90 m²	2,0 %
T1	deska kompozytowa na lega...	63,08 m²	rz. 101,63
T2	płyty betonowe 60×60 na p...	2,34 m²	rz. 101,63
T3	płyty betonowe 60×60, spa...	1,20 m²	rz. 101,63

Kierunek spadku — strzałki na rysunku (od budynku, do odwodnień liniowych i niecek).

ODLEGŁOŚCI URZĄDZEŃ RETENCJI I PC

Element	Od	d [m]	min [m]	Zgodność
zbiornik	budynek	6,70	3,00	TAK
zbiornik	granica	11,60	2,00	TAK
zbiornik	drzewo	9,06	1,00	TAK
niecka	budynek	12,70	3,00	TAK
niecka	granica	8,10	2,00	TAK
niecka	drzewo	5,00	1,00	TAK
strefa R290	otwory, wpusty, studzienki	—	r = 1,00	TAK

Wymagania retencji — założenia projektowe (R8 pkt 3.5, W-144/W-145; nie przepis); zbiornik — odległość od środka (brak wymiarów w modelu); strefa R290 — W-156 (wytyczne producenta).



REW.	OPIS ZMIANY			DATA	
0	Wydanie — rysunek wygenerowany z modelu			2026-09-25	
PRACOWNIA PROJEKTOWA PRACOWNIA PROJEKTOWA — nazwa do uzupełnienia adres pracowni do uzupełnienia			STADIUM PB	BRANŻA ZAGOSPODAROWANIE TERENU	
INWESTOR (do uzupełnienia)					
OBJEKT / NAZWA ZAMIERZENIA BUDOWLANEGO Budynek mieszkalny jednorodzinny wolnostojący „Dom LAMELA” z zagospodarowaniem działki					
ADRES / LOKALIZACJA (NR DZIAŁKI, OBRĘB, JEDN. EWIDENCYJNA) ul. Lipowa (fikcyjna), dz. nr ewid. 123/4, obręb 0005 Przykładowo, gm. Przykładowo (fikcyjna)				KAT. OBJEKTU I	
FUNKCJA	IMIĘ I NAZWISKO		SPECJALNOŚĆ, NR UPRAWNIENI	DATA	PODPIS
Projektant	[DO UZUPEŁNIENIA]		[DO UZUPEŁNIENIA]		
Projektant (wsp.)	[DO UZUPEŁNIENIA]		[DO UZUPEŁNIENIA]		
Sprawdzający	nie dotyczy (art. 20 ust. 3 pkt 2 PB)		—		
Opracował	[DO UZUPEŁNIENIA]		[DO UZUPEŁNIENIA]		
TYTUŁ RYSUNKU PLAN SZCZEGÓŁOWY — WYMIARY I RZĘDNE					
SKALA 1:200	FORMAT 400×594	DATA WYDANIA 2026-09-25	RODZAJ DOK. plan szczegółowy	NR RYSUNKU PZT-02	ARKUSZ 2/3
REW.					0