


PROJEKT ZAGOSPODAROWANIA DZIAŁKI — CZĘŚĆ RYSUNKOWA

Lp.	Nr rys.	Tytuł rysunku	Skala	Format
1	PZT-01	PLAN ZAGOSPODAROWANIA DZIAŁKI	1:500	A2
2	PZT-02	PLAN SZCZEGÓŁOWY — WYMIARY I RZĘDNE	1:200	400×594
3	PZT-03	RYSUNEK KOORDYNACYJNY UZBROJENIA TERENU	1:200	620×420

PRACOWNIA PROJEKTOWA PRACOWNIA PROJEKTOWA — nazwa do uzupełnienia		STADIUM PB	BRANŻA ZAGOSPODAROWANIE TERENU			
INWESTOR (do uzupełnienia)						
OBIEKT / NAZWA ZAMIERZENIA BUDOWLANEGO Budynek mieszkalny jednorodzinny wolnostojący „Dom LAMELA” z zagospodarowaniem działki						
ADRES / LOKALIZACJA (NR DZIAŁKI, OBRĘB, JEDN. EWIDENCYJNA) ul. Lipowa (fikcyjna), dz. nr ewid. 123/4, obręb 0005 Przykładowo, gm. Przykładowo (fikcyjna)			KAT. OBIEKTU I			
FUNKCJA	IMIĘ I NAZWISKO	SPECJALNOŚĆ, NR UPRAWNIENI	DATA	PODPIS		
Projektant	[DO UZUPEŁNIENIA]	[DO UZUPEŁNIENIA]				
Projektant (wsp.)	[DO UZUPEŁNIENIA]	[DO UZUPEŁNIENIA]				
Sprawdzający	nie dotyczy (art. 20 ust. 3 pkt 2 PB)	—				
Opracował	[DO UZUPEŁNIENIA]	[DO UZUPEŁNIENIA]				
TYTUŁ RYSUNKU SPIS RYSUNKÓW						
SKALA —	FORMAT A4	DATA WYDANIA 2026-09-25	RODZAJ DOK. spis	NR RYSUNKU PZT-00	ARKUSZ —	REW.

MAPA DO CELÓW PROJEKTOWYCH — PODKŁAD PRZYKŁADOWY

PODKŁAD PRZYKŁADOWY — mapa do celów projektowych fikcyjna [DANE PRZYKŁADOWE – FIKCYJNE], narysowana z modelu działki (działka.yaml); w projekcie rzeczywistym — aktualna mapa do celów projektowych wg art. 34 ust. 3 pkt 1 PB (z klauzulą urzędową lub oświadczeniem geodety — art. 34b PB), treść i opis mapy wg § 32–33 rozp. w sprawie standardów technicznych (t.j. Dz.U. 2022 poz. 1670), znaki wg zał. 4 rozp. w sprawie BDOT500 i mapy zasadniczej (Dz.U. 2021 poz. 1385; oba akty zweryfikowane w ELI 25.09.2026 — status: obowiązujące).

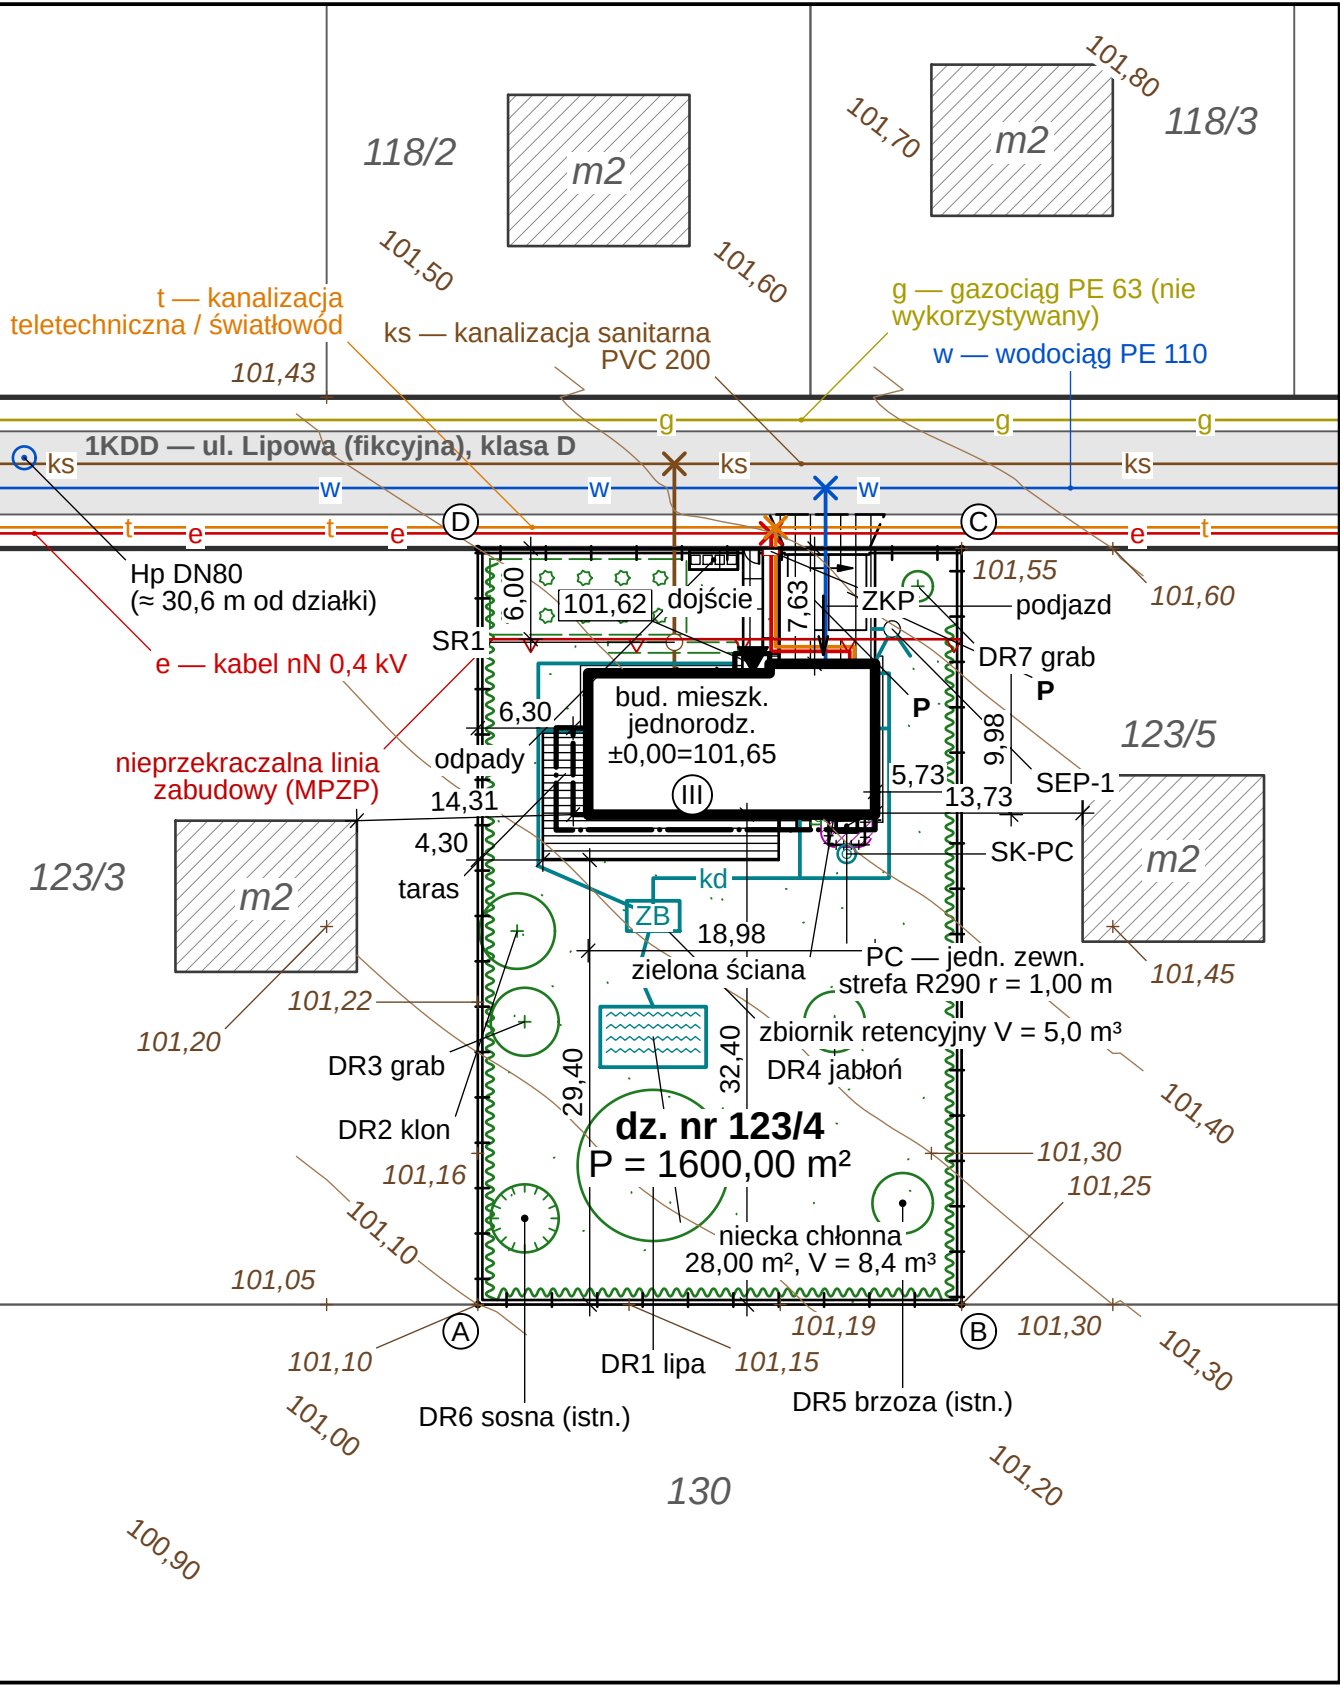

PLAN ZAGOSPODAROWANIA DZIAŁKI 1:500

LEGENDA

- zasięg podkładu mapowego (mapa do celów projektowych — PRZYKŁADOWA)

granicza działki budowlanej, punkt graniczny, narożnik (PN-B-01027 poz. 2.7)

linia rozgraniczająca drogi publicznej (PN-B-01027 poz. 2.5)

jezdnia drogi publicznej (wg mapy)

budynek istniejący (mapa); m2 — mieszkalny, 2 kondygnacje

nieprzekraczalna linia zabudowy wg MPZP (PN-B-01027 poz. 2.2)

budynek projektowany — obrys ścian parteru 1,0 m nad terenem (poz. 1.1)

obrys wyższych kondygnacji poza obrysem parteru (poz. 1.6 d)

obrys płyt wspornikowych, okapów i daszku — przewieszenia (poz. 1.6 c)

rzędna ±0,00 (posadzka parteru) w m n.p.m.; w kółku liczba kondygnacji nadziemnych

wejście główne do budynku (poz. 1.7)

wjazd do garażu

zjazd z drogi publicznej — wg zezwolenia zarządcy drogi [DO UZUPEŁNIENIA]

nawierzchnia z kostki betonowej (poz. 7.10)

nawierzchnia z płyt betonowych (poz. 7.11)

płyty w trawie (ażur) — poza PBC

taras naziemny — deska kompozytowa na legarach

opaska żwirowa 16/32 na geowłókninie

stanowisko postojowe 2,50 × 5,00 m (WT § 21)

osłona pojemników na odpady — segregacja (WT § 22)

trawnik projektowany (poz. 7.8)

rabata z krzewami

żywiplot projektowany (poz. 7.6)

drzewo liściaste projektowane (poz. 7.1)

drzewo istniejące — zachowane (poz. 7.2)

ogrodzenie projektowane (poz. 2.8; na granicy — odsunięte granicznie)
- brama przesuwana (poz. 2.9)
- furtka otwierana do wewnątrz działki (WT § 42)
- jednostka zewn. pompy ciepła (fundament) i strefa czynnika R290
- ażurowa osłona z lamel jednostki PC (bez dachu, prześwit przy terenie)
- zielona ściana — pnącza na kratownicy stalowej odsuniętej od elewacji
- zbiornik retencyjny szczelny (ZB)
- niecka chłonna — ogród deszczowy (przelew zbiornika)
- miejsce włączenia przyłącza do sieci (PN-B-01027 poz. 6)
- złącze kablowo-pomiarowe ZKP (w linii ogrodzenia)
- studzienka rewizyjna kanalizacji
- studnia chłonna skroplin pompy ciepła
- hydrant zewnętrzny na sieci (Hp)
- warstwa terenu istniejącego (PN-B-01027 poz. 5.2)
- rzędna terenu istniejącego [m n.p.m.]
- rzędna terenu projektowanego [m n.p.m.]
- wymiar / odległość w m z dokładnością 0,01 m
- w — sieć wodociągowa istniejąca (mapa)
- w — przyłącze wodociągowe projektowane
- ks — sieć kanalizacji sanitarnej istniejąca (mapa)
- ks — przykanalik sanitarny projektowany
- kd — kanalizacja deszczowa projektowana (kolektory, przelewy)
- e — linia kablowa nN istniejąca (mapa)
- e — kabel nN projektowany (ZKP → RG)
- t — sieć telekomunikacyjna istniejąca (mapa)
- t — przyłącze telekomunikacyjne projektowane
- g — sieć gazowa istniejąca (mapa)

ZESTAWIENIE POWIERZCHNI I WSKAŹNIKÓW ZAGOSPODAROWANIA (RPB § 14 pkt 4, MPZP)

Wskaźnik / element	Projekt	MPZP / wymaganie	Zgodność
Powierzchnia działki nr 123/4	1600,00 m ²	—	
Pow. zabudowy (upzp art. 2 pkt 35)	187,50 m ²	≤ 480,00 m ²	TAK
Udział pow. zabudowy	11,72%	≤ 30%	TAK
— z płytami i okapami (kontrolnie)	218,08 m ² (13,63%)	informacyjnie	TAK
Drogi, dojścia, place	64,87 m ²	—	
Tarasы naziemne, podesty	66,62 m ²	—	
Opaska żwirowa	13,38 m ²	—	
PBC (upzp art. 2 pkt 28)	1270,23 m ² (79,39%)	≥ 800,00 m ² (50%)	TAK
— z 50 % dachu ziel. D4 (rezerwa)	1299,76 m ² (81,24%)	informacyjnie	
Pow. kondygnacji nadz. (P0+P1+P2)	396,39 m ²	80,00 m ² –1280,00 m ²	TAK
Nadziemna intensywność zabudowy	0,248	0,05–0,80	TAK
Wysokość zabudowy (art. 2 pkt 30)	10,47 m	≤ 11,00 m	TAK
Wysokość budynku (WT § 6)	9,97 m	N: ≤ 12,00 m	TAK
Kondygnacje nadziemne	3	≤ 3	TAK
Miejsca postojowe (garaż + zewn.)	2 + 2	≥ 2	TAK
Dach — kąt nachylenia	1,1° (płaski)	płaski ≤ 12° lub 30–45°	TAK
Lico ścian od linii zabudowy	1,63 m	nie przekraczać	TAK
Elementy poza linią zabudowy	brak	—	

MPZP: uchwała nr XII/123/2024 Rady Gminy Przykładowo z 21.03.2024 — teren 3MN (fikcyjny). Limity: ustalenia MPZP przyjęte w projekcie (dane przykładowe) — wypis i wyrys z MPZP [DO UZUPEŁNIENIA]. Wartości z modułu lamela.wskazniki (jedyne źródło; definicje upzp art. 2 pkt 28–35, t.j. Dz.U. 2026 poz. 538): PBC bez nawierzchni ażurowych, opaski, pojemników i terenu nad zbiornikiem; dach zielony (≥ 10 m²) w 50 % — tylko rezerwa. Wysokość zabudowy = z_top 111,85 (wyrzutnia wentylacji (dachowa, szczyt urządzenia)) – t_śr 101,38 (t_min 101,29, t_max 101,48 na obwodzie rzutu ścian zewn.; w każdym punkcie niższa z rzędnych terenu istniejącego/projektowanego). WT § 6: od terenu przy wejściu O0-03 (101,30) do wierzchu stropodachu D1 (bez attyki) — grupa N.

ODLEGŁOŚCI OD GRANIC DZIAŁKI (WT § 12)

Granica	Element (płaszczyzna ściany)	Odl. [m]	Wymagana [m]	Zgodność
S (130)	ściana P0 z otworami	32,40	≥ 4,00	TAK
S (130)	T1 — okap/płyta/taras	29,40	≥ 1,50	TAK
E (123/5)	ściana P0 z otworami	5,73	≥ 4,00	TAK
E (123/5)	ściana P2 bez otworów	15,60	≥ 3,00	TAK
E (123/5)	PL-D — okap/płyta/taras	5,73	≥ 1,50	TAK
N (1KDD)	ściana P0 z otworami	7,63	nie dot. (ust. 10)	—
N (1KDD)	ściana P2 bez otworów	11,88	nie dot. (ust. 10)	—
N (1KDD)	PL-DA — okap/płyta/taras	6,95	nie dot. (ust. 10)	—
W (123/3)	ściana P2 z otworami	6,30	≥ 4,00	TAK
W (123/3)	ściana P2 bez otworów	11,18	≥ 3,00	TAK
W (123/3)	T1 — okap/płyta/taras	4,30	≥ 1,50	TAK



WT § 12 ust. 1: 4,00 m — ściana z oknami/drzwiami, 3,00 m — bez otworów (każda płaszczyzna ściany osobno); ust. 6: 1,50 m — okap, taras, daszek; ust. 10: od działki drogowej — nie dotyczy. Odległość w poziomie w miejscu najmniejszego oddalenia (§ 9). WT stosowane na podstawie art. 102a PB.

OBSZAR ODDZIAŁ YWANIA OBIEKTU (PB art. 3 pkt 20; RPB § 14 pkt 8)


Obszar oddziaływania obiektu mieści się w całości w granicach działki 123/4 (PB art. 3 pkt 20): odległości od granic ≥ 4,0 m (ściany z otworami ≥ 5,70 m, płyty ≥ 5,20 m), przesłanianie i nasłonecznienie sąsiednich budynków (≥ 8 m od granicy) bez ograniczeń (WT §13, §60), hałas PC ≤ 40 dB(A) nocą na granicy (W-024), wody opadowe zagospodarowane na działce (PW art. 234), brak odprowadzania na drogę. Podstawa ustalenia (RPB § 18 pkt 1): WT § 12, 13, 19, 23, 28–29, 60, 271 (art. 102a PB); u.d.p. art. 43; POŚ art. 144 ust. 2 i rozp. MŚ w sprawie dopuszczalnych poziomów hałasu (Dz.U. 2014 poz. 112); PW art. 234; ustalenia MPZP.

OBJAŚNIENIA I UWAGI

- Wymiary i odległości w m (dokładność 0,01 m), rzędne w m n.p.m. (PL-EVRF2007-NH).
- Układ współrzędnych: lokalny układ działki (x → wschód, y → północ, początek w narożniku A); w projekcie rzeczywistym — układ PL-2000 strefa 6 z mapy do celów projektowych.
- Obrys budynku — lico zewnętrzne ścian parteru na wys. 1,0 m nad terenem; wspornik bryły A (II piętro) — obrys wyższych kondygnacji; płyty wspornikowe, okapy i daszek — przewieszenia (PN-B-01027 poz. 1.6).
- Wody opadowe zagospodarowane w granicach działki: rury spustowe → kolektory KD → zbiornik retencyjny szczelny → przelew do niecki chłonnej; odwodnienie liniowe przed bramą — brak spływu na drogę (MPZP; u.d.p. art. 39 ust. 1 pkt 9; WT § 28–29).
- Wymiary i rzędne szczegółowe — rys. PZT-02; uzbrojenie i koordynacja sieci — rys. PZT-03.
- Zjazd z drogi 1KDD pokazano jako przedłużenie bramy do krawędzi jezdni — geometria zastępcza [DO UZUPEŁNIENIA]: szerokość, skosy/luki, nawierzchnia i przepust wg zezwolenia zarządcy drogi (u.d.p. art. 29 ust. 3a).
- Braki danych modelu (6 poz.) oznaczono [DO UZUPEŁNIENIA]; wykaz: projekt/02_PZT/BRAKI_DANYCH.md.
- Rysunek wygenerowany automatycznie z modelu model/budynek.yaml (wersja 1.0, 2026-09-25) — generatory lamela.views.

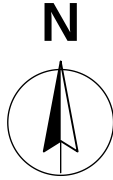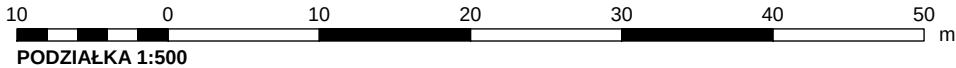

REW.	OPIS ZMIANY			DATA
0	Wydanie — rysunek wygenerowany z modelu			2026-09-25
PRACOWNIA PROJEKTOWA PRACOWNIA PROJEKTOWA — nazwa do uzupełnienia adres pracowni do uzupełnienia			STADIUM PB	BRANŻA ZAGOSPODAROWANIE TERENU
INWESTOR (do uzupełnienia)				
OBIEKT / NAZWA ZAMIERZENIA BUDOWLANEGO Budynek mieszkalny jednorodzinny wolnostojący „Dom LAMELA” z zagospodarowaniem działki				
ADRES / LOKALIZACJA (NR DZIAŁKI, OBRĘB, JEDN. EWIDENCYJNA) ul. Lipowa (fikcyjna), dz. nr ewid. 123/4, obręb 0005 Przykładowo, gm. Przykładowo (fikcyjna)				KAT. OBIEKTU I
FUNKCJA	IMIĘ I NAZWISKO	SPECJALNOŚĆ, NR UPRAWNIENI	DATA	PODPIS
Projektant	[DO UZUPEŁNIENIA]	[DO UZUPEŁNIENIA]		
Projektant (wsp.)	[DO UZUPEŁNIENIA]	[DO UZUPEŁNIENIA]		
Sprawdzający	nie dotyczy (art. 20 ust. 3 pkt 2 PB)	—		
Opracował	[DO UZUPEŁNIENIA]	[DO UZUPEŁNIENIA]		
TYTUŁ RYSUNKU PLAN ZAGOSPODAROWANIA DZIAŁKI				
SKALA 1:500	FORMAT A2	DATA WYDANIA 2026-09-25	RODZAJ DOK. plan zagospodarowania	NR RYSUNKU PZT-01
ARKUSZ 1/3			REW. 0	

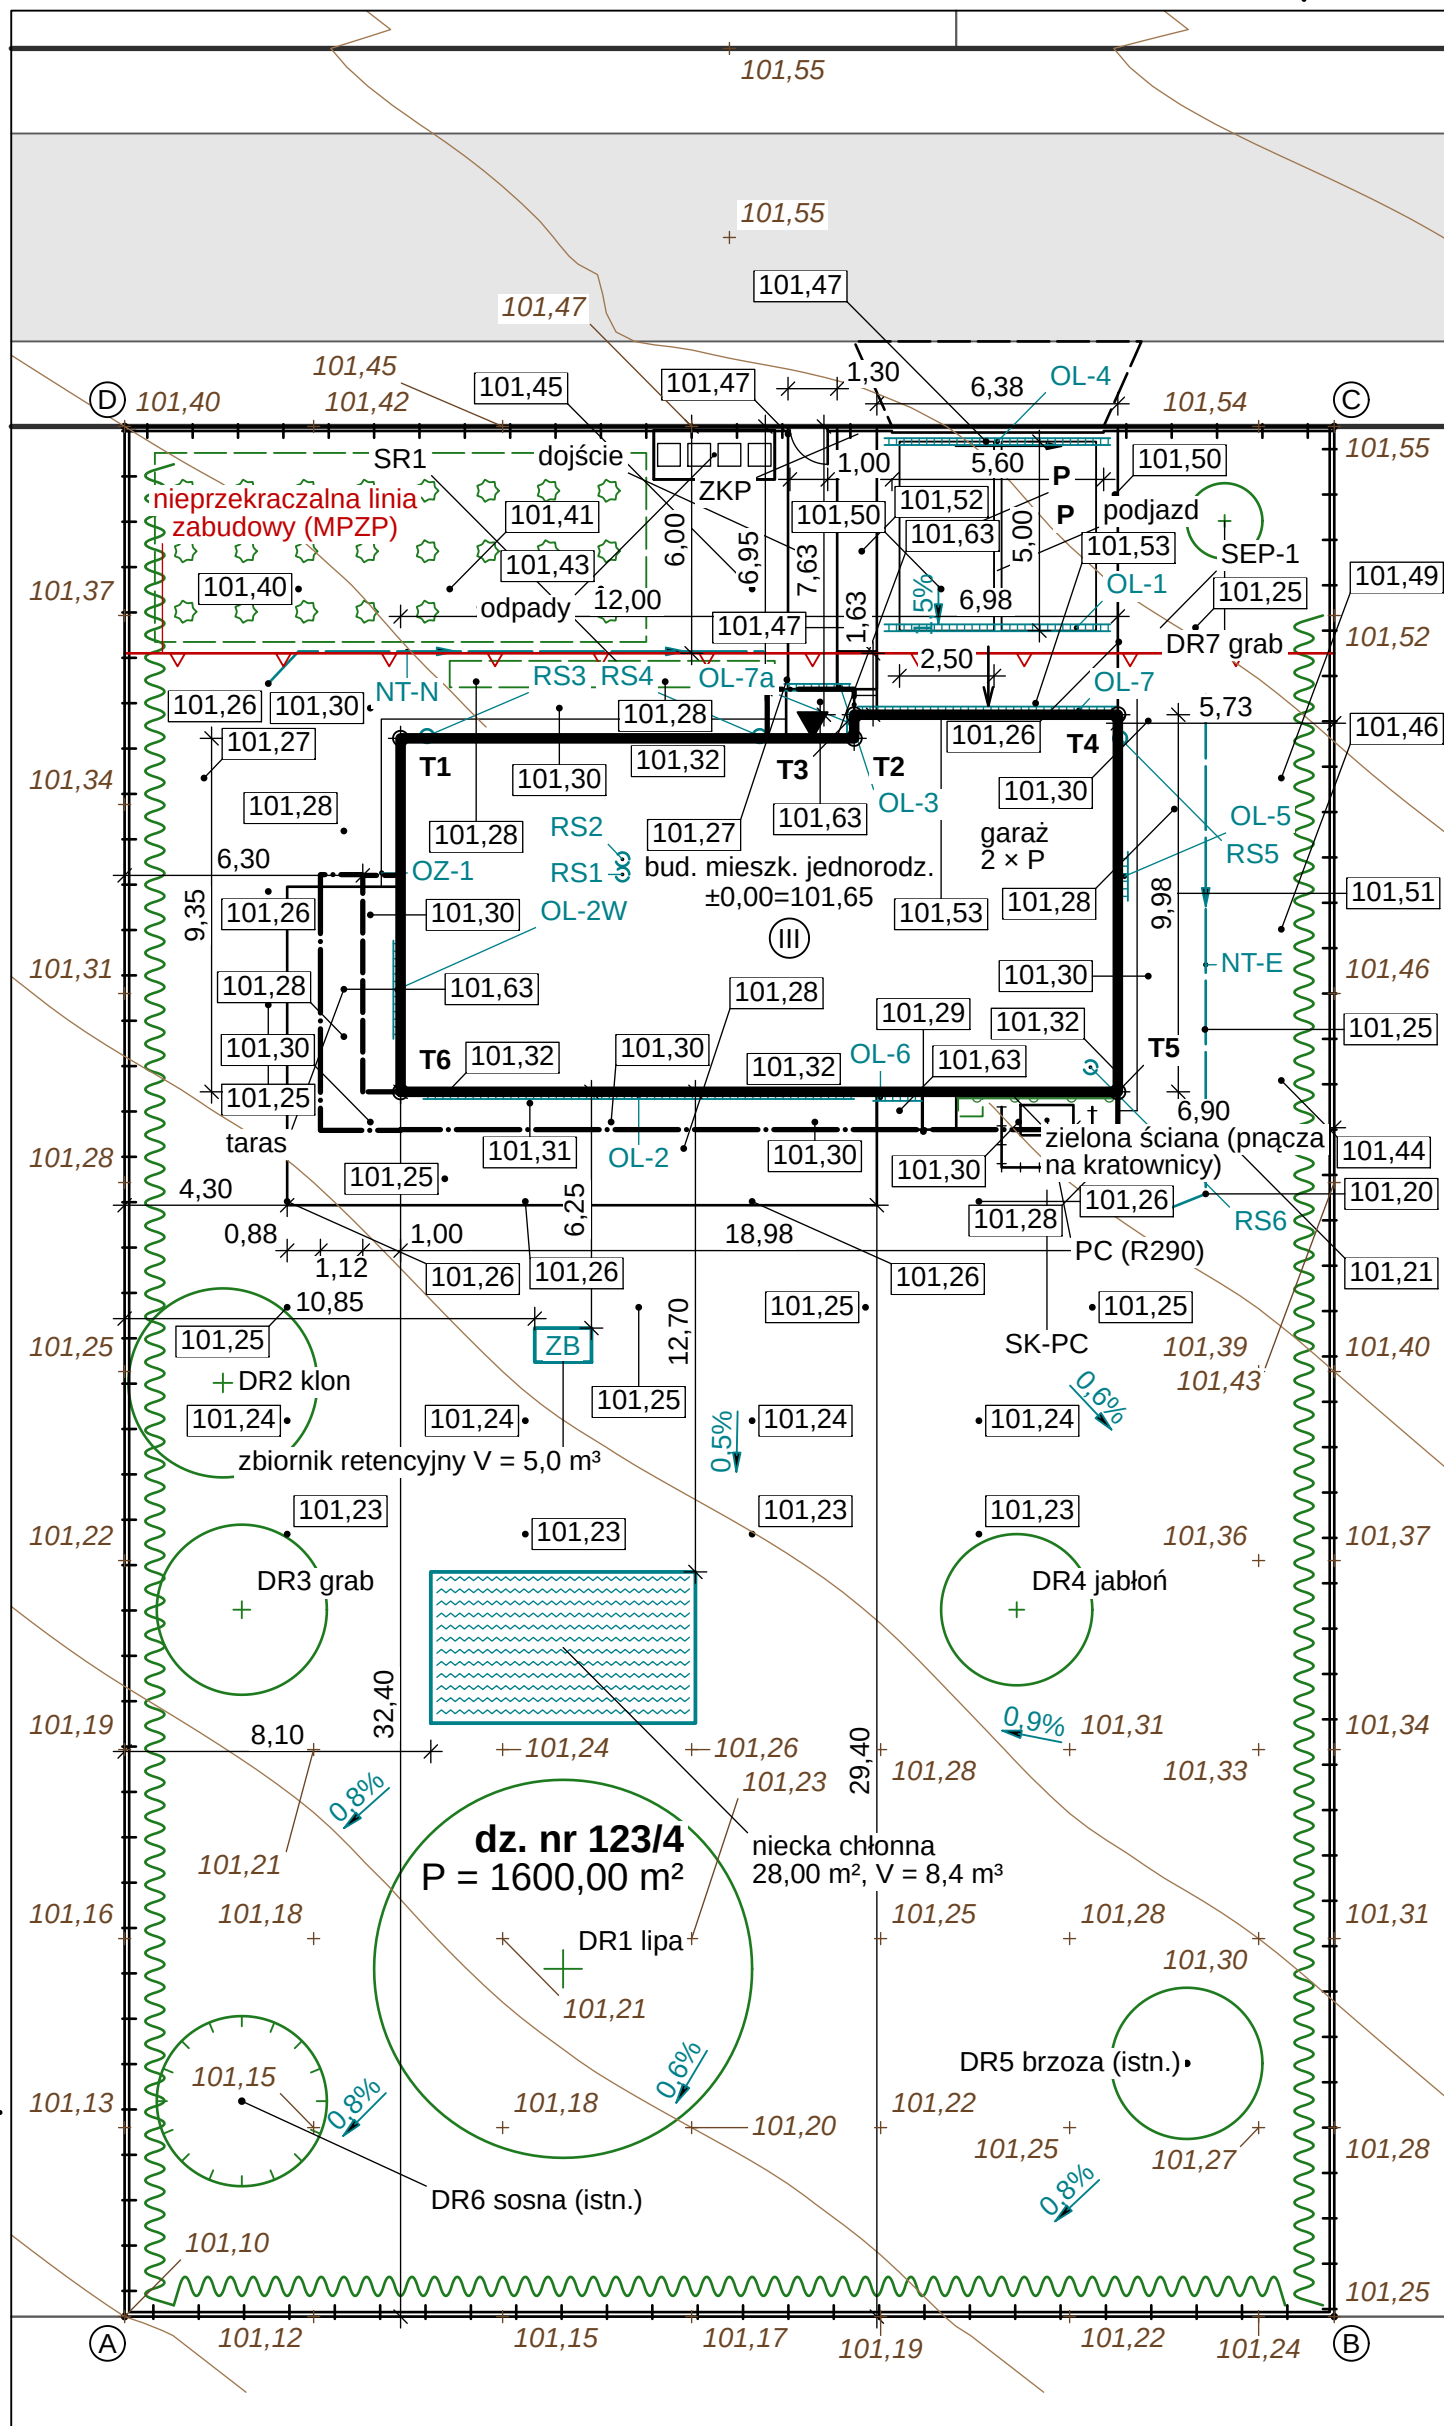

WYKAZ PUNKTÓW TYCZENIA I GRANICZNYCH

Pkt	x [m]	y [m]	Opis
T1	7,30	41,75	narożnik obrysu parteru
T2	19,30	41,75	narożnik obrysu parteru
T3	19,30	42,38	narożnik obrysu parteru
T4	26,28	42,38	narożnik obrysu parteru
T5	26,28	32,40	narożnik obrysu parteru
T6	7,30	32,40	narożnik obrysu parteru
A	0,00	0,00	punkt graniczny działki
B	32,00	0,00	punkt graniczny działki
C	32,00	50,00	punkt graniczny działki
D	0,00	50,00	punkt graniczny działki

Układ lokalny działki: początek — narożnik A, x → wschód, y → północ. W projekcie rzeczywistym współrzędne w układzie PL-2000 (X — północ, Y — wschód) z mapy do celów projektowych; tyczenie — geodeta uprawniony (PB art. 43 ust. 1).

RZĘDNE CHARAKTERYSTYCZNE [m n.p.m.]

Poziom	Rzędna
±0,00 — posadzka parteru	101.65
T1 — deska kompozytowa...	101.63
T2 — płyty betonowe 60...	101.63
T3 — płyty betonowe 60...	101.63
teren proj. przy wejściu głównym	101.62
teren na obwodzie ścian — min.	101.29
teren na obwodzie ścian — maks.	101.48
najwyższy punkt budynku	111.85
zwierciadło wody gruntowej (ZWG)	97.60

Rzędne projektowane terenu: spadek $\geq 2\%$ od budynku; na granicach działki rzędne istniejące (bez zmiany spływu na działki sąsiednie — WT § 29, PW art. 234).

ODWODNIENIE POWIERZCHNIOWE

Ozn.	Typ	Wymiar	Spadek	Odbiornik
OL-1	liniowe	L = 5,98 m	0,5 %	SEP-1 → NT-E
OL-2	liniowe	L = 11,40 m	0,5 %	opaska / KD-W
OL-2W	liniowe	L = 2,60 m	0,5 %	KD-W
OL-3	liniowe	L = 1,75 m	0,5 %	KD-W
OL-7	liniowe	L = 6,88 m	0,5 %	SEP-1 → NT-E
OL-7a	liniowe	L = 0,70 m	0,5 %	OL-7 → SEP-1
OL-4	liniowe	L = 5,98 m	0,5 %	SEP-1 → NT-E
OZ-1	opaska żwir.	b = 0,50 m	—	—
NT-N	niecka	L = 13,47 m	0,5 %	pas zach. → ogród p...
NT-E	niecka	L = 14,28 m	0,5 %	ogród pd.
OL-5	liniowe	L = 1,30 m	0,5 %	KD-E
OL-6	liniowe	L = 1,30 m	0,5 %	RS8 → KD-E
NCH-1	niecka	A = 28,00 m ²	—	grunt (piaski, ZWG...

DR-0: NIE PROJEKTUJE SIĘ — piaski przepuszczalne, ZWG $\approx 3,8$ m p.p.t., posadowienie $\approx 0,5$ m p.p.t. (W-285); ochrona płyty: XPS + membrana SBS, opaska żwirowa i spadki terenu

NAWIERZCHNIE UTWARDZONE I TARASY

Ozn.	Nawierzchnia	Pow.	Spadek
U1	podjazd	48,61 m ²	1,5 %
U2	dojście	9,04 m ²	2,0 %
U3	łącznik dojście–podjazd	1,05 m ²	2,0 %
U4	stanowisko pojemników	4,16 m ²	2,0 %
U5	fundament jednostki zewn....	1,12 m ²	—
U6	ścieżka gospodarcza	0,90 m ²	2,0 %
T1	deska kompozytowa na lega...	63,08 m ²	rz. 101,63
T2	plyty betonowe 60×60 na p...	2,34 m ²	rz. 101,63
T3	plyty betonowe 60×60, spa...	1,20 m ²	rz. 101,63

Kierunek spadku — strzałki na rysunku (od budynku, do odwodnień liniowych i niecek).

ODLEGŁOŚCI URZĄDZEŃ RETENCJI I PC

Element	Od	d [m]	min [m]	Zgodność
zbiornik	budynek	6,70	3,00	TAK
zbiornik	granica	11,60	2,00	TAK
zbiornik	drzewo	9,06	1,00	TAK
niecka	budynek	12,70	3,00	TAK
niecka	granica	8,10	2,00	TAK
niecka	drzewo	5,00	1,00	TAK
strefa R290	otwory, wpusty, studzienki	—	r = 1,00	TAK

Wymagania retencji — założenia projektowe (R8 pkt 3.5, W-144/W-145; nie przepis); zbiornik — odległość od środka (brak wymiarów w modelu); strefa R290 — W-156 (wytyczne producenta).


PLAN SZCZEGÓŁOWY — WYMIARY I RZĘDNE 1:200

LEGENDA

- | | | | |
|--|---|--|--|
| | granica działki budowlanej, punkt graniczny, narożnik (PN-B-01027 poz. 2.7) | | drzewo liściaste projektowane (poz. 7.1) |
| | linia rozgraniczająca drogi publicznej (PN-B-01027 poz. 2.5) | | drzewo iglaste — zachowane (poz. 7.2) |
| | jezdni drogi publicznej (wg mapy) | | ogrodzenie projektowane (poz. 2.8; na granicy — odsunięte graficznie) |
| | nieprzekraczalna linia zabudowy wg MPZP (PN-B-01027 poz. 2.2) | | brama przesuwna (poz. 2.9) |
| | budynek projektowany — obrys ścian parteru 1,0 m nad terenem (poz. 1.1) | | furtka otwierana do wewnątrz działki (WT § 42) |
| | obrys wyższych kondygnacji poza obrysem parteru (poz. 1.6 d) | | azurowa osłona z lamel jednostki PC (bez dachu, przewiit przy terenie) |
| | obrys płyt wspornikowych, okapów i daszku — przewieszenia (poz. 1.6 c) | | zielenia ściana — pnącza na kratownicy stalowej odsuniętej od elewacji |
| | rzędna $\pm 0,00$ (posadzka parteru) w m n.p.m.; w kółku liczba kondygnacji nadziemnych | | zbiornik retencyjny szczelny (ZB) |
| | w wejście główne do budynku (poz. 1.7) | | niecka chłonna — ogród deszczowy (przelew zbiornika) |
| | wjazd do garażu | | odwodnienie liniowe |
| | zjazd z drogi publicznej — wg zezwolenia zarządcy drogi [DO UZUPEŁNIENIA] | | niecka trawiasta — grot w kierunku spływu |
| | nawierzchnia z kostki betonowej (poz. 7.10) | | rura spustowa: zewnętrzna / w szachcie (RS) |
| | nawierzchnia z płyt betonowych (poz. 7.11) | | warstwa terenu istniejącego [m n.p.m.] |
| | płyty w trawie (ażur) — poza PBC | | rzędna terenu istniejącego [m n.p.m.] |
| | taras naziemny — deska kompozytowa na legarach | | rzędna terenu projektowanego [m n.p.m.] |
| | opaska żwirowa 16/32 na geowłókninie | | spadek nawierzchni [%] — grot w kierunku spadku |
| | stanowisko postojowe 2,50 × 5,00 m (WT § 21) | | kierunek spływu wód opadowych, spadek terenu [%] |
| | osłona pojemników na odpady — segregacja (WT § 22) | | wymiar / odległość w m / dokładnością 0,01 m |
| | rabata z krzewami | | punkt tyczenia (narożnik obrysu parteru) — wykaz współrzędnych |
| | żywiopłot projektowany (poz. 7.6) | | |

OBJAŚNIENIA I UWAGI

1. Wymiary i odległości w m (dokładność 0,01 m), rzędne w m n.p.m. (PL-EVRF2007-NH).
2. Wymiary obrusy – lico zewnętrzne ścian parteru (1,0 m nad terenem); odległości od granic w miejscu najmniejszego oddalenia (WT § 9), z dokładnością 0,01 m (RPB § 15 ust. 3 w brzmieniu Dz.U. 2026 poz. 597, od 5.11.2026 – stosowane).
3. Rzędne terenu istniejącego – z mapy (przekładowe), projektowane – z modelu (działka, wymi: teren.punkty_projektowane); spadki nawig wg modelu, kierunek wg terenu projektowanego; kierunki spływu na trawnikach – wg spadku terenu projektowanego (interpolacja).
4. Wody opadowe z nawierzchni i dachów – na teren własny, do nieciek i zbiornika (WT § 28 ust. 2); zakaz zmiany spływu w kierunku działek sąsiednich (WT § 29) i odprowadzania na drogę (u.d.p. art. 39).
5. Punkty tyczenia – narożniki obrusy zewnętrznego ścian parteru; współrzędne w wykazie obok rysunku.
6. Jazd – geometria zastępcza [DO UZUPEŁNIENIA] (wg zezwolenia zarządcy drogi).
7. Braki danych modelu oznaczono [DO UZUPEŁNIENIA]; wykaz: projekt02_PZT/BRAKI_DANYCH.md.
8. Rysunek wygenerowany automatycznie z modelu modelu/budynek_navi (wersja 1.0, 2026-09-25) – generatory lamela.views.

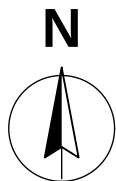

REW.	OPIS ZMIANY			DATA
0	Wydanie — rysunek wygenerowany z modelu			2026-09-25
PRACOWNIA PROJEKTOWA PRACOWNIA PROJEKTOWA — nazwa do uzupełnienia		STADIUM PB	BRANŻA ZAGOSPODAROWANIE TERENU	
adres pracowni do uzupełnienia				
INWESTOR (do uzupełnienia)				
OBIEKT / NAZWA ZAMIERZENIA BUDOWLANEGO				
Budynek mieszkalny jednorodzinny wolnostojący „Dom LAMELA” z zagospodarowaniem działki				
ADRES / LOKALIZACJA (NR DZIAŁKI, OBRĘB, JEDN. EWIDENCYJNA) ul. Lipowa (fikcyjna), dz. nr ewid. 123/4, obręb 0005 Przykładowo, gm. Przykładowo (fikcyjna)				KAT. OBIEKTU I
FUNKCJA	IMIĘ I NAZWISKO	SPECJALNOŚĆ, NR UPRAWNIEN	DATA	PODPIS
Projektant	[DO UZUPEŁNIENIA]	[DO UZUPEŁNIENIA]		
Projektant (wsp.)	[DO UZUPEŁNIENIA]	[DO UZUPEŁNIENIA]		
Sprawdzający	nie dotyczy (art. 20 ust. 3 pkt 2 PB)	—		
Opracował	[DO UZUPEŁNIENIA]	[DO UZUPEŁNIENIA]		

PLAN SZCZEGÓŁOWY — WYMIARY I RZĘDNE

SKALA 1:200	FORMAT 400×594	DATA WYDANIA 2026-09-25	RODZAJ DOK. plan szczegółowy	NR RYSUNKU PZT-02	ARKUSZ 2/3	REW. 0
-----------------------	-------------------	----------------------------	---------------------------------	-----------------------------	---------------	------------------

