


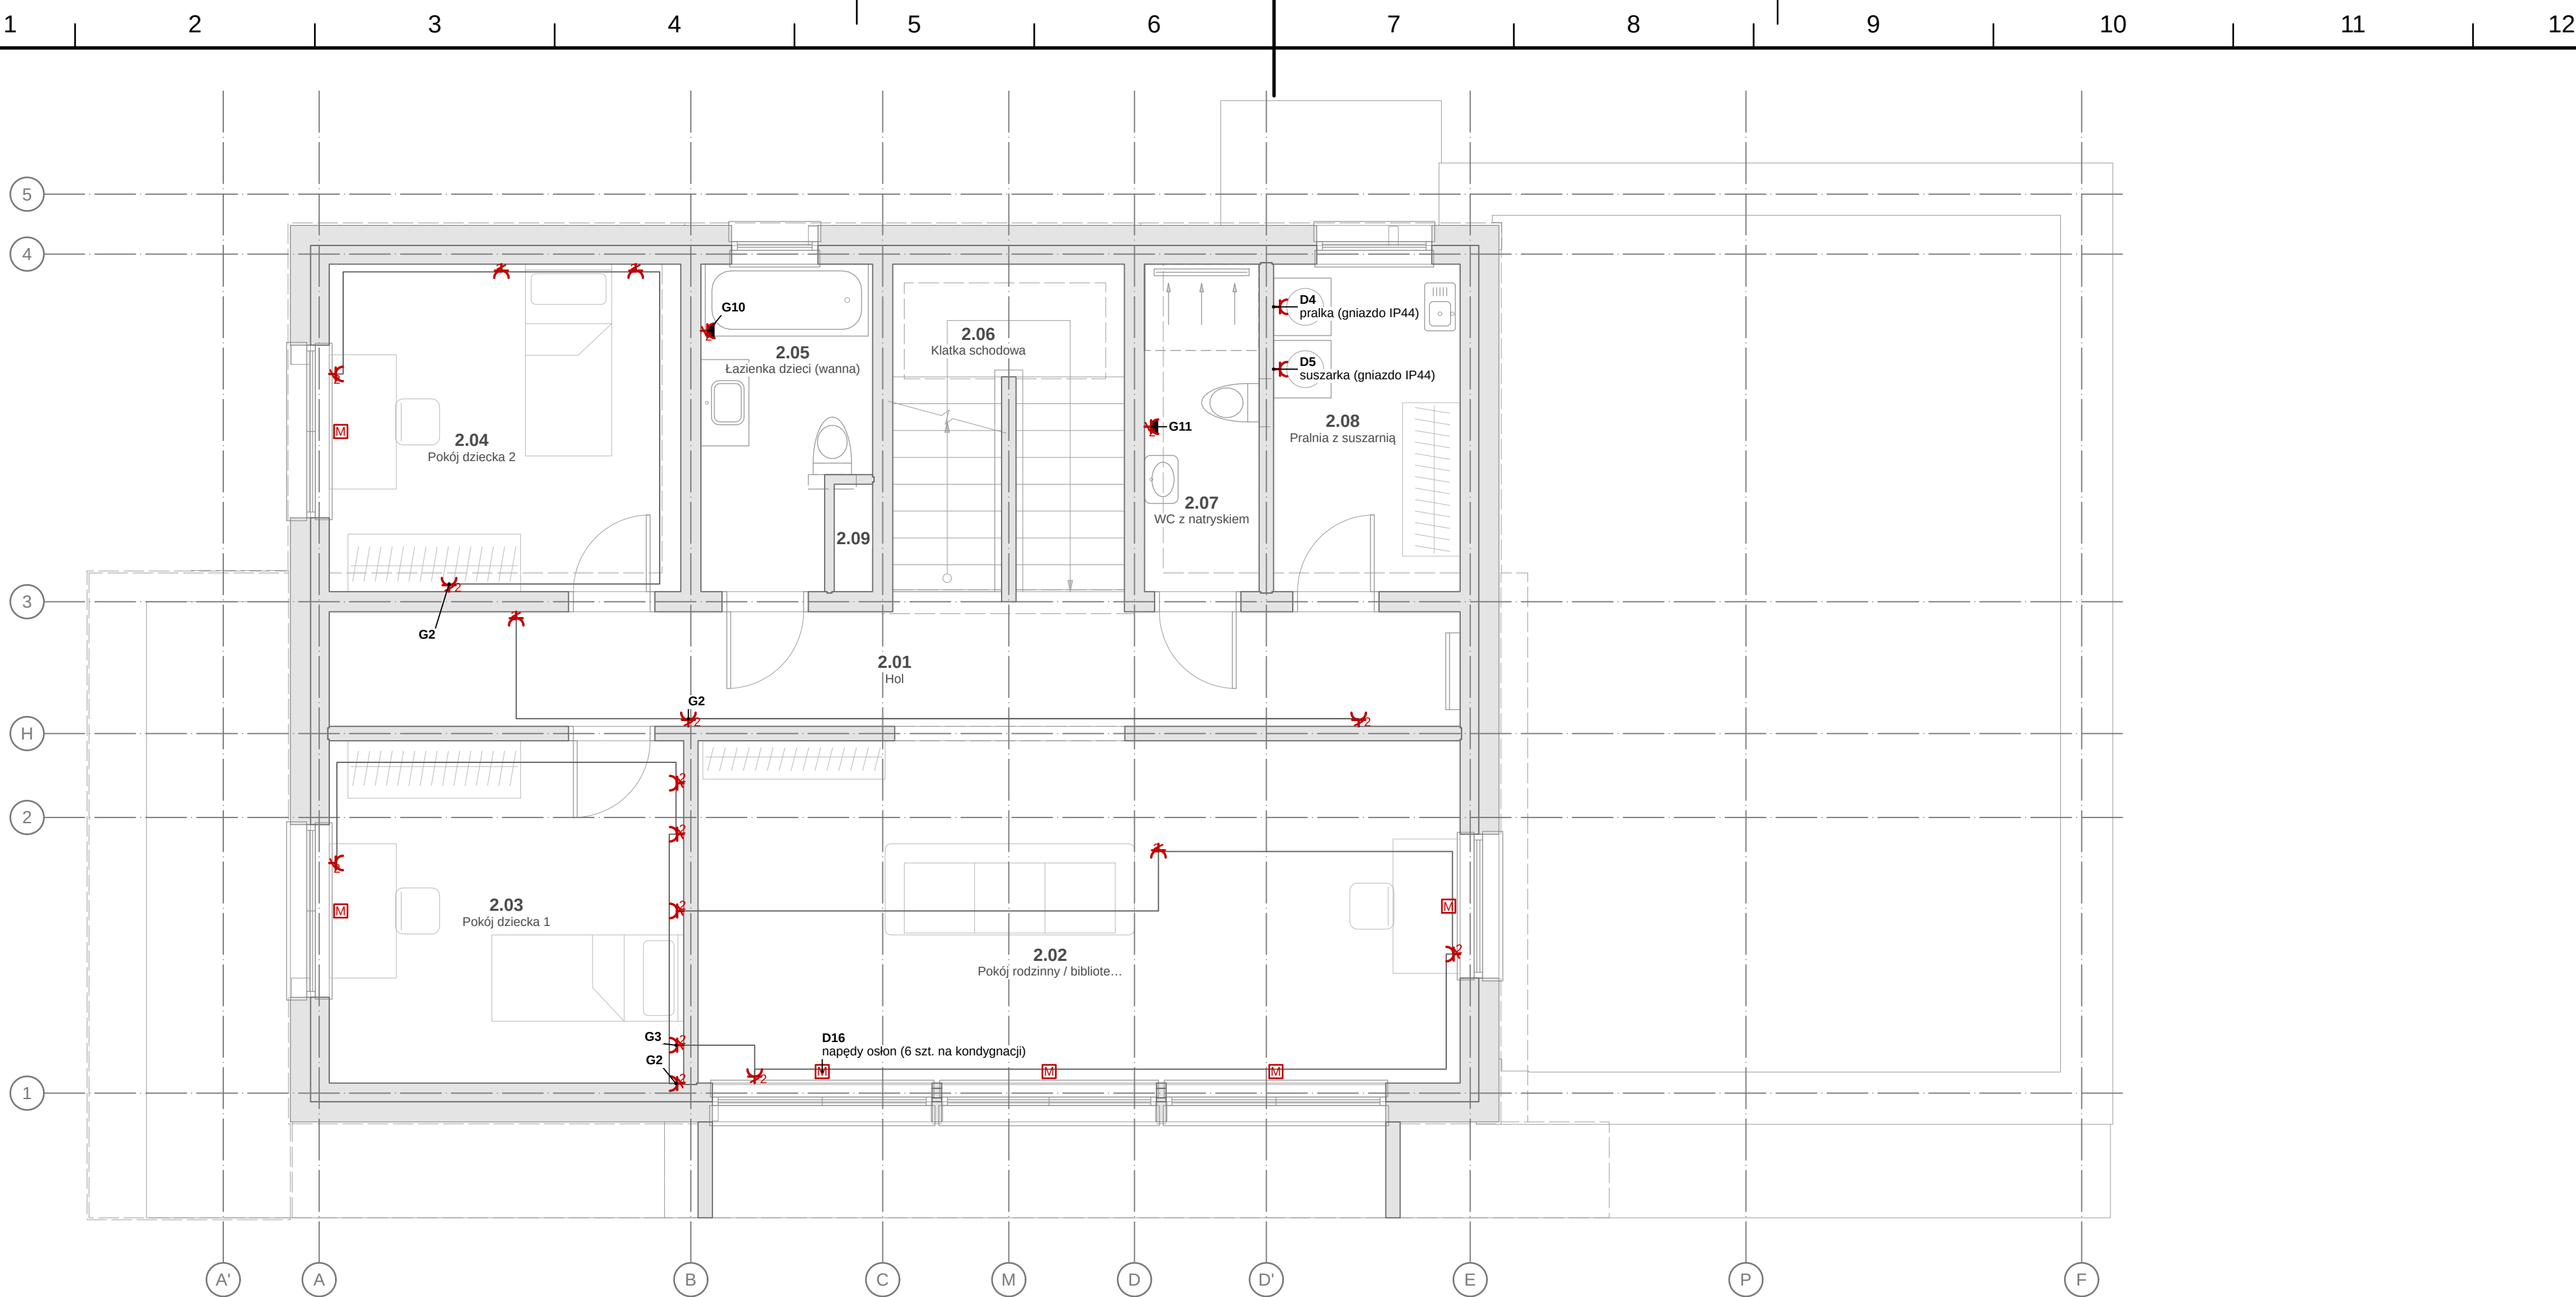

GNIAZDA I ZASILANIE URZĄDZEŃ — RZUT I PIĘTRA 1:50

OBWODY NA ARKUSZU (lamela.obliczenia.elektryka.obwody)

Obw.	Odbiorniki	Zab.	Przewód	L [m]	ΔU [%]	Faza	RCD
G2	Gniazda P1: 1.04 Pokój dziecka 2, 1.03 Pokój dziecka 1, 1.09 Szacht instalacyjny SI, 1.01 Hol, 1.06 Klatka schodowa	B16	YDYp 3×4	22,8	1,97	L3	RCBO typ A 30 mA
G3	Gniazda P1: 1.02 Pokój rodzinny / biblioteka (boks C)	B16	YDYp 3×2,5	15,9	2,22	L2	RCBO typ A 30 mA
G10	Gniazda łazienki (1.05 Łazienka dzieci (wanna))	B16	YDYp 3×4	25,8	2,18	L3	RCBO typ A 30 mA
G11	Gniazda łazienki (1.07 WC z natryskiem)	B16	YDYp 3×2,5	20,4	2,74	L2	RCBO typ A 30 mA
D4	Pralnia	B16	YDYp 3×2,5	21,0	1,77	L2	RCBO typ A 30 mA
D5	Suszarka	B16	YDYp 3×2,5	20,2	1,92	L3	RCBO typ A 30 mA
D16	Napędy osłon przeciwsłonecznych (19 szt.)	B10	YDYp 3×1,5	3,0	0,66	L2	RCBO typ A 30 mA

OBJAŚNIENIA I UWAGI


- Średnice przewodów w mm (d, z×s — rury wielowarstwowe, Ø/DN — kanalizacja, kanały wentylacyjne), przekroje żył w mm², odległości i rzędne w m; ±0,000 = 101,650 m n.p.m. (PL-EVRF2007-NH)
- Rysunki instalacji na podkładzie rzutów architektury (PB-AR); podkład — linie cienie szare (warstwy I-PODKŁAD*)
- Instalacja gniazd wtyczkowych i zasilania urządzeń wg PN-HD 60364-4-41 (samoczynne wyłączenie, RCD 30 mA dla gniazd ≤ 32 A — p. 411.3.3), PN-HD 60364-5-52 (przewody), PN-HD 60364-7-701 (łazienki), PN-HD 60364-7-722 (ładowanie EV); WT § 180–188 (obwody gniazd oddzielne od oświetlenia, gniazda ze stykiem ochronnym)
- Bilans mocy (lamela.obliczenia.elektryka.bilans): P_inst = 71,3 kW, P_szczyt z DLM = 24,8 kW ≤ P_przył = 27 kW, zabezpieczenie przedlicznikowe 40 A
- Liczbę i rozmieszczenie gniazd wyznaczono algorytmicznie (praktyka branżowa, DIN 18015-2): przy łóżkach, biurkach, sofach, nad blatem kuchennym co ok. 1,1 m, przy umywalkach (poza strefami 0–2), pozostałe równomiernie wzdłuż ścian bez otworów; urządzenia stałe — wypusty/gniazda dedykowane wg obwodów D
- Wysokości montażu (od posadзки): gniazda 0,30 m; nad blatem 1,10 m; łazienki 1,20 m (IP44); garaż, pom. techniczne 1,10 m (IP44); łączniki 1,10 m
- Rysunek wygenerowany automatycznie z modelu model/budynek.yaml (wersja 1.0, 2026-09-25) — generatory lamela.views



OZNACZENIA — LEGENDA SYMBOLI

Symbolne instalacji elektrycznych wg IEC 60617 (baza IEC; PN-EN 60617 — wycofana, stosowana jako praktyka branżowa) i PN-EN ISO 14617; oznaczenia teletechniczne — praktyka branżowa. Obowiązuje legenda na arkuszu.

—	podkład architektoniczny (rzut AR — ściany przecięte, stolarka, wyposażenie) — linie cienie szare	⚡	gniazdo bryzgoszczelne IP44 (łazienki h = 1,20 m, garaż, pom. techniczne, zewnętrzne)
—	przewody obwodów gniazd YDYp 3×2,5 (5×2,5 — 3f) — połączenia punktów (przebieg schematyczny w tynku / w posadzce)	●	wypust / puszka przyłączeniowa urządzenia zasilanego na stałe (opis: obwód, urządzenie, moc)
⌂	gniazdo wtyczkowe podwójne ze stykiem ochronnym, h = 0,30 m (kuchnia nad blatem 1,10 m)	M	M — zasilanie napędu osłony przeciwsłonecznej (żaluzja/screen) przy oknie

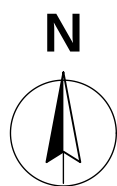

REW.	OPIS ZMIANY			DATA	
0	Wydanie — rysunek wygenerowany z modelu			2026-09-25	
PRACOWNIA PROJEKTOWA PRACOWNIA PROJEKTOWA — nazwa do uzupełnienia adres pracowni do uzupełnienia			STADIUM PT	BRANŻA INSTALACJE ELEKTRYCZNE (IE)	
INWESTOR (do uzupełnienia)					
OBIEKT / NAZWA ZAMIERZENIA BUDOWLANEGO Budynek mieszkalny jednorodzinny wolnostojący „Dom LAMELA”					
ADRES / LOKALIZACJA (NR DZIAŁKI, OBRĘB, JEDN. EWIDENCYJNA) ul. Lipowa (fikcyjna), dz. nr ewid. 123/4, obręb 0005 Przykładowo, gm. Przykładowo (fikcyjna)				KAT. OBIEKTU I	
FUNKCJA	IMIĘ I NAZWISKO		SPECJALNOŚĆ, NR UPRAWNIEŃ	DATA	PODPIS
Projektant	[DO UZUPEŁNIENIA]		[DO UZUPEŁNIENIA]		
Projektant (wsp.)	[DO UZUPEŁNIENIA]		[DO UZUPEŁNIENIA]		
Sprawdzający	nie dotyczy (art. 20 ust. 3 pkt 2 PB)		—		
Opracował	[DO UZUPEŁNIENIA]		[DO UZUPEŁNIENIA]		
TYTUŁ RYSUNKU GNIAZDA I ZASILANIE URZĄDZEŃ — RZUT I PIĘTRA					
SKALA 1:50	FORMAT A2	DATA WYDANIA 2026-09-25	RODZAJ DOK. rzut instalacji	NR RYSUNKU PT-IE-05	ARKUSZ 5/14
					REW. 0