


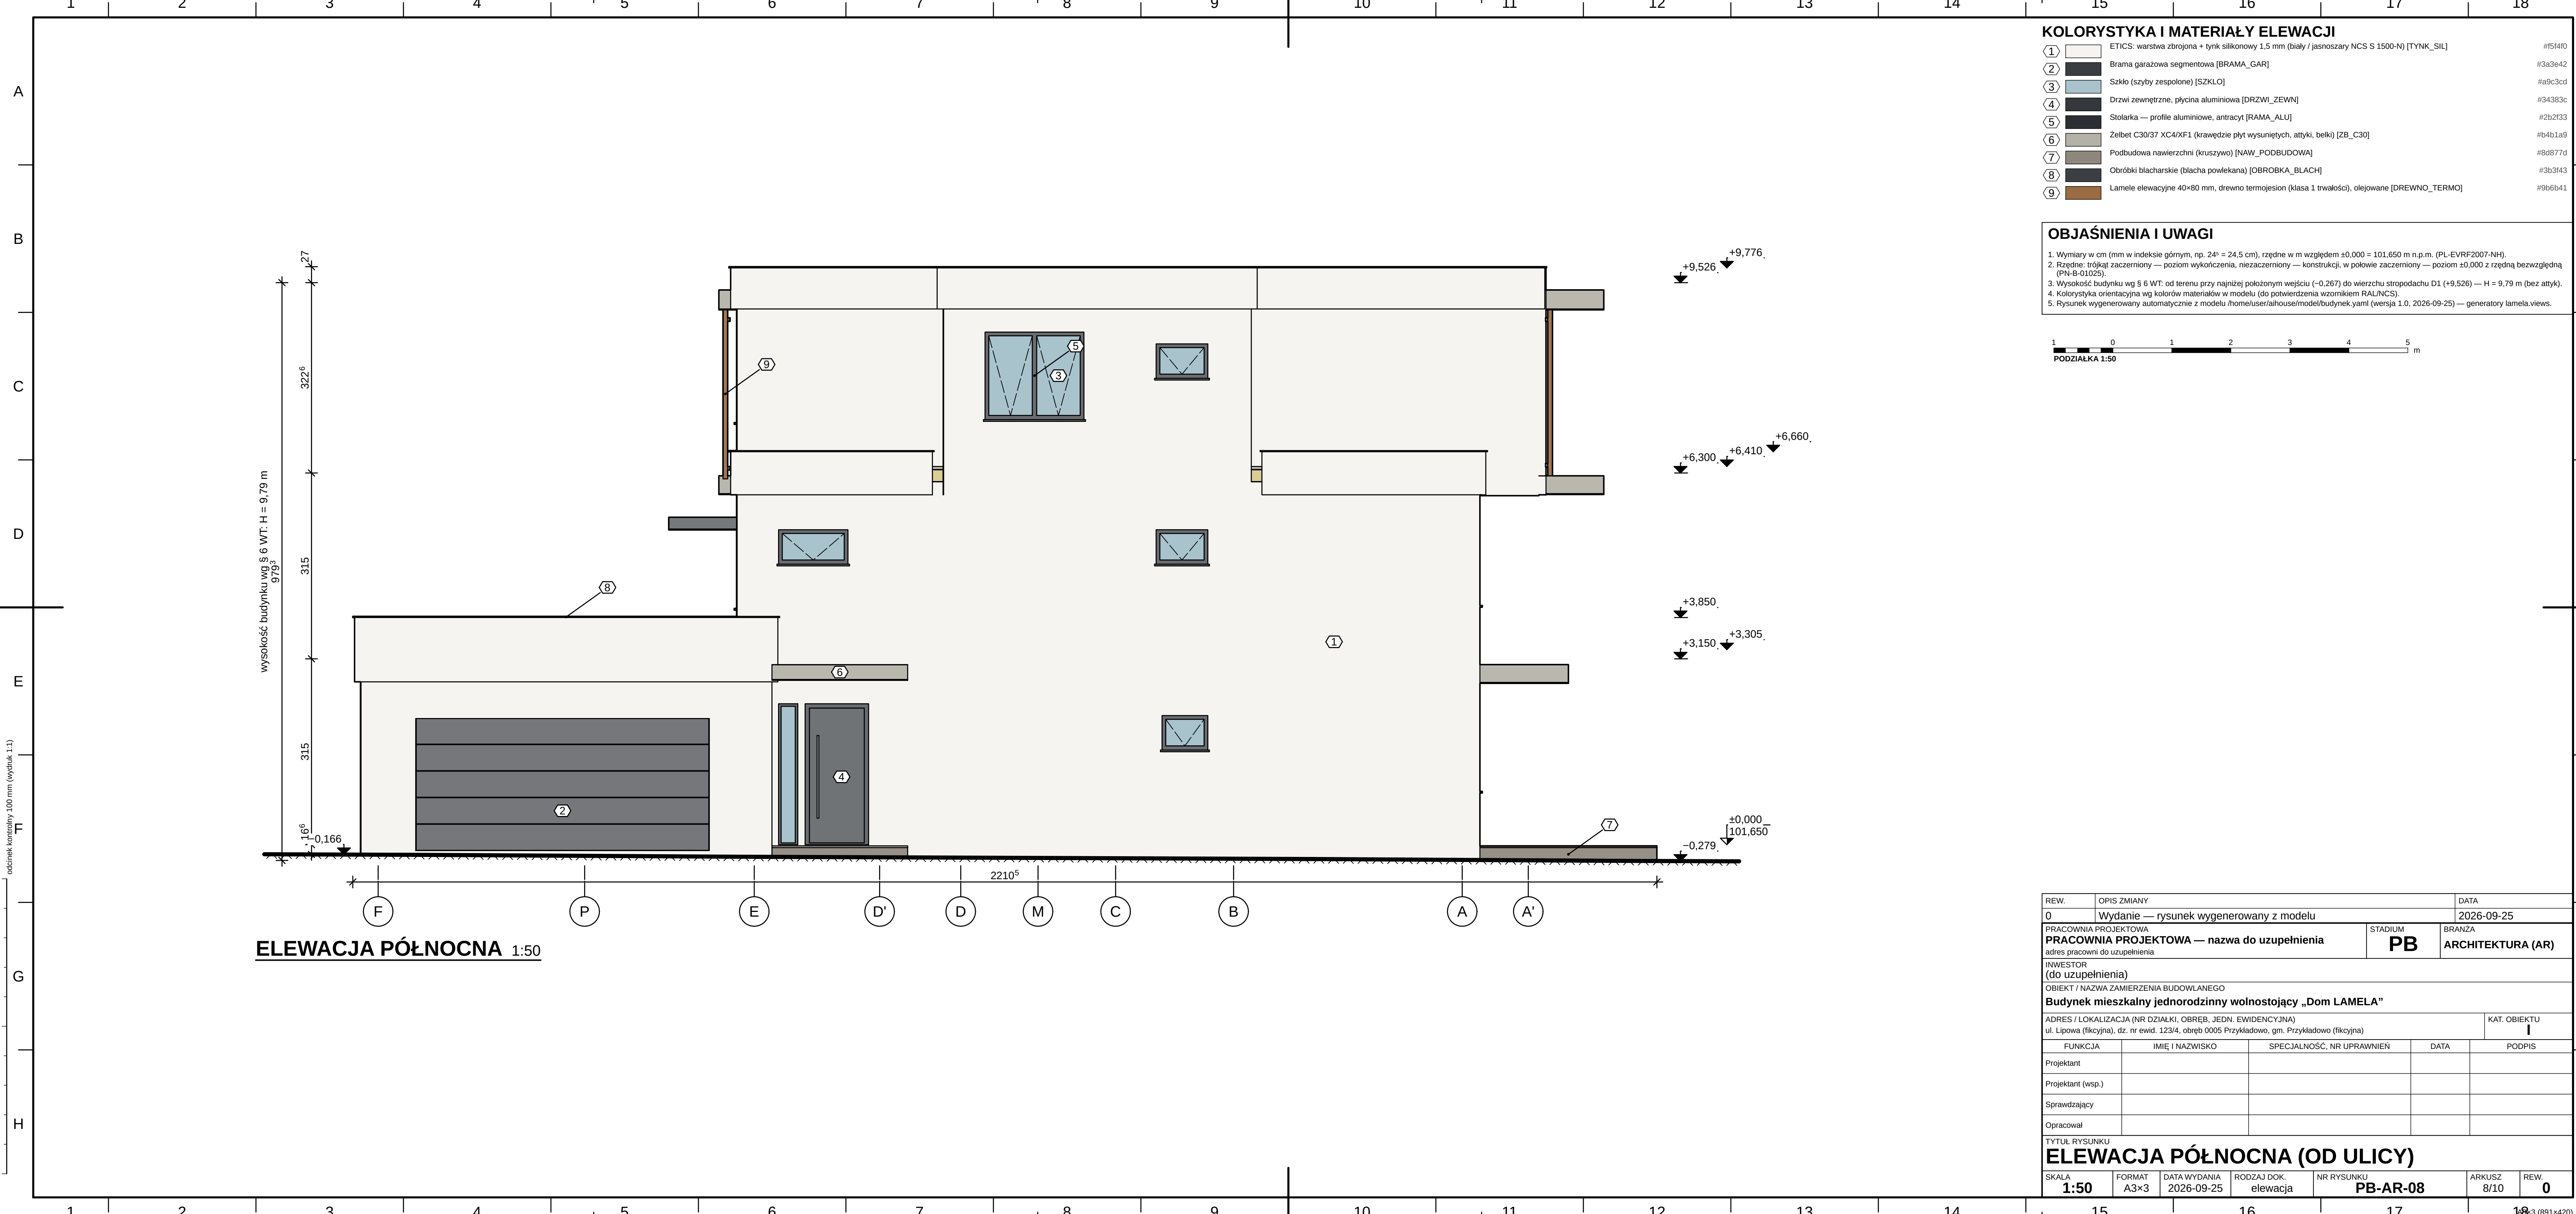


KOLORYSTYKA I MATERIAŁY ELEWACJI

①	ETICS: warstwa zbrojona + tynk silikonowy 1,5 mm (biały / jasnoszary NCS S 1500-N) [TYNK_SIL]	#f5f4f0
②	Brama garażowa segmentowa [BRAMA_GAR]	#3a3e42
③	Szkoło (szyby zespolone) [SZKLO]	#a9c3cd
④	Drzwi zewnętrzne, płycina aluminiowa [DRZWI_ZEWN]	#34383c
⑤	Stolarka — profile aluminiowe, antracyt [RAMA_ALU]	#2b2f33
⑥	Żelbet C30/37 XC4/XF1 (krawędzie płyt wysuniętych, attyki, belki) [ZB_C30]	#b4b1a9
⑦	Podbudowa nawierzchni (kruszywo) [NAW_PODBUDOWA]	#8d877d
⑧	Otróbbki blacharskie (blacha powlekana) [OBROBKA_BLACH]	#3b3f43
⑨	Lamele elewacyjne 40×80 mm, drewno termojesion (klasa 1 trwałości), olejowane [DREWNO_TERMO]	#9b6b41

OBJAŚNIENIA I UWAGI

- Wymiary w cm (mm w indeksie górnym, np. 24⁶ = 24,5 cm), rzędne w m względem ±0,000 = 101,650 m n.p.m. (PL-EVRF2007-NH).
- Rzędne: trójkąt zaczerpiony — poziom wykończenia, niezaczerpiony — konstrukcji, w połowie zaczerpiony — poziom ±0,000 z rzędną bezwzględną (PN-B-01025).
- Wysokość budynku wg § 6 WT: od terenu przy najniżej położonym wejściu (−0,267) do wierzchu stropodachu D1 (+9,526) — H = 9,79 m (bez attyki).
- Kolorystyka orientacyjna wg kolorów materiałów w modelu (do potwierdzenia wzornikiem RALNCS).
- Rysunek wygenerowany automatycznie z modelu /home/user/ai/house/model/budynek.yaml (wersja 1.0, 2026-09-25) — generatory lamela.views.

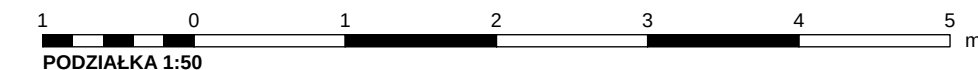

REW.	OPIS ZMIANY			DATA	
0	Wydanie — rysunek wygenerowany z modelu			2026-09-25	
PRACOWNIA PROJEKTOWA			STADIUM	BRANŻA	
PRACOWNIA PROJEKTOWA — nazwa do uzupełnienia			PB	ARCHITEKTURA (AR)	
adres pracowni do uzupełnienia					
INWESTOR					
(do uzupełnienia)					
OBIEKT / NAZWA ZAMIERZENIA BUDOWLANEGO					
Budynek mieszkalny jednorodzinny wolnostojący „Dom LAMELA”					
ADRES / LOKALIZACJA (NR DZIAŁKI, OBRĘB, JEDN. EWIDENCYJNA)					KAT. OBIEKTU
ul. Lipowa (fikcyjna), dz. nr ewid. 123/4, obręb 0005 Przykładowo, gm. Przykładowo (fikcyjna)					I
FUNKCJA		IMIĘ I NAZWISKO	SPECJALNOŚĆ, NR UPRAWNIENIEŃ	DATA	PODPIS
Projektant					
Projektant (wsp.)					
Sprawdzający					
Opracował					
TYTUŁ RYSUNKU					
ELEWACJA PÓŁNOCNA (OD ULICY)					
SKALA	FORMAT	DATA WYDANIA	RODZAJ DOK.	NR RYSUNKU	ARKUSZ
1:50	A3×3	2026-09-25	elewacja	PB-AR-08	8/10
					REW.
					0