

# TOM RYSUNKÓW ARCHITEKTURY — WIDOKI Z MOD

| Lp. | Nr rys.  | Tytuł rysunku                  | Skala | Format |
|-----|----------|--------------------------------|-------|--------|
| 1   | PB-AR-01 | RZUT PARTERU                   | 1:50  | A1     |
| 2   | PB-AR-02 | RZUT I PIĘTRA                  | 1:50  | A3×3   |
| 3   | PB-AR-03 | RZUT II PIĘTRA                 | 1:50  | A3×3   |
| 4   | PB-AR-05 | PRZEKRÓJ A-A                   | 1:50  | A3×3   |
| 5   | PB-AR-06 | PRZEKRÓJ B-B                   | 1:50  | A3×3   |
| 6   | PB-AR-07 | ELEWACJA POŁUDNIOWA (OGRODOWA) | 1:50  | A3×3   |
| 7   | PB-AR-08 | ELEWACJA PÓŁNOCNA (OD ULICY)   | 1:50  | A3×3   |
| 8   | PB-AR-09 | ELEWACJA WSCHODNIA             | 1:50  | A2     |
| 9   | PB-AR-10 | ELEWACJA ZACHODNIA             | 1:50  | A2     |

|   |                 |                            |                                    |                               |             |      |
|---|-----------------|----------------------------|------------------------------------|-------------------------------|-------------|------|
| PRACOWNIA PROJEKTOWA<br><b>PRACOWNIA PROJEKTOWA — nazwa do uzupełnienia</b>                                                                                 |                 | STADIUM<br><b>PB</b>       | BRANŻA<br><b>ARCHITEKTURA (AR)</b> |                               |             |      |
| INWESTOR<br>(do uzupełnienia)   |                 |                            |                                    |                               |             |      |
| OBIEKT / NAZWA ZAMIERZENIA BUDOWLANEGO<br><b>Budynek mieszkalny jednorodzinny wolnostojący „Dom LAMELA”</b>                                                 |                 |                            |                                    |                               |             |      |
| ADRES / LOKALIZACJA (NR DZIAŁKI, OBRĘB, JEDN. EWIDENCYJNA)<br>ul. Lipowa (fikcyjna), dz. nr ewid. 123/4, obręb 0005 Przykładowo, gm. Przykładowo (fikcyjna) |                 |                            |                                    | KAT. OBIEKTU<br><b>I</b>      |             |      |
| FUNKCJA   | IMIĘ I NAZWISKO | SPECJALNOŚĆ, NR UPRAWNIENI | DATA                               | PODPIS                        |             |      |
| Projektant   |                 |                            |                                    |                               |             |      |
| Projektant (wsp.)   |                 |                            |                                    |                               |             |      |
| Sprawdzający   |                 |                            |                                    |                               |             |      |
| Opracował   |                 |                            |                                    |                               |             |      |
| TYTUŁ RYSUNKU<br><b>SPIS RYSUNKÓW</b>   |                 |                            |                                    |                               |             |      |
| SKALA<br>—   | FORMAT<br>A4    | DATA WYDANIA<br>2026-09-25 | RODZAJ DOK.<br>spis                | NR RYSUNKU<br><b>PB-AR-00</b> | ARKUSZ<br>— | REW. |


odcinek kontury 100 mm (wydruk 1:1)

RZUT PARTERU 1:50

|                                                                                              |                                         |                           |             |                   |
|----------------------------------------------------------------------------------------------|-----------------------------------------|---------------------------|-------------|-------------------|
| REW.                                                                                         | OPIS ZMIANY                             |                           |             | DATA              |
| 0                                                                                            | Wydanie — rysunek wygenerowany z modelu |                           |             | 2026-09-25        |
| PRACOWNIA PROJEKTOWA                                                                         |                                         |                           | STADIUM     | BRANŻA            |
| PRACOWNIA PROJEKTOWA — nazwa do uzupełnienia                                                 |                                         |                           | PB          | ARCHITEKTURA (AR) |
| adres pracowni do uzupełnienia                                                               |                                         |                           |             |                   |
| INWESTOR                                                                                     |                                         |                           |             |                   |
| (do uzupełnienia)                                                                            |                                         |                           |             |                   |
| OBJEKT / NAZWA ZAMIERZENIA BUDOWLANEGO                                                       |                                         |                           |             |                   |
| Budynek mieszkalny jednorodzinny wolnostojący „Dom LAMELA”                                   |                                         |                           |             |                   |
| ADRES / LOKALIZACJA (NR DZIAŁKI, OBRĘB, JEDN. EWIDENCYJNA)                                   |                                         |                           |             | KAT. OBJEKTU      |
| ul. Lipowa (fikcyjna), dz. nr ewid. 1234, obręb 0005 Przykładowo, gm. Przykładowo (fikcyjna) |                                         |                           |             | I                 |
| FUNKCJA                                                                                      | IMIĘ I NAZWISKO                         | SPECJALNOŚĆ, NR UPRAWNIEN | DATA        | PODPIS            |
| Projektant                                                                                   |                                         |                           |             |                   |
| Projektant (wsp.)                                                                            |                                         |                           |             |                   |
| Sprawdzający                                                                                 |                                         |                           |             |                   |
| Opracował                                                                                    |                                         |                           |             |                   |
| TYTUŁ RYSUNKU                                                                                |                                         |                           |             |                   |
| RZUT PARTERU                                                                                 |                                         |                           |             |                   |
| SKALA                                                                                        | FORMAT                                  | DATA WYDANIA              | RODZAJ DOK. | NR RYSUNKU        |
| 1:50                                                                                         | A1                                      | 2026-09-25                | Izot        | PB-AR-01          |
|                                                                                              |                                         |                           |             | ARKUSZ            |
|                                                                                              |                                         |                           |             | 1/10              |
|                                                                                              |                                         |                           |             | REW.              |
|                                                                                              |                                         |                           |             | 0                 |

OBJAŚNIENIA I UWAGI

- Wymiary w cm (mm w indeksie górnym, np. 24<sup>5</sup> = 24,5 cm), rzędne w m względem ±0,000 = 101,650 m n.p.m. (PL-EVRF2007-NH).
- Rzuty: płaszczyzna cięcia +1,10 m nad posadzką kondygnacji. Linia kreskową — elementy nad płaszczyznę cięcia (obrys płyt i wsporników, brył wyższych kondygnacji, otwory w stropie nad, belki); linia cienią — elementy poniżej (widok).
- Otwory: licznik — szerokość, mianownik — wysokość w świetle otworu, w nawiasie wysokość parapetu; symbol stolarki wg zestawienia stolarki.
- Numeracja pomieszczeń wg PN-B-01025 / PN-EN ISO 4157-2: <nr kondygnacji (parter = 1)> <nr>; identyfikator w modelu: <kond> <nr> (parter = 0).
- Drzwi: strona otwierania (lewej/prawej) wg modelu — patrząc od strony, w którą otwiera się skrzydło.
- Rysunek wygenerowany automatycznie z modelu /home/user/ai/house/model/budynek.yaml (wersja 1.0, 2026-09-25) — generatory lamela.views.

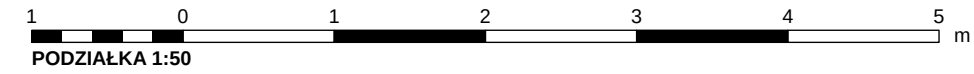

ZESTAWIENIE POMIESZCZEŃ


| Nr                               | Nazwa pomieszczenia             | Posadzka                                            | Kat. | Wys. [m] | Pow. [m²] |
|----------------------------------|---------------------------------|-----------------------------------------------------|------|----------|-----------|
| 1.06                             | Salon + jadalnia + kuchnia      | Deska warstwowa dębowa 15 mm, klejona, podst.       |      | 2,77     | 54,44     |
| 1.13                             | Garaż 2-stanowiskowy            | Posadzka żywiczna epoksydowa antypoślizgowa (garaż) |      | 2,76     | 37,42     |
| 1.10                             | Pokój gościnny / gabinet        | Deska warstwowa dębowa 15 mm, klejona, podst.       |      | 2,77     | 12,52     |
| 1.12                             | Pomieszczenie techniczne        | Płytki gresowe 60×120 na kleju C2TE S1 techn.       |      | 2,76     | 8,85      |
| 1.11                             | Przedśionek gospodarczy         | Płytki gresowe 60×120 na kleju C2TE S1 ruchu        |      | 2,76     | 7,18      |
| 1.05                             | Śpiżarnia (pod schodami)        | Płytki gresowe 60×120 na kleju C2TE S1 pomoc.       |      | 1,90     | 5,40      |
| 1.02                             | Hol                             | Płytki gresowe 60×120 na kleju C2TE S1 ruchu        |      | 2,77     | 4,44      |
| 1.01                             | Wiatrołap                       | Płytki gresowe 60×120 na kleju C2TE S1 ruchu        |      | 2,77     | 3,89      |
| 1.09                             | Łazienka gościnna (natrysk)     | Płytki gresowe 60×120 na kleju C2TE S1 pomoc.       |      | 2,77     | 3,84      |
| 1.07                             | Pas komunikacyjny przy schodach | Deska warstwowa dębowa 15 mm, klejona, ruchu        |      | 2,77     | 3,51      |
| 1.04                             | Klatka schodowa                 | Deska warstwowa dębowa 15 mm, klejona, ruchu        |      | 2,77     | 2,82      |
| 1.03                             | WC gościnne                     | Płytki gresowe 60×120 na kleju C2TE S1 pomoc.       |      | 2,77     | 2,32      |
| 1.08                             | Przedpokój gościnny             | Deska warstwowa dębowa 15 mm, klejona, ruchu        |      | 2,77     | 1,44      |
| RAZEM powierzchnia netto         |                                 |                                                     |      |          | 148,07    |
| w tym użytkowa (podst. + pomoc.) |                                 |                                                     |      |          | 115,94    |

OZNACZENIA MATERIAŁÓW (PN-B-01030 + przyjęte)

|  |   |  |                                                                                                  |
|--|---|--|--------------------------------------------------------------------------------------------------|
|  | Wełna mineralna 035 (szkielet, docieplenia, ściana dom-garaż) — materiał UKU7   |  | Ściana szklana VSG 2 x 8 mm w ramie aluminiowej (wiatrołap / hol)                                |
|  | Styropian grafaitowy EPS 031 (ETICS, NRO w systemie) — zryzek VVV   |  | Żelbet C25/30, B500SP (stropy, płyta fundamentowa, ściany) — 45° na przeniam ciągle i przerywane |
|  | Bloczek wapienno-piaskowy 12 cm, kl. 15 (ścianki działowe, liczy w klatce), Bloczek wapienno-piaskowy (silika) 18 cm, kl. 20, gr. 1, na zaprawie cienkowarstwowej — kratka ukośna 45°/135° |  |                                                                                                  |

OZNACZENIA LINII

- elementy nad płaszczyznę cięcia (obrys płyt, wsporników, brył wyższych kondygnacji)
- elementy poniżej płaszczyzny cięcia (widok z góry)
- osie konstrukcyjne; linia punktowa z pogrubionymi końcami — ślad przekroju

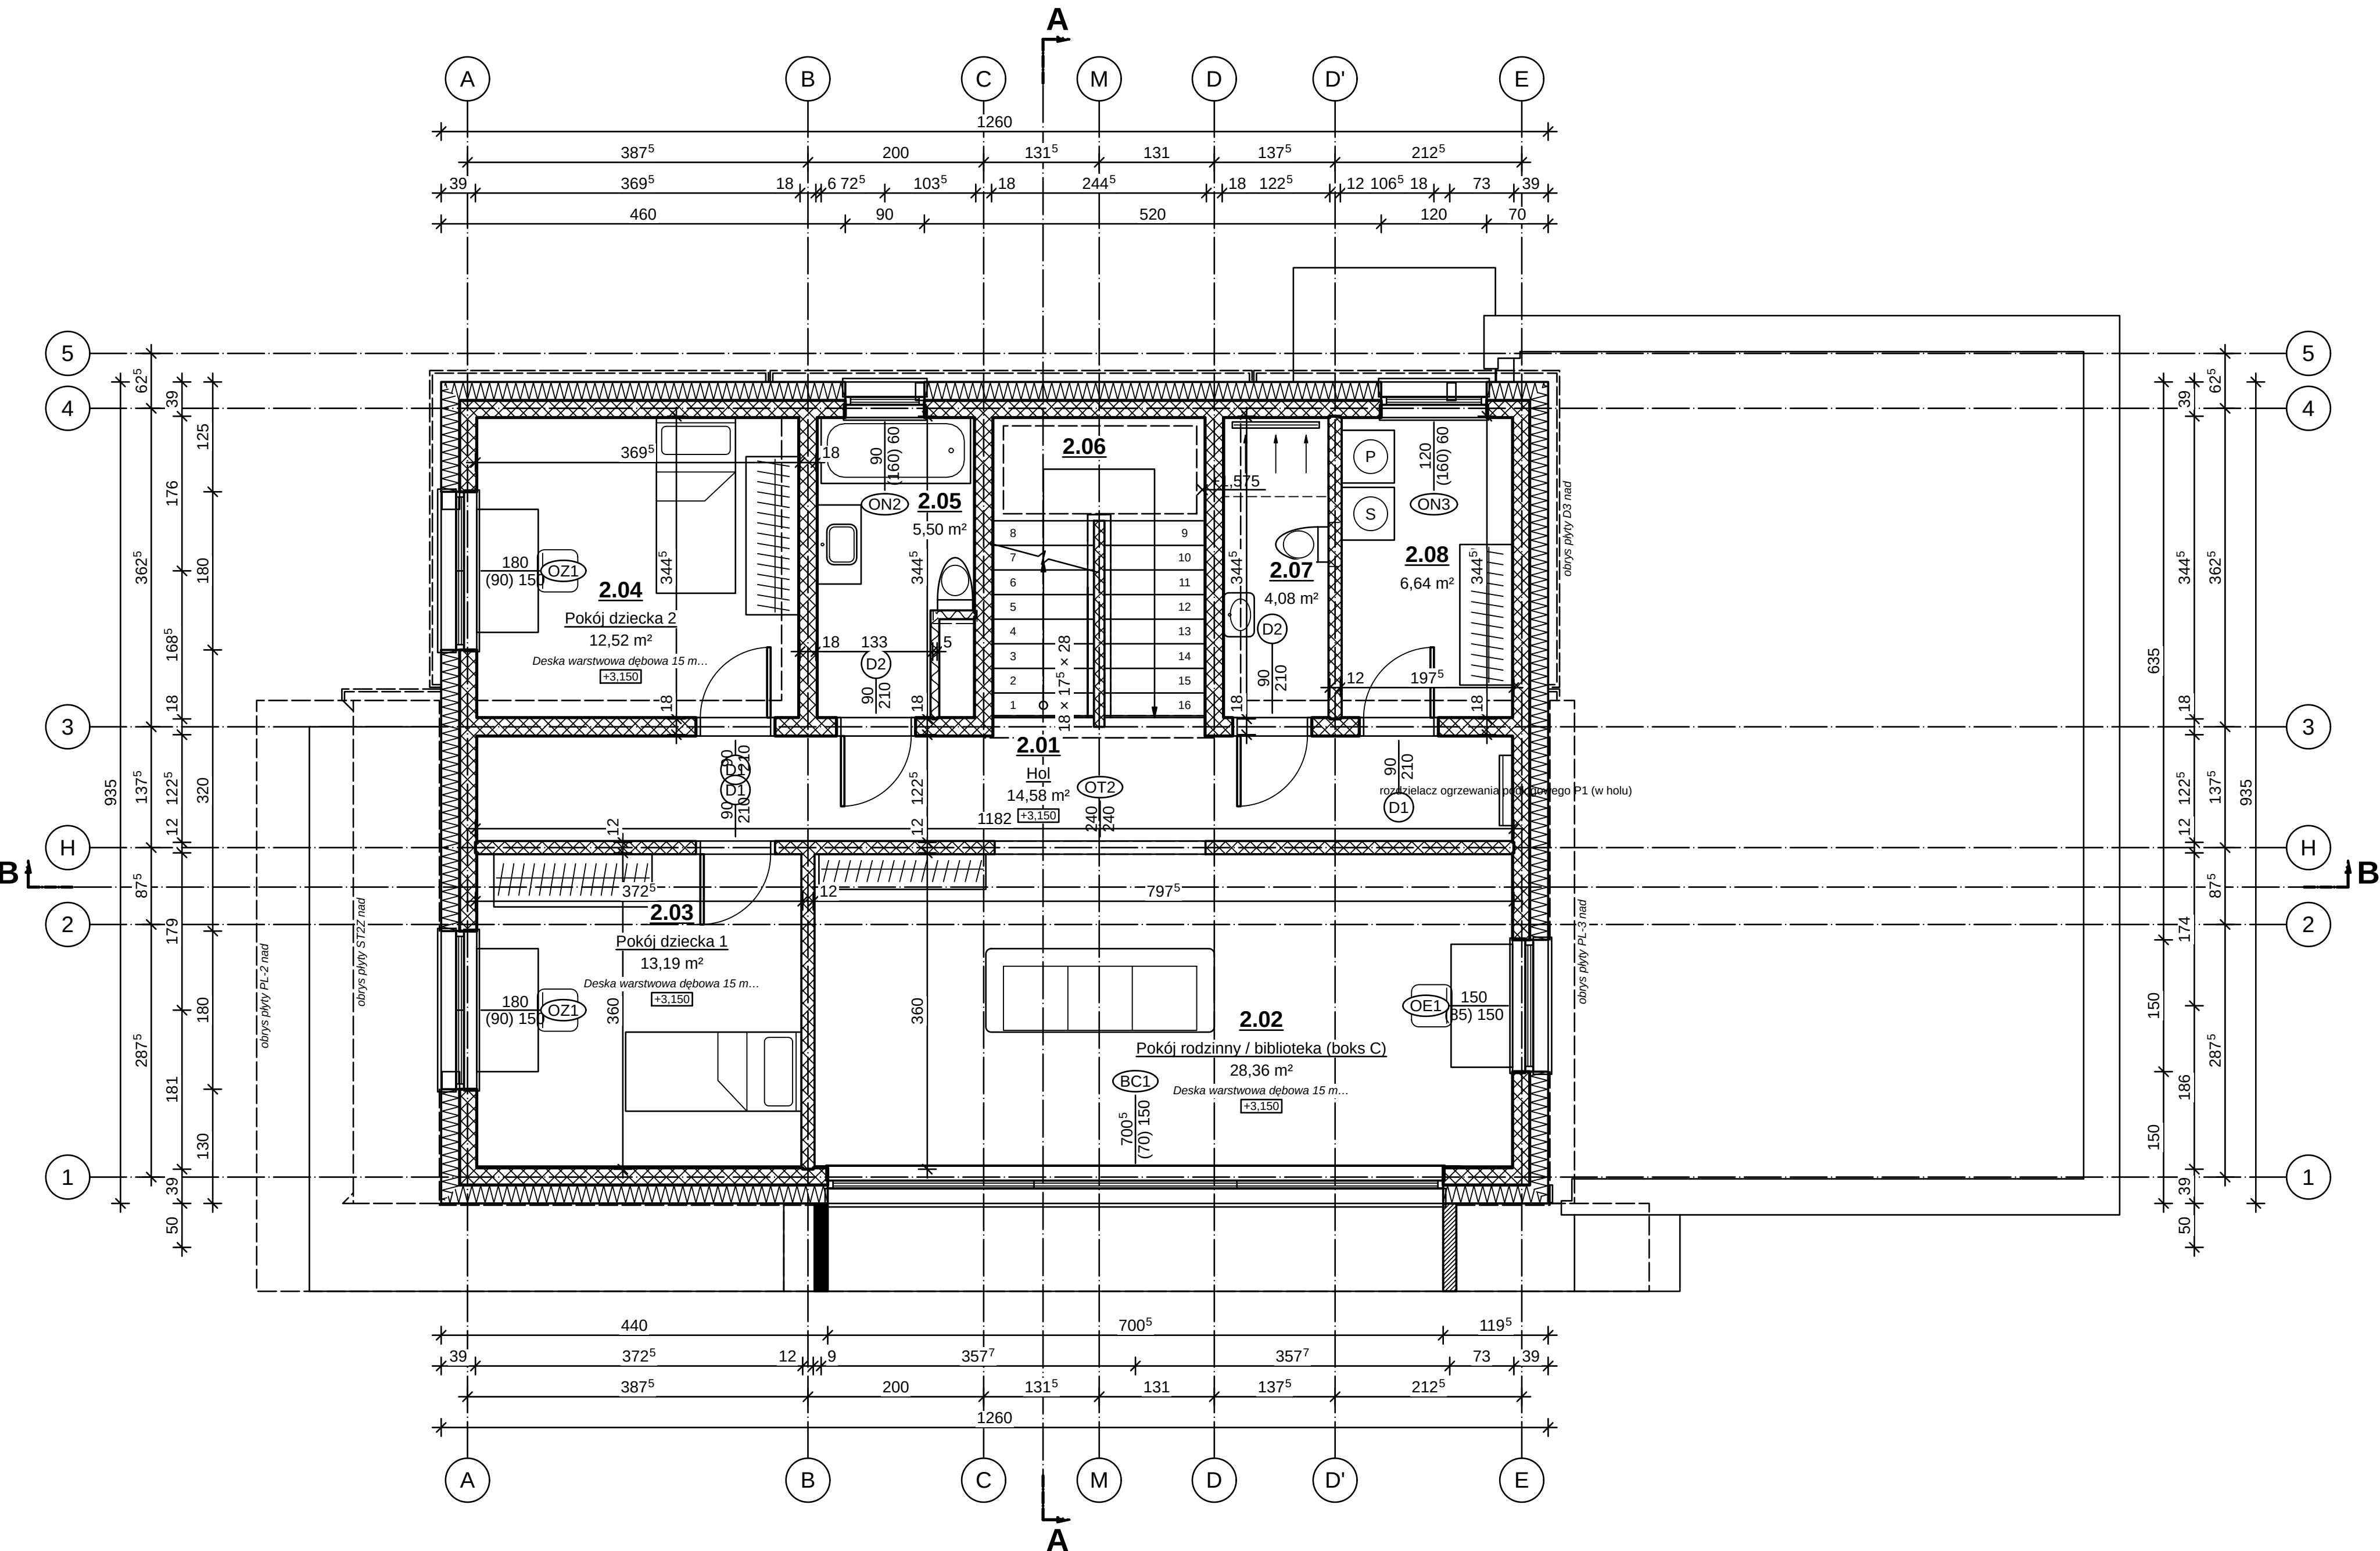



| Nr   | Nazwa pomieszczenia                  | Posadzka                                 | Kat.   | Wys. [m] | Pow. [m²] |
|------|--------------------------------------|------------------------------------------|--------|----------|-----------|
| 2.02 | Pokój rodzinny / biblioteka (boks C) | Deska warstwowa dębowa 15 mm, klejona    | podst. | 2,77     | 28,36     |
| 2.01 | Hol                                  | Deska warstwowa dębowa 15 mm, klejona    | uchu   | 2,77     | 14,58     |
| 2.03 | Pokój dziecka 1                      | Deska warstwowa dębowa 15 mm, klejona    | podst. | 2,77     | 13,19     |
| 2.04 | Pokój dziecka 2                      | Deska warstwowa dębowa 15 mm, klejona    | podst. | 2,77     | 12,52     |
| 2.08 | Pralnia z suszarnią                  | Platyki gresowe 60x120 na kleju C2TE \$1 | pomoc. | 2,77     | 6,64      |
| 2.05 | Łazienka dzieci (wanna)              | Platyki gresowe 60x120 na kleju C2TE \$1 | pomoc. | 2,77     | 5,50      |
| 2.07 | WC z natryskiem                      | Platyki gresowe 60x120 na kleju C2TE \$1 | pomoc. | 2,77     | 4,08      |
| 2.06 | Klatka schodowa                      | Deska warstwowa dębowa 15 mm, klejona    | uchu   | 2,77     | 0,00      |
|      | RAZEM powierzchnia netto             |                                          |        |          | 84,88     |
|      | w tym użytkowa (podst. + pomoc.)     |                                          |        |          | 70,30     |

|   |   |
|---|---|
|  <p>Wetna mineralna 035 (szkielet, docieplenia, ściana dom-garaz) – meander „UUU”</p>  <p>Styropian grafitowy EPS 031 (ETICS, NRO w systemie) – zygzak „VVV”</p> |  <p>Bloczek wapieno-piaskowy 12 cm, kl. 15 (ściana ścianki, nogi w łazie); Bloczek wapieno-piaskowy (słitka) 18 cm, kl. 20, gr. 1 na zaprawie cementowo-wodnej – kratka ukośna 45°/135°</p>  <p>Rama boku C: ruszt stalowy ocynkowany w oddzielnie z blachy aluminiowej RAL 7016 (pusta w środku); Stal konstrukcyjna S355 (slaty RK, rama boku C); cynkowana ognowo + malowana proszkowo RAL 7016 – zaczerpienie</p> |
|---|---|

— — — — — elementy nad płaszczyzną cięcia (obrysy płyt, wsporników, brył wyższych kondygnacji)  
 — — — — — elementy poniżej płaszczyzny cięcia (widok z góry)  
 — — — — — osie konstrukcyjne; linia punktowa z pogrubionymi końcami — ślad przekroju

1. Wymiar:  $x$  cm (mm w indeksie górnym, np. 24<sup>+</sup> = 24,5 cm), rzędne  $y$  w m względem 0+000 = 101,650 m n.p.m. (PL-EVRF7007-NH).  
2. Rzut: planszyczna cisła +1,10 m nad posadzką podziemną. Linia kreskowa – element nad planszyczną cisłą (obrys był i wsporników, brył wyznaczających), otwory w rzucie (nad, belki), linie cisła – elementy poniżej wlotu.  
3. Otwory: rurki, szerokość, min. wysokość w rzucie (nad, belki), min. wysokość parapełtu. Symbol stołarki w zestawieniu stołarki.  
4. Numeracja pomieszczeń: np. 01025 / PN-EV 01157-2 (01157-2 to kod kondygnacji, 01157-2 – identyfikator w zestawieniu). (parter = 0)  
5. Rzut: sygnatura otwierania (lewe/prawe) w modelu – parter/od w rzucie, w która otwiera się skrzydło.  
6. Długość: wygenerowana automatycznie z modelu – path/user/aihouse/model/budynek.yamł (wersja 1.0, 2026-09-25) – generatory lambda.views

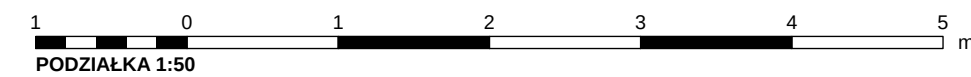19x3 (891x420)

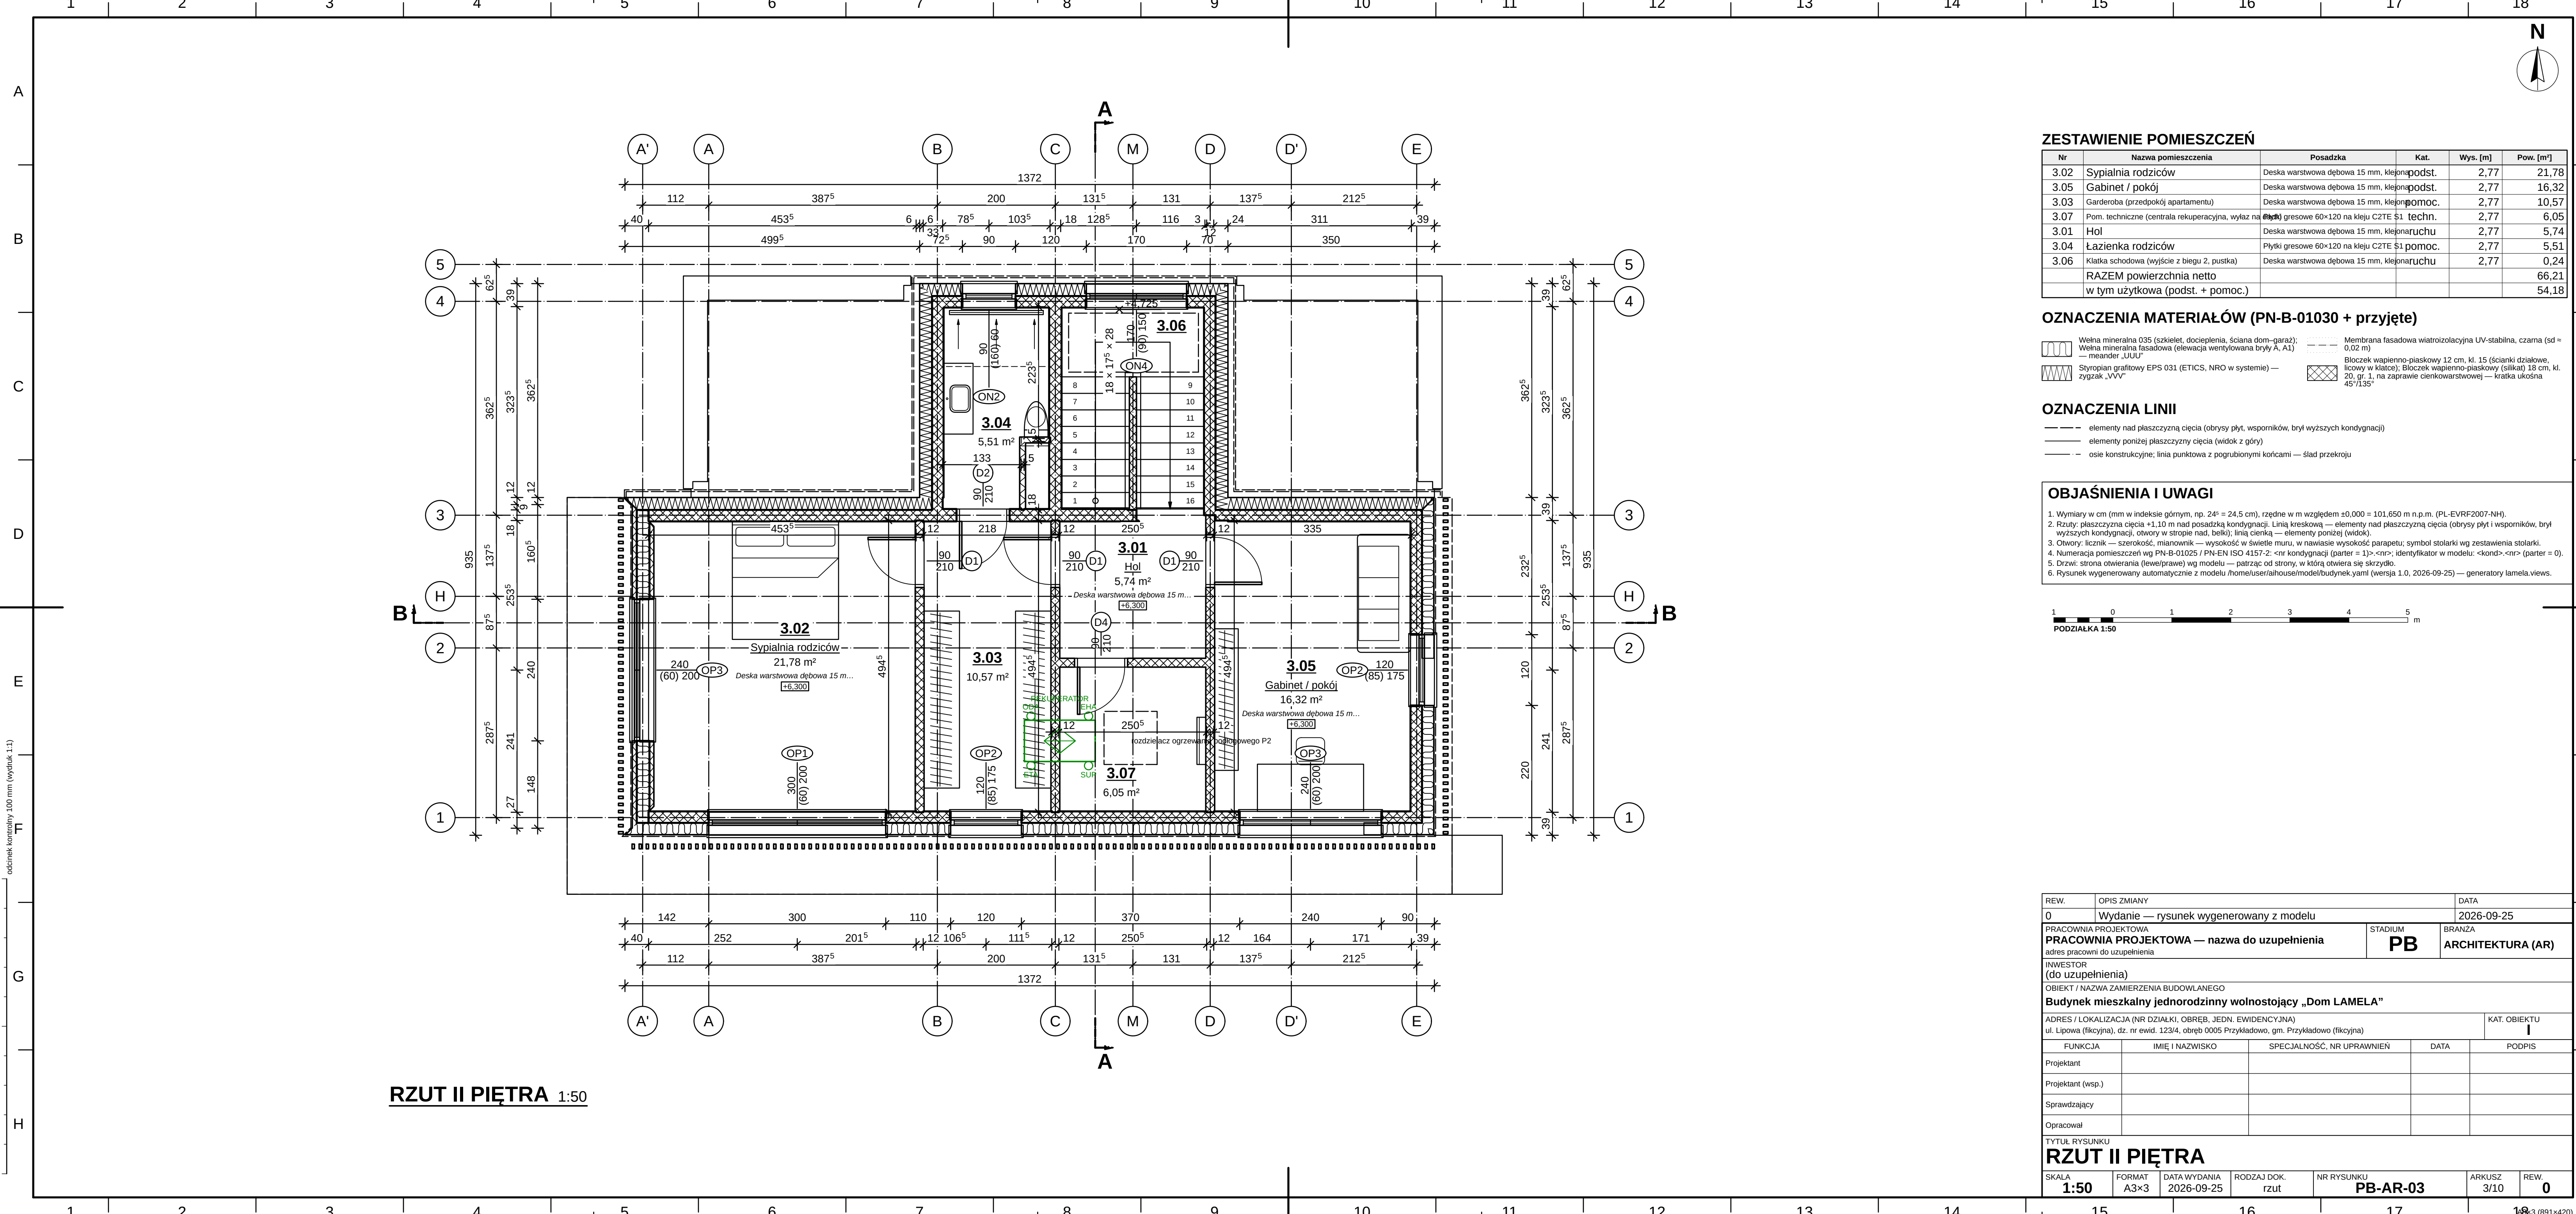

RZUT II PIĘTRA 1:50

ZESTAWIENIE POMIESZCZEŃ

| Nr                               | Nazwa pomieszczenia                                     | Posadzka                                       | Kat.   | Wys. [m] | Pow. [m²] |
|----------------------------------|---------------------------------------------------------|------------------------------------------------|--------|----------|-----------|
| 3.02                             | Sypialnia rodziców                                      | Deska warstwowa dębowa 15 mm, klejona          | podst. | 2,77     | 21,78     |
| 3.05                             | Gabinet / pokój                                         | Deska warstwowa dębowa 15 mm, klejona          | podst. | 2,77     | 16,32     |
| 3.03                             | Garderoba (przedpokój apartamentu)                      | Deska warstwowa dębowa 15 mm, klejona          | pomoc. | 2,77     | 10,57     |
| 3.07                             | Pom. techniczne (centrala rekuperacyjna, wylaz na dach) | Płytki gresowe 60x120 na kleju C2TE \$1 techn. | pomoc. | 2,77     | 6,05      |
| 3.01                             | Hol                                                     | Deska warstwowa dębowa 15 mm, klejona          | aruchu | 2,77     | 5,74      |
| 3.04                             | Łazienka rodziców                                       | Płytki gresowe 60x120 na kleju C2TE \$1 techn. | pomoc. | 2,77     | 5,51      |
| 3.06                             | Klatka schodowa (wyjście z biegu 2, pustka)             | Deska warstwowa dębowa 15 mm, klejona          | aruchu | 2,77     | 0,24      |
| RAZEM powierzchnia netto         |                                                         |                                                |        |          | 66,21     |
| w tym użytkowa (podst. + pomoc.) |                                                         |                                                |        |          | 54,18     |

OZNACZENIA MATERIAŁÓW (PN-B-01030 + przyjęte)


|  |   |  |   |
|--|---|--|---|
|  | Wetna mineralna 035 (szkielet, docieplenia, ściana dom-garaż);<br>Wetna mineralna fasadowa (elewacja wentylowana bryły A, A1) |  | Membrana fasadowa wiatroizolacyjna UV-stabilna, czarna (sd = 0,02 m)   |
|  | — meander „UUU”   |  | Błoczek wapienno-piaskowy 12 cm, kl. 15 (ścianki działkowe, licowy w klatce); Błoczek wapienno-piaskowy (silikat) 18 cm, kl. 20, gr. 1, na zaprawie cienkowarstwowej — kratka ukośna 45°/135° |
|  | Styropian grafitowy EPS 031 (ETICS, NRO w systemie) —<br>zygzak „VVV”                                                         |  |   |

OZNACZENIA LINII

- elementy nad płaszczyzną cięcia (obryszy płyt, wsporników, brył wyższych kondygnacji)
- elementy poniżej płaszczyzny cięcia (widok z góry)
- osie konstrukcyjne; linia punktowa z pogrubionymi końcami — ślad przekroju


OBJAŚNIENIA I UWAGI

- Wymiary w cm (mm w indeksie górnym, np. 24° = 24,5 cm), rzędne w m względem ±0,000 = 101,650 m n.p.m. (PL-EVRF2007-NH).
- Rzuty: płaszczyzna cięcia +1,10 m nad posadzką kondygnacji. Linia kreskowa — elementy nad płaszczyzną cięcia (obryszy płyt i wsporników, brył wyższych kondygnacji, otwory w stropie nad, belki); linia cienka — elementy poniżej (widok).
- Otwory: licznik — szerokość, mianownik — wysokość w świetle muru, w nawiasie wysokość parapetu; symbol stolarki wg zestawienia stolarki.
- Numeracja pomieszczeń wg PN-B-01025 / PN-EN ISO 4157-2: <nr kondygnacji (parter = 1)>.<nr>; identyfikator w modelu: <kond>.<nr> (parter = 0).
- Drzwi: strona otwierania (lewe/prawe) wg modelu — patrząc od strony, w którą otwiera się skrzydło.
- Rysunek wygenerowany automatycznie z modelu /home/user/aihouse/model/budynek.yaml (wersja 1.0, 2026-09-25) — generatory lamela views.

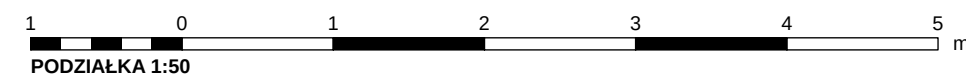

|   |        |                                         |             |                            |                             |
|---|--------|-----------------------------------------|-------------|----------------------------|-----------------------------|
| REW.   |        | OPIS ZMIANY                             |             | DATA                       |                             |
| 0   |        | Wydanie — rysunek wygenerowany z modelu |             |                            | 2026-09-25                  |
| PRACOWNIA PROJEKTOWA<br>PRACOWNIA PROJEKTOWA — nazwa do uzupełnienia                                                                                        |        |                                         |             | STADIUM<br>PB              | BRANŻA<br>ARCHITEKTURA (AR) |
| INWESTOR<br>(do uzupełnienia)   |        |                                         |             |                            |                             |
| OBIEKT / NAZWA ZAMIERZENIA BUDOWLANEGO<br>Budynek mieszkalny jednorodzinny wolnostojący „Dom LAMELA”                                                        |        |                                         |             |                            |                             |
| ADRES / LOKALIZACJA (NR DZIAŁKI, OBRĘB, JEDN. EWIDENCYJNA)<br>ul. Lipowa (fikcyjna), dz. nr ewid. 123/4, obręb 0005 Przykładowo, gm. Przykładowo (fikcyjna) |        |                                         |             |                            | KAT. OBIEKTU<br>I           |
| FUNKCJA   |        | IMIĘ I NAZWISKO                         |             | SPECJALNOŚĆ, NR UPRAWNIENI | DATA                        |
| Projektant   |        |                                         |             |                            |                             |
| Projektant (wsp.)   |        |                                         |             |                            |                             |
| Sprawdzający   |        |                                         |             |                            |                             |
| Opracował   |        |                                         |             |                            |                             |
| TYTUŁ RYSUNKU   |        |                                         |             |                            |                             |
| RZUT II PIĘTRA   |        |                                         |             |                            |                             |
| SKALA   | FORMAT | DATA WYDANIA                            | RODZAJ DOK. | NR RYSUNKU                 | ARKUSZ                      |
| 1:50   | A3x3   | 2026-09-25                              | rzut        | PB-AR-03                   | 3/10                        |
|   |        |                                         |             |                            | REW.                        |
|   |        |                                         |             |                            | 0                           |

PRZEKRÓJ A-A 1:50

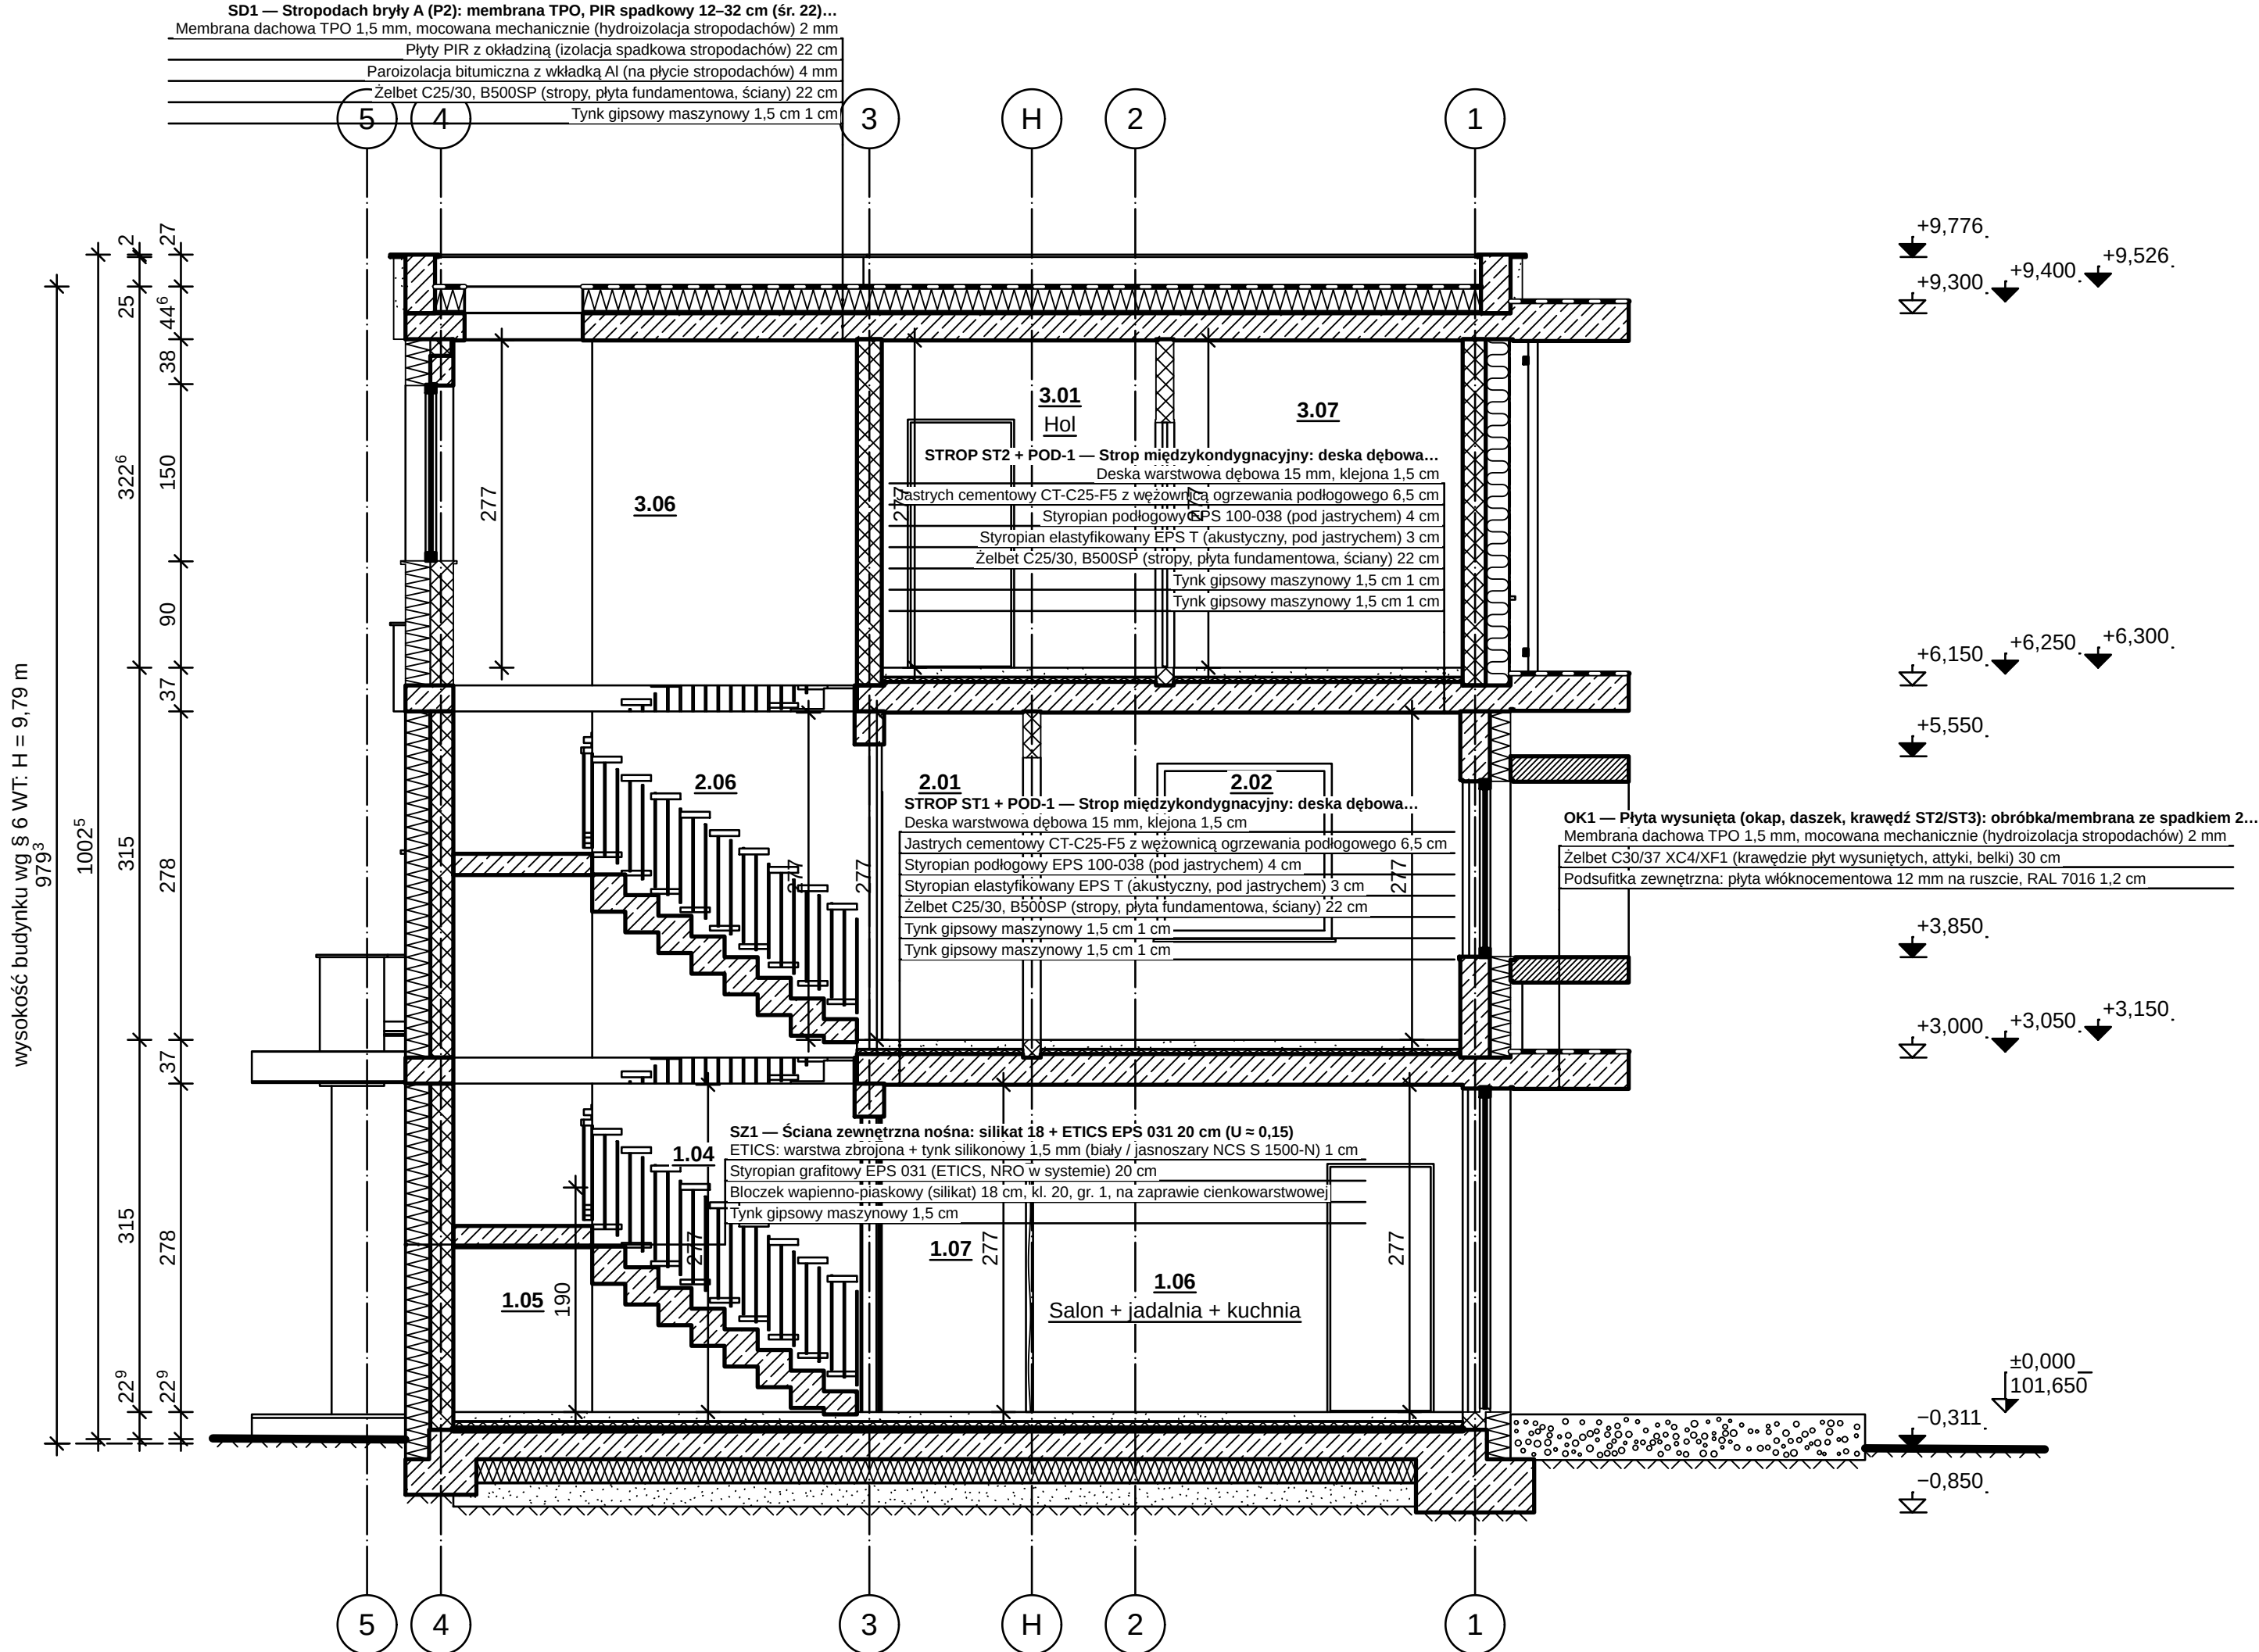


OZNACZENIA MATERIAŁÓW (PN-B-01030 + przyjęte)

- Lamele dębowe 30x60 mm (ekran komunikacji P0, h 2,10 m); Deska warstwowa dębowa 15 mm, klejona — przekrój wzdłuż włókien
- grunt rodzimy
- Wetna mineralna fasadowa (elewacja wentylowana bryły A, A1) — meander „UUU”
- Płyty PIR z okładziną (izolacja spadkowa stropodachów) — zygzak z okładziną
- Izolacja przeciwwilgociowa i przeciwdrońowa: membrana SBS 4 mm na płycie fundamentowej — linia bardzo gruba
- Membrana dachowa TPO 1.5 mm, mocowana mechanicznie (hydroizolacja stropodachów) — pas czarno-biały
- Styropian grafitowy EPS 031 (ETICS, NRO w systemie); Styropian podłogowy EPS 100-038 (pod jastrychem); Styropian elastyfikowany EPS T (akustyczny, pod jastrychem) — zygzak „VVV”
- Polistyren ekstrudowany XPS 300 (pod płytą fundamentową, cokół, izolacja obwodowa) — zygzak podwójny
- Jastrych cementowy CT-C25-F5 z węzownicą ogrzewania podłogowego — kropki
- Membrana fasadowa wiatroizolacyjna UV-stabilna, czarna (sd = 0,02 m)
- Błoczek wapienno-piaskowy 12 cm, kl. 15 (ścianki działowe, licowy w klatce); Błoczek wapienno-piaskowy (silikat) 18 cm, kl. 20, gr. 1, na zaprawie cienkowarstwowej — krata ukośna 45°/135°
- Folia PE 0,2 mm (warstwa rozdzielająca); Paroizolacja bitumiczna z wkładką Al (na płycie stropodachów) — linia kropkowa cienka 3/1 po ciepłej stronie
- Podsypka piaskowa zagęszczona (l<sub>s</sub> ≥ 0,98)
- Obróbki blacharskie (blacha powlekana); Stoiarka — profile aluminiowe, antracyt; Rama boksu C; ruszt stalowy ocynkowany w okładzinie z blachy aluminiowej RAL 7016 (pusia w środku); Stal malowana proszkowo (balustrady, rygle) — zaczerpnienie
- Tynk gipsowy maszynowy 1,5 cm; ETICS: warstwa zbrojona + tynk silikonowy 1,5 mm (biały / jasnoszary NCS S 1500-N) — kropki nieregularne
- Żelbet C25/30, B500SP (stropy, płyta fundamentowa, ściany); Żelbet C30/37 XC4/XF1 (krawędzie płyt wysuniętych, atyki, belki) — 45° na przemian ciągłe i przerywane
- Podbudowa nawierzchni (kruzywo)

OBJAŚNIENIA I UWAGI

- Wymiary w cm (mm w indeksie górnym, np. 24<sup>6</sup> = 24,5 cm), rzędne w m względem ±0,000 = 101,650 m n.p.m. (PL-EVRF2007-NH).
- Rzędne: trójkąt zaczerpiony — poziom wykończenia, niezaczerpiony — konstrukcji, w polowie zaczerpiony — poziom ±0,000 z rzędną bezwzględną (PN-B-01025).
- Wysokość budynku wg § 6 WT: od terenu przy najniższym wejściu (−0,267) do wierzchu stropodachu D1 (+9,526) — H = 9,79 m (bez atyki).
- Opisy warstw: kod i nazwa przegrody z modelu, materiały i grubości wg modelu (od góry / od lewej).
- Opisy warstw pominięte na rysunku (brak miejsca w podziale 1:50): POD-0 — układ warstw wg zestawienia przegród w części opisowej / przekroju 1:50.
- Rysunek wygenerowany automatycznie z modelu /home/user/aihouse/model/budynek.yaml (wersja 1.0, 2026-09-25) — generatory lamele.views.

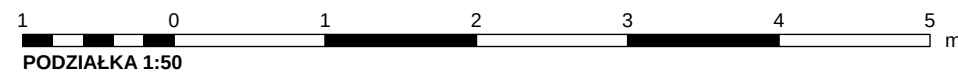

| REW.                                                                                          | OPIS ZMIANY                             | DATA                      |
|-----------------------------------------------------------------------------------------------|-----------------------------------------|---------------------------|
| 0                                                                                             | Wydanie — rysunek wygenerowany z modelu | 2026-09-25                |
| PRACOWNIA PROJEKTOWA                                                                          |                                         | STADIUM                   |
| PRACOWNIA PROJEKTOWA — nazwa do uzupełnienia                                                  |                                         | PB                        |
| adres pracowni do uzupełnienia                                                                |                                         | BRANZA                    |
| INWESTOR                                                                                      |                                         | ARCHITEKTURA (AR)         |
| (do uzupełnienia)                                                                             |                                         |                           |
| OBIEKT / NAZWA ZAMIERZENIA BUDOWLANEGO                                                        |                                         |                           |
| Budynek mieszkalny jednorodzinny wolnostojący „Dom LAMELA”                                    |                                         |                           |
| ADRES / LOKALIZACJA (NR DZIAŁKI, OBRĘB, JEDN. EWIDENCYJNA)                                    |                                         | KAT. OBIEKTU              |
| ul. Lipowa (fikcyjna), dz. nr ewid. 123/4, obręb 0005 Przykładowo, gm. Przykładowo (fikcyjna) |                                         | I                         |
| FUNKCJA                                                                                       | IMIĘ I NAZWISKO                         | SPECJALNOŚĆ, NR UPRAWNIEN |
| Projektant                                                                                    |                                         | DATA                      |
| Projektant (wsp.)                                                                             |                                         | PODPIS                    |
| Sprawdzający                                                                                  |                                         |                           |
| Opracował                                                                                     |                                         |                           |
| TYTUŁ RYSUNKU                                                                                 |                                         |                           |
| PRZEKRÓJ A-A                                                                                  |                                         |                           |
| SKALA                                                                                         | FORMAT                                  | DATA WYDANIA              |
| 1:50                                                                                          | A3x3                                    | 2026-09-25                |
| RODZAJ DOK.                                                                                   | NR RYSUNKU                              | ARKUSZ                    |
| przekrój                                                                                      | PB-AR-05                                | 5/10                      |
| REW.                                                                                          |                                         | 0                         |

PRZEKRÓJ B-B 1:50

wysokość budynku wg § 6 WT: H = 9,79 m

odcinek kontynuacji 100 mm (wydruk 1:1)

SD1 — Stropodach bryły A (P2): membrana TPO, PIR spadkowy 12–32 cm (śr. 22)...

Membrana dachowa TPO 1,5 mm, mocowana mechanicznie (hydroizolacja stropodachów) 2 mm

Płyty PIR z okładziną (izolacja spadkowa stropodachów) 22 cm

Paroizolacja bitumiczna z wkładką Al (na płycie stropodachów) 4 mm

Żelbet C25/30, B500SP (stropy, płyta fundamentowa, ściany) 22 cm

Tynk gipsowy maszynowy 1,5 cm 1 cm

A'

A

B

C

M

D

D'

E

P

F

3.02  
Sypialnia rodziców

STROP ST2 + POD-1 — Strop międzykondygnacyjny: deska dębowa...

Deska warstwowa dębowa 15 mm, klejona 1,5 cm

Jasnych cementowy CT-C25-F5 z węzownicą ogrzewania podłogowego 6,5 cm

Styropian podłogowy EPS 100-038 (pod jasnym) 4 cm

Styropian elastyczny EPS T (akustyczny, pod jasnym) 3 cm

Żelbet C25/30, B500SP (stropy, płyta fundamentowa, ściany) 22 cm

Tynk gipsowy maszynowy 1,5 cm 1 cm

Tynk gipsowy maszynowy 1,5 cm 1 cm

3.03

3.01

Hol

3.05  
Gabinet / pokój

2.02 STROP ST1 + POD-1 — Strop międzykondygnacyjny: deska dębowa...

Deska warstwowa dębowa 15 mm, klejona 1,5 cm

Jasnych cementowy CT-C25-F5 z węzownicą ogrzewania podłogowego 6,5 cm

Styropian podłogowy EPS 100-038 (pod jasnym) 4 cm

Styropian elastyczny EPS T (akustyczny, pod jasnym) 3 cm

Żelbet C25/30, B500SP (stropy, płyta fundamentowa, ściany) 22 cm

Tynk gipsowy maszynowy 1,5 cm 1 cm

Tynk gipsowy maszynowy 1,5 cm 1 cm

2.03  
Pokój dziecka 1

1.06

POD-0 — Podłoga na płycie fundamentowej (P0): deska/gres, jasnych z ogrzewaniem podł., EPS...

Deska warstwowa dębowa 15 mm, klejona 1,5 cm

Jasnych cementowy CT-C25-F5 z węzownicą ogrzewania podłogowego 6,5 cm

Styropian podłogowy EPS 100-038 (pod jasnym) 6,5 cm

Izolacja przeciwwilgociowa i przeciwradowna: membrana SBS 4 mm na płycie fundamentowej 5 mm

Żelbet C25/30, B500SP (stropy, płyta fundamentowa, ściany) 25 cm

Polistyren ekstrudowany XPS 300 (pod płytą fundamentową, cokół, izolacja obwodowa) 20 cm

Folia PE 0,2 mm (warstwa rozdzielająca)

Podsyпка piaskowa zagęszczona (l<sub>s</sub> ≥ 0,98) 20 cm

A'

A

B

C

M

D

D'

E

P

F

DZ1 — Dach zielony ekstensywny NIEUŻYTKOWY nad garażem (pom....)

Substrat ekstensywny 8 cm z matą rozchodnikową (sedum)

Geowłókna filtracyjna PP 150 g/m² 2 mm

Matą drenażowo-retencyjną HDPE 25 mm (dach zielony) 2,5 cm

Włókna ochronna PP 300 g/m² 4 mm

Bariera przeciwwodna PE-HD 0,5 mm (PN-EN 13948)

Hydroizolacja 2 × papa SBS (podkładowa + wierzchniego krycia, dach zielony) 9,5 mm

Płyty PIR z okładziną (izolacja spadkowa stropodachów) 18 cm

Paroizolacja bitumiczna z wkładką Al (na płycie stropodachów) 4 mm

Żelbet C25/30, B500SP (stropy, płyta fundamentowa, ściany) 24 cm

SZ1 — Ściana zewnętrzna nośna: silikat 18 + ETICS EPS 031 20 cm (U = 0,15)

Tynk gipsowy maszynowy 1,5 cm

Błoczek wapniowo-piaskowy (silikat) 18 cm, kl. 20, gr. 1, na zaprawie cienkowarstwowej

Styropian grafitowy EPS 031 (ETICS, NRO w systemie) 20 cm

ETICS: warstwa zbrojona + tynk silikonowy 1,5 mm (biały / jasnoszary NCS S 1500-N) 1 cm

1.13

±0,000  
101,650

-0,206

-0,700

OZNACZENIA MATERIAŁÓW (PN-B-01030 + przyjęte)

- grunt rodzimy
- Substrat ekstensywny 8 cm z matą rozchodnikową (sedum)
- Włna mineralna 035 (szkielet, docieplenia, ściana dom-garaż); Włna mineralna fasadowa (elewacja wentylowana bryły A, A1) — meander „UUU”
- Płyty PIR z okładziną (izolacja spadkowa stropodachów) — zygzak z okładzinami
- Izolacja przeciwwilgociowa i przeciwradowna: membrana SBS 4 mm na płycie fundamentowej — linia bardzo gruba
- Membrana dachowa TPO 1,5 mm, mocowana mechanicznie (hydroizolacja stropodachów); Hydroizolacja 2 × papa SBS (podkładowa + wierzchniego krycia, dach zielony) — pas
- Styropian grafitowy EPS 031 (ETICS, NRO w systemie); Styropian podłogowy EPS 100-038 (pod jasnym); Styropian elastyczny EPS T (akustyczny, pod jasnym) — zygzak „VVV”
- Polistyren ekstrudowany XPS 300 (pod płytą fundamentową, cokół, izolacja obwodowa) — zygzak podwójny
- Jasnych cementowy CT-C25-F5 z węzownicą ogrzewania podłogowego — kropki
- Membrana fasadowa wiatroizolacyjna UV-stabilna, czarna (sd = 0,02 m)
- Błoczek wapniowo-piaskowy 12 cm, kl. 15 (ścianki działowe, licowy w klatce); Błoczek wapniowo-piaskowy (silikat) 18 cm, kl. 20, gr. 1, na zaprawie cienkowarstwowej — krętka ukośna 45°/135°
- Folia PE 0,2 mm (warstwa rozdzielająca); Paroizolacja bitumiczna z wkładką Al (na płycie stropodachów) — linia kreskowa cienka 3/1 po ciepłej stronie
- Podsyпка piaskowa zagęszczona (l<sub>s</sub> ≥ 0,98)
- Obróbki blacharskie (blacha powlekana); Stolaria — profile aluminiowe, antracyt; Stal malowana proszkowo (balustrady, rygle) — zaczerpienie
- Tynk cementowo-wapniowy 1,5 cm (garaż, pom. techniczne); Tynk gipsowy maszynowy 1,5 cm; ETICS: warstwa zbrojona + tynk silikonowy 1,5 mm (biały / jasnoszary NCS S 1500-N) — kropki nieregularne
- Żelbet C25/30, B500SP (stropy, płyta fundamentowa, ściany); Żelbet C30/37 XC4/XF1 (krawędzie płyt wysuniętych, atyki, belki) — 45° na przemian ciagle i przerywane
- Podbudowa nawierzchni (kruzywo)


OBJAŚNIENIA I UWAGI

1. Wymiary w cm (mm w indeksie górnym, np. 24<sup>6</sup> = 24,5 cm), rzędne w m względem ±0,000 = 101,650 m n.p.m. (PL-EVRF2007-NH).
2. Rzędne: trójkąt zaczerpienie — poziom wykończenia, niezaczerpienie — konstrukcji, w pokłowie zaczerpienie — poziom ±0,000 z rzędną bezwzględną (PN-B-01025).
3. Wysokość budynku wg § 6 WT: od terenu przy najniższym wejściu (-0,267) do wierzchu stropodachu D1 (+9,526) — H = 9,79 m (bez atyki).
4. Opisy warstw: kod i nazwa przegrody z modelu, materiały i grubości wg modelu (od góry / od lewej).
5. Opisy warstw pominęte na rysunku (brak miejsca w podziale 1:50): STROP ST22 + POD-1, OK1 — układ warstw wg zestawienia przegród w części opisowej / przekroju 1:50.
6. Rysunek wygenerowany automatycznie z modelu /home/user/aihouse/model/budynek.yaml (wersja 1.0, 2026-09-25) — generatory lamela.views.

1 0 1 2 3 4 5 m


PODZIAŁKA 1:50

| REW.                                                                                          |                 | OPIS ZMIANY                             | DATA        |                   |
|-----------------------------------------------------------------------------------------------|-----------------|-----------------------------------------|-------------|-------------------|
| 0                                                                                             |                 | Wydanie — rysunek wygenerowany z modelu | 2026-09-25  |                   |
| PRACOWNIA PROJEKTOWA                                                                          |                 |                                         | STADIUM     | BRANZA            |
| PRACOWNIA PROJEKTOWA — nazwa do uzupełnienia                                                  |                 |                                         | PB          | ARCHITEKTURA (AR) |
| adres pracowni do uzupełnienia                                                                |                 |                                         |             |                   |
| INWESTOR                                                                                      |                 |                                         |             |                   |
| (do uzupełnienia)                                                                             |                 |                                         |             |                   |
| OBIEKT / NAZWA ZAMIERZENIA BUDOWLANEGO                                                        |                 |                                         |             |                   |
| Budynek mieszkalny jednorodzinny wolnostojący „Dom LAMELA”                                    |                 |                                         |             |                   |
| ADRES / LOKALIZACJA (NR DZIAŁKI, OBRĘB, JEDN. EWIDENCYJNA)                                    |                 |                                         |             | KAT. OBIEKTU      |
| ul. Lipowa (fikcyjna), dz. nr ewid. 123/4, obręb 0005 Przykładowo, gm. Przykładowo (fikcyjna) |                 |                                         |             |                   |
| FUNKCJA                                                                                       | IMIĘ I NAZWISKO | SPECJALNOŚĆ, NR UPRAWNIEN               | DATA        | PODPIS            |
| Projektant                                                                                    |                 |                                         |             |                   |
| Projektant (wsp.)                                                                             |                 |                                         |             |                   |
| Sprawdzający                                                                                  |                 |                                         |             |                   |
| Opracował                                                                                     |                 |                                         |             |                   |
| TYTUŁ RYSUNKU                                                                                 |                 |                                         |             |                   |
| PRZEKRÓJ B-B                                                                                  |                 |                                         |             |                   |
| SKALA                                                                                         | FORMAT          | DATA WYDANIA                            | RODZAJ DOK. | NR RYSUNKU        |
| 1:50                                                                                          | A3×3            | 2026-09-25                              | przekrój    | PB-AR-06          |
| ARKUSZ                                                                                        |                 | REW.                                    |             |                   |
| 6/10                                                                                          |                 |                                         |             | 0                 |

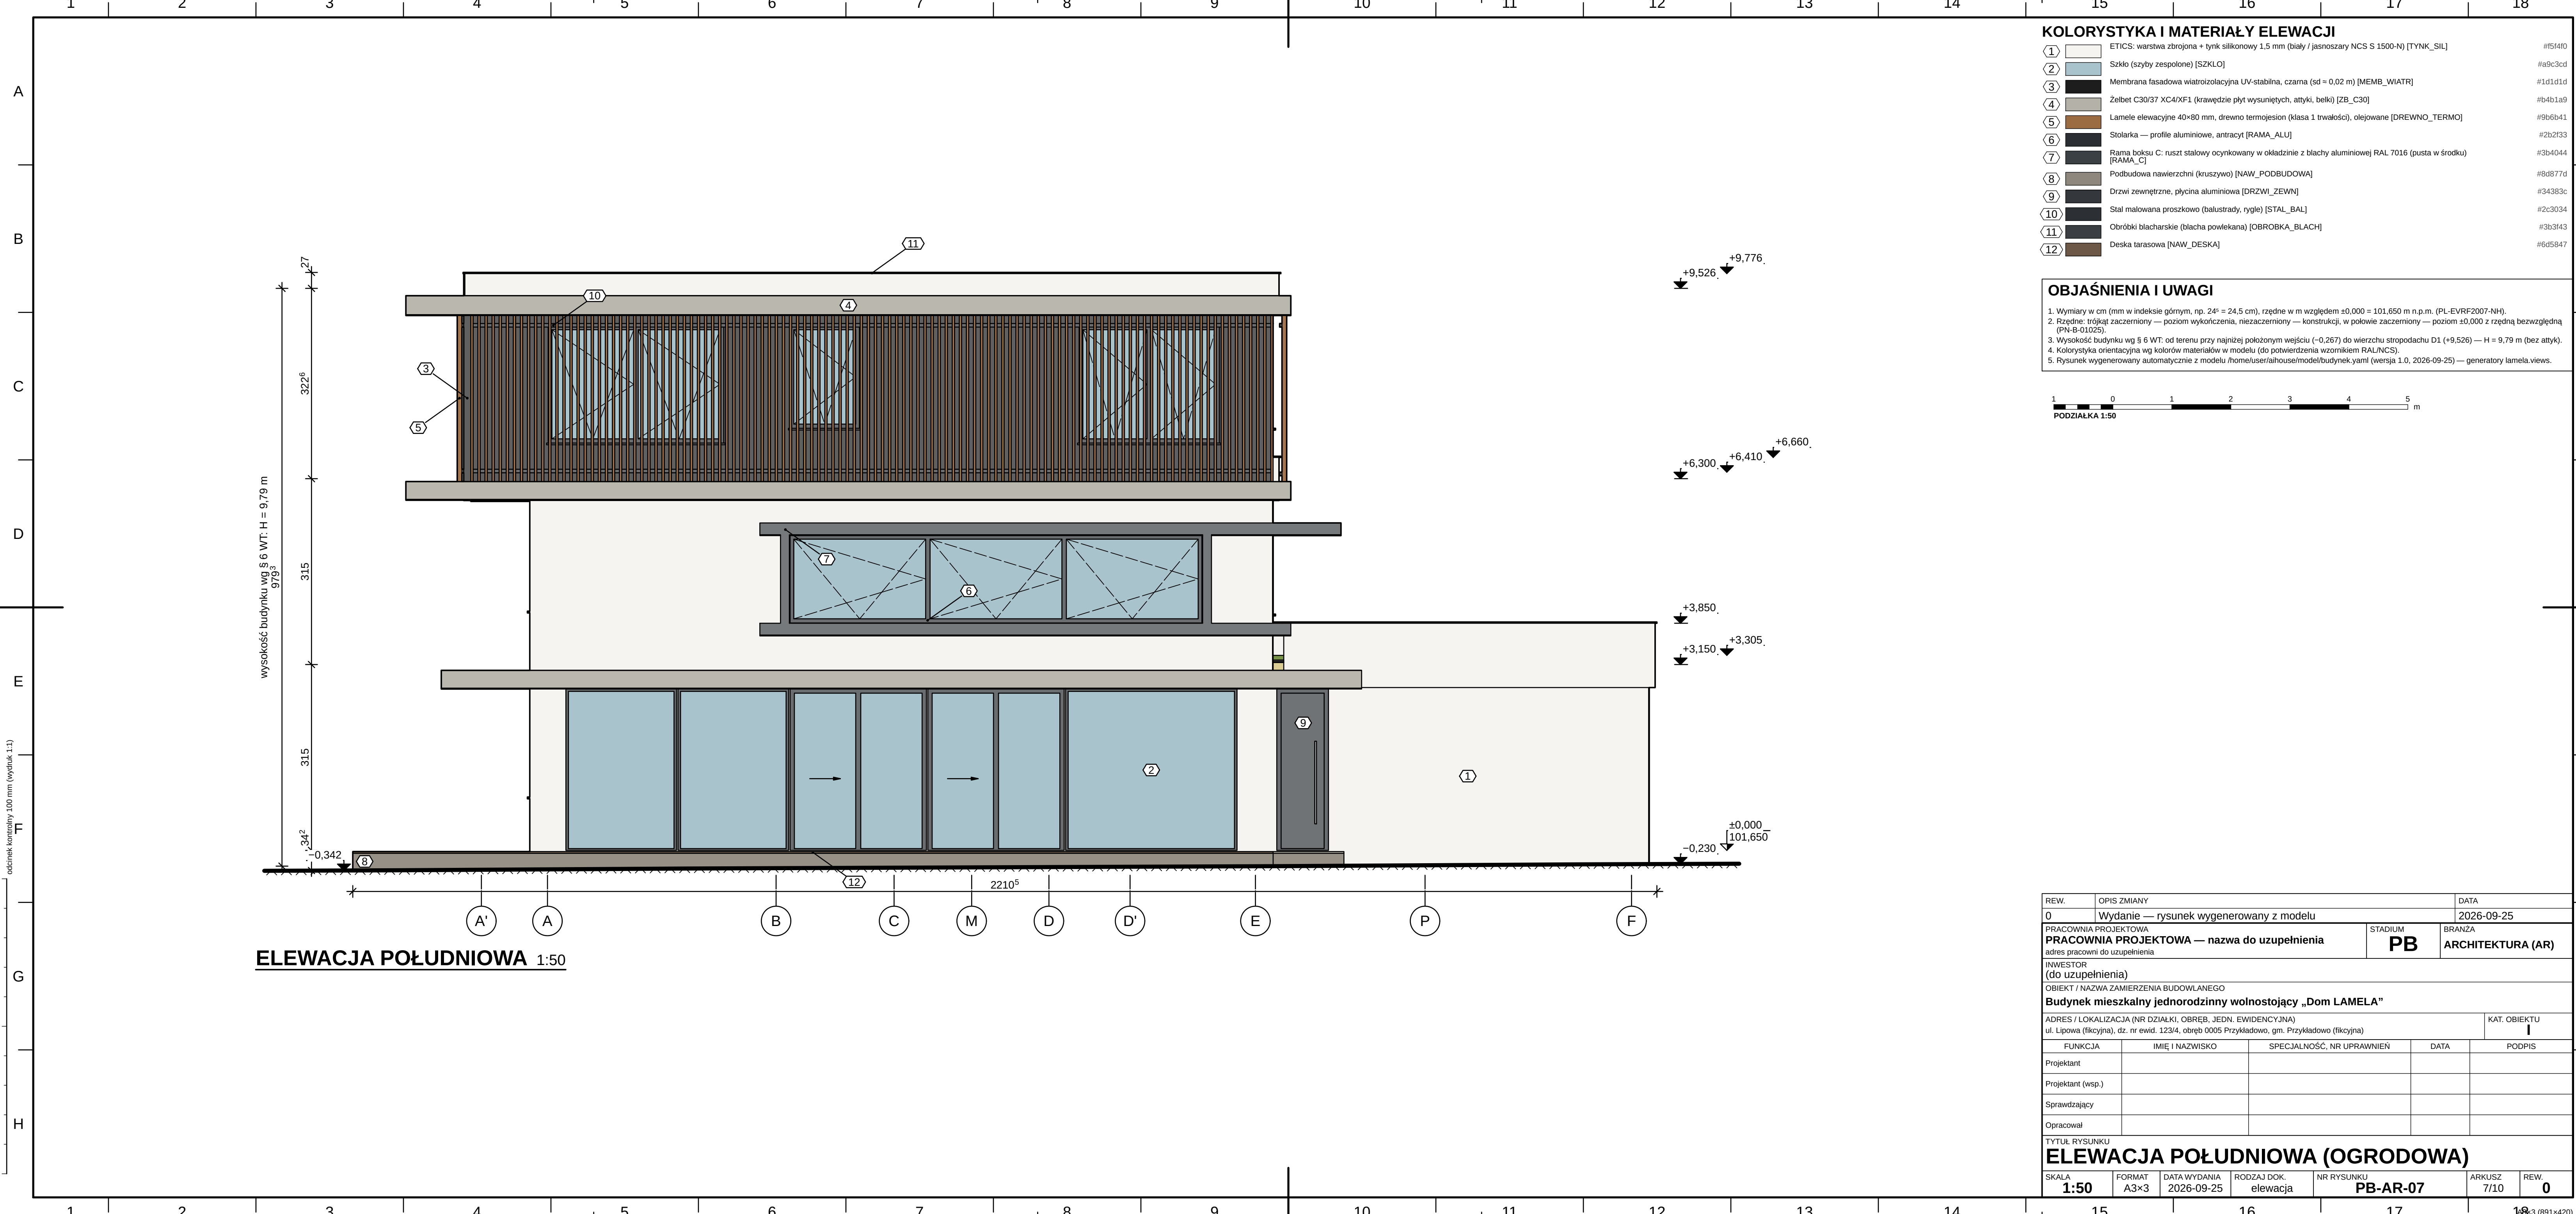


| KOLORYSTYKA I MATERIAŁY ELEWACJI |   |         |
|----------------------------------|---|---------|
| 1                                | ETICS: warstwa zbrojona + tynk silikonowy 1,5 mm (biały / jasnoszary NCS S 1500-N) [TYNK_SIL]              | #f5f4f0 |
| 2                                | Szko (szyby zespolone) [SZKLO]                                                                             | #a9c3cd |
| 3                                | Membrana fasadowa wiatroizolacyjna UV-stabilna, czarna (sd = 0,02 m) [MEMB_WIATR]                          | #1d1d1d |
| 4                                | Żelbet C30/37 XC4/XF1 (krawędzie płyt wysuniętych, attyki, belki) [ZB_C30]                                 | #b4b1a9 |
| 5                                | Lamele elewacyjne 40×80 mm, drewno termojesion (klasa 1 trwałości), olejowane [DREWNO_TERMO]               | #9b6b41 |
| 6                                | Stolarka — profile aluminiowe, antracyt [RAMA_ALU]                                                         | #2b2f33 |
| 7                                | Rama boku C: ruszt stalowy ocynkowany w okładzinie z blachy aluminiowej RAL 7016 (pusta w środku) [RAMA_C] | #3b4044 |
| 8                                | Podbudowa nawierzchni (kruszywo) [NAW_PODBUDOWA]                                                           | #8d877d |
| 9                                | Drzwi zewnętrzne, płycina aluminiowa [DRZWI_ZEWN]                                                          | #34383c |
| 10                               | Stal malowana proszkowo (balustrady, rygle) [STAL_BAL]                                                     | #2c3034 |
| 11                               | Obróbki blacharskie (blacha powlekana) [OBROBKA_BLACH]                                                     | #3b3f43 |
| 12                               | Deska tarasowa [NAW_DESKA]                                                                                 | #6d5847 |

| OBJAŚNIENIA I UWAGI   |  |
|---|--|
| 1. Wymiary w cm (mm w indeksie górnym, np. 24 <sup>2</sup> = 24,5 cm), rzędne w m względem ±0,000 = 101,650 m n.p.m. (PL-EVRF2007-NH).                      |  |
| 2. Rzędne: trójkąt zaczerpiony — poziom wykończenia, niezaczerpiony — konstrukcji, w polowie zaczerpiony — poziom ±0,000 z rzędną bezwzględną (PN-B-01025). |  |
| 3. Wysokość budynku wg § 6 WT: od terenu przy najniższym wejściu (-0,267) do wierzchu stropodachu D1 (+9,526) — H = 9,79 m (bez attyki).                    |  |
| 4. Kolorystyka orientacyjna wg kolorów materiałów w modelu (do potwierdzenia wzornikiem RAL/NCS).                                                           |  |
| 5. Rysunek wygenerowany automatycznie z modelu /home/user/aihouse/model/budynek.yaml (wersja 1.0, 2026-09-25) — generatory lamela.views.                    |  |

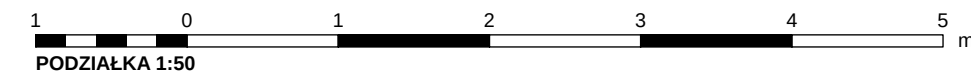

|   |                                         |                            |                         |                             |                |           |
|---|-----------------------------------------|----------------------------|-------------------------|-----------------------------|----------------|-----------|
| REW.   | OPIS ZMIANY                             |                            |                         | DATA                        |                |           |
| 0   | Wydanie — rysunek wygenerowany z modelu |                            |                         | 2026-09-25                  |                |           |
| PRACOWNIA PROJEKTOWA<br>PRACOWNIA PROJEKTOWA — nazwa do uzupełnienia<br>adres pracowni do uzupełnienia                                                      |                                         |                            | STADIUM<br>PB           | BRANŻA<br>ARCHITEKTURA (AR) |                |           |
| INWESTOR<br>(do uzupełnienia)   |                                         |                            |                         |                             |                |           |
| OBIEKT / NAZWA ZAMIERZENIA BUDOWLANEGO<br>Budynek mieszkalny jednorodzinny wolnostojący „Dom LAMELA”                                                        |                                         |                            |                         |                             |                |           |
| ADRES / LOKALIZACJA (NR DZIAŁKI, OBREB, JEDN. EWIDENCYJNA)<br>ul. Lipowa (fikcyjna), dz. nr ewid. 123/4, obręb 0005 Przykładowo, gm. Przykładowo (fikcyjna) |                                         |                            |                         | KAT. OBIEKTU<br>I           |                |           |
| FUNKCJA   | IMIĘ I NAZWISKO                         | SPECJALNOŚĆ, NR UPRAWNIENI | DATA                    | PODPIS                      |                |           |
| Projektant   |                                         |                            |                         |                             |                |           |
| Projektant (wsp.)   |                                         |                            |                         |                             |                |           |
| Sprawdzający   |                                         |                            |                         |                             |                |           |
| Opracował   |                                         |                            |                         |                             |                |           |
| TYTUŁ RYSUNKU<br>ELEWACJA POŁUDNIOWA (OGRODOWA)   |                                         |                            |                         |                             |                |           |
| SKALA<br>1:50   | FORMAT<br>A3×3                          | DATA WYDANIA<br>2026-09-25 | RODZAJ DOK.<br>elewacja | NR RYSUNKU<br>PB-AR-07      | ARKUSZ<br>7/10 | REW.<br>0 |

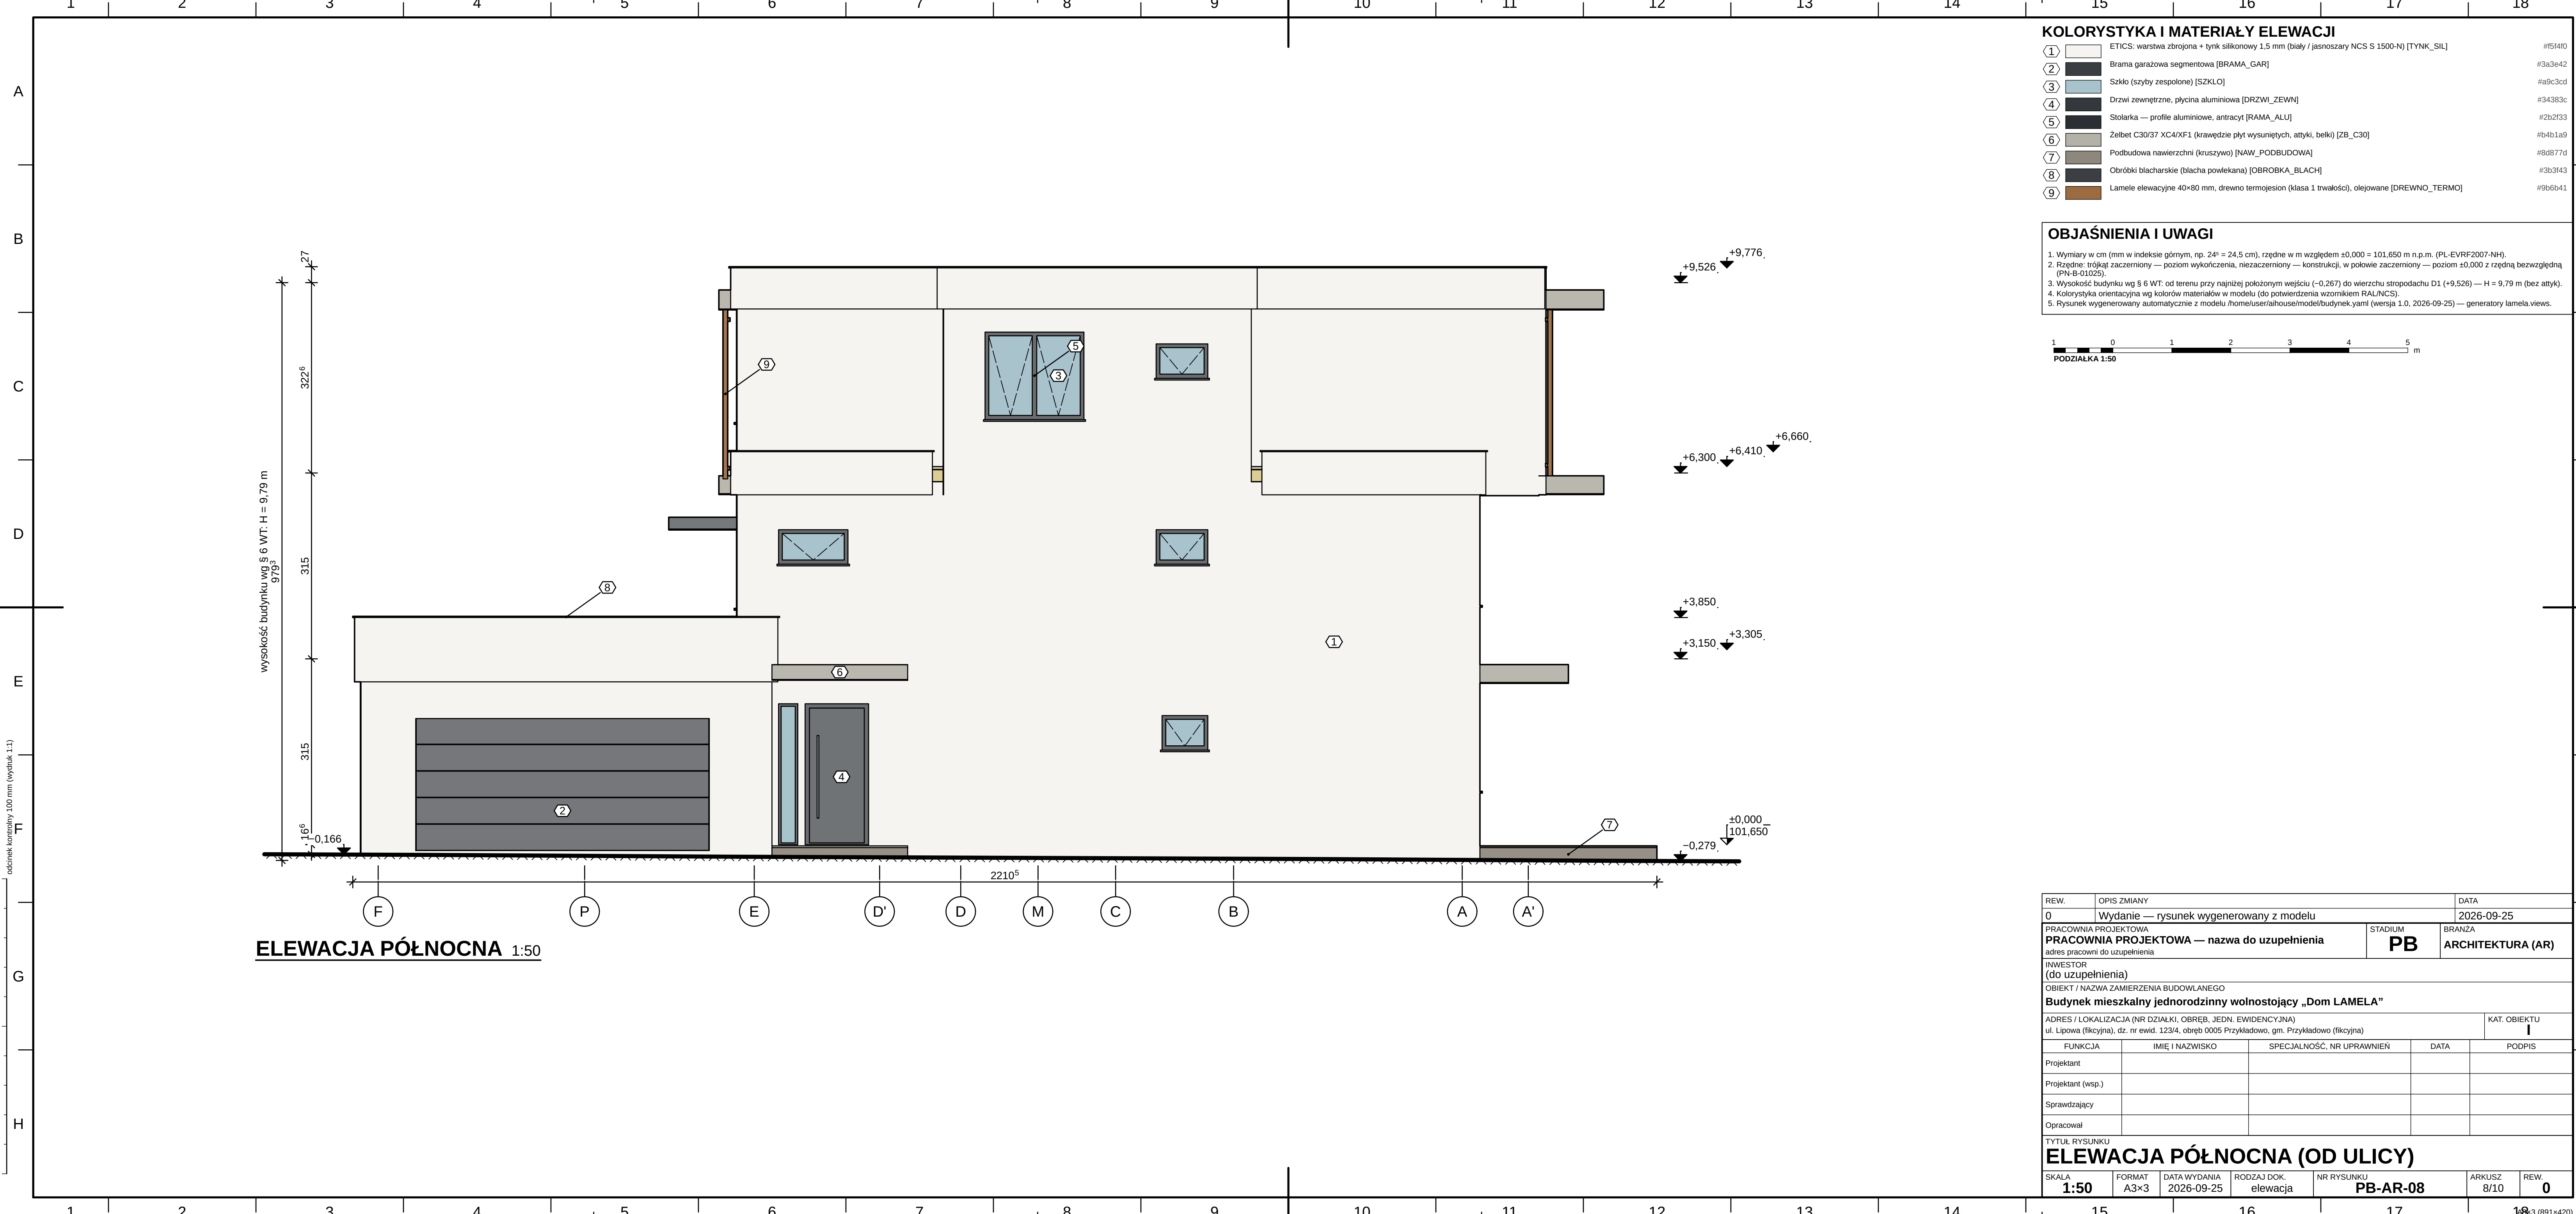


### KOLORYSTYKA I MATERIAŁY ELEWACJI

|   |                                                                                               |         |
|---|-----------------------------------------------------------------------------------------------|---------|
| ① | ETICS: warstwa zbrojona + tynk silikonowy 1.5 mm (biały / jasnoszary NCS S 1500-N) [TYNK_SIL] | #f5f4f0 |
| ② | Brama garażowa segmentowa [BRAMA_GAR]                                                         | #3a3e42 |
| ③ | Szkle (szyby zespolone) [SZKLO]                                                               | #a9c3cd |
| ④ | Drzwi zewnętrzne, płycina aluminiowa [DRZWI_ZEWN]                                             | #34383c |
| ⑤ | Stolarka — profile aluminiowe, antracyt [RAMA_ALU]                                            | #2b2f33 |
| ⑥ | Żelbet C30/37 XC4/XF1 (krawędzie płyt wysuniętych, attyki, belki) [ZB_C30]                    | #b4b1a9 |
| ⑦ | Podbudowa nawierzchni (kruszywo) [NAW_PODBUDOWA]                                              | #8d877d |
| ⑧ | Otróbki blacharskie (blacha powlekana) [OBROBKA_BLACH]                                        | #3b3f43 |
| ⑨ | Lamele elewacyjne 40×80 mm, drewno termojesion (klasa 1 trwałości), olejowane [DREWNO_TERMO]  | #9b6b41 |

### OBJAŚNIENIA I UWAGI

- Wymiary w cm (mm w indeksie górnym, np. 24<sup>6</sup> = 24,5 cm), rzędne w m względem ±0.000 = 101,650 m n.p.m. (PL-EVRF2007-NH).
- Rzędne: trójkąt zaczerpiony — poziom wykończenia, niezaczerpiony — konstrukcji, w połowie zaczerpiony — poziom ±0.000 z rzędną bezwzględną (PN-B-01025).
- Wysokość budynku wg § 6 WT: od terenu przy najniżej położonym wejściu (−0,267) do wierzchu stropodachu D1 (+9,526) — H = 9,79 m (bez attyki).
- Kolorystyka orientacyjna wg kolorów materiałów w modelu (do potwierdzenia wzornikiem RALNCS).
- Rysunek wygenerowany automatycznie z modelu /home/user/ai/house/model/budynek.yaml (wersja 1.0, 2026-09-25) — generatory lamela.views.

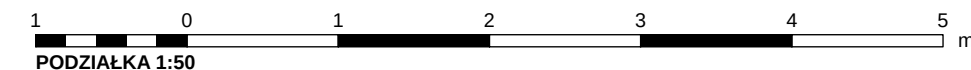

|   |                                         |                            |                            |                                              |                |           |
|---|-----------------------------------------|----------------------------|----------------------------|----------------------------------------------|----------------|-----------|
| REW.   | OPIS ZMIANY                             |                            |                            | DATA                                         |                |           |
| 0   | Wydanie — rysunek wygenerowany z modelu |                            |                            | 2026-09-25                                   |                |           |
| PRACOWNIA PROJEKTOWA<br>PRACOWNIA PROJEKTOWA — nazwa do uzupełnienia<br>adres pracowni do uzupełnienia                                                      |                                         |                            |                            | STADIUM<br>PB<br>BRANŻA<br>ARCHITEKTURA (AR) |                |           |
| INWESTOR<br>(do uzupełnienia)   |                                         |                            |                            |                                              |                |           |
| OBIEKT / NAZWA ZAMIERZENIA BUDOWLANEGO   |                                         |                            |                            |                                              |                |           |
| Budynek mieszkalny jednorodzinny wolnostojący „Dom LAMELA”                                                                                                  |                                         |                            |                            |                                              |                |           |
| ADRES / LOKALIZACJA (NR DZIAŁKI, OBREB, JEDN. EWIDENCYJNA)<br>ul. Lipowa (fikcyjna), dz. nr ewid. 123/4, obręb 0005 Przykładowo, gm. Przykładowo (fikcyjna) |                                         |                            |                            | KAT. OBIEKTU<br>I                            |                |           |
| FUNKCJA   | IMIĘ I NAZWISKO                         |                            | SPECJALNOŚĆ, NR UPRAWNIENI | DATA                                         | PODPIS         |           |
| Projektant   |                                         |                            |                            |                                              |                |           |
| Projektant (wsp.)   |                                         |                            |                            |                                              |                |           |
| Sprawdzający   |                                         |                            |                            |                                              |                |           |
| Opracował   |                                         |                            |                            |                                              |                |           |
| TYTUŁ RYSUNKU   |                                         |                            |                            |                                              |                |           |
| ELEWACJA PÓŁNOCNA (OD ULICY)   |                                         |                            |                            |                                              |                |           |
| SKALA<br>1:50   | FORMAT<br>A3×3                          | DATA WYDANIA<br>2026-09-25 | RODZAJ DOK.<br>elewacja    | NR RYSUNKU<br>PB-AR-08                       | ARKUSZ<br>8/10 | REW.<br>0 |

