




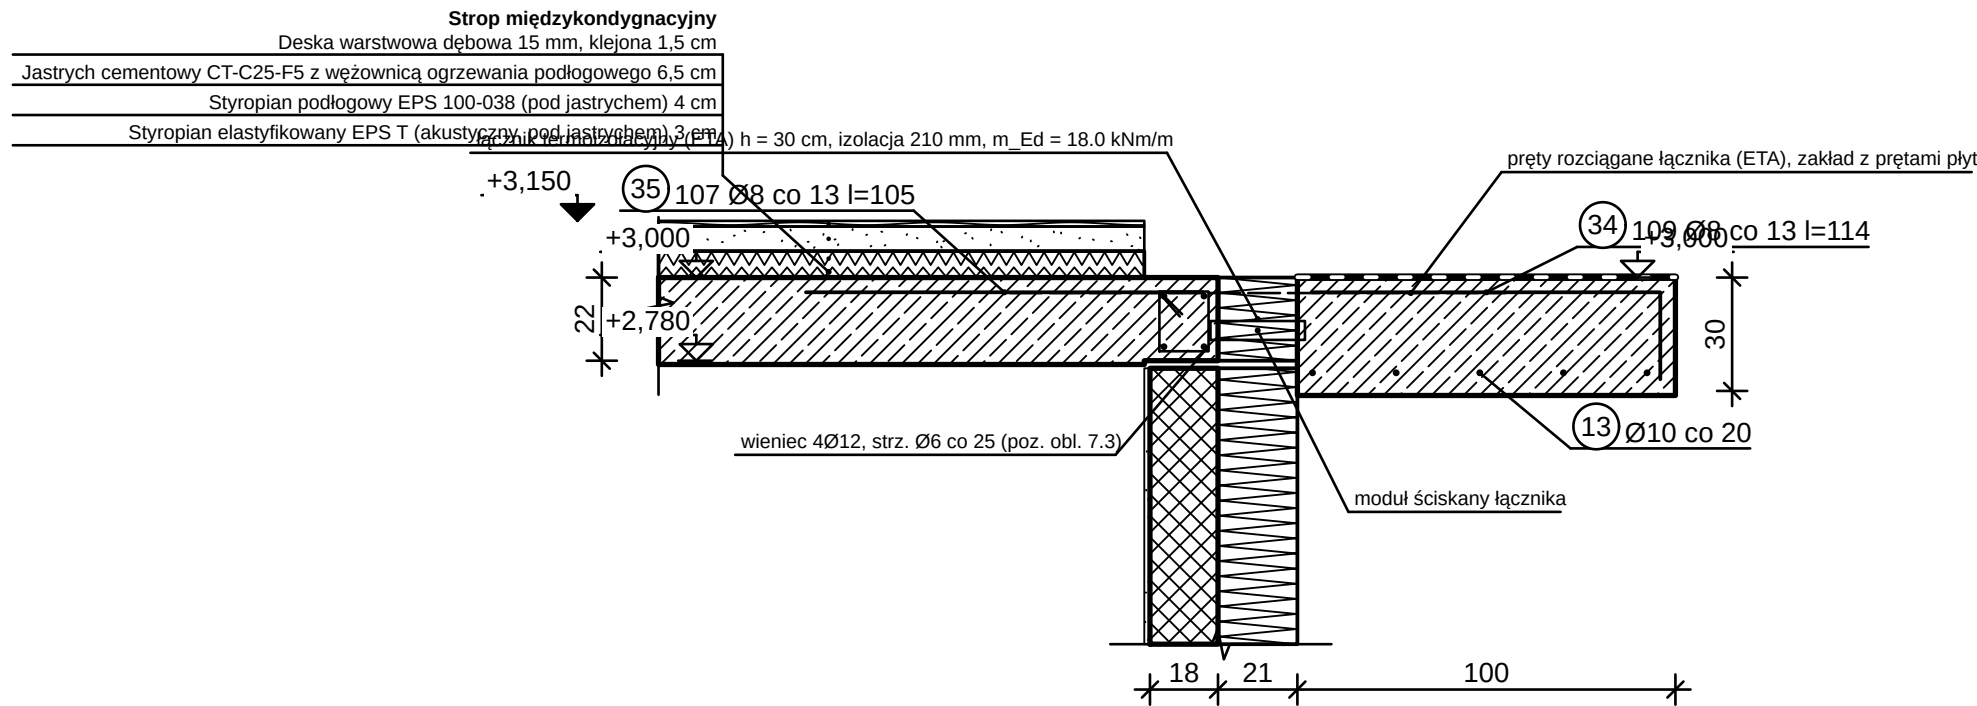

WĘZŁ WSPORNIKA PL-E — ŁĄCZNIK TERMOIZOLACYJNY 1:20

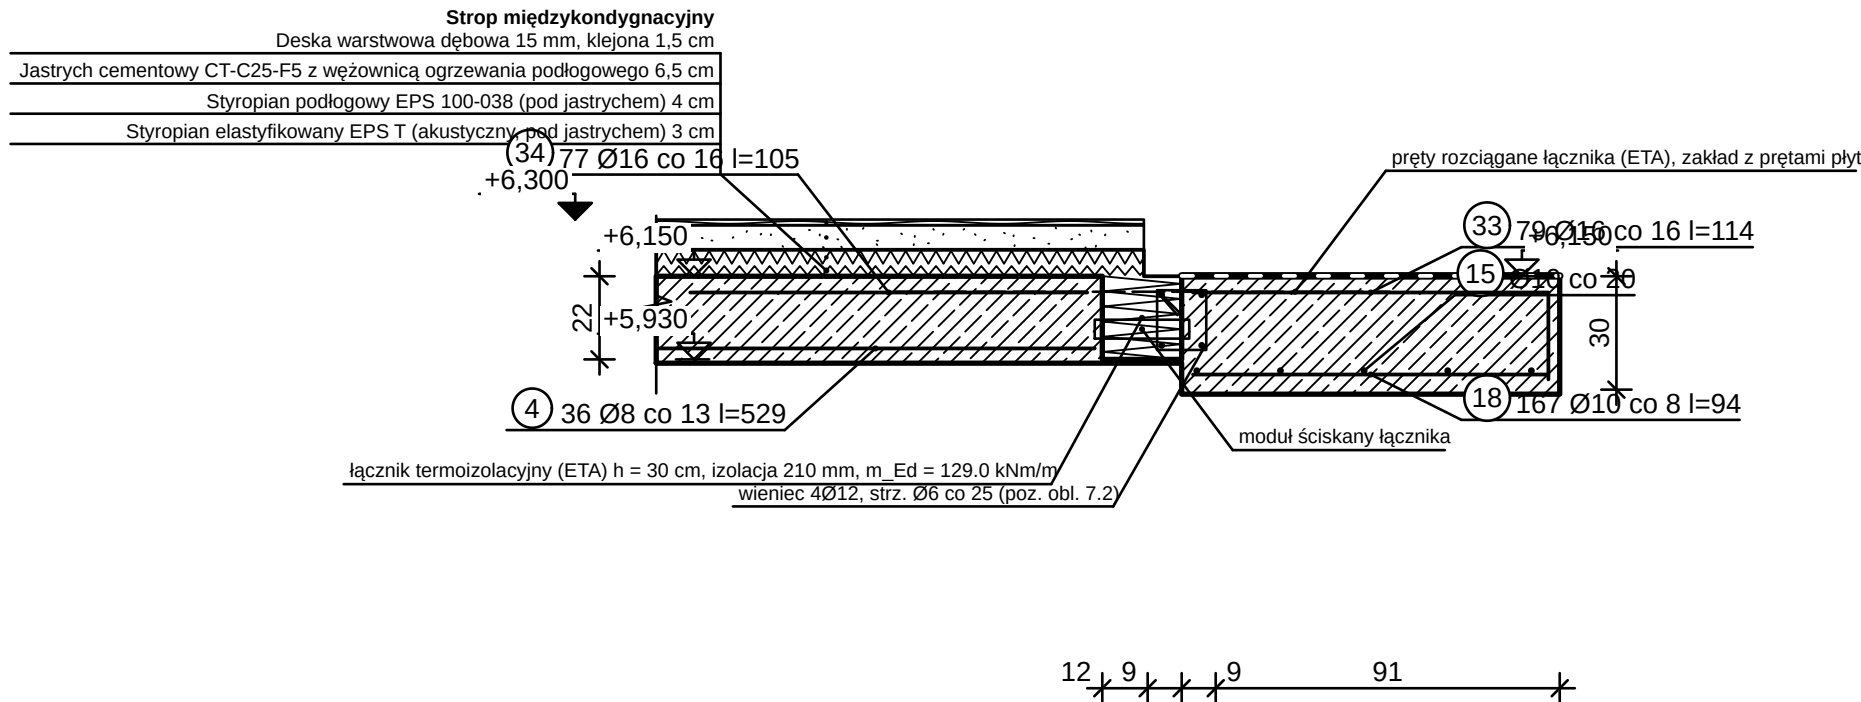


WĘZŁ WSPORNIKA PL-2 — ŁĄCZNIK TERMOIZOLACYJNY 1:20

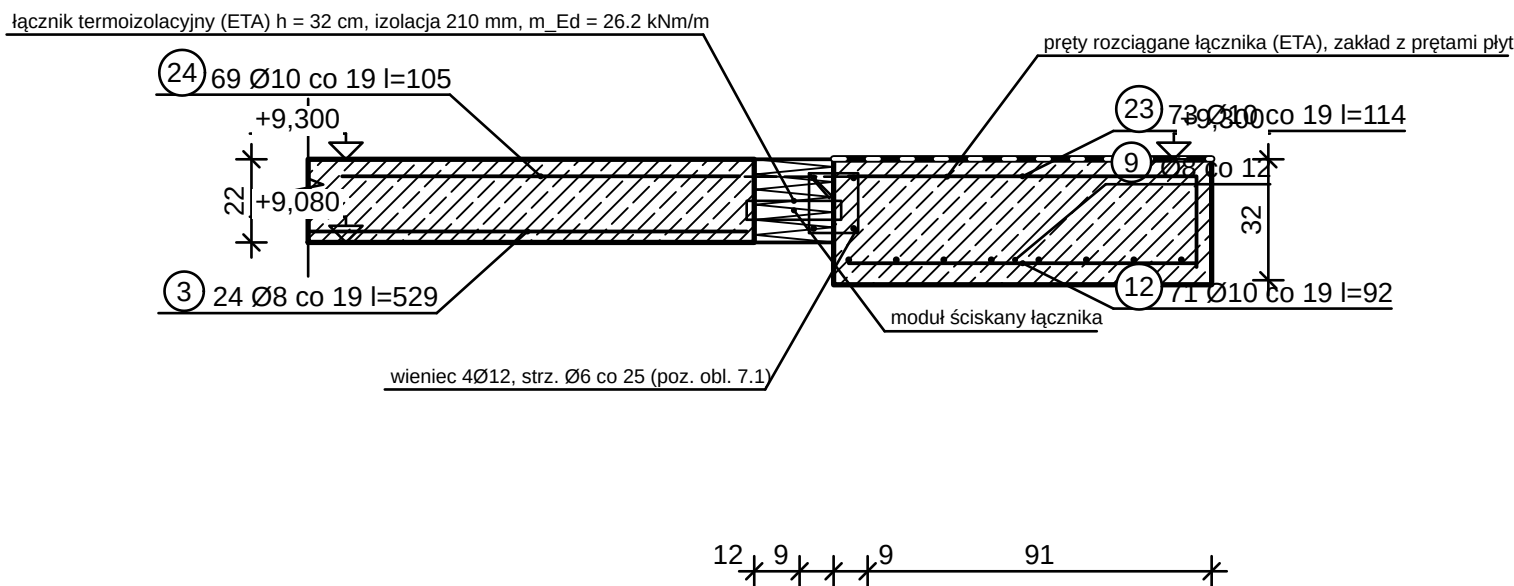

WĘZŁ WSPORNIKA PL-3 — ŁĄCZNIK TERMOIZOLACYJNY 1:20

OBJAŚNIENIA I UWAGI

- Wymiary w cm (mm w indeksie górnym, np. 24⁵ = 24,5 cm), rzędne w m względem ±0,000 = 101,650 m n.p.m. (PL-EVRF2007-NH).
- Węzły stropów: warstwy wg przegród z modelu; zbrojenie — numery pozycji jak na arkuszach zbrojenia płyt poziomym (warstwa dolna/górna); wieniec wg pozycji obliczeniowej wieńców.
- Otuliny (c_{nom}) — wg klasy ekspozycji elementów (PN-EN 1992-1-1 tabl. 4.4N + NA, Δc_{dev} = 10 mm); podkładki dystansowe wg PN-EN 13670.
- Stal B500SP (PN-H-93220), beton wg arkuszy zbrojenia; oznaczenia prętów wg PN-EN ISO 3766.
- Rysunek wygenerowany automatycznie z modelu /home/user/aihouse/model/budynek.yaml (wersja 1.0, 2026-09-25) — generatory lamela.views.

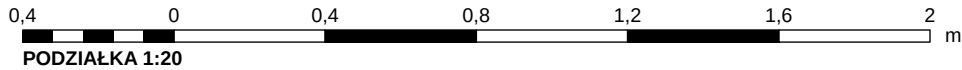

REW.	OPIS ZMIANY			DATA			
0	Wydanie — rysunek wygenerowany z modelu			2026-09-25			
PRACOWNIA PROJEKTOWA PRACOWNIA PROJEKTOWA — nazwa do uzupełnienia adres pracowni do uzupełnienia			STADIUM PT	BRANŻA KONSTRUKCJA (BO)			
INWESTOR (do uzupełnienia)							
OBIEKT / NAZWA ZAMIERZENIA BUDOWLANEGO Budynek mieszkalny jednorodzinny wolnostojący „Dom LAMELA”							
ADRES / LOKALIZACJA (NR DZIAŁKI, OBREB, JEDN. EWIDENCYJNA) ul. Lipowa (fikcyjna), dz. nr ewid. 123/4, obręb 0005 Przykładowo, gm. Przykładowo (fikcyjna)				KAT. OBIEKTU I			
FUNKCJA	IMIĘ I NAZWISKO		SPECJALNOŚĆ, NR UPRAWNIENI		DATA	PODPIS	
Projektant							
Projektant (wsp.)							
Sprawdzający							
Opracował							
TYTUŁ RYSUNKU WĘZŁY WSPORNIKÓW Z ŁĄCZNIKAMI TERMOIZOLACYJNYMI							
SKALA 1:20	FORMAT A2	DATA WYDANIA 2026-09-25	RODZAJ DOK. przekrój konstrukcyjny	NR RYSUNKU PT-BO-14		ARKUSZ 14/21	REW. 0