

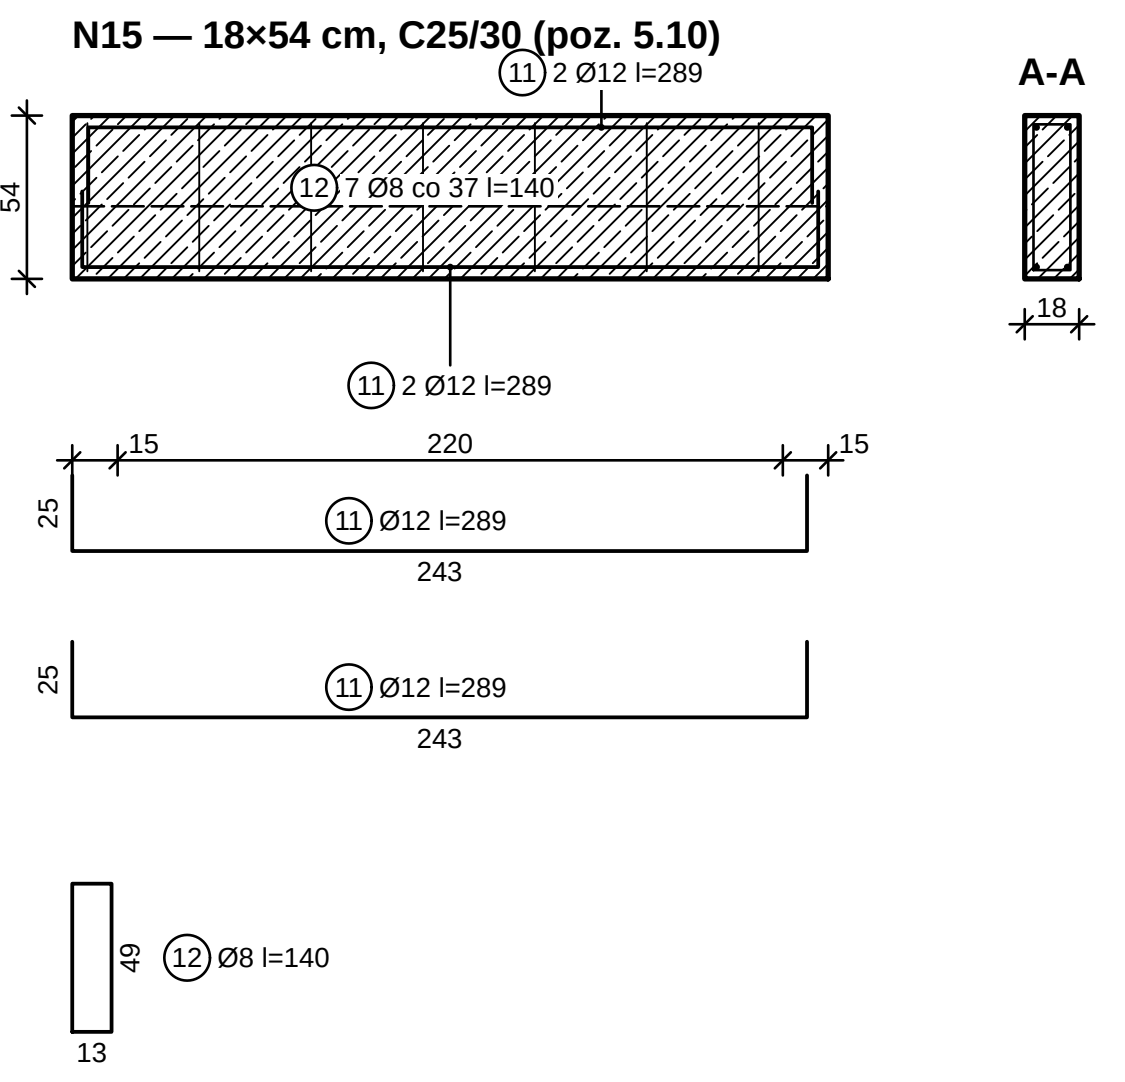
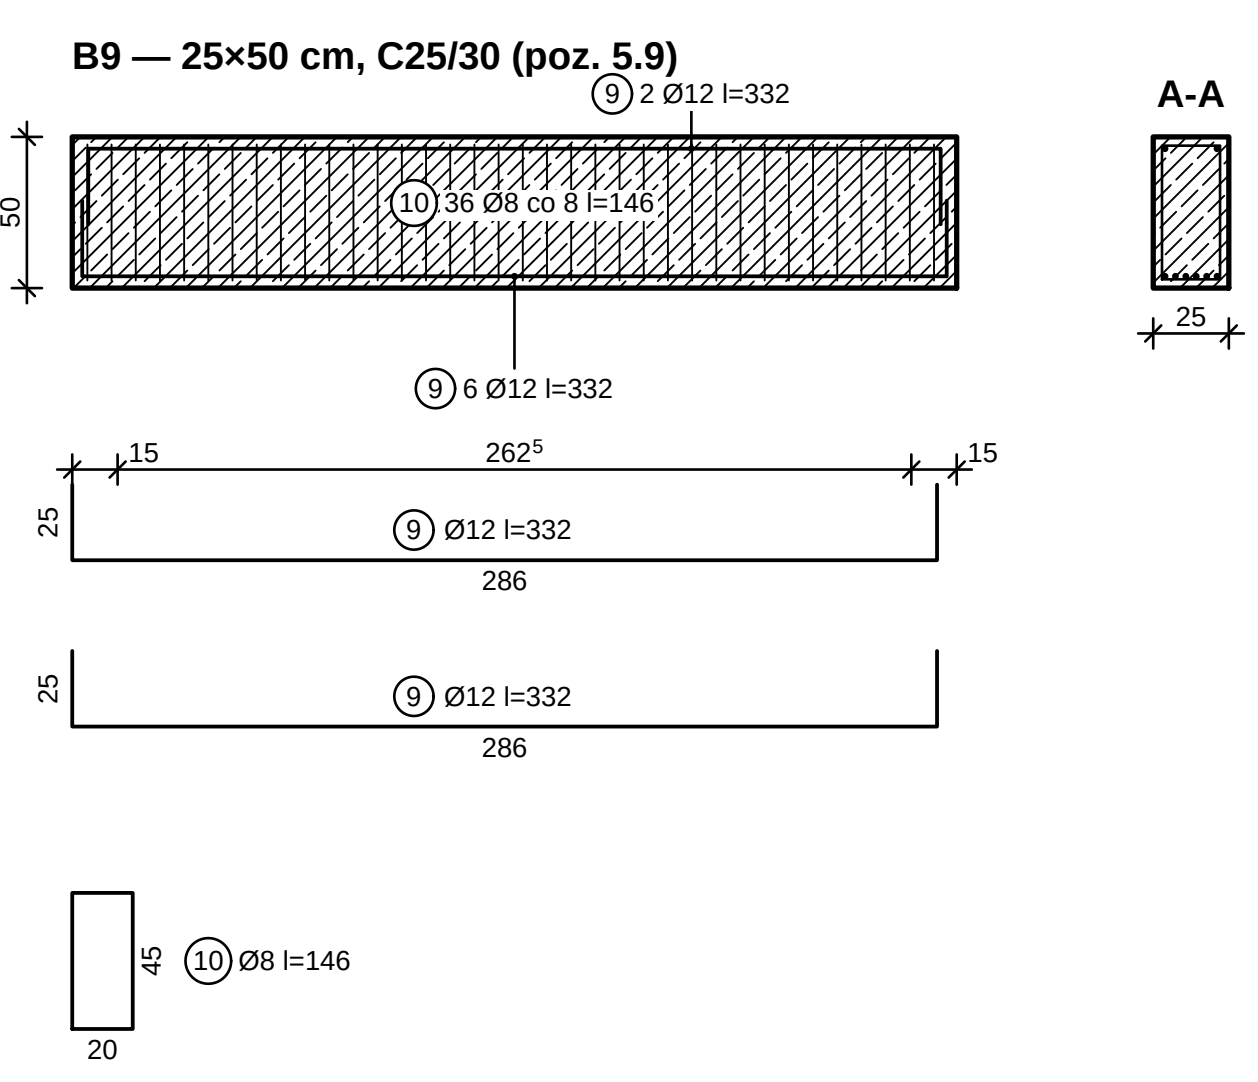
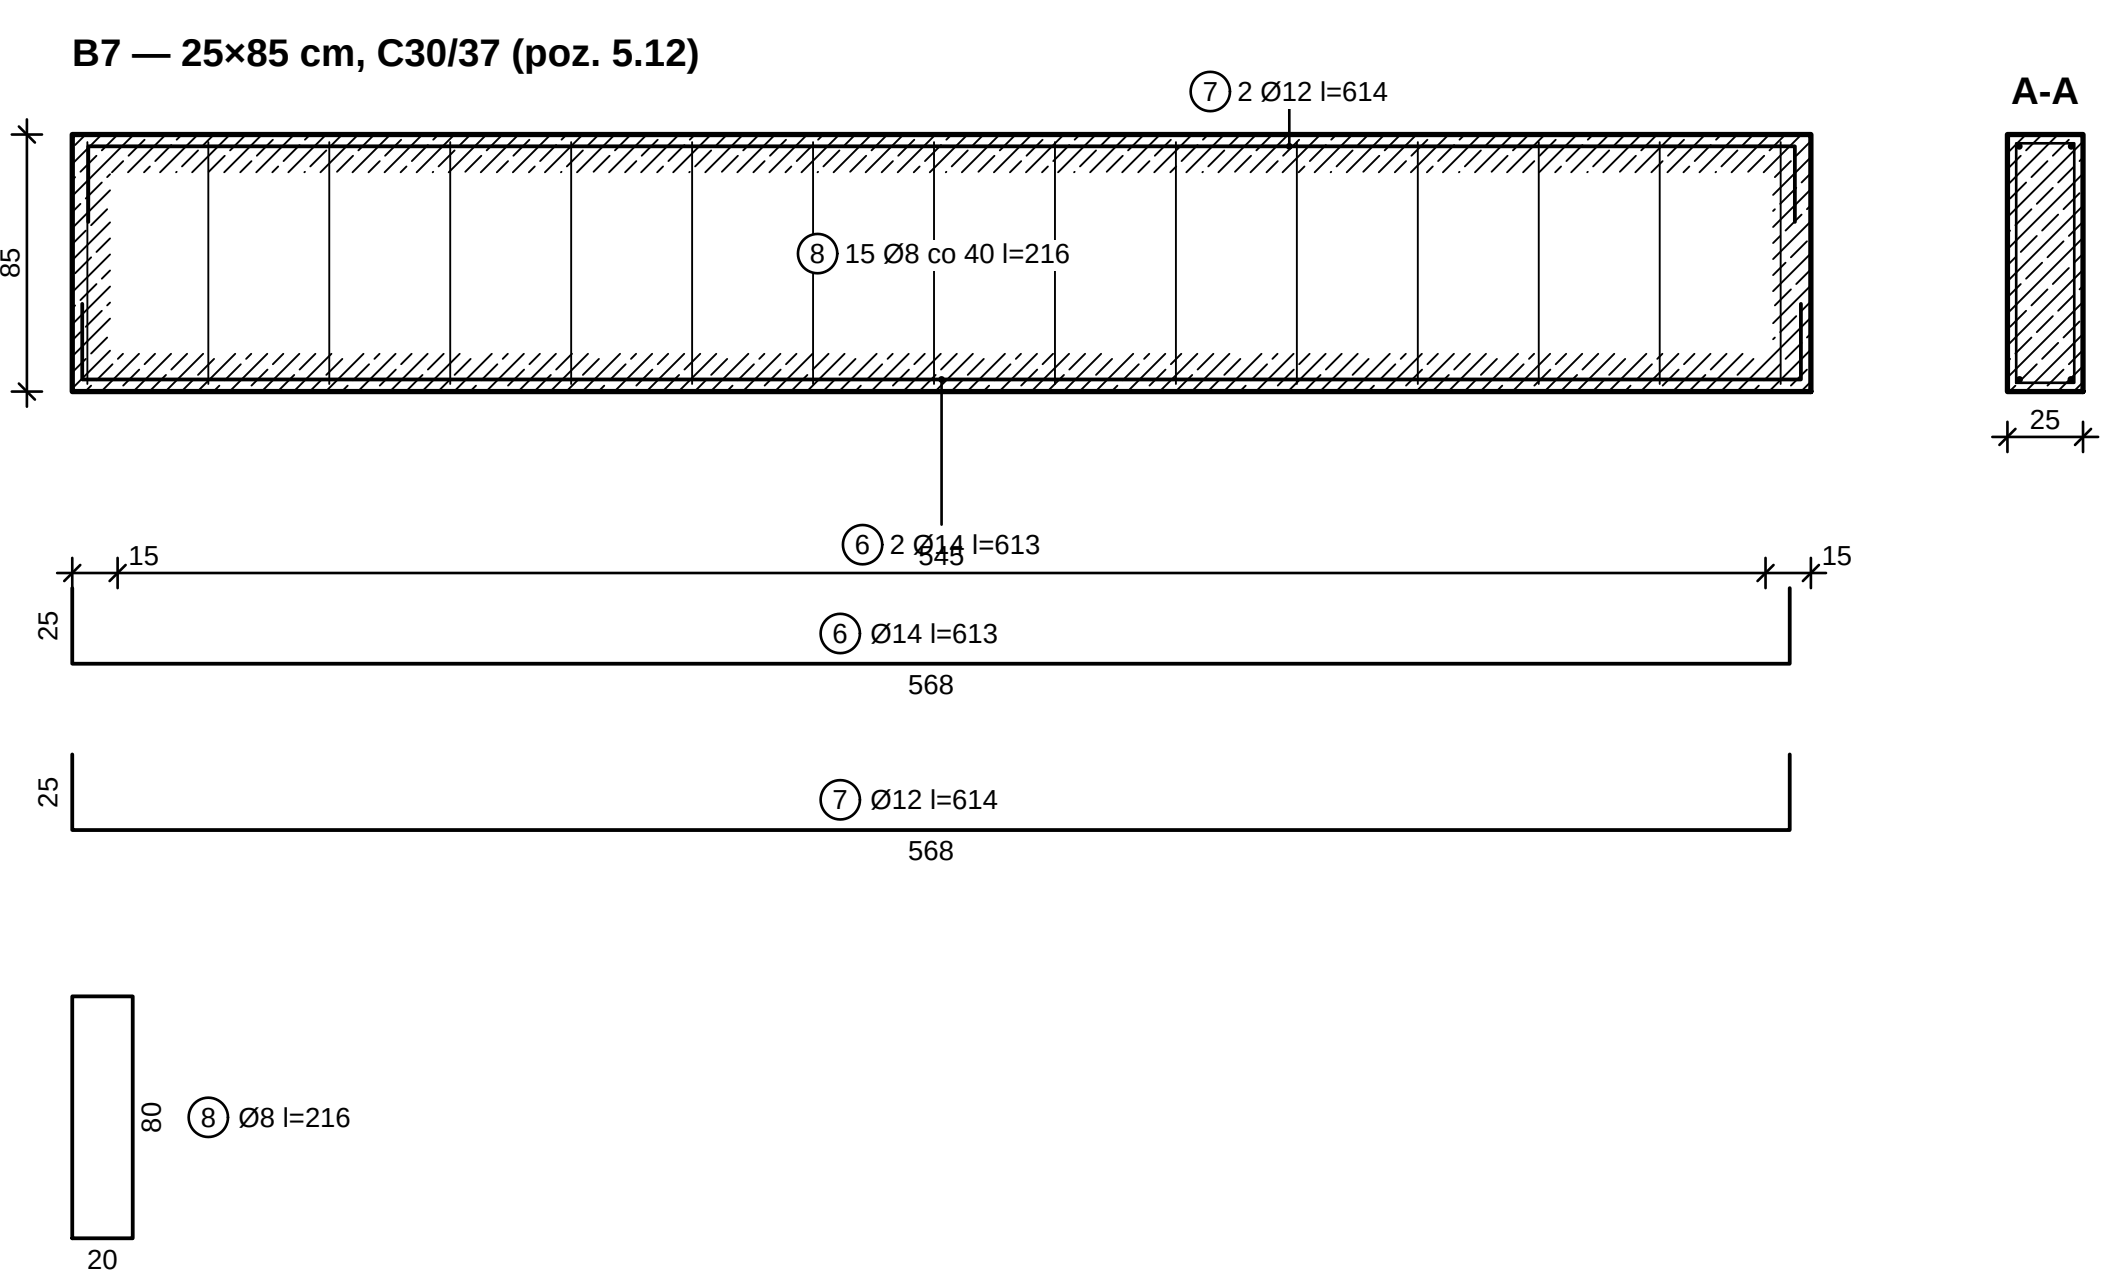
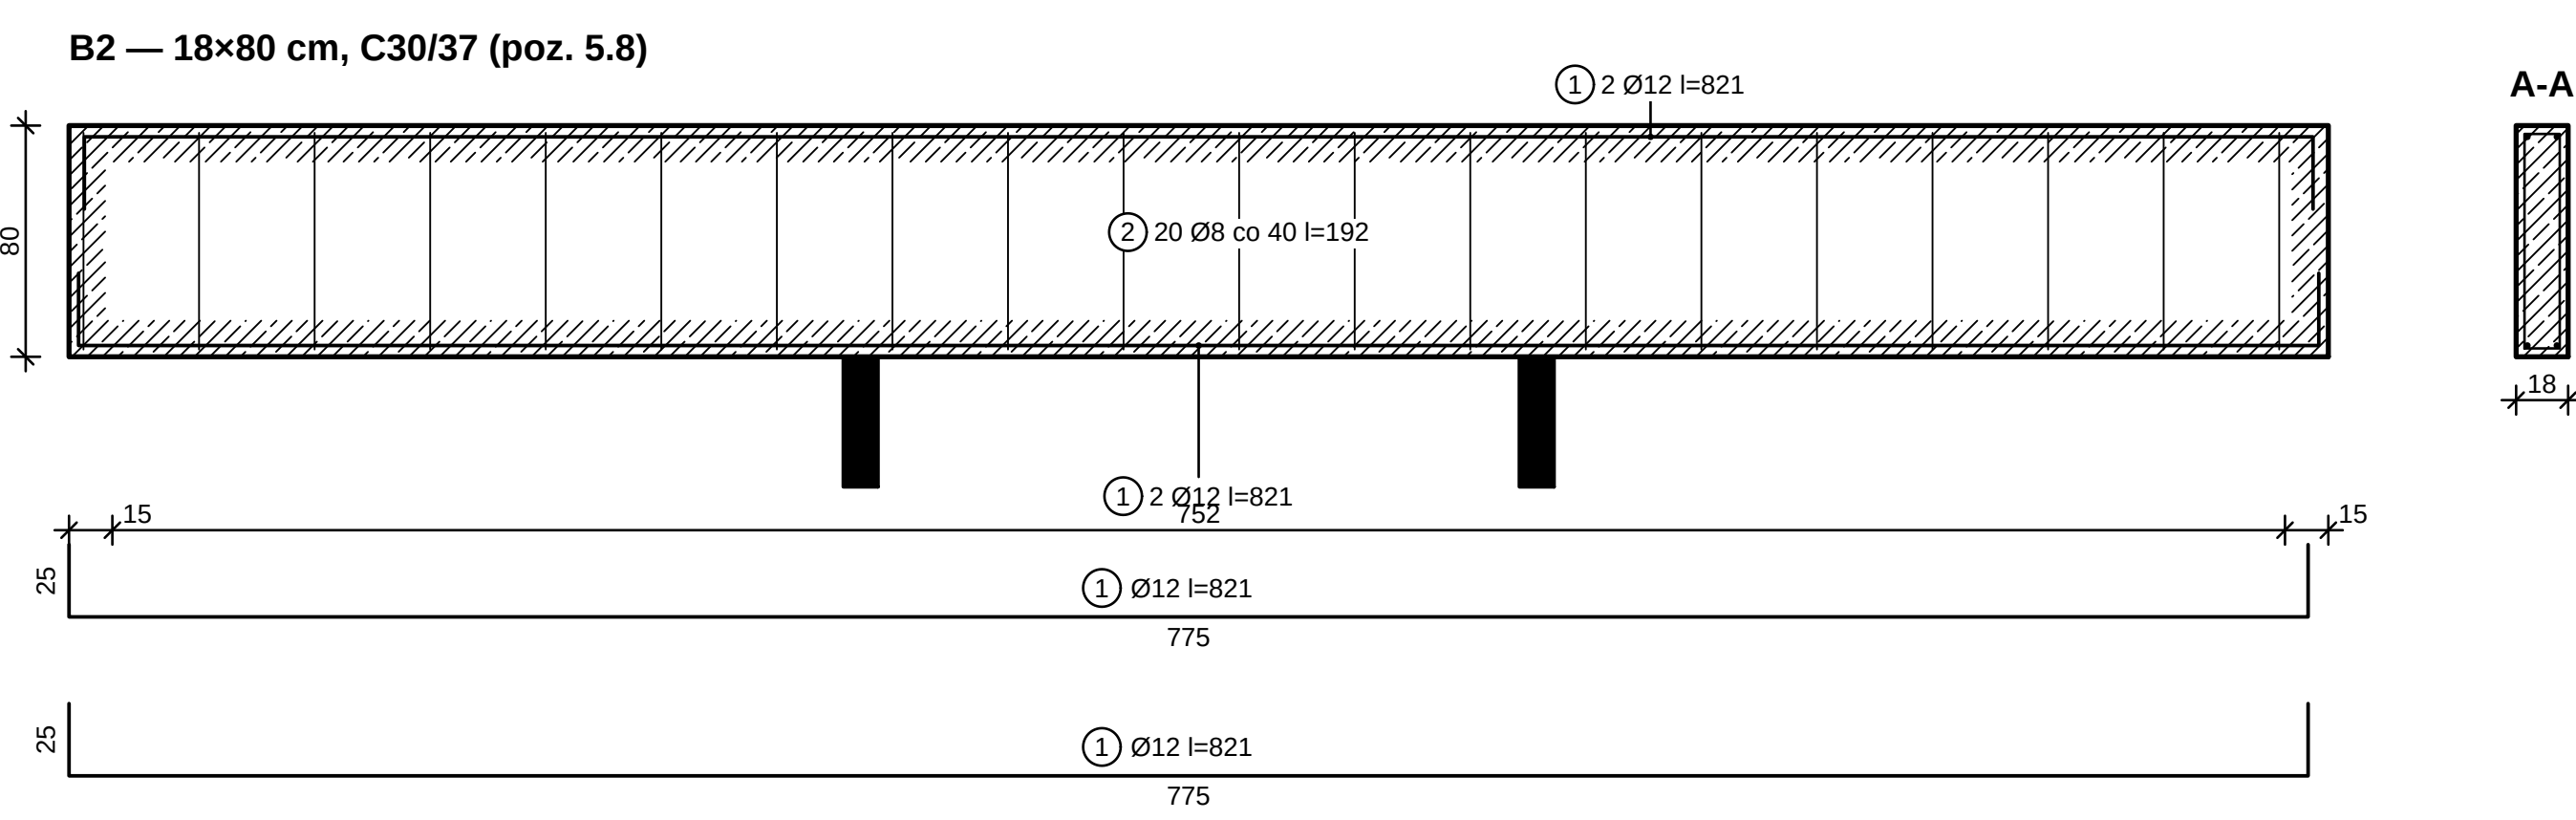
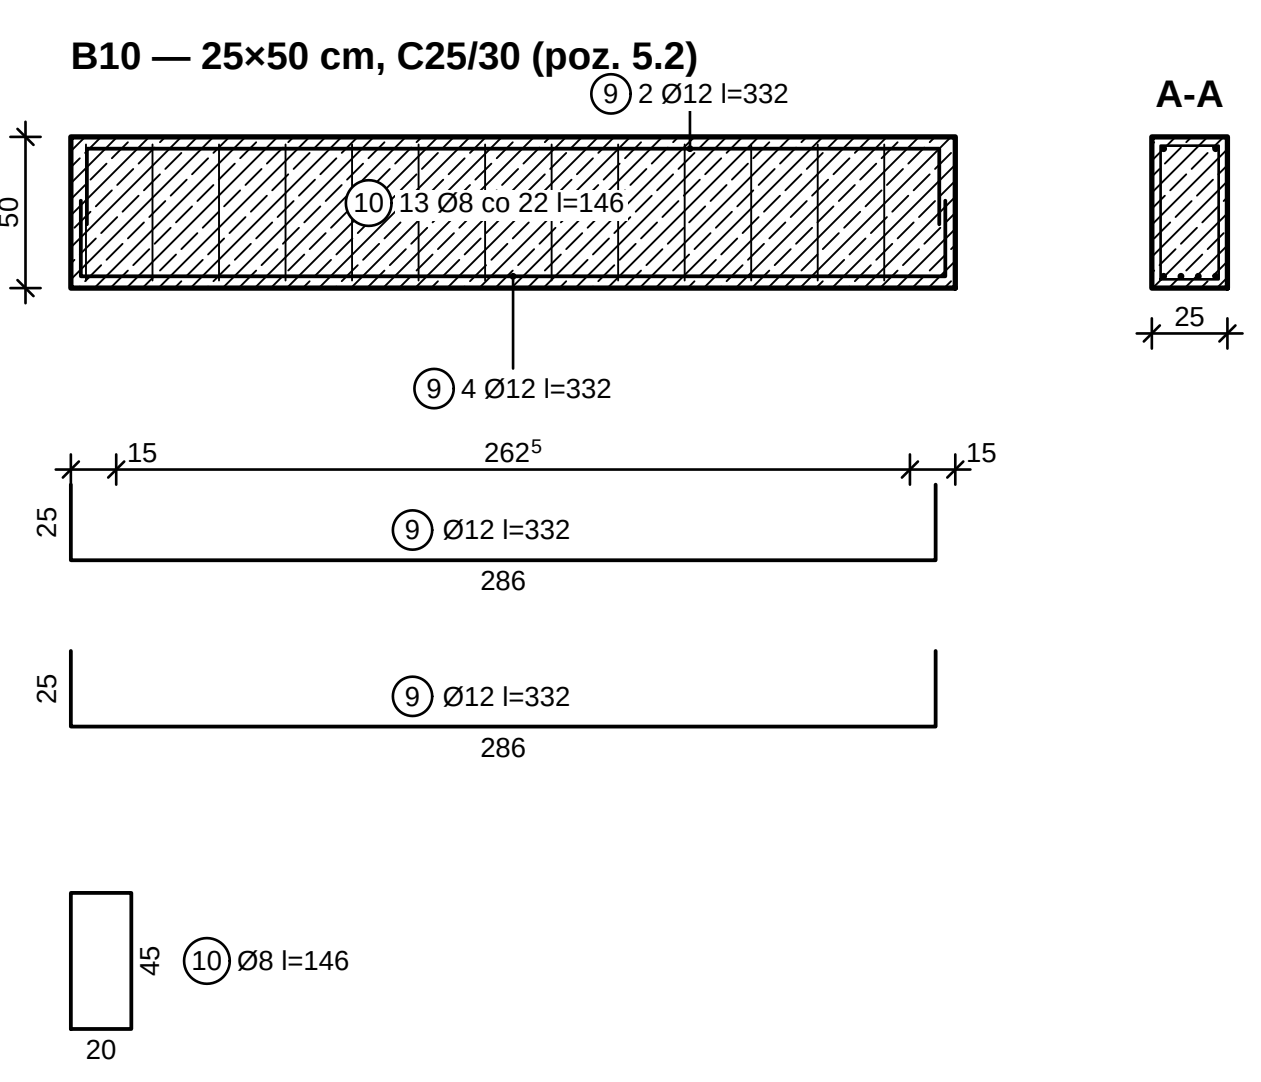


A
B
C
D
E
F
G
H
J
K
L
M
N
P
Q
R

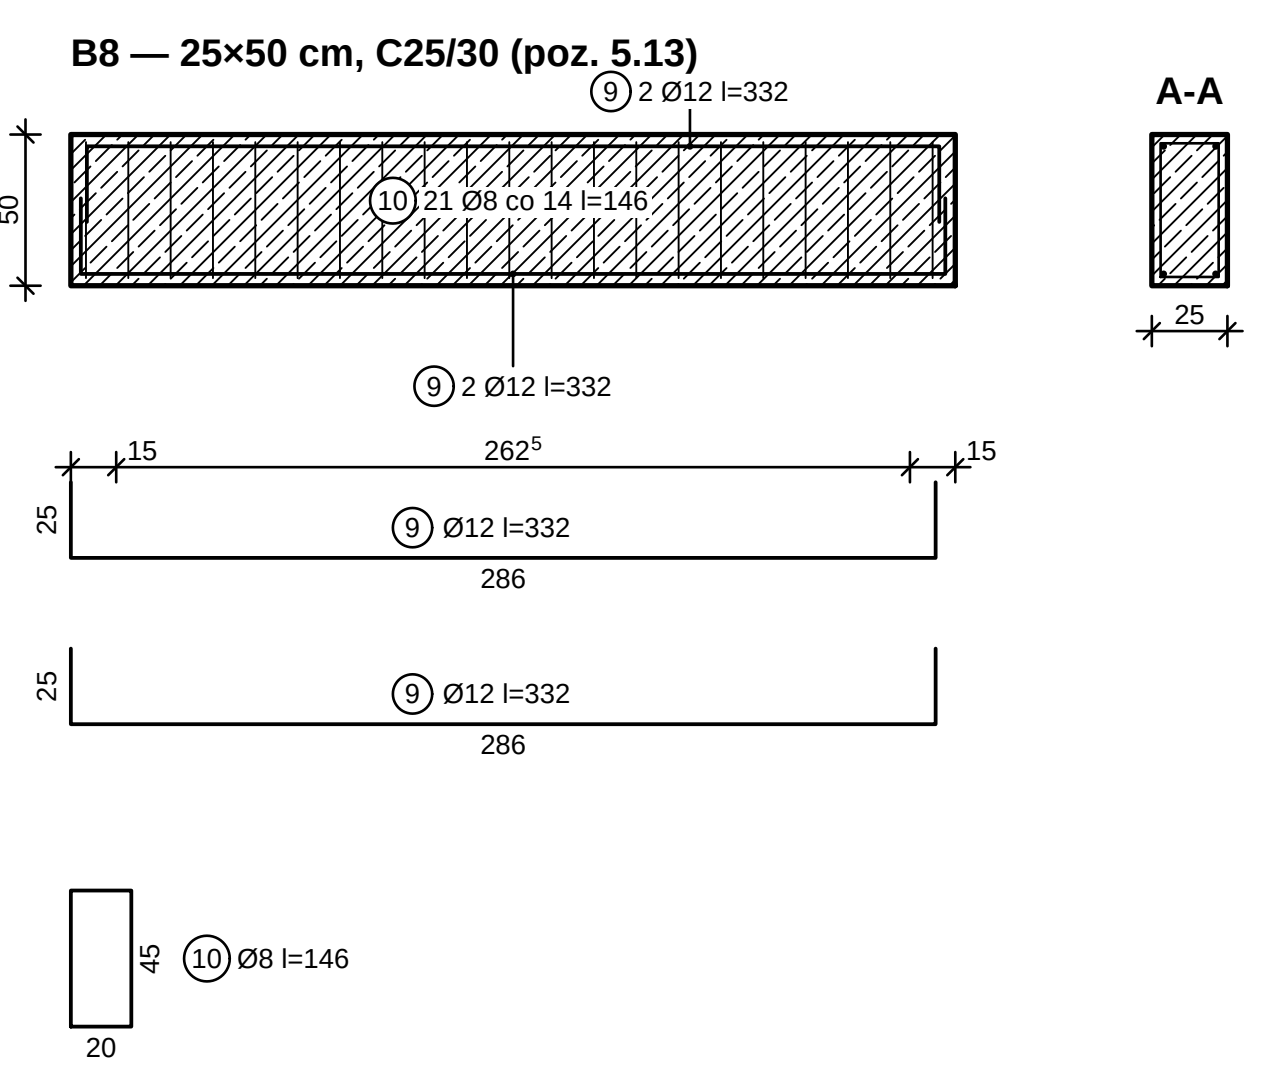

ZBROJENIE BELEK B2, B6, B7, B8, B9, B10, N15 1:25

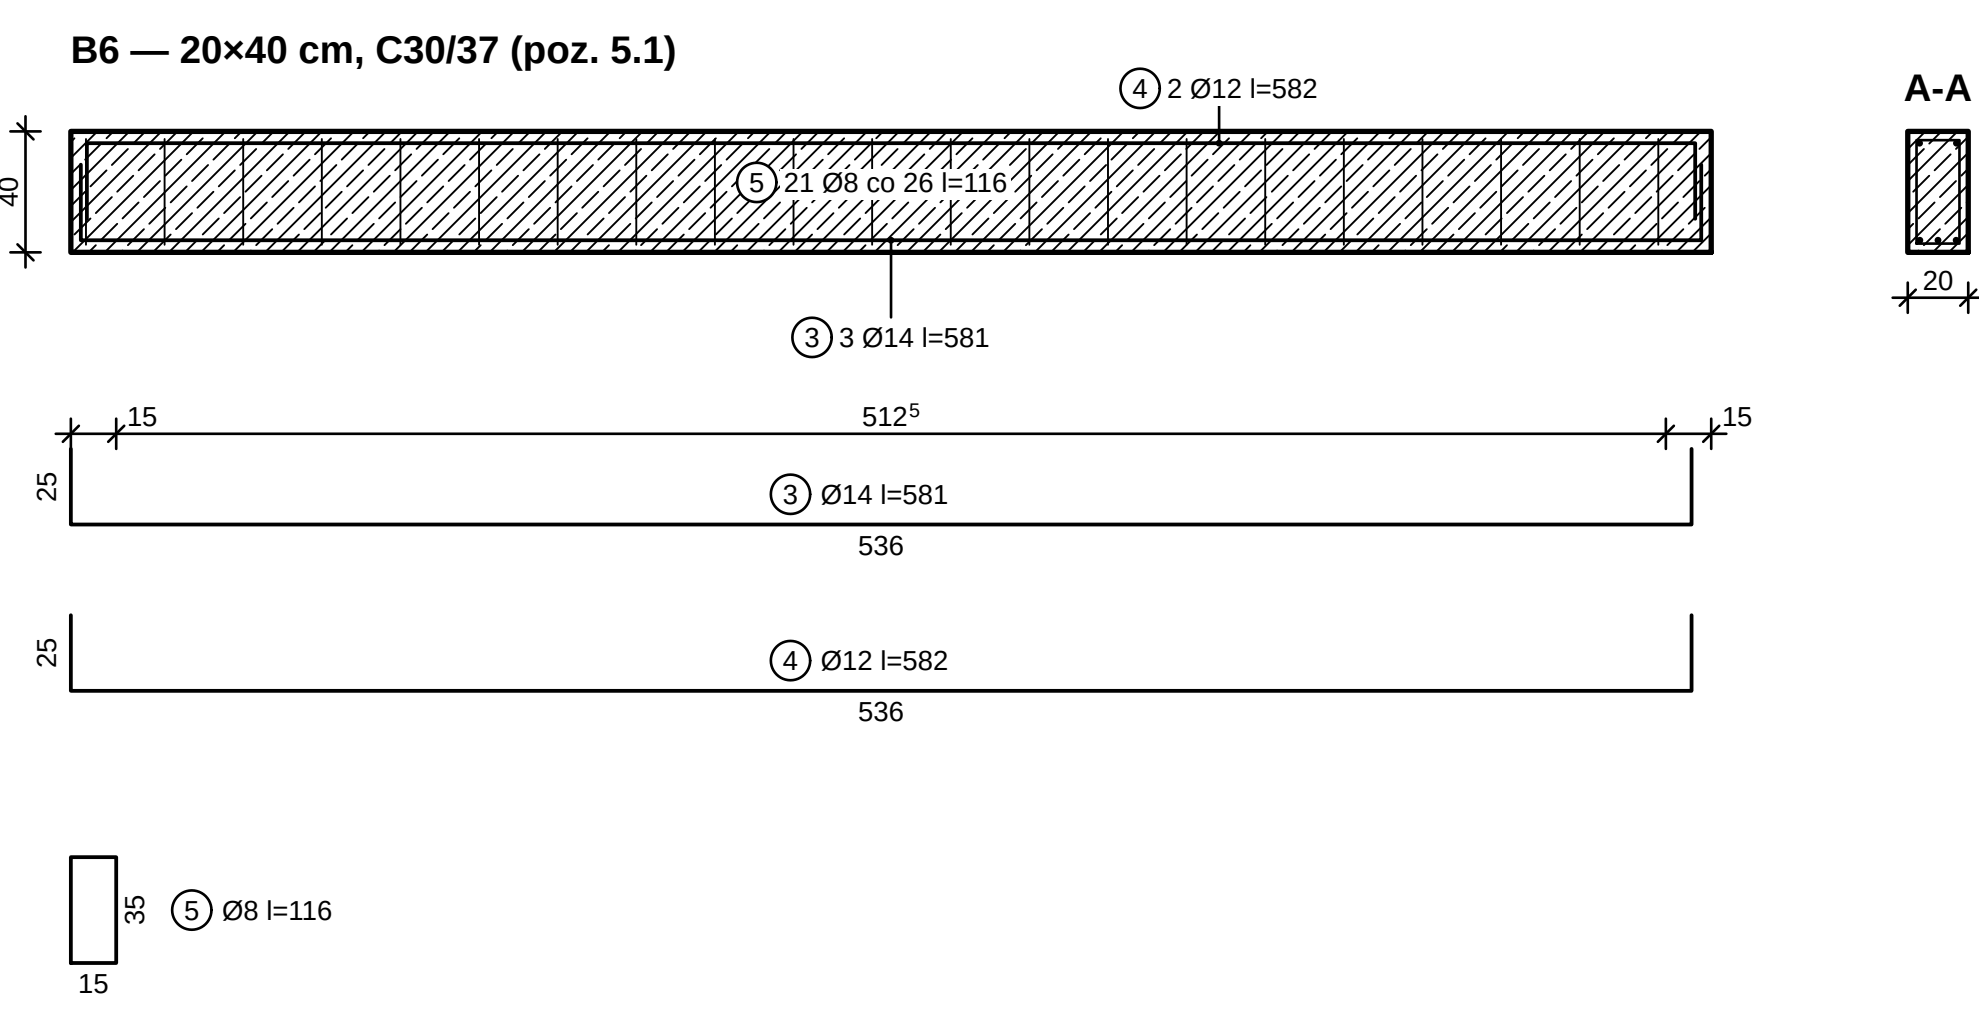


ZESTAWIENIE STALI									
Poz.	Ø [mm]	Kształ ISO 3766, wymiary [mm]	Øleg. [mm]	Liczba [szt.]	Elem.	ØB [mm]	Ø12 [mm]	Ø14 [mm]	
1	12	21. ø125 h=775 c=25	821	4	B2		32.84		
2	8	51. ø113 h=75	192	21	B2	40.32			
3	14	21. ø125 h=536 c=25	581	3	B6			17.43	
4	12	21. ø125 h=536 c=25	582	2	B6		11.64		
5	8	51. ø15 h=35	116	22	B6	25.52			
6	14	21. ø125 h=568 c=25	613	2	B7			12.28	
7	12	51. ø125 h=568 c=25	614	2	B7	34.56			
8	8	51. ø120 h=80	216	16	B7	34.56			
9	12	21. ø125 h=286 c=25	332	18	B8		59.76		
10	8	51. ø120 h=45	146	13	B8	106.58			
11	12	21. ø125 h=243 c=25	289	4	N15		11.56		
12	8	51. ø13 h=49	140	8	N15	11.20			
Długość całkowita [m]						218.2	129.1	29.7	
Masa całkowita [kg]						0.395	0.888	1.208	
Masa [kg]							86.1	113.7	35.9
RAZEM stał B500SPP [kg]									235.7

B2, B6, B7: beton C30/37, XC1, okładka wystrzelen c_nom = 25 mm (tab. 4.4b + NA).
B8, B9, B10, N15: beton C25/30, XC1, okładka wystrzelen c_nom = 25 mm (tab. 4.4b + NA).

OBJAŚNIENIA I UWAGI

1. Wymiary w cm, mm w okrągłych słupkach, np. 24° = 24,5 cm, okrągłe w węgłach ø0,000 = 101,600 mm a.n.m. (PN-EN ISO 3007-N4).
2. Białe przerywane linie — głównie z odstępami 90° w węzłach podporowych (zakazanie z 1, 3 od ścia podłogi — PN-EN 13962-1 9.2.1.4), strażnica zewnętrzna i nakładki 130° (0,5, 0,5, 0,5), powierzchnie strzemie 5 cm od ścia podłogi, rozmiar węg. okładki (0,2, 0,3, 0,4 mm) (0,5, 0,5, 0,5) (0,5, 0,5).
3. Przekrój A-A — w środku rozpiętości, długość przelotu — długość rozpiętości (wymiar zewnętrzny, odcięcie gęstości wg PN-EN ISO 3766).
4. Bezpłatnie: beton wg PN-EN 12618-2 (PN-EN 12618-2:2005) (Masa, ekspozycja, D, masa 18 mm, kompresyjność 53); przebieg z 7 dni (kategoria przebiegu) 2 — PN-EN 13870 p. 10, przeloty robocze wyłącznie w miejscach rozpiętości i rozpiętości.
5. Rozdzielanie i uszczelnienie robocze: gęstość przelotu przelotu z 7 dni (PN-EN 12618 p. 5.6 i 6.5), wspornik — nie wchodzi w grę po 28 dniach po wykonaniu elementów docelowych zaprawy, przeloty robocze do 28 dni.
6. Rysunek wygenerowany automatycznie z modelu Homoluxen/Arconet/ModulBudynki.yam (wersja 1.0, 2025-09-25) — generatory lamela views.

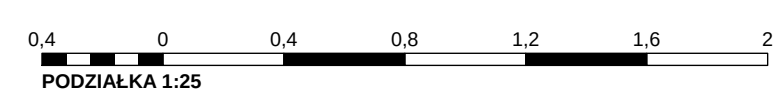

REV.	OPIS ZMIANY	DATA
0	Wydanie — rysunek wygenerowany z modelu	2026-09-25
PRACOWNIA PROJEKTOWA PRACOWNIA PROJEKTOWA — nazwa do uzupełnienia		STANOWISKO PT
adres pracowni do uzupełnienia		BRANŻA KONSTRUKCJA (BO)
INWESTOR (do uzupełnienia)		
OBJEKT / NAZWA ZAMIERZENIA BUDOWLANEGO Budynek mieszkalny jednorodzinny wolnostojący „Dom LAMELA”		
ADRES / LOKALIZACJA (NR DZIAŁKI, OBRĘB, DZPŁ, ENWIDENCJA)		
ul. Lipowa (Włocławek), dz. nr ewid. 123/4, obręb 0005 Przyładowo, gm. Przyładowo (Włocławek)		KAT. OBJEKTU I
Funkcja	Imię i Nazwisko	Specjalność, nr uprawnień
Projektant		Data
Projektant (wsp.)		Podpis
Sprawdzający		
Opracował		
Tytuł rysunku		
ZBROJENIE BELEK (1)		
Skala	Format	Data wydania
1:25	A0	2026-09-25
Rodzaj dok.	Nr rysunku	Arkusz
PT-BO-16	16/21	0