


odcinek kontroli 100 mm (wydruk 1:1)

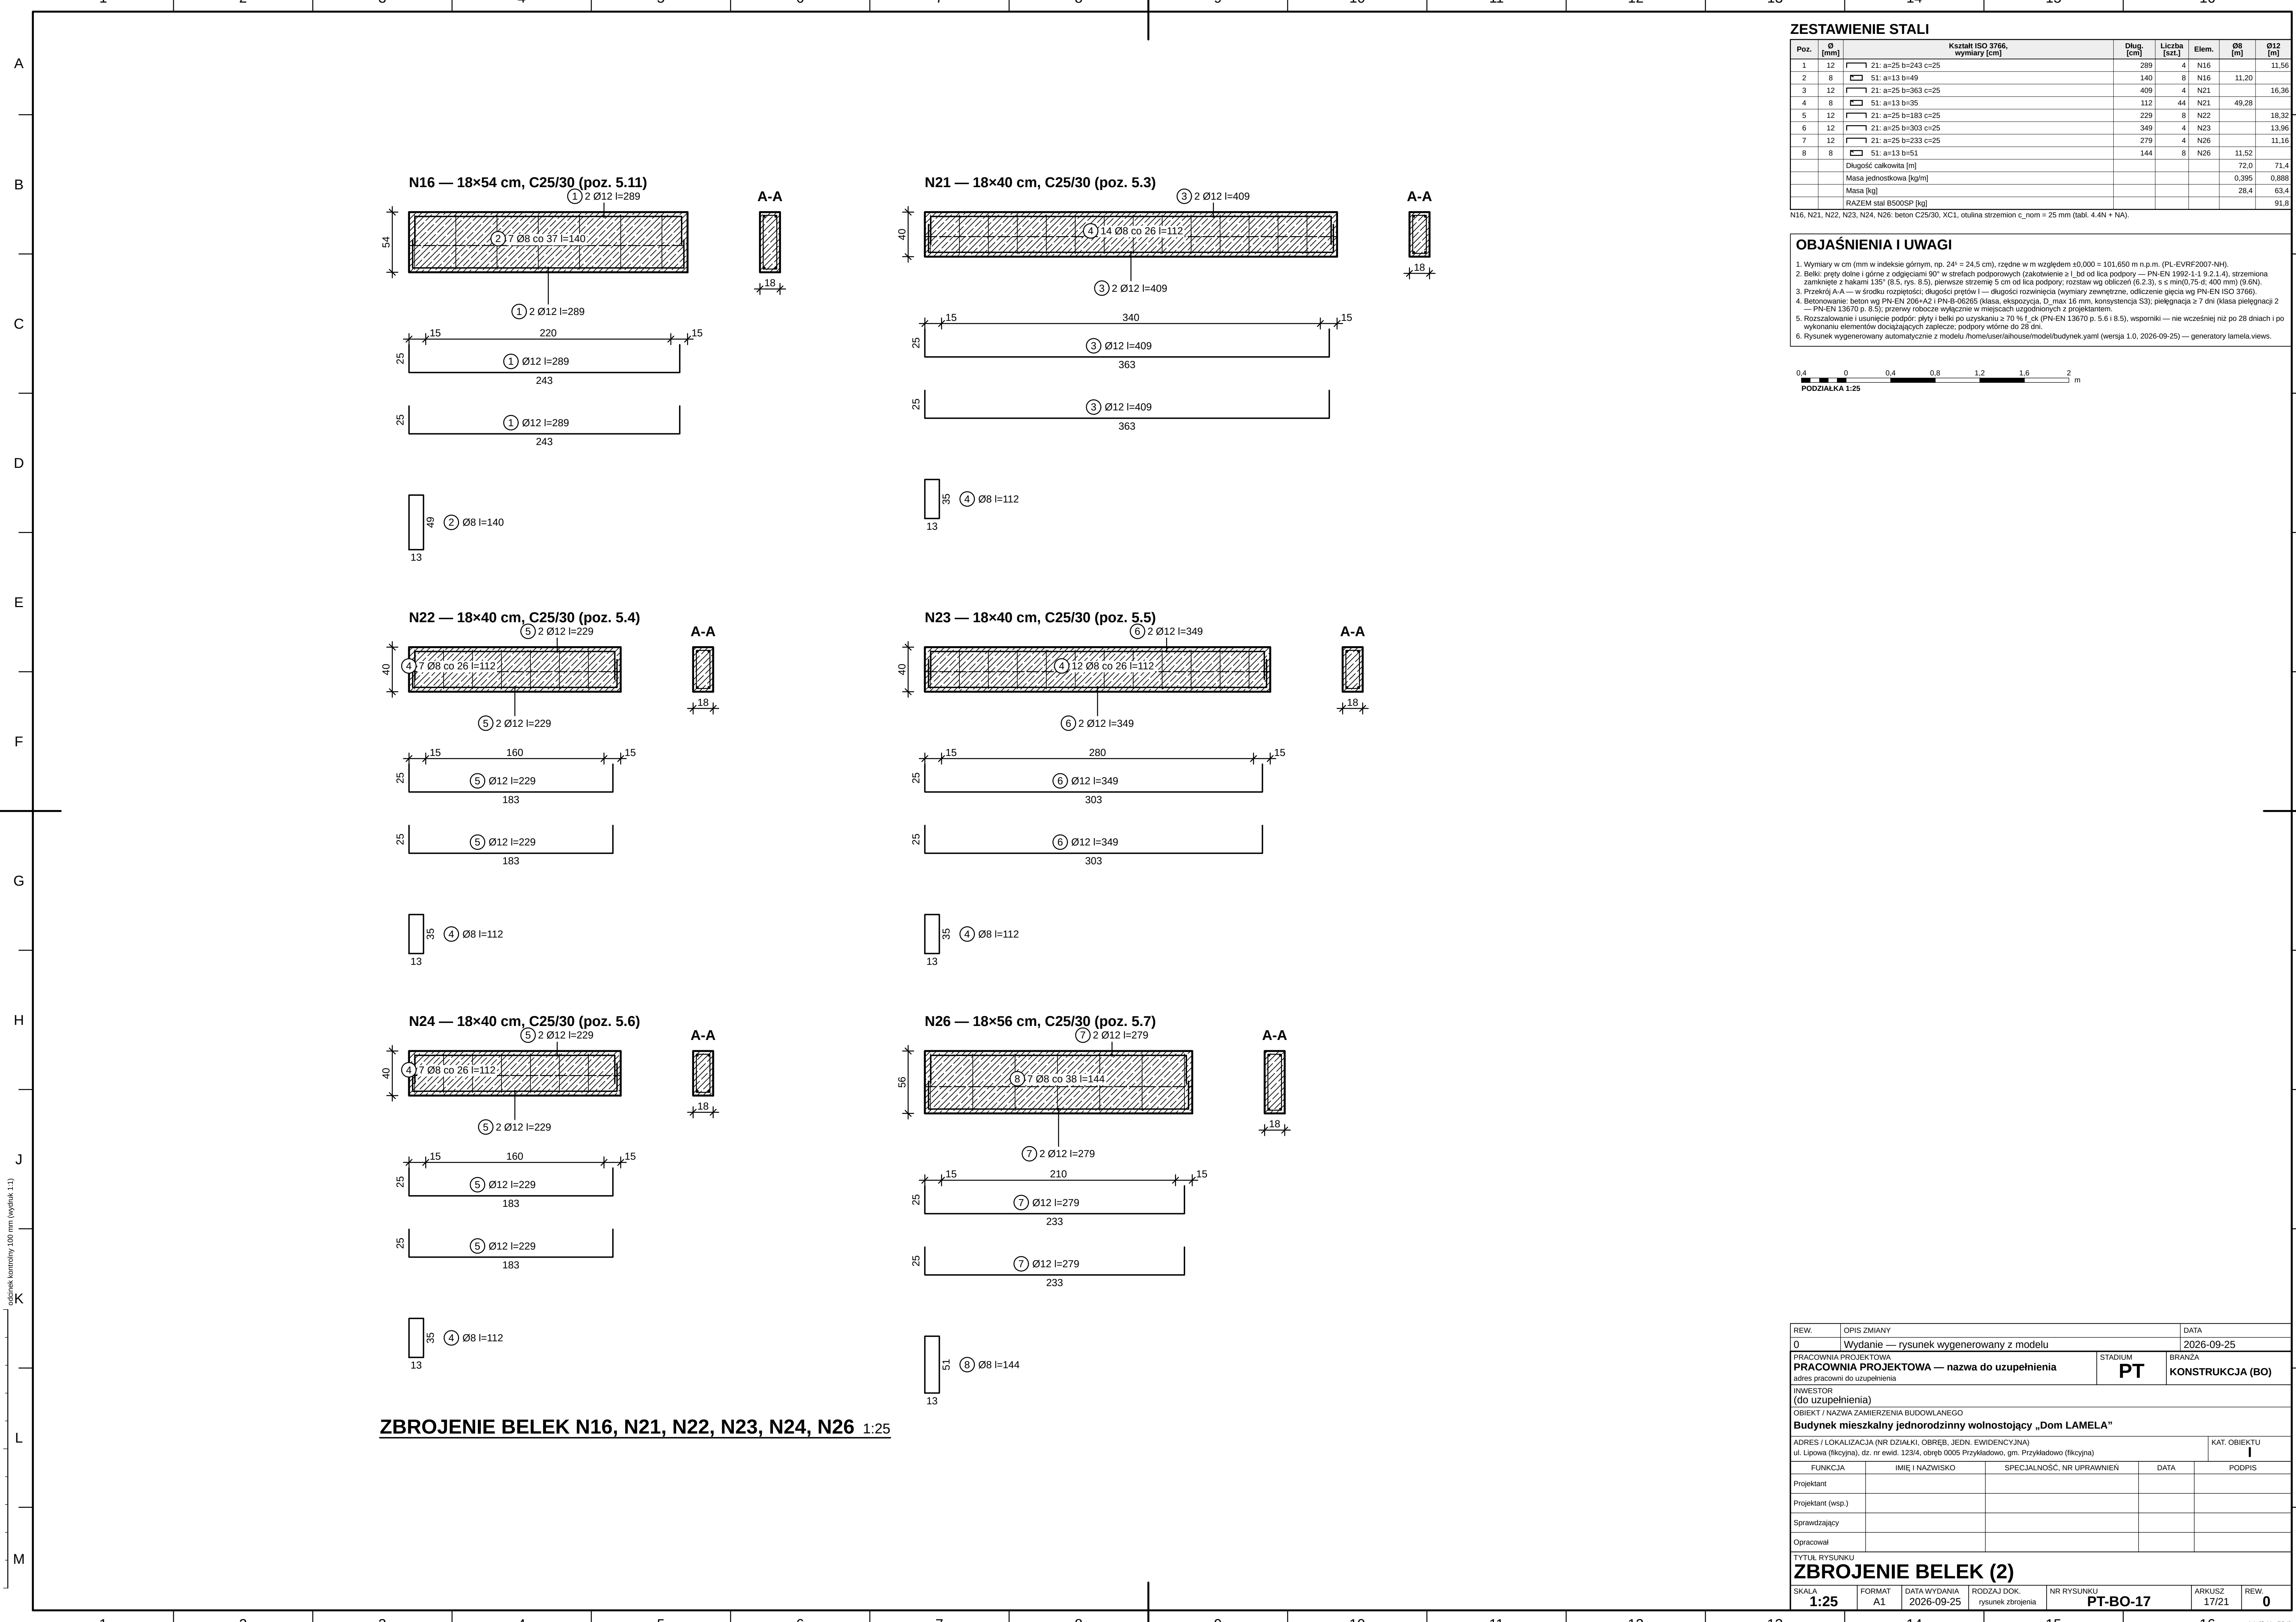

ZBROJENIE BELEK N16, N21, N22, N23, N24, N26 1:25


ZESTAWIENIE STALI

Poz.	Ø [mm]	Kształt ISO 3766, wymiary [cm]	Dług. [cm]	Liczba [szt.]	Elem.	Ø8 [m]	Ø12 [m]
1	12	21: a=25 b=243 c=25	289	4	N16		11,56
2	8	51: a=13 b=49	140	8	N16	11,20	
3	12	21: a=25 b=363 c=25	409	4	N21		16,36
4	8	51: a=13 b=35	112	44	N21	49,28	
5	12	21: a=25 b=183 c=25	229	8	N22		18,32
6	12	21: a=25 b=303 c=25	349	4	N23		13,96
7	12	21: a=25 b=233 c=25	279	4	N26		11,16
8	8	51: a=13 b=51	144	8	N26	11,52	
Długość całkowita [m]						72,0	71,4
Masa jednostkowa [kg/m]						0,395	0,888
Masa [kg]						28,4	63,4
RAZEM stal B500SP [kg]							91,8

N16, N21, N22, N23, N24, N26: beton C25/30, XC1, otulina strzemiem c_nom = 25 mm (tabl. 4.4N + NA).

OBJAŚNIENIA I UWAGI

- Wymiary w cm (mm w indeksie górnym, np. 24^o = 24,5 cm), rzędne w m względem ±0,000 = 101,650 m n.p.m. (PL-EVRF2007-NH).
- Belki: przędy dółne i górne z odgięciem 90° w strefach podporowych (zakotwienie ≥ 1,5d od łoża podpory — PN-EN 1992-1-1 § 2.1.4), strzemięna zamknięte z hakami 135° (8.5, rys. 8.5), pierwsze strzemię 5 cm od łoża podpory, rozstaw wg obliczeń (6.2.3), s ≤ min(0,75 d, 400 mm) (8.6N).
| 3. Przekrój A-A — w środku rozpiętości; długości prętów I — długości rozwinięcia (wymiary zewnętrzne, odliczenie gięcia wg PN-EN ISO 3766). | | | | | | | |
| 4. Betonowanie: beton wg PN-EN 206+A2 i PN-B-06265 (klasa, ekspozycja, D_max 16 mm, konsystencja S3); pielęgnacja ≥ 7 dni (klasa pielęgnacji 2 — PN-EN 13670 p. 8.5), przewij robocze wyłącznie w miejscach uzgodnionych z projektantem. | | | | | | | |
| 5. Rozszalowanie i usunięcie podpor: płyty i belki po uzyskaniu ≥ 70 % f_{ck} (PN-EN 13670 p. 5.6 i 8.5), wsporniki — nie wcześniej niż po 28 dniach i po wykonaniu elementów docinających zaplecze; podpory wtórne do 28 dni. | | | | | | | |
| 6. Rysunek wygenerowany automatycznie z modelu /home/user/ai/house/model/budynek.yam1 (wersja 1.0, 2026-09-25) — generatory lamela.views. | | | | | | | |

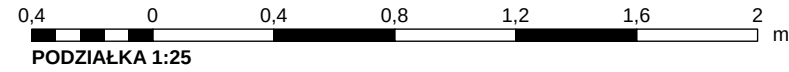

REW.	OPIS ZMIANY			DATA	
0	Wydanie — rysunek wygenerowany z modelu			2026-09-25	
PRACOWNIA PROJEKTOWA PRACOWNIA PROJEKTOWA — nazwa do uzupełnienia			STADIUM PT	BRANŻA KONSTRUKCJA (BO)	
adres pracowni do uzupełnienia					
INWESTOR (do uzupełnienia)					
OBJEKT / NAZWA ZAMIERZENIA BUDOWLANEGO Budynek mieszkalny jednorodzinny wolnostojący „Dom LAMELA”					
ADRES / LOKALIZACJA (NR DZIAŁKI, OBRĘB, JEDN. EWIDENCYJNA) ul. Lipowa (fikcyjna), dz. nr ewid. 1234, obręb 0005 Przykładowo, gm. Przykładowo (fikcyjna)					KAT. OBJEKTU I
FUNKCJA		IMIĘ I NAZWISKO	SPECJALNOŚĆ, NR UPRAWNIEN	DATA	PODPIS
Projektant					
Projektant (wsp.)					
Sprawdzający					
Opracował					
TYTUŁ RYSUNKU ZBROJENIE BELEK (2)					
SKALA 1:25	FORMAT A1	DATA WYDANIA 2026-09-25	RODZAJ DOK. rysunek zbrojenia	NR RYSUNKU PT-BO-17	ARKUSZ 17/21
				REW. 0	