

A

B

C

D









E

F

G

H

odcinek kontynuacji 100 mm (wydruk 1:1)

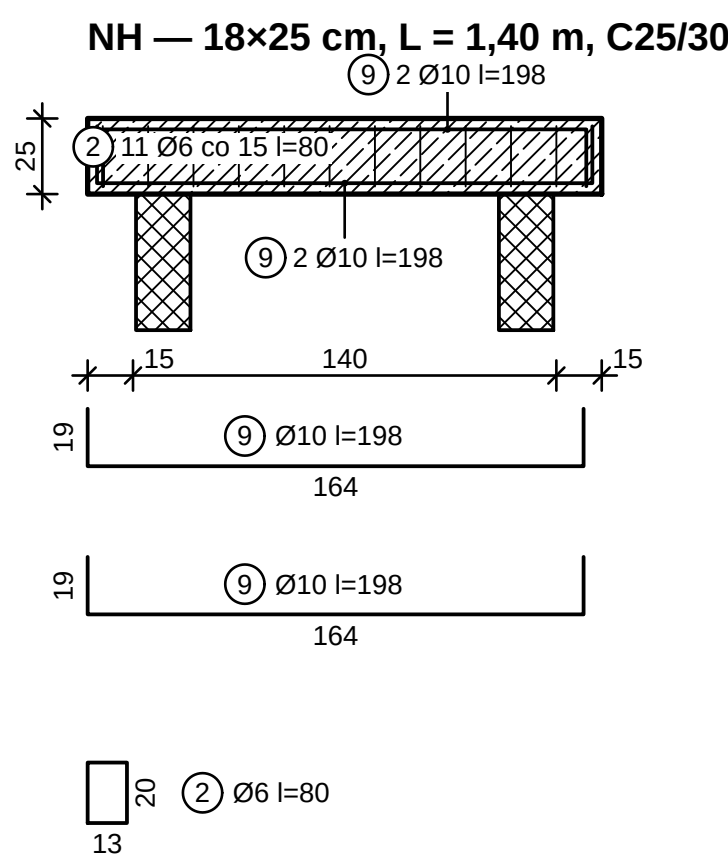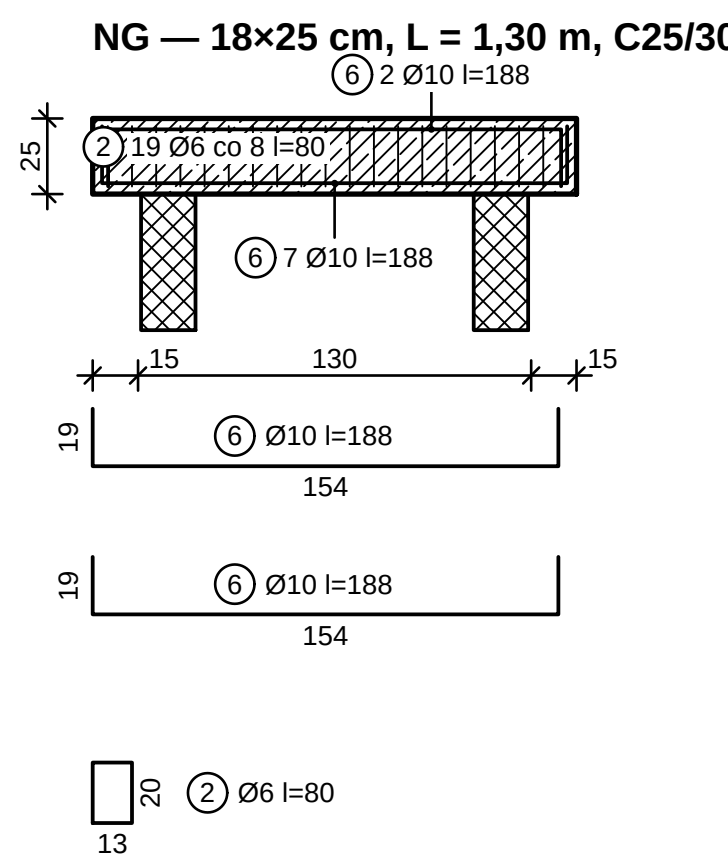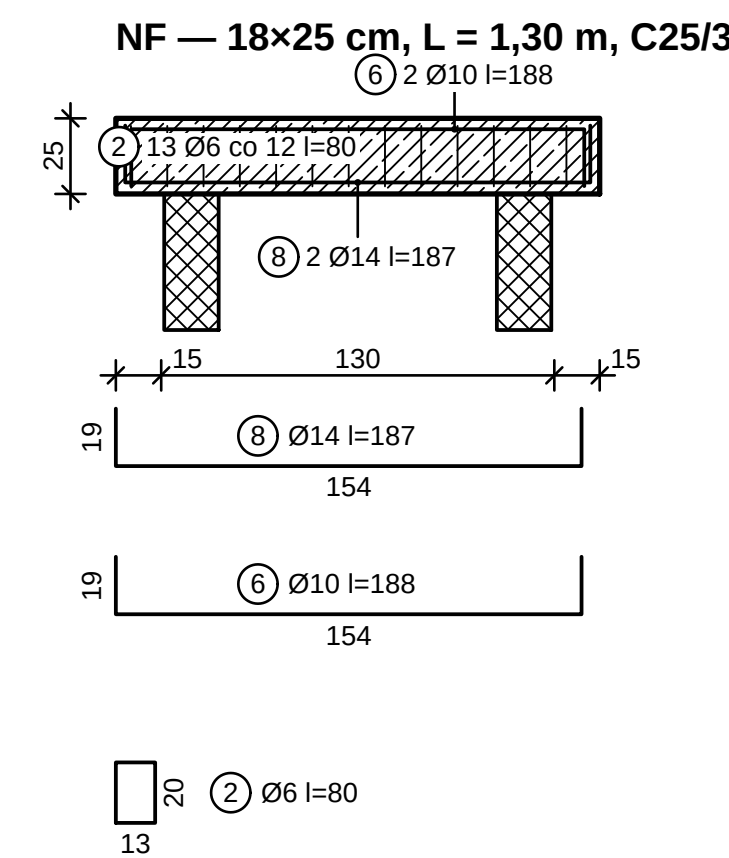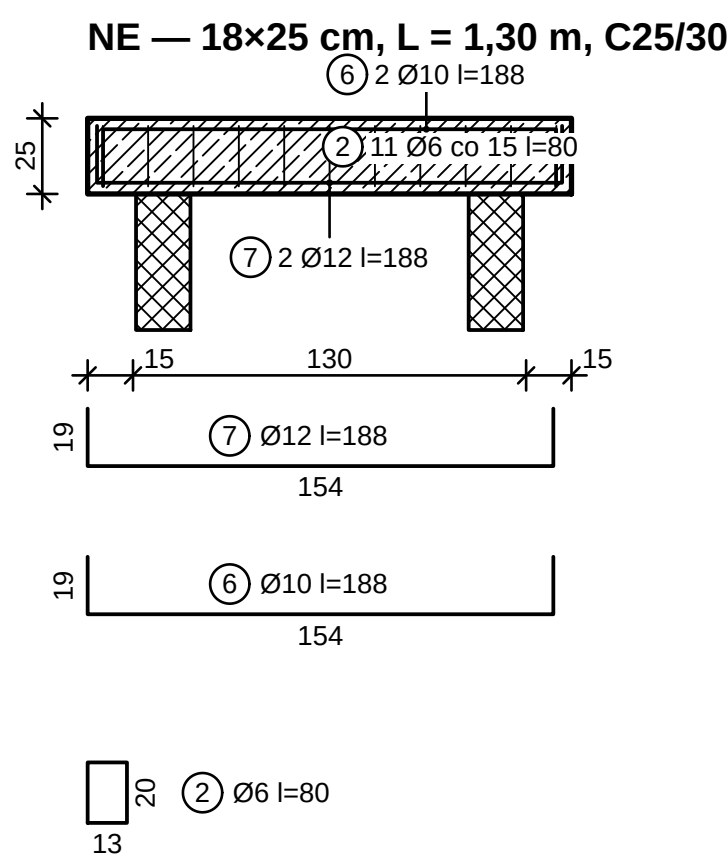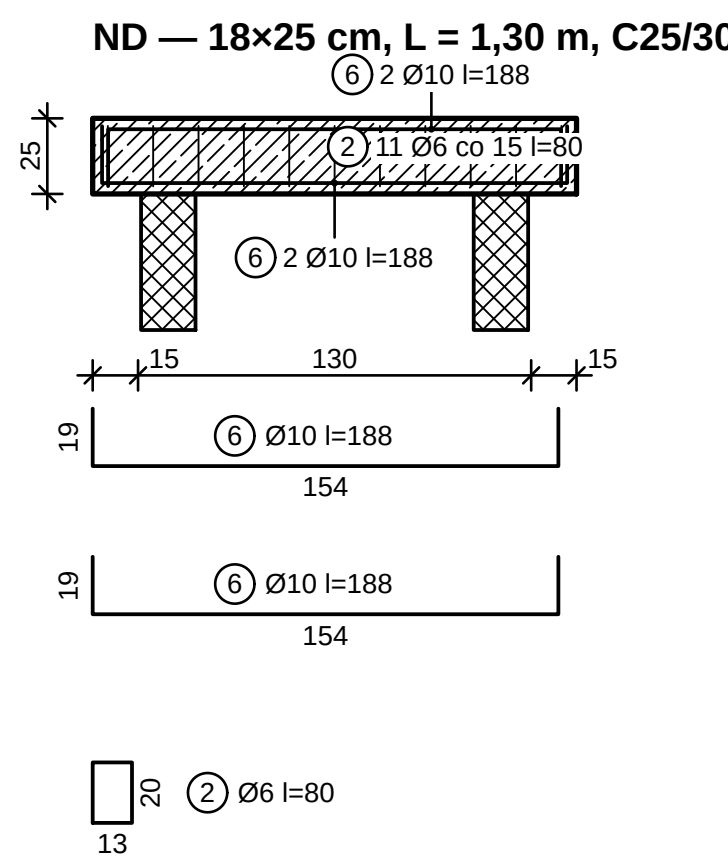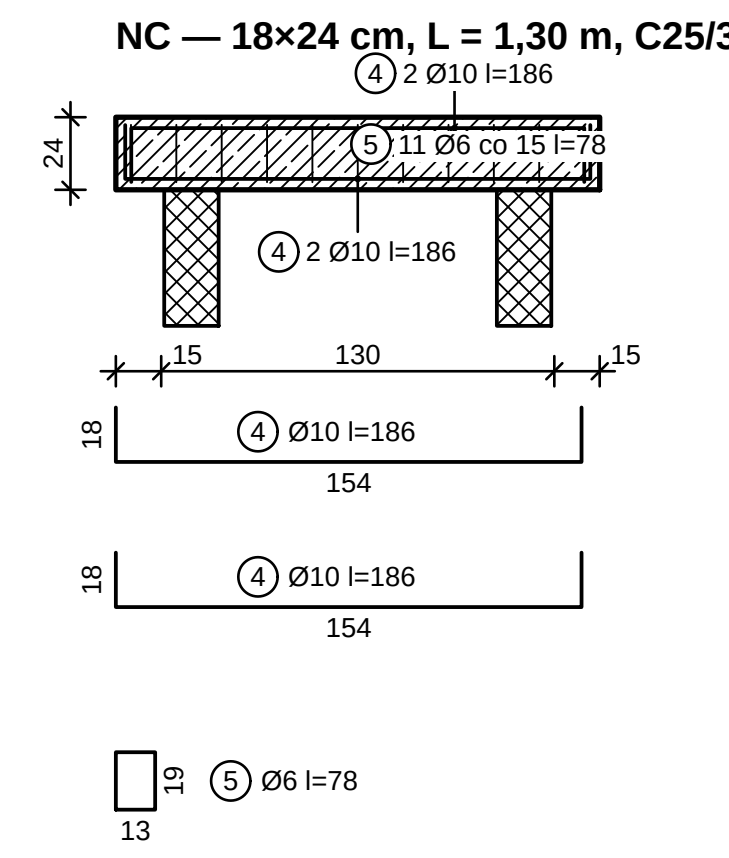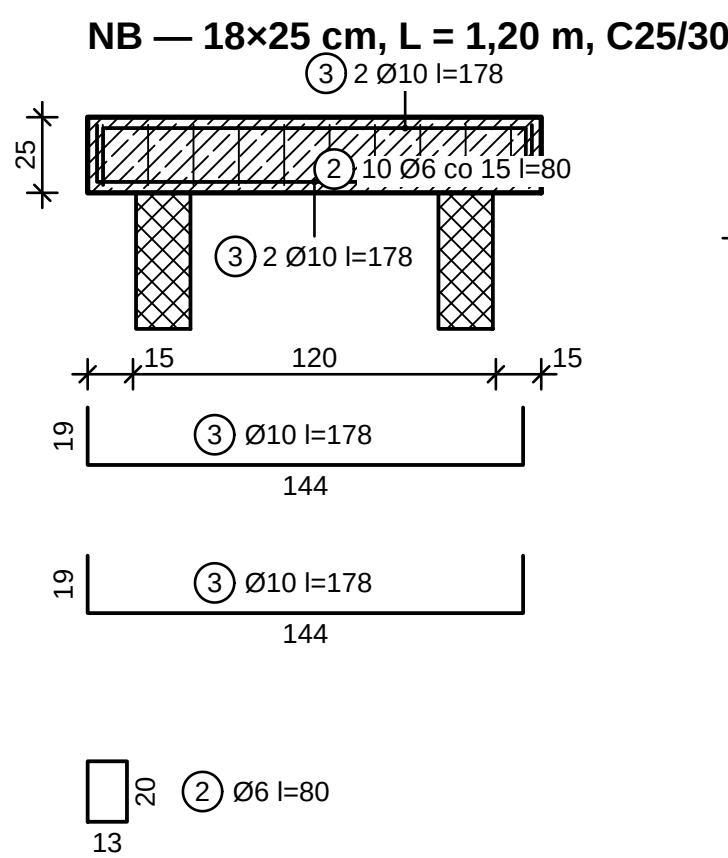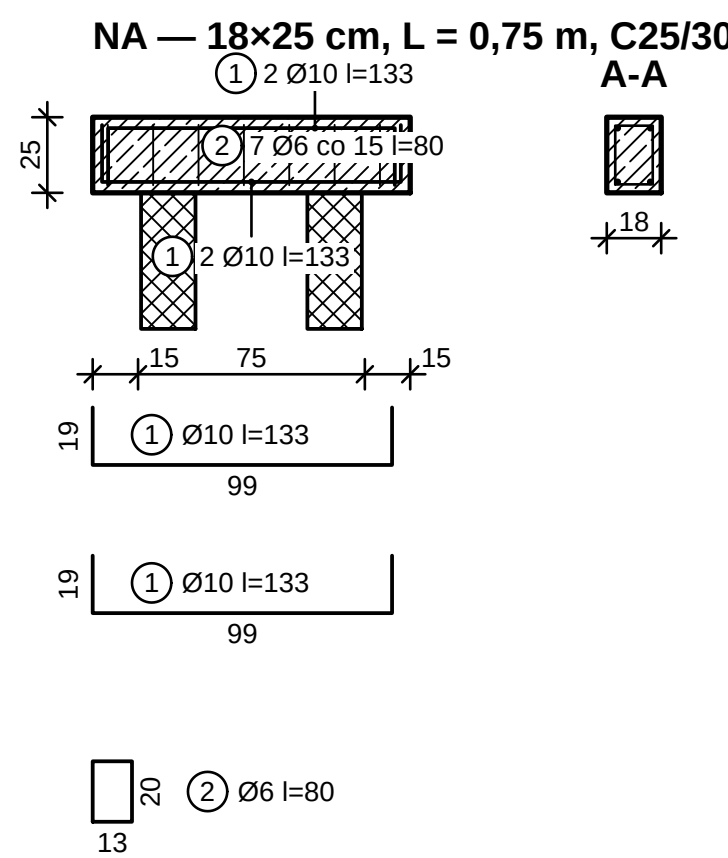

ZBROJENIE NADPROŻY NA, NB, NC, ND, NE, NF, NG, NH 1:25

TYPY NADPROŻY — OTWORY I POZYCJE OBLICZEŃ

Typ	Otwory	Poz. obl.	Szt.
NA	O0-10	6.10	1
NB	O0-13, O0-17	6.13, 6.16	2
NC	O0-06	6.6	1
ND	O0-15, O0-22, O1-03, O1-09, O1-12, O2-06	6.15, 6.19, 6.22, 6.26, 6.29, 6.37	6
NE	O0-14, O0-21, O2-10	6.14, 6.18, 6.39	3
NF	O1-10	6.27	1
NG	O1-11	6.28	1
NH	O0-08	6.8	1


ZESTAWIENIE STALI

Poz.	Ø [mm]	Kształt ISO 3766, wymiary [cm]	Długość [m]	Liczba [szt.]	Elem.	Ø6 [m]	Ø10 [m]	Ø12 [m]	Ø14 [m]
1	10	21: a=19 b=99 c=19	133	4	N-O0-1		5,32		
2	6	51: a=13 b=20	80	178	N-O0-1	142,40			
3	10	21: a=19 b=144 c=19	178	8	N-O0-1		14,24		
4	10	21: a=18 b=154 c=18	186	4	N-O0-0		7,44		
5	6	51: a=13 b=19	78	11	N-O0-0	8,58			
6	10	21: a=19 b=154 c=19	188	41	N-O0-1		77,08		
7	12	21: a=19 b=154 c=19	188	6	N-O0-1			11,28	
8	14	21: a=19 b=154 c=19	187	2	N-O1-1				3,74
9	10	21: a=19 b=164 c=19	198	4	N-O0-0		7,92		
Długość całkowita [m]						151,0	112,0	11,3	3,7
Masa jednostkowa [kg/m]						0,222	0,617	0,888	1,208
Masa [kg]						33,5	69,1	10,0	4,5
RAZEM stal B500SP [kg]									117,1

O0-10, O0-13, O0-06, O0-15, O0-14, O1-10, O1-11, O0-08: beton C25/30, XC1, otulina strzemion c_nom = 25 mm (tabl. 4.4N + NA).

OBJAŚNIENIA I UWAGI

- Wymiary w cm (mm w indeksie górnym, np. 24^o = 24,5 cm), rzędne w m względem ±0,000 = 101,650 m n.p.m. (PL-EVRF2007-NH).
- Belki: pręty dolne i górne z odgięciami 90° w strefach podporowych (zakotwienie ≥ l_{bd} od lica podpory — PN-EN 1992-1-1 9.2.1.4), strzemiona zamknięte z hakami 135° (8.5, rys. 8.5), pierwsze strzemie 5 cm od lica podpory, rozstaw wg obliczeń (6.2.3), s.s. min(0,75 d; 400 mm) (9.6N).
- Przekrój A-A — w środku rozpiętości; długości prętów l — długości rozwinięcia (wymiary zewnętrzne, odliczenie gięcia wg PN-EN ISO 3766).
- Bełtonowanie: beton wg PN-EN 206+A2 i PN-B-06265 (klasa, ekspozycja, D_{max} 16 mm, konsystencja S3); pielęgnacja ≥ 7 dni (klasa pielęgnacji 2 — PN-EN 13670 p. 8.5); przerwy robocze wyłącznie w miejscach uzgodnionych z projektantem.
- Rozszalowanie i usunięcie podpór: płyty i belki po uzyskaniu ≥ 70 % f_{ck} (PN-EN 13670 p. 5.6 i 8.5), wsporniki — nie wcześniej niż po 28 dniach i po wykonaniu elementów dociągających zaplecze; podpory wtórne do 28 dni.
- Nadproża pogrupowano w typy (jednakowy przekrój, długość i zbrojenie z obliczeń); liczby sztuk w zestawieniu — łącznie dla wszystkich nadproży typu.
- Rysunek wygenerowany automatycznie z modelu /home/user/aihouse/model/budynek.yaml (wersja 1.0, 2026-09-25) — generatory lamela.views.

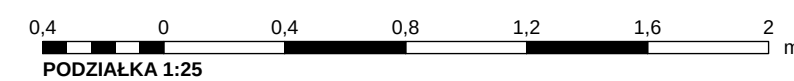

REW.	OPIS ZMIANY			DATA	
0	Wydanie — rysunek wygenerowany z modelu			2026-09-25	
PRACOWNIA PROJEKTOWA PRACOWNIA PROJEKTOWA — nazwa do uzupełnienia adres pracowni do uzupełnienia			STADIUM PT	BRANŻA KONSTRUKCJA (BO)	
INWESTOR (do uzupełnienia)					
OBIEKT / NAZWA ZAMIERZENIA BUDOWLANEGO Budynek mieszkalny jednorodzinny wolnostojący „Dom LAMELA”					
ADRES / LOKALIZACJA (NR DZIAŁKI, OBRĘB, JEDN. EWIDENCYJNA) ul. Lipowa (fikcyjna), dz. nr ewid. 123/4, obręb 0005 Przykładowo, gm. Przykładowo (fikcyjna)				KAT. OBIEKTU I	
FUNKCJA		IMIĘ I NAZWISKO	SPECJALNOŚĆ, NR UPRAWNIENIEŃ	DATA	PODPIS
Projektant					
Projektant (wsp.)					
Sprawdzający					
Opracował					
TYTUŁ RYSUNKU ZBROJENIE NADPROŻY (1)					
SKALA 1:25	FORMAT A3×3	DATA WYDANIA 2026-09-25	RODZAJ DOK. rysunek zbrojenia	NR RYSUNKU PT-BO-18	ARKUSZ 18/21
					REW. 0