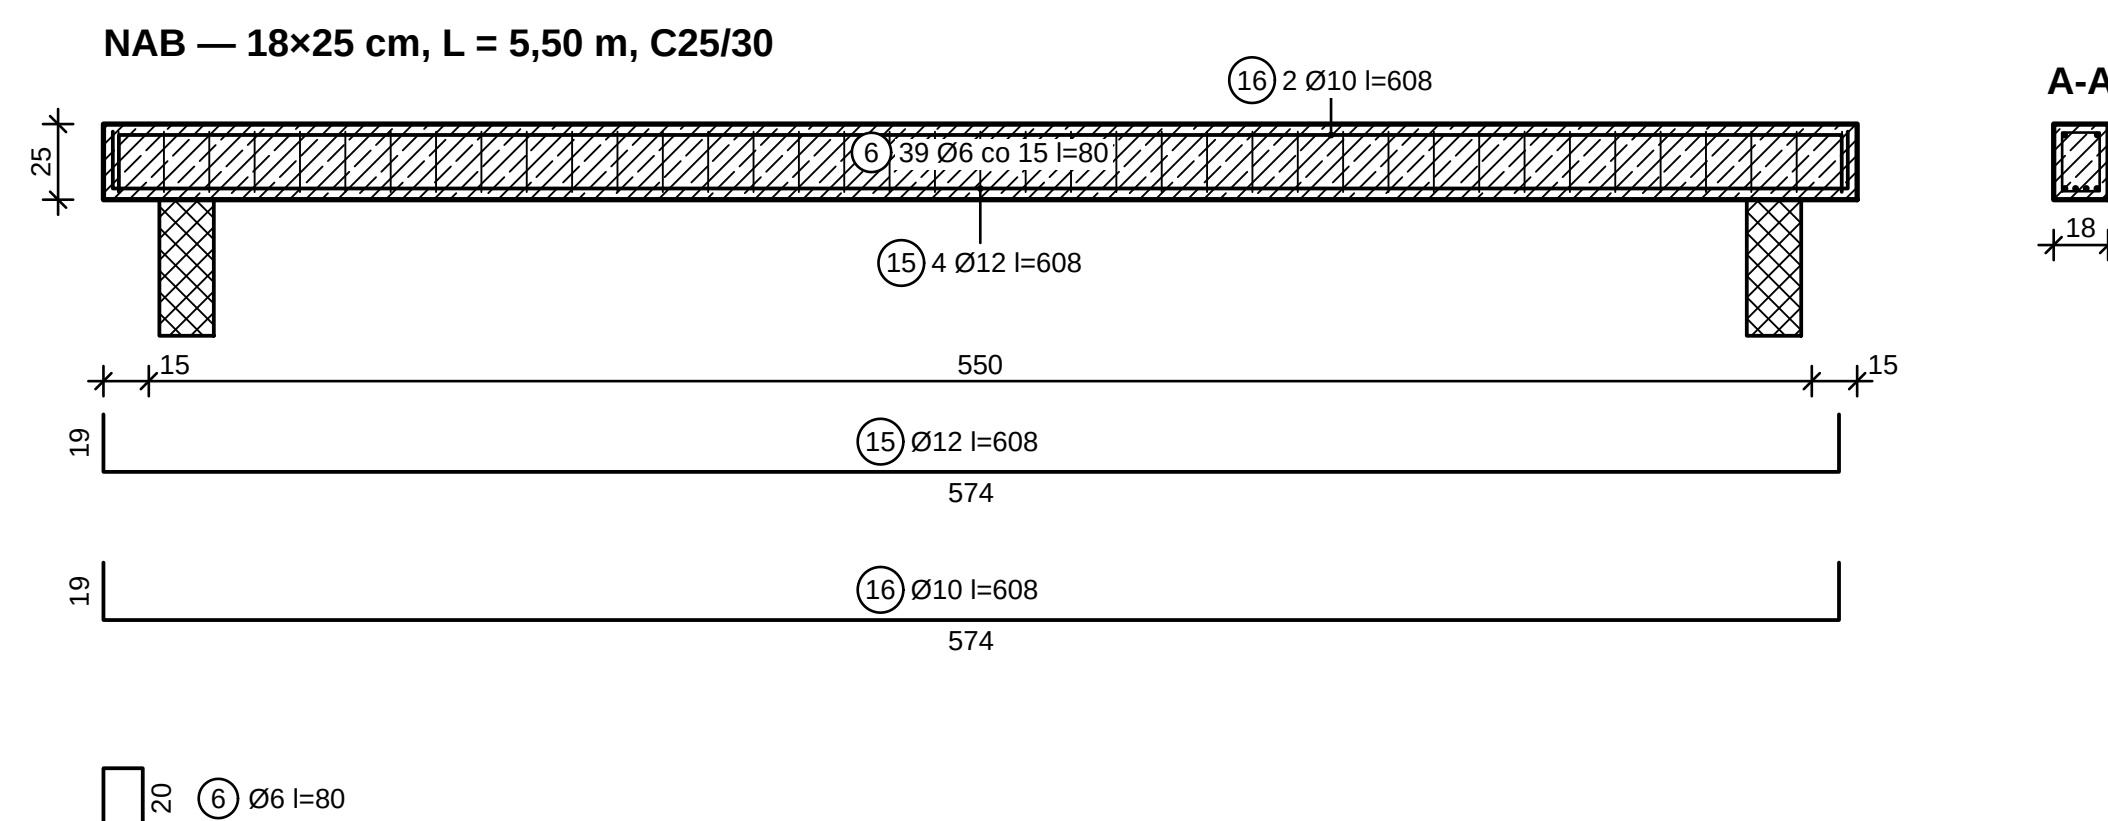
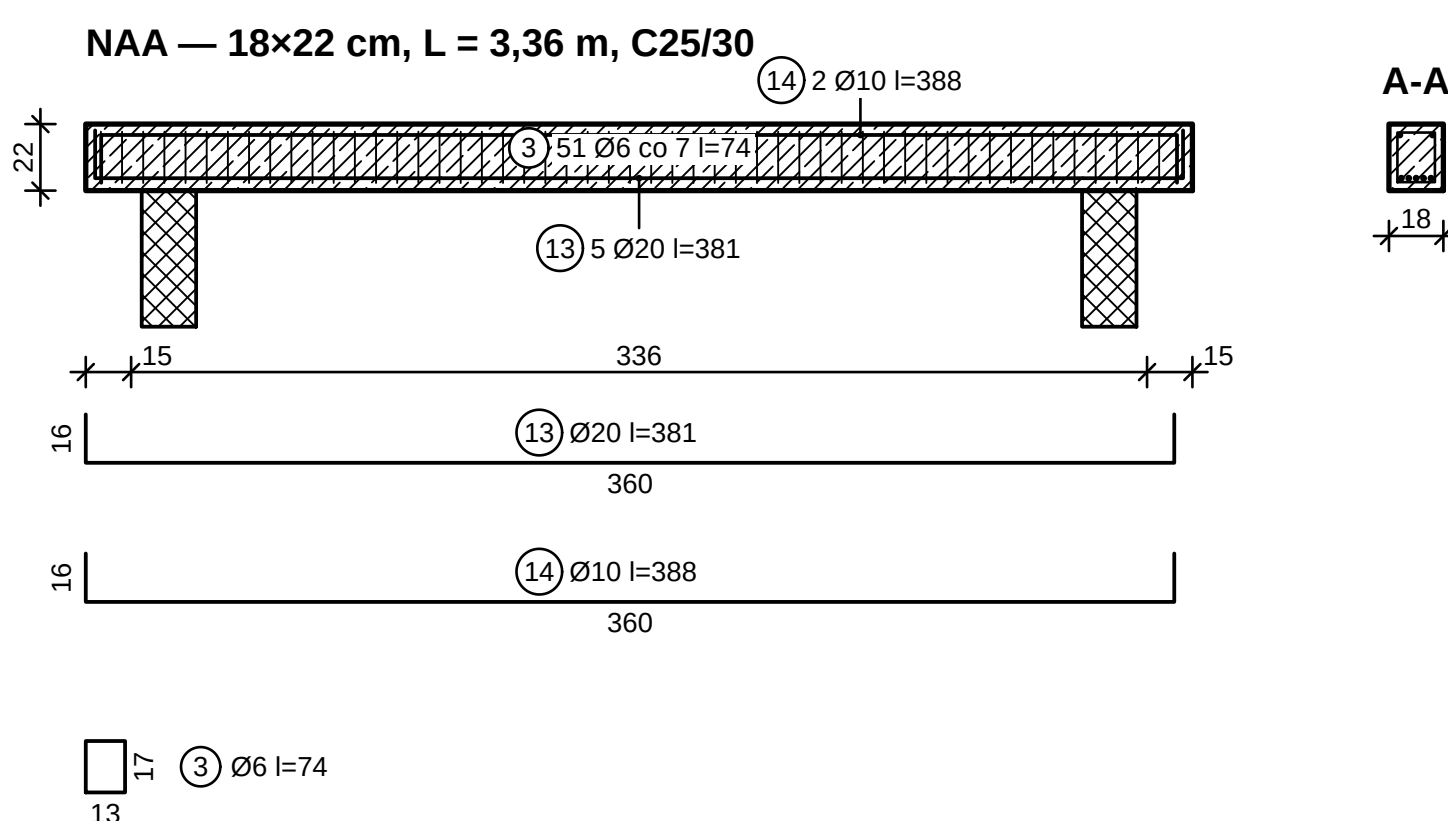
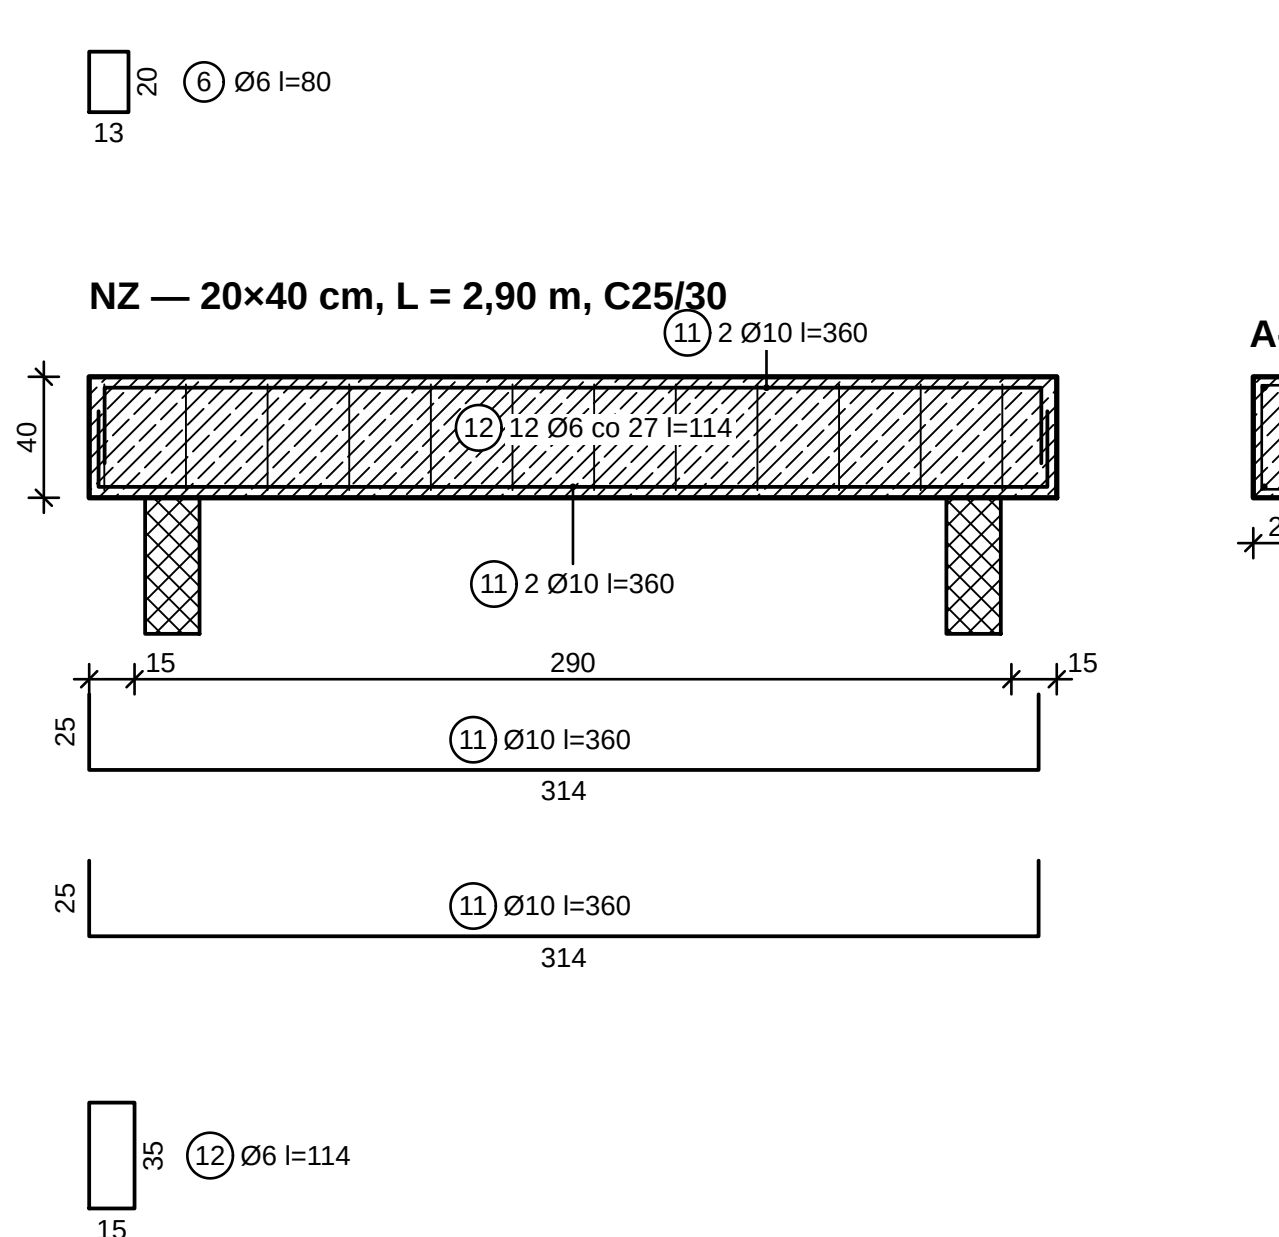
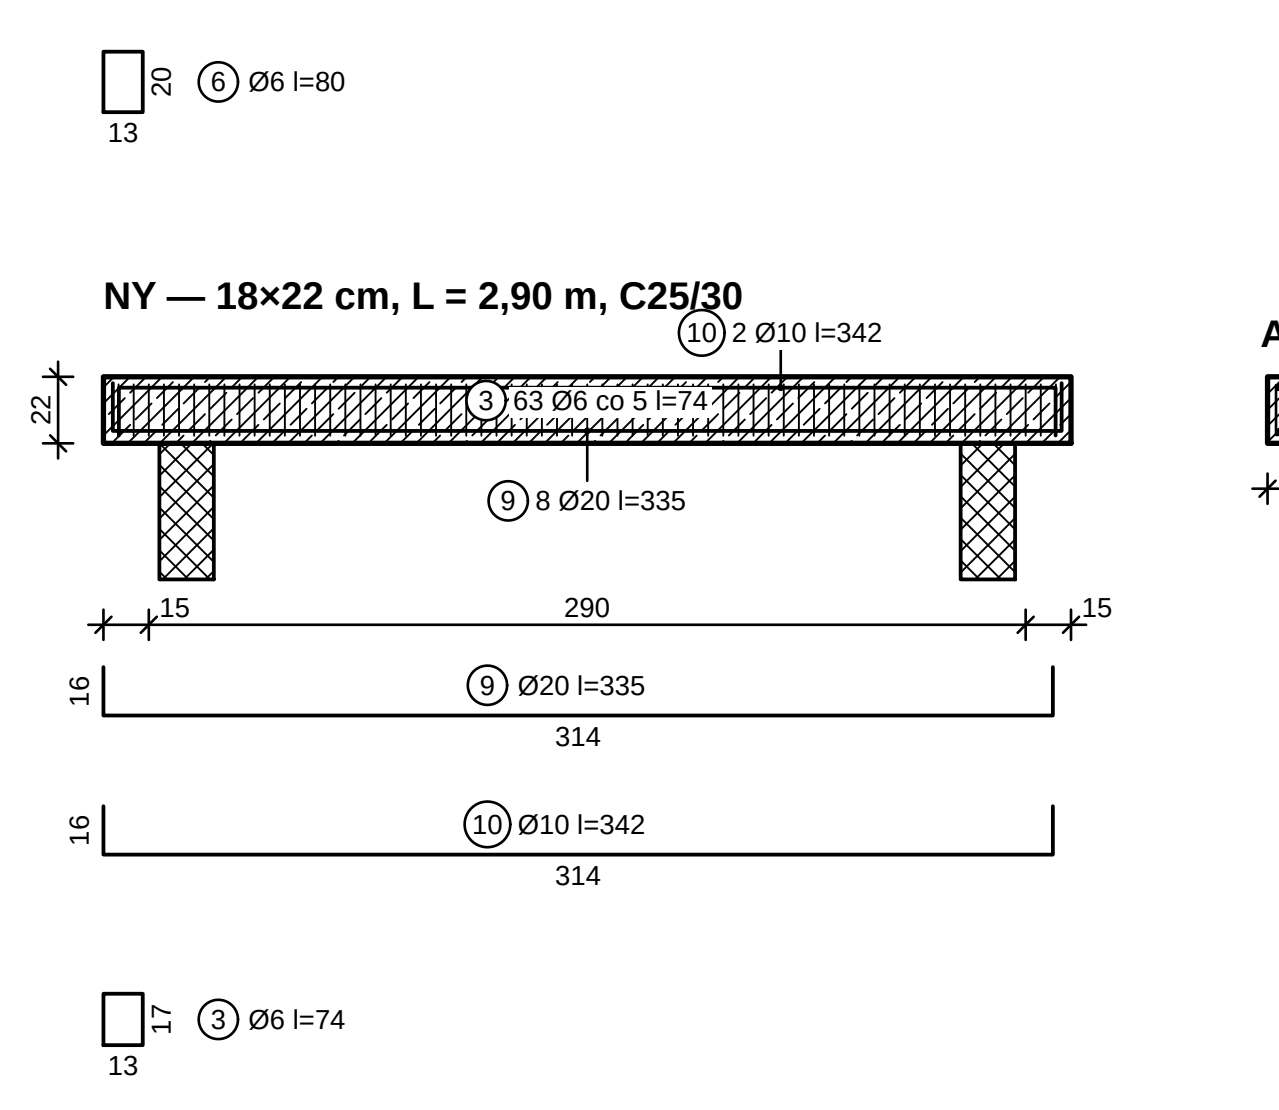
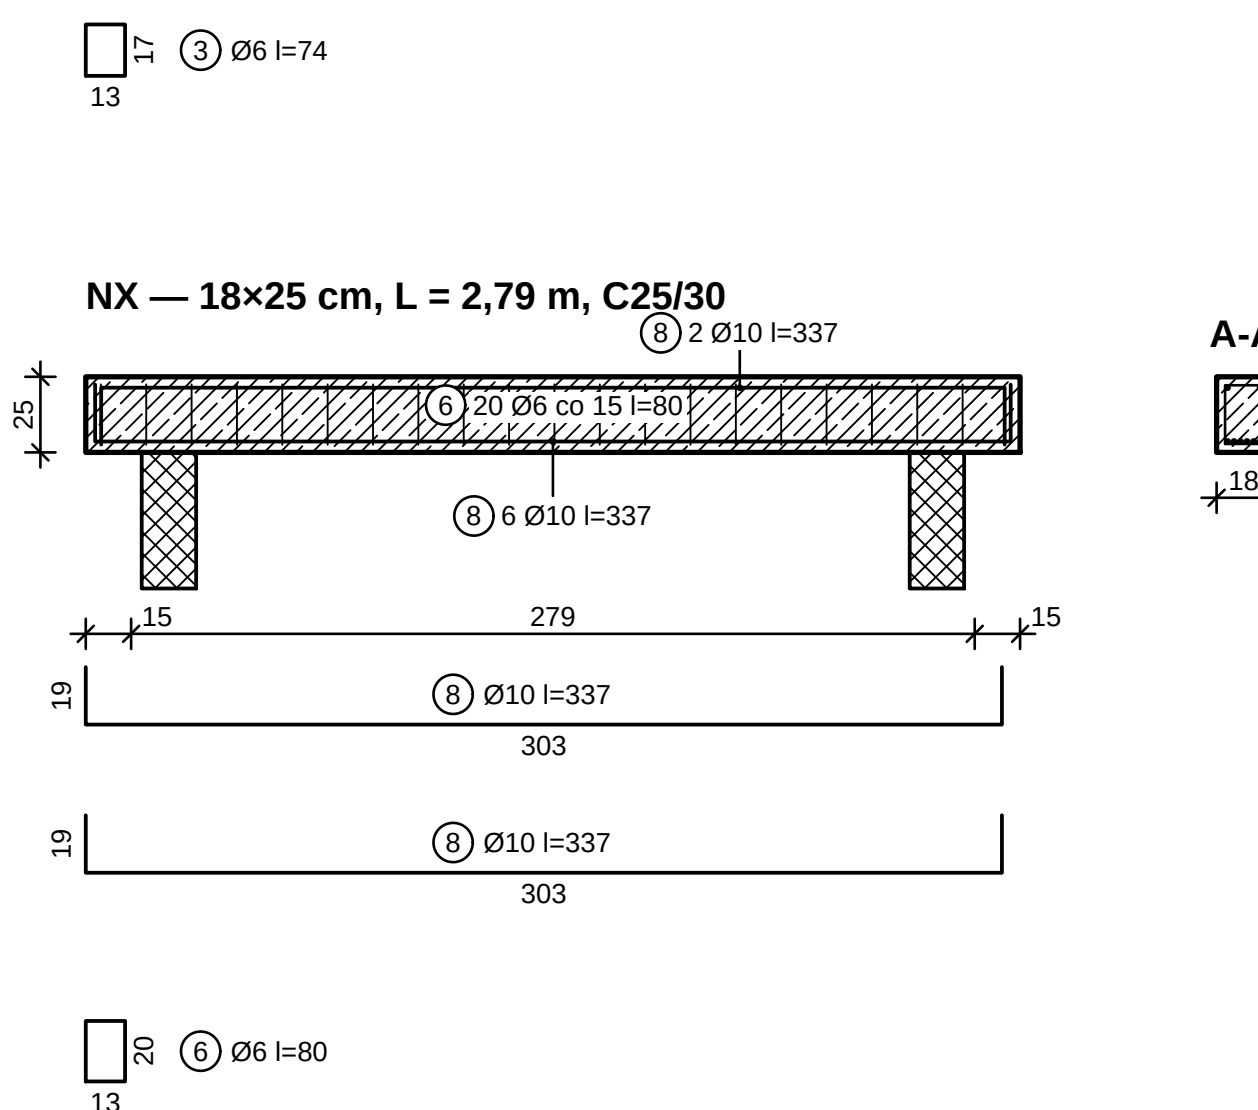
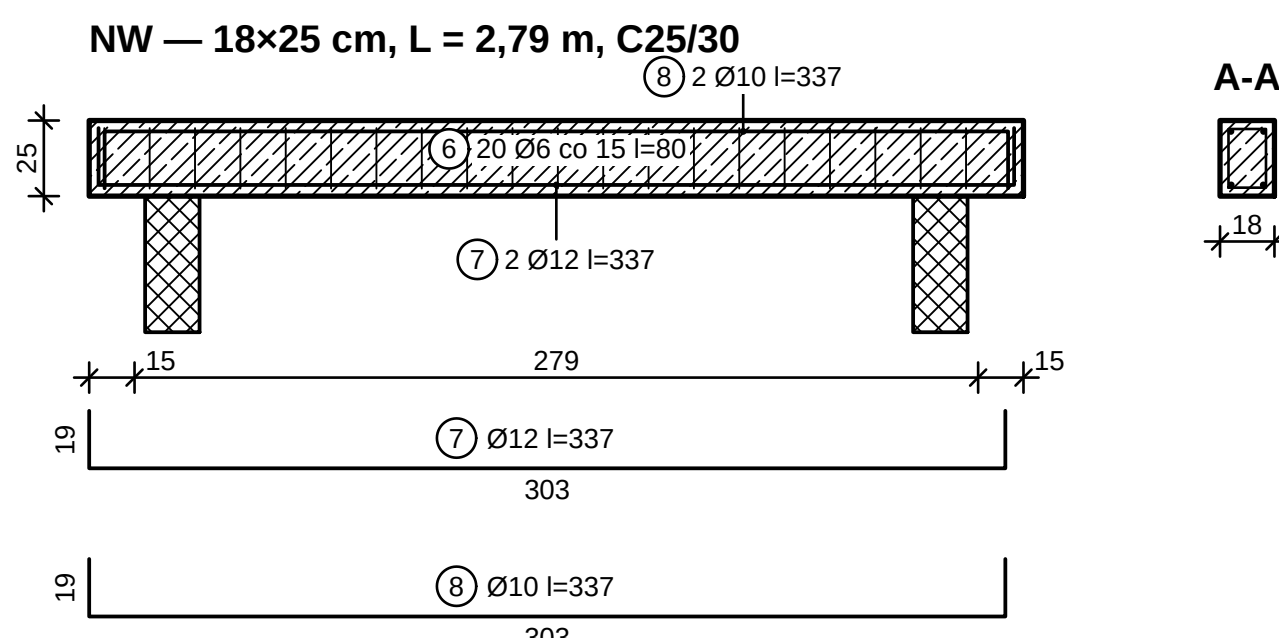
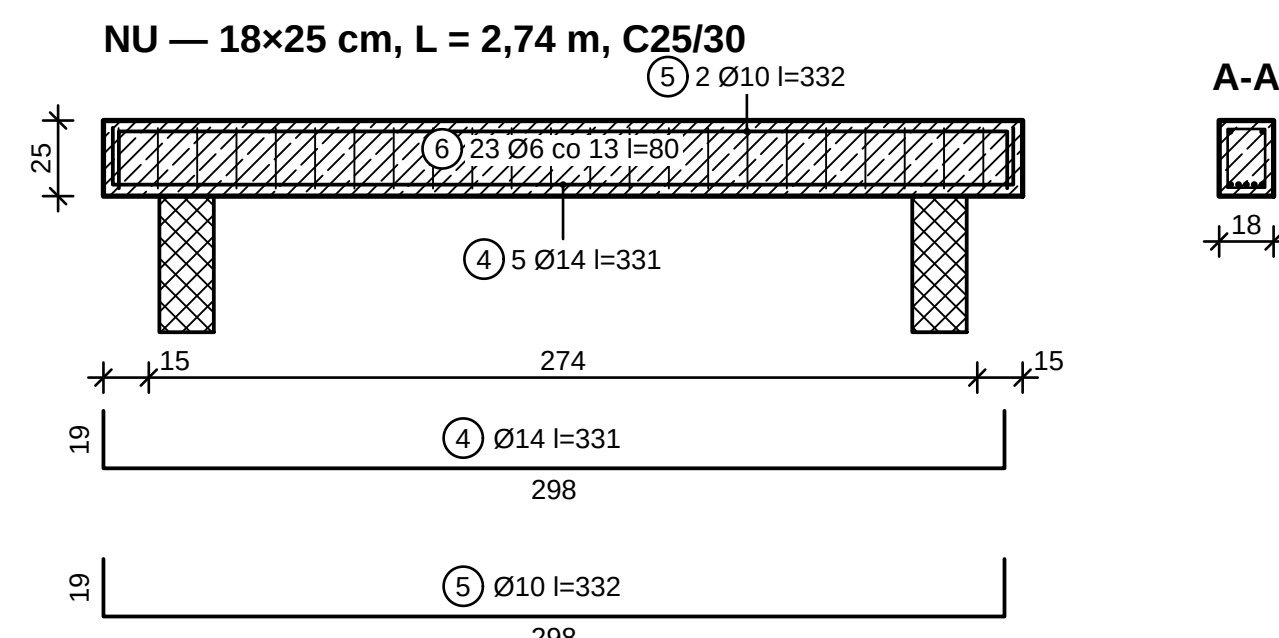
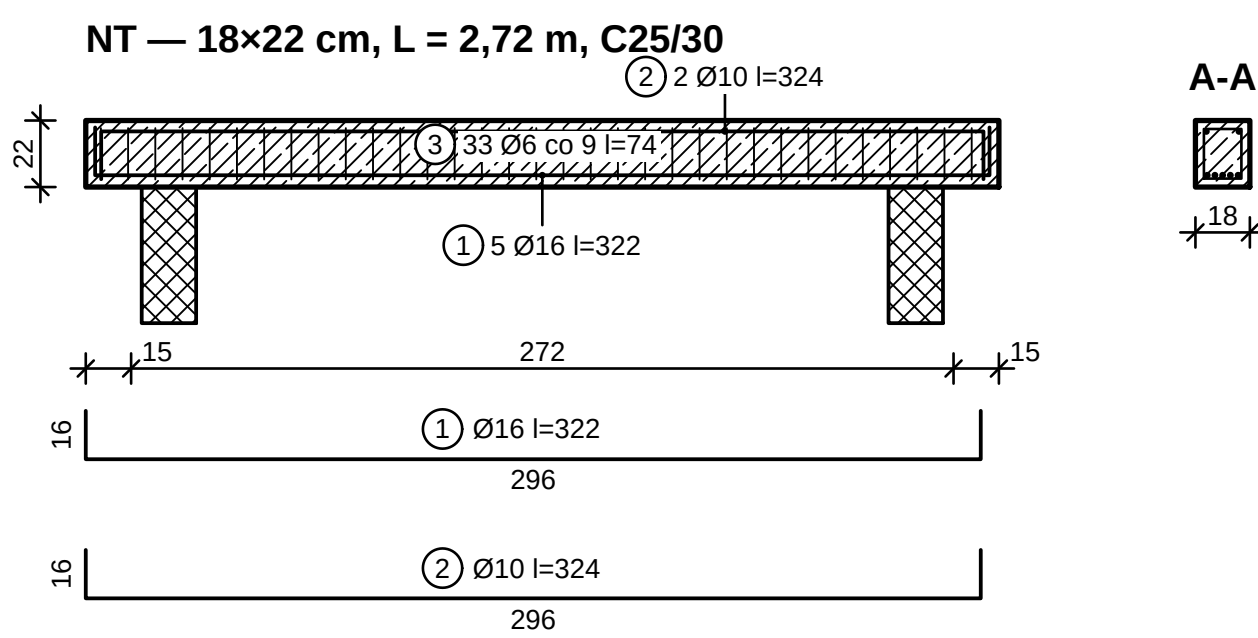
 
 
 
 
 
 
 
 
 
 
 
 
 
 
 
 


**ZBROJENIE NADPROŻY NT, NU, NW, NX, NY, NZ, NAA, NAB** 1:25


TYPY NADPROŻY — OTWORY I POZYCJE OBLICZEŃ				
	Otwory		Poz. obl.	Szt.
Typ	00-03	6.3		1
NU	01-13	6.30		1
NV	01-14	6.31		1
NX	01-01	6.20		1
NY	00-11	6.11		1
NZ	02-04	6.55		1
NAB	00-05	6.5		1
NAB	00-07	6.7		1

ZESTAWIENIE STALI											
Poz.	Kształt ISO 3766, wymiar [mm]		Drug.	Liczba [szt.]	Elem.	Ø6 [mm]	Ø10 [mm]	Ø12 [mm]	Ø14 [mm]	Ø16 [mm]	Ø20 [mm]
1	16	 21: a=16 b=296 c=16	322	5	N-O-00					16,10	
2	10	 21: a=10 b=296 c=16	324	2	N-O-00		6,48				
3	6	 51: a=6 b=137 c=17	74	149	N-O-11	110,26					
4	14	 21: a=14 b=299 c=19	331	5	N-O-11				16,55		
5	10	 21: a=10 b=298 c=19	332	2	N-O-11		6,64				
6	6	 51: a=6 b=20 c=20	80	105	N-O-11	84,00					
7	12	 21: a=12 b=303 c=19	337	2	N-O-11			6,74			
8	10	 21: a=10 b=305 c=19	337	10	N-O-11		33,70				
9	20	 21: a=20 b=314 c=16	335	8	N-O-01						26,80
10	10	 21: a=10 b=314 c=16	342	4	N-O-01		6,84				
11	10	 21: a=10 b=314 c=25	360	4	N-O-20		14,40				
12	6	 51: a=6 b=35 c=35	114	13	N-O-20	14,82					
13	20	 21: a=20 b=360 c=16	381	5	N-O-00						19,05
14	10	 21: a=10 b=360 c=16	388	2	N-O-00		7,16				
15	12	 21: a=12 b=574 c=19	608	4	N-O-00		12,16	24,32			
16	10	 21: a=10 b=574 c=19	608	2	N-O-00						
Dopuszcz. ciężarowna [kg]						209,1	38,0	31,1	16,6	16,1	45,3
Masa jednostkowa [kg/mm]						0,222	0,017	0,089	1,298	1,578	2,466
Masa [kg]						46,4	54,2	27,6	20,0	25,4	133,3
RAZEM stal 8500SP [kg]											286,1

O0-03, O1-13, O1-14, O1-01, O0-11, O2-04, O0-05, O0-07: beton C25/30, XC1, otulina strzemion $c_{nom} = 25$ mm (tabl. 4.4N + NA)

OBJAŚNIENIA I UWAGI

- [illegible]

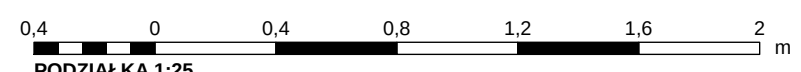

REW. 0	OPIS ZMIANY Wydanie — rysunek wygenerowany z modelu				DATA 2026-09-25	
PRACOWNIA PROJEKTOWA PRACOWNIA PROJEKTOWA — nazwa do uzupełnienia adres pracowni do uzupełnienia				STADIUM PT	BRANŻA KONSTRUKCJA (BO)	
INWESTOR (dł uzupełnienia) BUDOWA ZAMIERZANA BUDOWLANEGO Budynki mieszkalne jednorodzinnej wolnostojący „Dom LAMELA”						
ADRES / LOKALIZACJA (NR DZIAŁKI, OBRĘB. JEDN. EWIDENCYJNA) ul. Lipowa (Iłkocyna), dz. nr ewid. 1234, obręb 005 Przykładowo, gm. Przykładowo (Iłkocyna)					KAT. OBIEKTU I	
FUNKCJA		IMIĘ I NAZWISKO	SPECJALNOŚĆ, NR UPRAWNIENI	DATA	PODPIS	
Projektant						
Projektant (wsp.)						
Sprawdzający						
Opracował						
TYTUŁ RYSUNKU ZBUDOWANIE NADPROŻY (3)						
SKALA 1:25	FORMAT A2×3	DATA WYDANIA 2026-09-25	RODZAJ DOK. rysunek zbrojenia	NR RYSUNKU PT-BO-20	ARKUSZ 20/21	REW. 0