

TOM PRÓBNY — SILNIK RYSUNKOWY

Lp.	Nr rys.	Tytuł rysunku	Skala	Format
1	DEMO-01	RZUT PRÓBNY — FRAGMENT PARTERU	1:50	A3
2	DEMO-02	PRZEKRÓJ PRÓBNY A-A	1:50	A3
3	DEMO-03	TABLICA OZNACZEŃ: MATERIAŁY I SYMBOLE	bez skali	A2

PRACOWNIA PROJEKTOWA

STADIUM

BRANŻA

INWESTOR

OBIEKT / NAZWA ZAMIERZENIA BUDOWLANEGO

ADRES / LOKALIZACJA (NR DZIAŁKI, OBRĘB, JEDN. EWIDENCYJNA)


KAT. OBIEKTU

FUNKCJA	IMIĘ I NAZWISKO	SPECJALNOŚĆ, NR UPRAWNIEŃ	DATA	PODPIS
Projektant				
Projektant (wsp.)				
Sprawdzający				
Opracował				

TYTUŁ RYSUNKU

SPIS RYSUNKÓW

SKALA —	FORMAT A4	DATA WYDANIA	RODZAJ DOK.	NR RYSUNKU 00	ARKUSZ	REW.
------------	--------------	--------------	-------------	------------------	--------	------

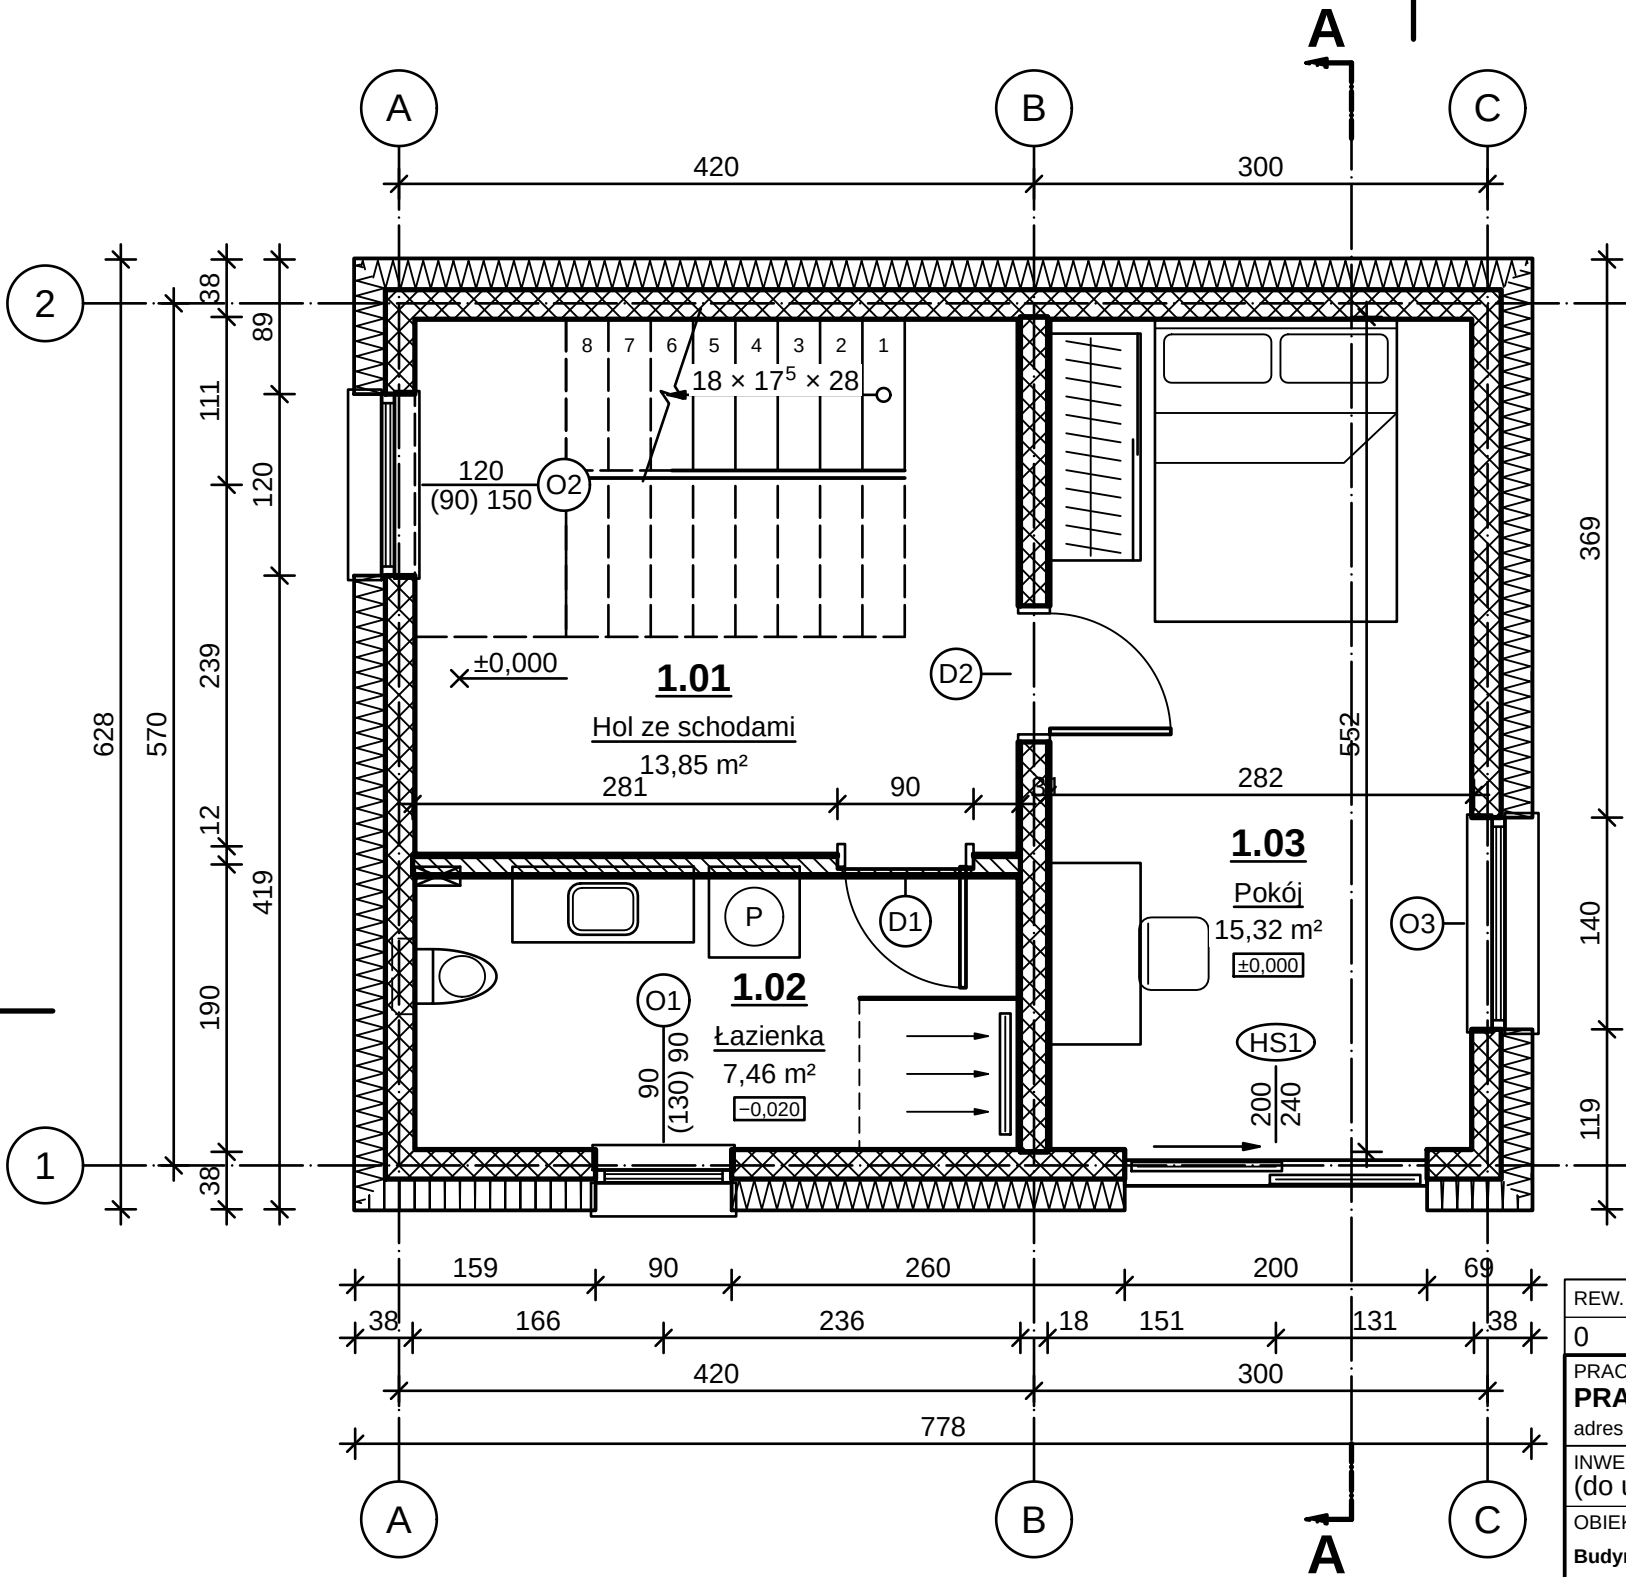

RZUT PARTERU — FRAGMENT 1:50

ZESTAWIENIE POMIESZCZEŃ

Nr	Nazwa pomieszczenia	Posadzka	Pow. [m²]
1.01	Hol ze schodami	gres	13,85
1.02	Łazienka	gres	7,46
1.03	Pokój	deska	15,32
RAZEM			36,62

ZESTAWIENIE OTWORÓW (w świetle muru)


Symbol	Szer. [cm]	Wys. [cm]	Parapet [cm]
O1	90	90	130
HS1	200	240	0
O2	120	150	90
O3	140	150	85
D1	90	205	—
D2	90	205	—

OZNACZENIA MATERIAŁÓW

	Mur z bloczków wapienno-piaskowych (silikatowych) — kratka ukośna 45°/135°		Izolacja termiczna twarda (EPS) — zygzak „VVV”
	Mur z cegieł i pustaków ceramicznych — 45° ciągłe		Tynk, zaprawa — kropki nieregularne

OBJAŚNIENIA I UWAGI


- Wymiary w cm (mm w indeksie górnym, np. 24⁵ = 24,5 cm), rzędne w m. ±0,000 = posadzka parteru = 101,650 m n.p.m. (PL-EVRF2007-NH).
- Otwory: licznik — szerokość, mianownik — wysokość w świetle muru, w nawiasie wysokość parapetu.
- Oznaczenia mur silikatowy i EPS/wełna — przyjęte (brak w PN-B-01030), objaśnione w legendzie.
- Rysunek testowy silnika — dane nie stanowią projektu.

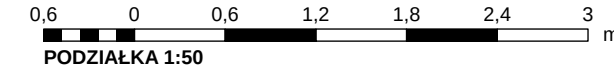


PODZIAŁKA 1:50

REW.	OPIS ZMIANY			DATA	
0	Wydanie do weryfikacji silnika rysunkowego			2026-09-25	
PRACOWNIA PROJEKTOWA PRACOWNIA PROJEKTOWA — nazwa do uzupełnienia adres pracowni do uzupełnienia			STADIUM PB	BRANŻA ARCHITEKTURA (AR)	
INWESTOR (do uzupełnienia)					
OBIEKT / NAZWA ZAMIERZENIA BUDOWLANEGO Budynek mieszkalny jednorodzinny „Dom LAMELA” — PRÓBA SILNIKA RYSUNKOWEGO (rysunek testowy)					
ADRES / LOKALIZACJA (NR DZIAŁKI, OBRĘB, JEDN. EWIDENCYJNA) dz. nr ewid. 123/4, obręb 0005 Przykładowo, jedn. ewid. Przykładowo (dane fikcyjne)				KAT. OBIEKTU I	
FUNKCJA	IMIĘ I NAZWISKO		SPECJALNOŚĆ, NR UPRAWNIENI	DATA	PODPIS
Projektant					
Projektant (wsp.)					
Sprawdzający					
Opracował					
TYTUŁ RYSUNKU RZUT PRÓBNY — FRAGMENT PARTERU					
SKALA 1:50	FORMAT A3	DATA WYDANIA 2026-09-25	RODZAJ DOK. rzut	NR RYSUNKU DEMO-01	ARKUSZ 1/3
					REW. 0

PRZEKRÓJ A-A (FRAGMENT) 1:50

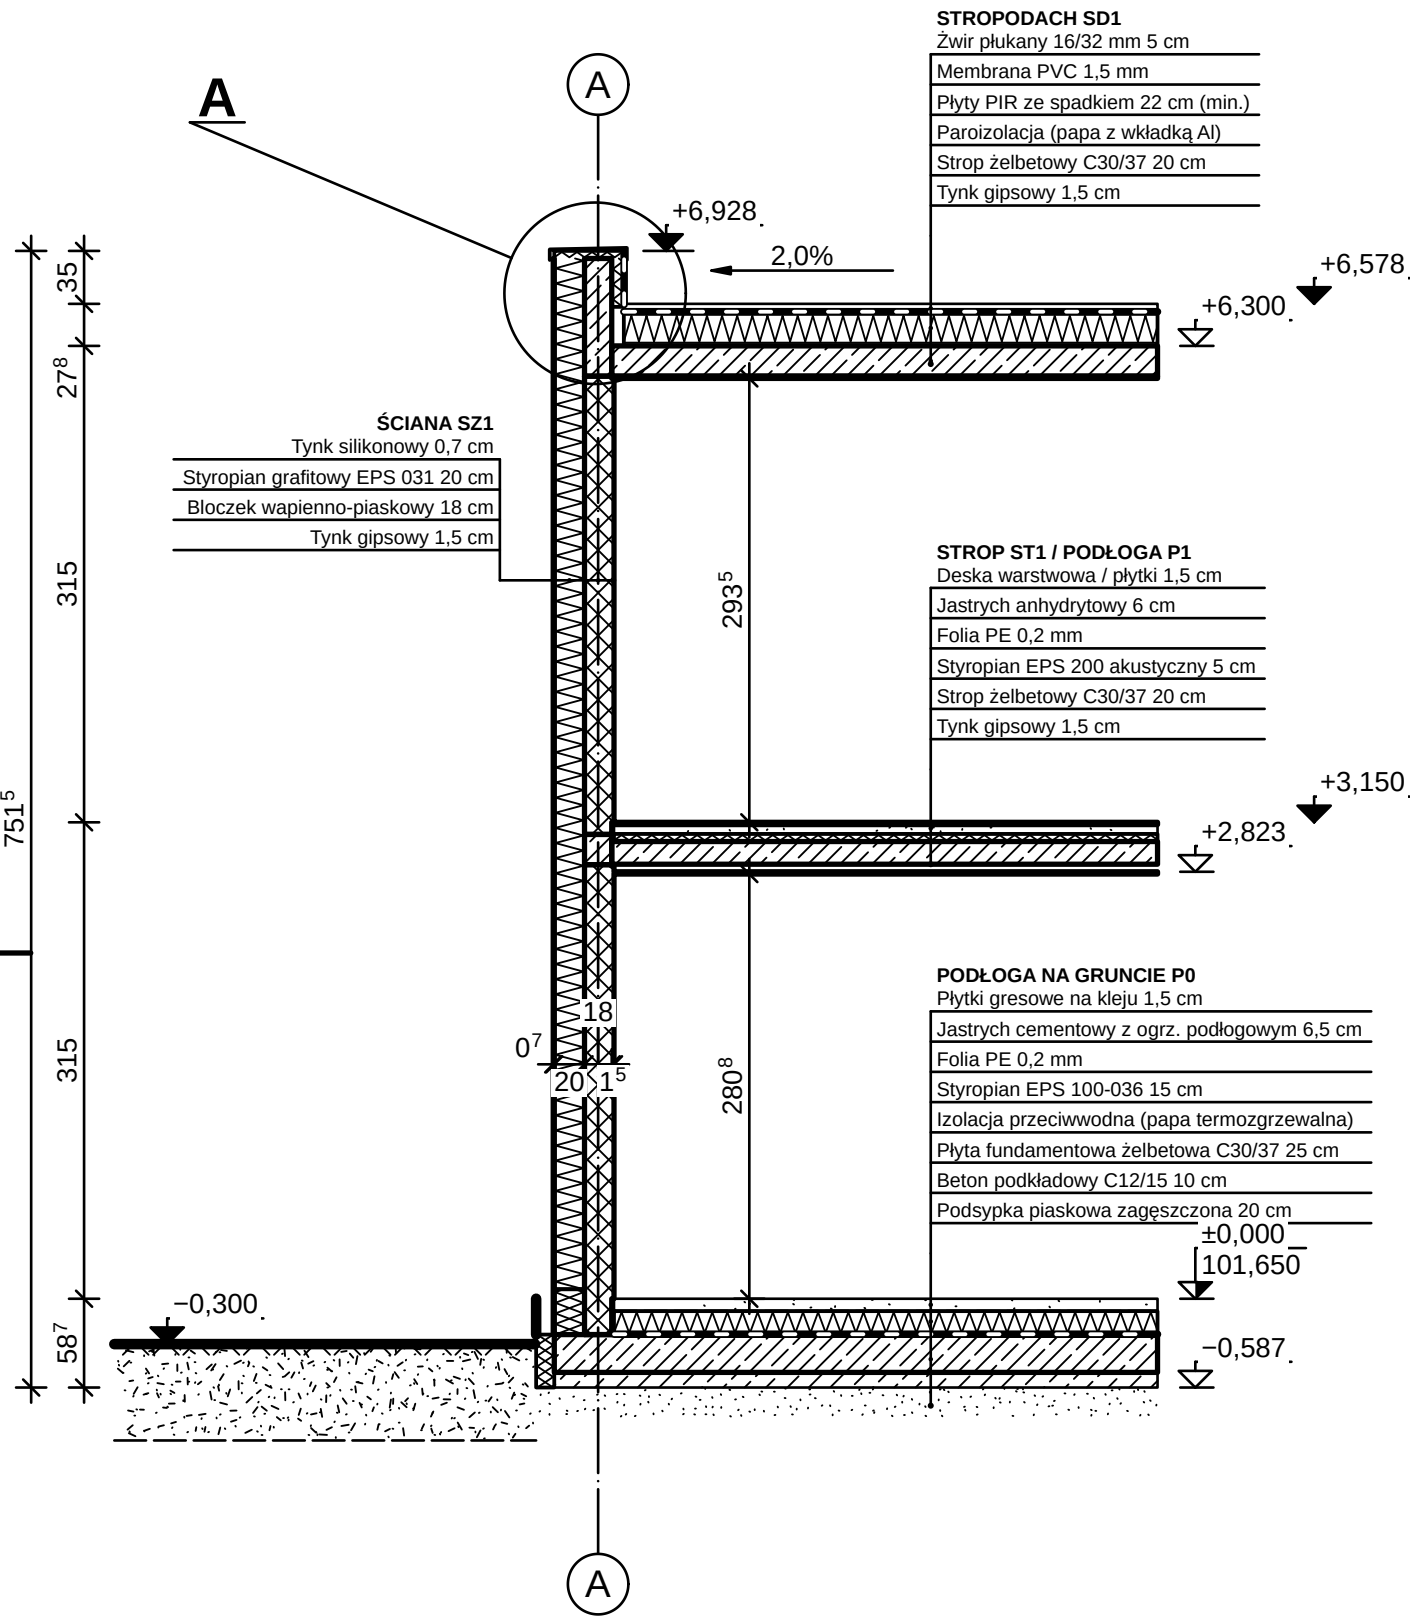

DETAL A — ATTYKA 1:20

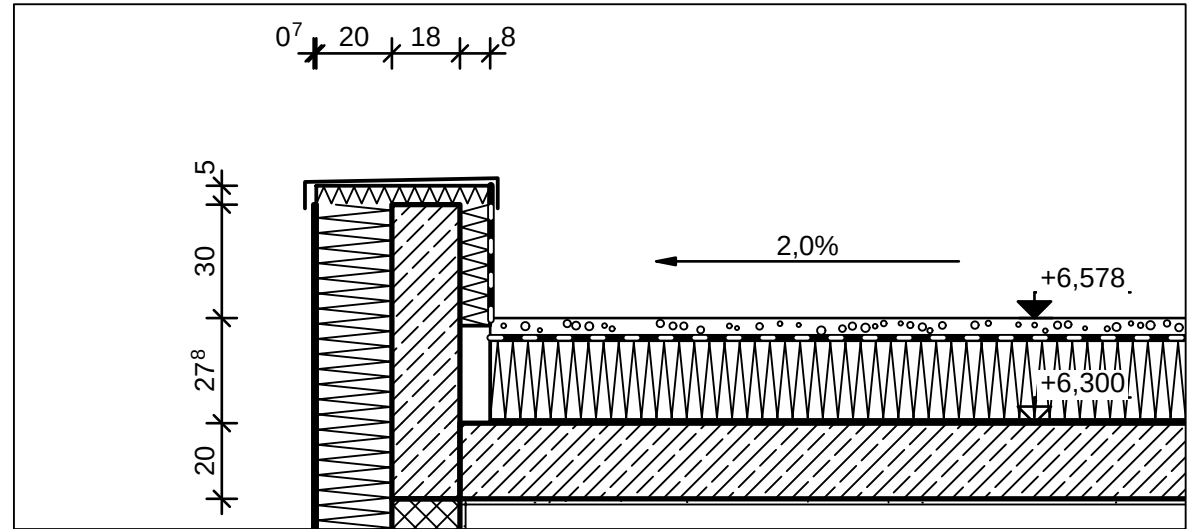


OZNACZENIA MATERIAŁÓW

	Beton zbrojony (żelbet) — 45° na przemian ciągle i przerywane		Paroizolacja (folia PE) — linia kreskowa cienka 3/1 po ciepłej stronie
	Beton niezbrojony, kamień — 45° przerywane		Jastrych (wylewka) cementowy/anhydrytowy — kropki
	Mur z bloczków wapienno-piaskowych (silikatowych) — kratka ukośna 45°/135°		Tynk, zaprawa — kropki nieregularne
	Izolacja termiczna twarda (EPS) — zygzak „VVV”		Piasek, podsypka piaskowa
	Izolacja termiczna twarda (XPS) — zygzak podwójny		Nasyp, zasypka (grunt nasypowy)
	Izolacja termiczna twarda (PIR/PUR) — zygzak z okładzinami		Żwir, tłuczeń
	Izolacja przeciwwodna (papa, membrana) — pas czarno-biały		Grunt rodzimy (powierzchnia gruntu w przekroju)

OBJAŚNIENIA I UWAGI

- Wymiary w cm (mm w indeksie górnym), rzędne w m względem $\pm 0,000 = 101,650$ m n.p.m.
- Rzędne: trójkąt zaczerpiony — wykończenie, niezaczerpiony — konstrukcja, w połowie zaczerpiony — poziom zerowy z rzędną bezwzględną (PN-B-01025).
- Rysunek testowy silnika — dane nie stanowią projektu.

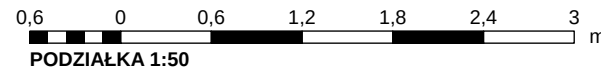

PRACOWNIA PROJEKTOWA PRACOWNIA PROJEKTOWA — nazwa do uzupełnienia adres pracowni do uzupełnienia			STADIUM PB	BRANŻA ARCHITEKTURA (AR)
INWESTOR (do uzupełnienia)				
OBIEKT / NAZWA ZAMIERZENIA BUDOWLANEGO Budynek mieszkalny jednorodzinny „Dom LAMELA” — PRÓBA SILNIKA RYSUNKOWEGO (rysunek testowy)				
ADRES / LOKALIZACJA (NR DZIAŁKI, OBRĘB, JEDN. EWIDENCYJNA) dz. nr ewid. 123/4, obręb 0005 Przykładowo, jedn. ewid. Przykładowo (dane fikcyjne)				KAT. OBIEKTU I
FUNKCJA	IMIĘ I NAZWISKO	SPECJALNOŚĆ, NR UPRAWNIENI	DATA	PODPIS
Projektant				
Projektant (wsp.)				
Sprawdzający				
Opracował				
TYTUŁ RYSUNKU PRZEKRÓJ PRÓBNY A-A				
SKALA 1:50	FORMAT A3	DATA WYDANIA 2026-09-25	RODZAJ DOK. przekrój	NR RYSUNKU DEMO-02
			ARKUSZ 2/3	REW. 0

OZNACZENIA MATERIAŁÓW W PRZEKROJACH (PN-B-01030:2000 + oznaczenia przyjęte)

	Beton zbrojony (żelbet) — 45° na przemian ciągle i przerywane PN-B-01030:2000 poz. 4		Metale (stal, aluminium) — zaciernienie PN-B-01030:2000 poz. 11		Tynk, zaprawa — kropki nieregularne PN-B-01030:2000 poz. 2
	Beton niezbrojony, kamień — 45° przerywane PN-B-01030:2000 poz. 3		Izolacja termiczna miękka (wełna mineralna) — meander „UUU” PN-B-01030:2000 poz. 12 (przypisanie do wełny — konwencja projektu)		Płyta gipsowo-kartonowa oznaczenie przyjęte (odmiana poz. 2)
	Beton lekki — jak beton + grupy kółek PN-B-01030:2000 poz. 5		Izolacja termiczna twarda (EPS) — zygzak „VVV” PN-B-01030:2000 poz. 12 (przypisanie do EPS — konwencja projektu)		Jastrych (wylewka) cementowy/anhydrytowy — kropki PN-B-01030:2000 poz. 2 (zaprawa)
	Beton lekki zbrojony — jak żelbet + grupy kółek PN-B-01030:2000 poz. 6		Izolacja termiczna twarda (XPS) — zygzak podwójny oznaczenie przyjęte (odmiana poz. 12)		Płytki ceramiczne / gres (okładzina) oznaczenie przyjęte
	Beton komórkowy — jak beton lekki (45° przerywane + grupy kółek Ø0,8) oznaczenie przyjęte (PN-B-01030 poz. 5)		Izolacja termiczna twarda (PIR/PUR) — zygzak z okładzinami oznaczenie przyjęte (odmiana poz. 12)		Grunt rodzimy (powierzchnia gruntu w przekroju) PN-B-01030:2000 poz. 1
	Mur z cegieł i pustaków ceramicznych — 45° ciągle PN-B-01030:2000 poz. 7		Izolacja przeciwwodna (papa, membrana) — pas czarno-biały PN-B-01030:2000 poz. 13		Nasyp, zasyпка (grunt nasypowy) oznaczenie przyjęte
	Mur z bloczków wapienno-piaskowych (silikatowych) — kratka ukośna 45°/135° oznaczenie przyjęte (brak w PN-B-01030; R4 pkt 3.8)		Izolacja przeciwwilgociowa (cienka warstwa) — linia bardzo gruba PN-B-01030 poz. 13 / R4 pkt 3.8		Piasek, podsypka piaskowa PN-B-01030:2000 poz. 2 (podsypka)
	Drewno — przekrój prostopadły do włókien PN-B-01030:2000 poz. 8a		Paroizolacja (folia PE) — linia kreskowa cienka 3/1 po ciepłej stronie oznaczenie przyjęte (R4 pkt 3.8)		Żwir, tłuczeń oznaczenie przyjęte
	Drewno — przekrój wzdłuż włókien PN-B-01030:2000 poz. 8b		Membrana paroprzepuszczalna / wiatroizolacja oznaczenie przyjęte		Pospółka (mieszanka piaskowo-żwirowa) oznaczenie przyjęte
	Sklejka PN-B-01030:2000 poz. 9		Szkło i inne materiały przezroczyste PN-B-01030:2000 poz. 14		Ziemia urodzajna (humus) oznaczenie przyjęte
	Płyty drewnopochodne (OSB, MFP, wiórowe) PN-B-01030:2000 poz. 10		Tworzywa sztuczne PN-B-01030:2000 poz. 15		

SYMBOLE GRAFICZNE (PN-B-01025, IEC 60617, praktyka instalacyjna, PN-B-01027)

Strzałka północy 	Oś konstrukcyjna 	Oznaczenie przekroju 	Oznaczenie pomieszczenia 	Symbol stolarki 	Rzędna — rzut (X / ramka) 	Rzędne — przekrój (±0,00 / wyk. / konstr.) 	Spadek / pochylnia
Wejście do budynku (±0,00 / poniżej) 	Odbośnik szczegółu 	Wymiar (cm, mm w indeksie) 	Otwór w stropie / szacht 	Drzwi rozwierane 	Drzwi przesuwne HS 	Okno (rama, szyba, parapety) 	Schody — bieg z linią cięcia
11-13-04 gniazdo z st. ochr. / ×2 / IP44 / 3~ 	11-14-03/-04/-06 łącznik 1-b. / 2-b. / schodowy 	11-15-03 oprawa / -02 kinkiet / ścienna / -04 liniowa 	11-12-07 rozdzielnica / puszka / 02-15-01 uziemienie 	Czujnik ruchu / dzwonek / wideodomofon 	11-13-09 gniazdo tele (RJ45, TV) / SPD 	Pion / zawór / zawór zwrotny 	Wodomierz / filtr / pompa
Przewody: Wz / Wc / Cyrk / Ks 	Rozdzielnik / zasobnik / pompa ciepła 	Czyszczak / wpust / rewizja 	Kratka / anemostat N / W 	Czerpnia ODA / wyrzutnia EHA 	Rekuperator (ODA / EHA / ETA / SUP) 	Grzejnik / ogrzewanie podłogowe 	Drzewo istn. / proj. / do usunięcia
Drzewo iglaste / krzew / żywopłot 	Trawnik / nawierzchnia drobna / duża 	Słup / punkt świetlny / hydrant / studz. 	Złącze ZK / studzienka wodomierzowa SW 	Granica działki (narożniki A, B, C) 	Linia zabudowy nieprzekr. / obowiązująca 	Linia rozgraniczająca / ogrodzenie 	Sieci: woda / Ks / Kd
Sieci: e / t / g / c 	Warstwiec istn. / proj., pkt wysokościowe 	Budynek (±0,00=..., III) / wejście / brama 					

RODZAJE I GRUBOŚCI LINII (PN-EN ISO 128-2, grupy linii wg podziałki)

Próbka	Rodzaj linii	Zastosowanie	1:20	1:50	1:100	1:500
	ciągła bardzo gruba	kontury przekroju bez kreskowania, pręty zbrojeniowe, izolacje przeciwwodne	1,40	1,40	1,00	1,40
	ciągła gruba	kontury elementów konstrukcyjnych w przekroju (z kreskowaniem)	0,70	0,70	0,50	0,70
	ciągła średnia	warstwy nienośne w przekroju, stolarka, krawędzie widoczne bliskie	0,50	0,50	0,35	0,35
	ciągła cienka	wymiary, linie pomocnicze, odnośniki, wyposażenie, krawędzie widoczne	0,35	0,35	0,25	0,25
	ciągła bardzo cienka	kreskowanie materiałów, meble	0,25	0,25	0,18	0,18
	kreskowa cienka	krawędzie niewidoczne, elementy nad płaszczyzną cięcia	0,35	0,35	0,25	0,25
	punktowa cienka	osie konstrukcyjne, osie symetrii	0,35	0,35	0,25	0,25
	punktowa gruba (krótka)	ślad płaszczyzny przekroju (końce i załamania)	0,70	0,70	0,50	0,70
	dwupunktowa	granice działki, elementy usuwane/projektowane, skrajne położenia	0,70	0,70	0,50	0,70
	kropkowa	elementy pomocnicze, zakres robót	0,35	0,35	0,25	0,25

PISMO (PN-EN ISO 3098; Liberation Sans — metrycznie zgodna z Arial)

h = 1,8 mm ĄĆĘŁŃÓŚŹŹ ąćęłńóśźź 0123456789 ±0,00 –1,20 24⁵
h = 2,5 mm ĄĆĘŁŃÓŚŹŹ ąćęłńóśźź 0123456789 ±0,00 –1,20 24⁵
h = 3,5 mm ĄĆĘŁŃÓŚŹŹ ąćęłńóśźź 0123456789 ±0,00 –1,20 24⁵
h = 5,0 mm ĄĆĘŁŃÓŚŹŹ ąćęłńóśźź 0123456789 ±0,00 –1,20 24⁵

odcinek kontrolny 100 mm (wydruk 1:1)

PRACOWNIA PROJEKTOWA PRACOWNIA PROJEKTOWA — nazwa do uzupełnienia adres pracowni do uzupełnienia			STADIUM PB		BRANŻA WIELOBRANŻOWY	
INWESTOR (do uzupełnienia) OBIEKT / NAZWA ZAMIERZENIA BUDOWLANEGO Budynek mieszkalny jednorodzinny „Dom LAMELA” — PRÓBA SILNIKA RYSUNKOWEGO (rysunek testowy)						
ADRES / LOKALIZACJA (NR DZIAŁKI, OBRĘB, JEDN. EWIDENCYJNA) dz. nr ewid. 123/4, obręb 0005 Przykładowo, jedn. ewid. Przykładowo (dane fikcyjne)						KAT. OBIEKTU I
FUNKCJA	IMIĘ I NAZWISKO	SPECJALNOŚĆ, NR UPRAWNIENI	DATA	PODPIS		
Projektant						
Projektant (wsp.)						
Sprawdzający						
Opracował						
TYTUŁ RYSUNKU TABLICA OZNACZEŃ: MATERIAŁY I SYMBOLE						
SKALA bez skali	FORMAT A2	DATA WYDANIA 2026-09-25	RODZAJ DOK. legenda	NR RYSUNKU DEMO-03	ARKUSZ 3/3	REW. 0