




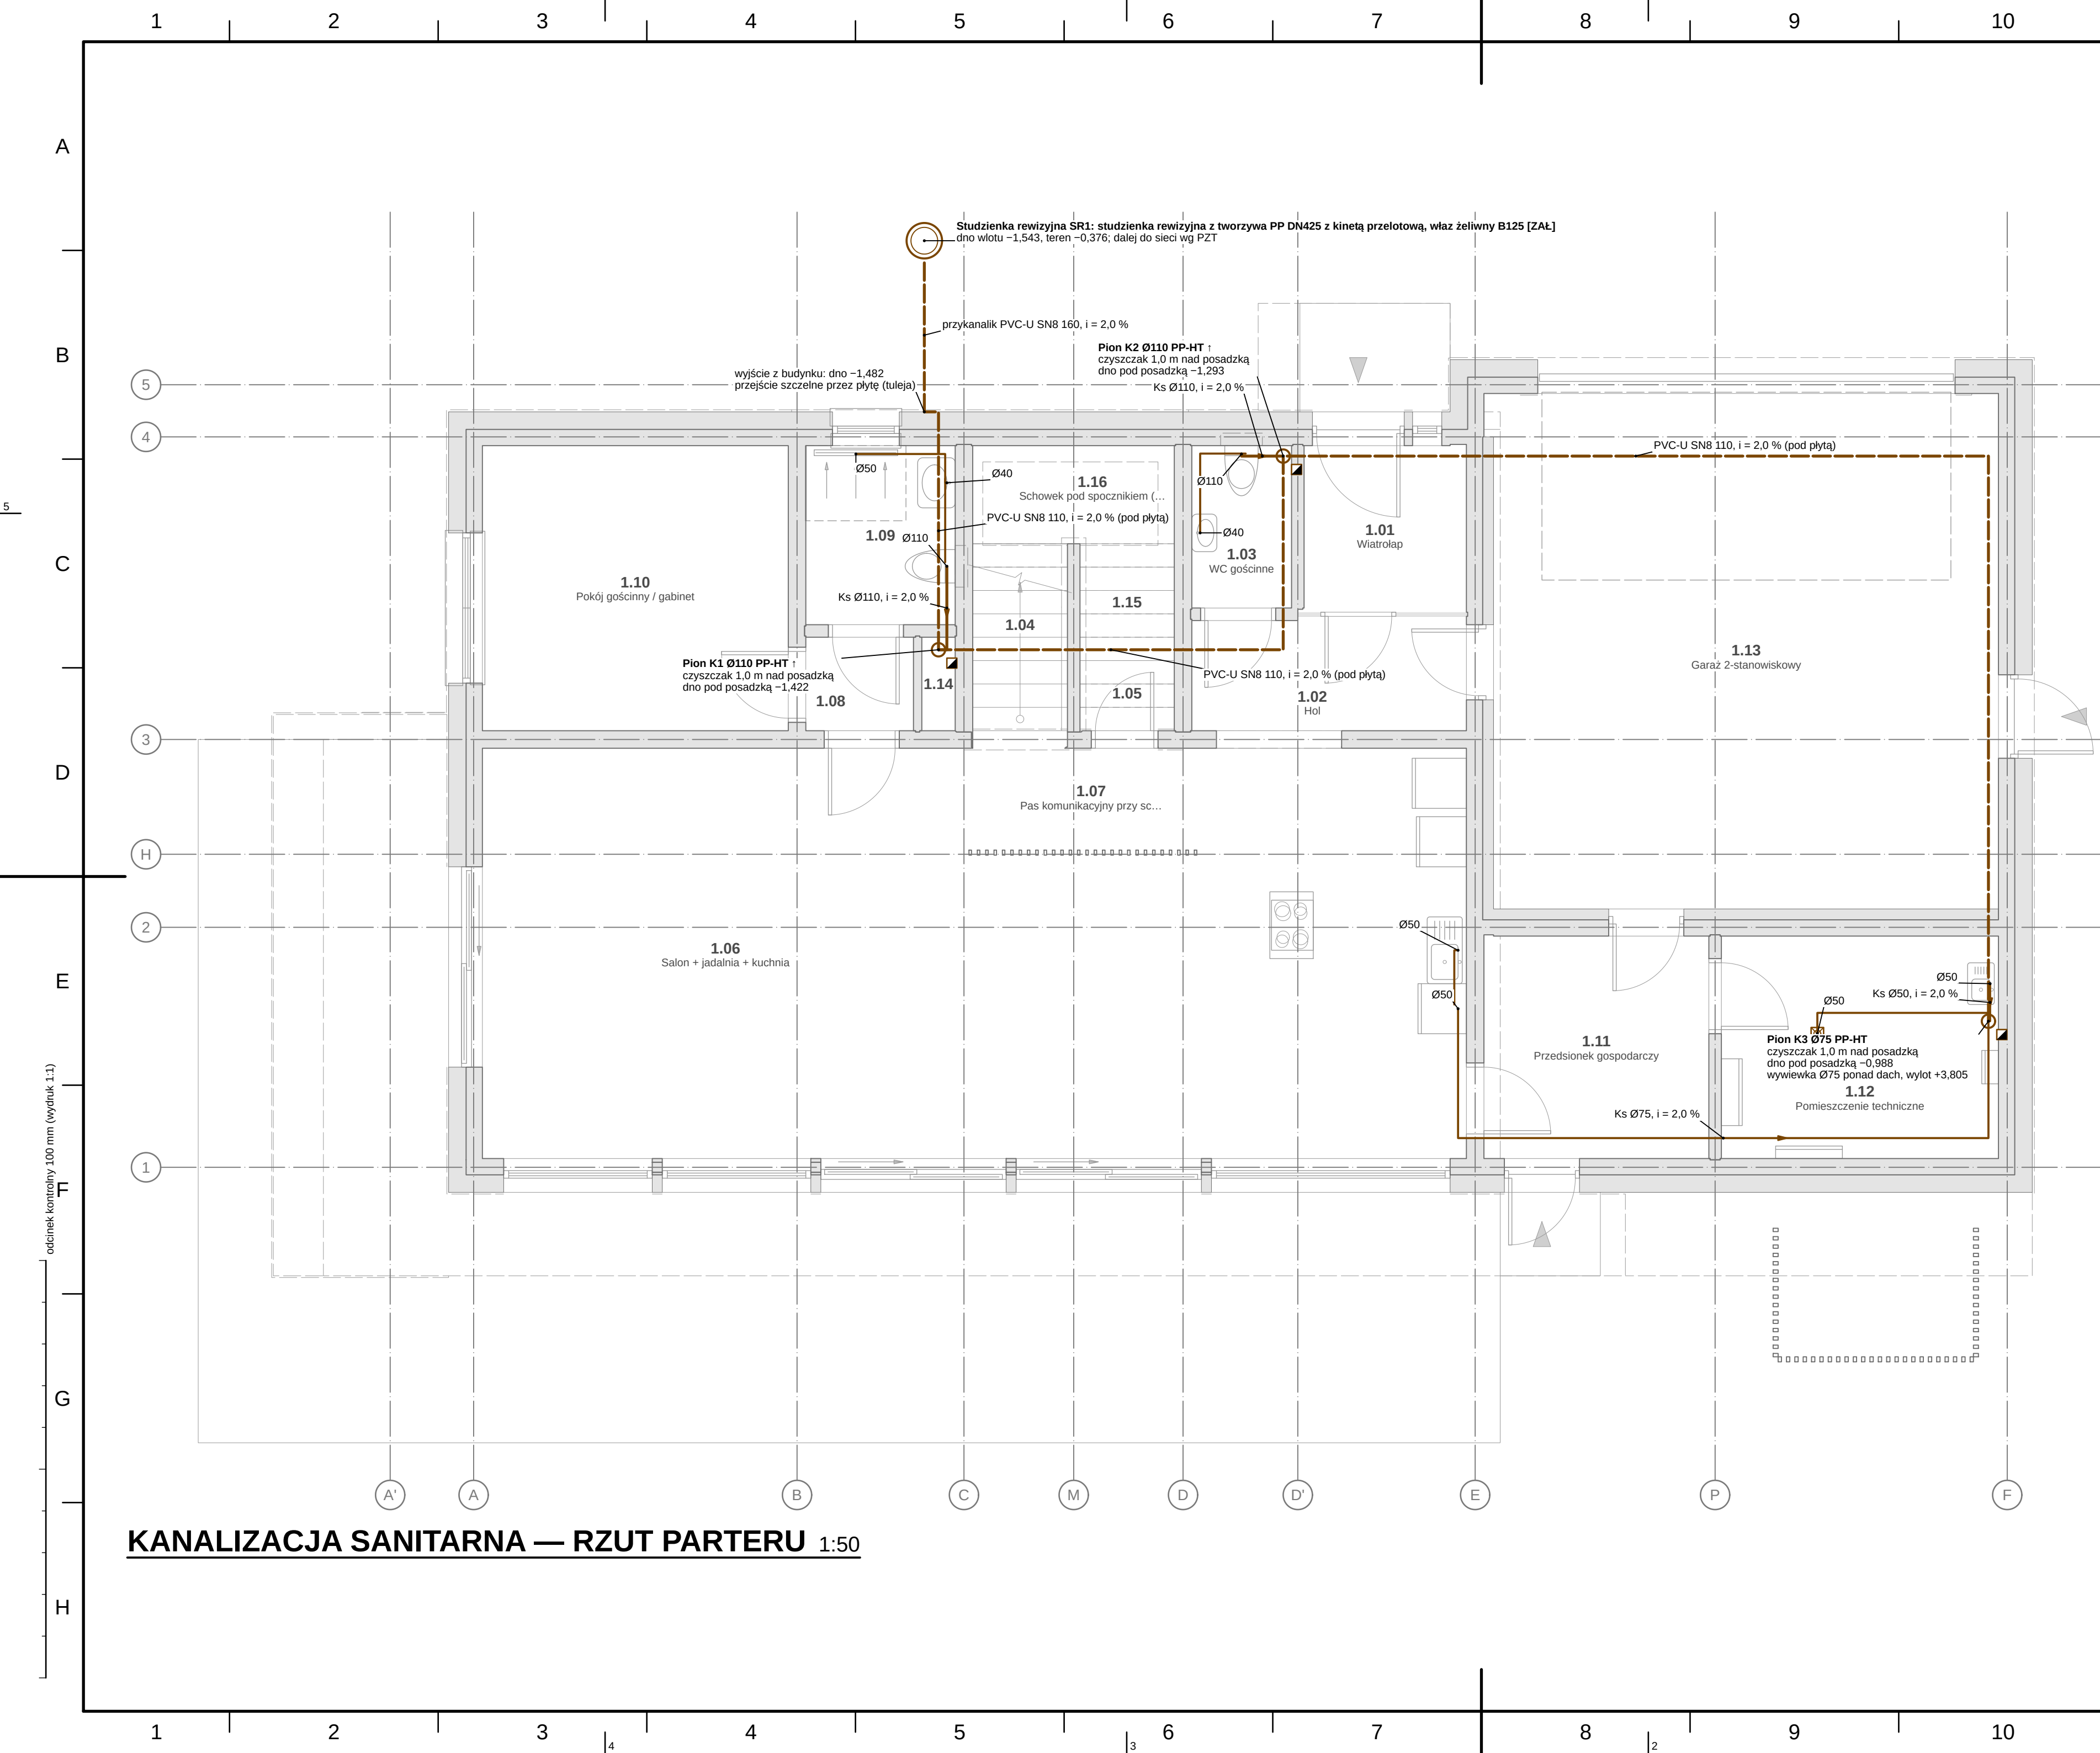


Oznaczenia instalacji sanitarnych — praktyka branżowa (PN-B-01410, PN-B-01411, PN-B-01430 — normy wycofane, bez następcy); armatura i urządzenia wg PN-EN ISO 10628-2 / PN-EN ISO 14617; rodzaj powietrza wg PN-EN 16798-3 (ODA, SUP, ETA, EHA). Obowiązuje legenda na arkuszu.

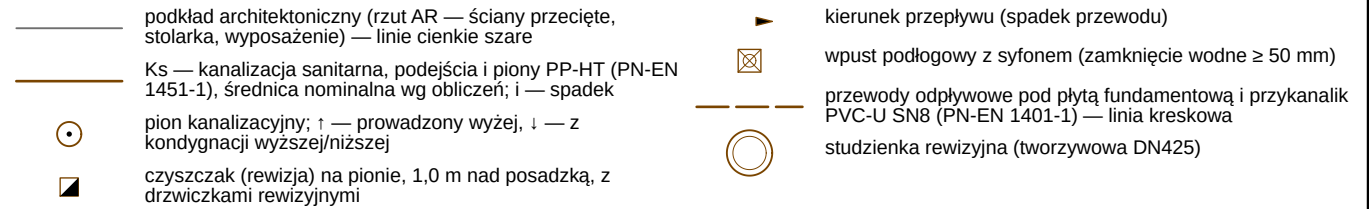

Odcinek	Opis	DN	L [m]	ΣDU	Q [l/s]	ι [%]
PZ_0.09	podęście zbiorcze w pom. 0.09 → pion K1	Ø110	3,43	3,1	2,00	2,0
PZ_1.05	podęście zbiorcze w pom. 1.05 → pion K1	Ø110	3,14	3,3	2,00	2,0
PZ_2.04	podęście zbiorcze w pom. 2.04 → pion K1	Ø110	3,14	3,1	2,00	2,0
PZ_0.03	podęście zbiorcze w pom. 0.03 → pion K2	Ø110	2,01	2,5	2,00	2,0
PZ_1.07	podęście zbiorcze w pom. 1.07 → pion K2	Ø110	3,21	3,1	2,00	2,0
PZ_1.08	podęście zbiorcze w pom. 1.08 → pion K2	Ø75	2,52	2,3	1,50	2,0
PZ_0.06	podęście zbiorcze w pom. 0.06 → pion K3	Ø75	7,10	1,6	0,80	2,0
PZ_0.12	podęście zbiorcze w pom. 0.12 → pion K3	Ø50	2,30	1,6	0,80	2,0
PION_K1	pion K1 (P0, P1, P2)	Ø110	7,90	9,5	2,00	—
PION_K2	pion K2 (P0, P1)	Ø110	4,75	7,9	2,00	—
PION_K3	pion K3 (P0)	Ø75	1,60	3,2	0,89	—
KOL1	przewód odpływowy pod posadzką: pion K3 → wł	Ø110	15,22	3,2	0,89	2,0
KOL2	przewód odpływowy pod posadzką: pion K2 → wł	Ø110	6,45	11,1	2,00	2,0
KOL3	przewód odpływowy pod posadzką: pion K1 → wy	Ø110	3,02	20,6	2,27	2,0
PRZ	przykanalik: budynek → studzienka rewizyjna	Ø160	3,05	20,6	2,27	2,0

1. Średnice przewodów w mm (d, z_{xs} – rury wielowarstwowe, Ø/DN – kanalizacja, kanały wentylacyjne), przekroje żył w mm², odległości i rzędne w mm; z₀+0.00 = 101.650 m n.p.m. (PL-EVRF2007-NH).
2. Rysunki instalacji na podkladzie rzutów architektury (PB-AR); podkład – linie cienkie szare (warstwy I-PDOKLAD*).
3. Kanalizacja sanitarna wg PN-EN 12056-1, -2 (system I), -5 i IT § 122-124; obliczenia: lamela obliczeniowa sanitarna kanalizacja (K = 0,5; ŚDU, Q_{ww}, napełnienia, wentylacja pionów).
4. Podęśzaki i piony: PP-PHT (PN-EN 1451-1) lub równoważne; pod płytą i przykanalik: PVC-U SN8 lity (PN-EN 1401-1). Spadki podejść ≥ 2 ‰, przewodów pod płytą 2 ‰ (≤ DN100).
5. Trasy podejść wyznaczono algorytmicznie (ortogonalnie, przy ścianach, do pionów w szachcie SI) – średnice i spadki z obliczeń; przebieg do weryfikacji na budowie.
6. Czyścaki na pionach w najniższej kondygnacji 1,0 m nad posadzką; rewizje w studziście SR1. Piony w szachcie izolowane akustycznie, przejścia przez stropy z opaskami/kolnierzami ppóz. wg klasy stropu.
7. Odpływ skroplin PC i zmywarki przez syfon; wpusty podłogowe z zamknięciem wodnym ≥ 50 mm.
8. ŚDU = 20,6 l/s, Q_{ww} = 2,27 l/s; przykanalik DN150 i=0.02.
9. Rysunek wygenerowany automatycznie z modelu modelu/budynk.yaml (wersja 1.0, 2026-09-25) – generatory lamela.wiews.

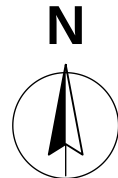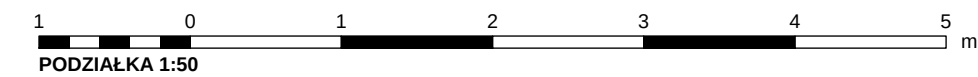

REW.	OPIS ZMIANY			DATA	
0	Wydanie — rysunek wygenerowany z modelu			2026-09-25	
PRACOWNIA PROJEKTOWA PRACOWNIA PROJEKTOWA — nazwa do uzupełnienia adres pracowni do uzupełnienia			STADIUM PT	BRANŻA INSTALACJE SANITARNE (IS)	
INWESTOR (do uzupełnienia)					
OBIEKT / NAZWA ZAMIERZENIA BUDOWLANEGO Budynek mieszkalny jednorodzinny wolnostojący „Dom LAMELA”					
ADRES / LOKALIZACJA (NR DZIAŁKI, OBRĘB, JEDN. EWIDENCYJNA) ul. Lipowa (fikcyjna), dz. nr ewid. 123/4, obręb 0005 Przykładowo, gm. Przykładowo (fikcyjna)				KAT. OBIEKTU I	
FUNKCJA		IMIĘ I NAZWISKO	SPECJALNOŚĆ, NR UPRAWNIEN	DATA	PODPIS
Projektant	[DO UZUPEŁNIENIA]	[DO UZUPEŁNIENIA]			
Projektant (wsp.)	[DO UZUPEŁNIENIA]	[DO UZUPEŁNIENIA]			
Sprawdzający	nie dotyczy (art. 20 ust. 3 pkt 2 PB)	—			
Opracował	[DO UZUPEŁNIENIA]	[DO UZUPEŁNIENIA]			
TYTUŁ RYSUNKU KANALIZACJA SANITARNA — RZUT PARTERU					
SKALA 1:50	FORMAT 710×420	DATA WYDANIA 2026-09-25	RODZAJ DOK. rzut instalacji	NR RYSUNKU PT-IS-03	ARKUSZ 3/11
				REW. 0	