

odcinek konteiny 100 mm (wydruk 1:1)

RZUT I PIĘTRA 1:50

ZESTAWIENIE POMIESZCZEŃ

Nr	Nazwa pomieszczenia	Posadzka	Kat.	Wys. [m]	Pow. [m²]
2.02	Pokój rodzinny / biblioteka (boks C)	Deska warstwowa dębowa 15 mm, klejona	podst.	2,77	28,36
2.01	Hol	Deska warstwowa dębowa 15 mm, klejona	naruchu	2,77	14,09
2.03	Pokój dziecka 1	Deska warstwowa dębowa 15 mm, klejona	podst.	2,77	13,19
2.04	Pokój dziecka 2	Deska warstwowa dębowa 15 mm, klejona	podst.	2,77	12,52
2.08	Pralnia z suszarnią	Płytki gresowe 60×120 na kleju C2TE \$1	pomoc.	2,77	6,64
2.05	Łazienka dzieci (wanna)	Płytki gresowe 60×120 na kleju C2TE \$1	pomoc.	2,77	5,50
2.07	WC z natryskiem	Płytki gresowe 60×120 na kleju C2TE \$1	pomoc.	2,77	4,08
2.06	Klatka schodowa	Deska warstwowa dębowa 15 mm, klejona	naruchu	2,77	0,49
2.09	Szacht instalacyjny SI		techn.	2,77	0,45
RAZEM powierzchnia netto					85,33
w tym użytkowa (podst. + pomoc.)					70,30

OZNACZENIA MATERIAŁÓW (PN-B-01030 + przyjęte)


	Wełna mineralna 035 (szkielet, docieplenia, ściana dom-garaż)		Rama boksu C: ruszt stalowy ocynkowany w okładzinie z blachy aluminiowej RAL 7016 (pusta w środku); Stal konstrukcyjna S355 (skłupy RK, rama boksu C); cynkowana ogniowo + malowana proszkowo RAL 7016 — zacczernienie
	Styropian grafitowy EPS 031 (ETICS, NRO w systemie) — zygzak „VVV”		Żelbet C25/30, B500SP (stropy, płyta fundamentowa, ściany) — 45° na przemiern ciągle i przerywane
	Bloczek wapniowo-piaskowy 12 cm, kl. 15 (ścianki działowe, licowy w klatce); Bloczek wapniowo-piaskowy (slikat) 18 cm, kl. 20, gr. 1, na zaprawie cienkowarstwowej — kratka ukośna 45°/135°		

OZNACZENIA LINII

- elementy nad płaszczyzną cięcia (obryszy płyt, wsporników, brył wyższych kondygnacji)
- elementy poniżej płaszczyzny cięcia (widok z góry)
- osie konstrukcyjne; linia punktowa z pogrubionymi końcami — ślad przekroju

OBJAŚNIENIA I UWAGI

- Wymiary w cm (mm w indeksie górnym, np. 24⁵ = 24,5 cm), rzędne w m względem ±0,000 = 101,650 m n.p.m. (PL-EVRF2007-NH).
- Rzuty: płaszczyzna cięcia +1,10 m nad posadzką kondygnacji. Linia kreskową — elementy nad płaszczyzną cięcia (obryszy płyt i wsporników, brył wyższych kondygnacji, otwory w stropie nad, belki); linia cieniłą — elementy poniżej (widok).
- Otwory: licznik — szerokość, mianownik — wysokość w świetle muru, w nawiasie wysokość parapetu; symbol stolarki wg zestawienia stolarki.
- Numeracja pomieszczeń wg PN-B-01025 / PN-EN ISO 4157-2: <nr kondygnacji (parter = 1)>. <nr>; identyfikator w modelu: <kond>.<nr> (parter = 0).
- Drzwi: strona otwierania (lewe/prawe) wg modelu — patrząc od strony, w którą otwiera się skrzydło.
- Rysunek wygenerowany automatycznie z modelu /home/user/aihouse/model/budynek.yamł (wersja 1.0, 2026-09-25) — generatory lamela.views.

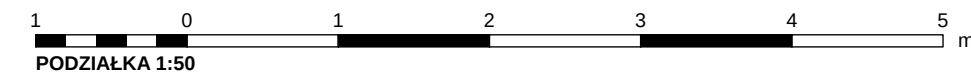

REW.	OPIS ZMIANY			DATA		
0	Wydanie — rysunek wygenerowany z modelu			2026-09-25		
PRACOWNIA PROJEKTOWA PRACOWNIA PROJEKTOWA — nazwa do uzupełnienia adres pracowni do uzupełnienia			STADIUM PB	BRANŻA ARCHITEKTURA (AR)		
INWESTOR (do uzupełnienia)						
OBIEKT / NAZWA ZAMIERZENIA BUDOWLANEGO						
Budynek mieszkalny jednorodzinny wolnostojący „Dom LAMELA”						
ADRES / LOKALIZACJA (NR DZIAŁKI, OBRĘB, JEDN. EWIDENCYJNA) ul. Lipowa (fikcyjna), dz. nr ewid. 123/4, obręb 0005 Przykładowo, gm. Przykładowo (fikcyjna)					KAT. OBIEKTU I	
FUNKCJA	IMIĘ I NAZWISKO		SPECJALNOŚĆ, NR UPRAWNIENI		DATA	PODPIS
Projektant						
Projektant (wsp.)						
Sprawdzający						
Opracował						
TYTUŁ RYSUNKU						
RZUT I PIĘTRA						
SKALA 1:50	FORMAT A3×3	DATA WYDANIA 2026-09-25	RODZAJ DOK. rzut	NR RYSUNKU PB-AR-02	ARKUSZ 2/10	REW. 0