


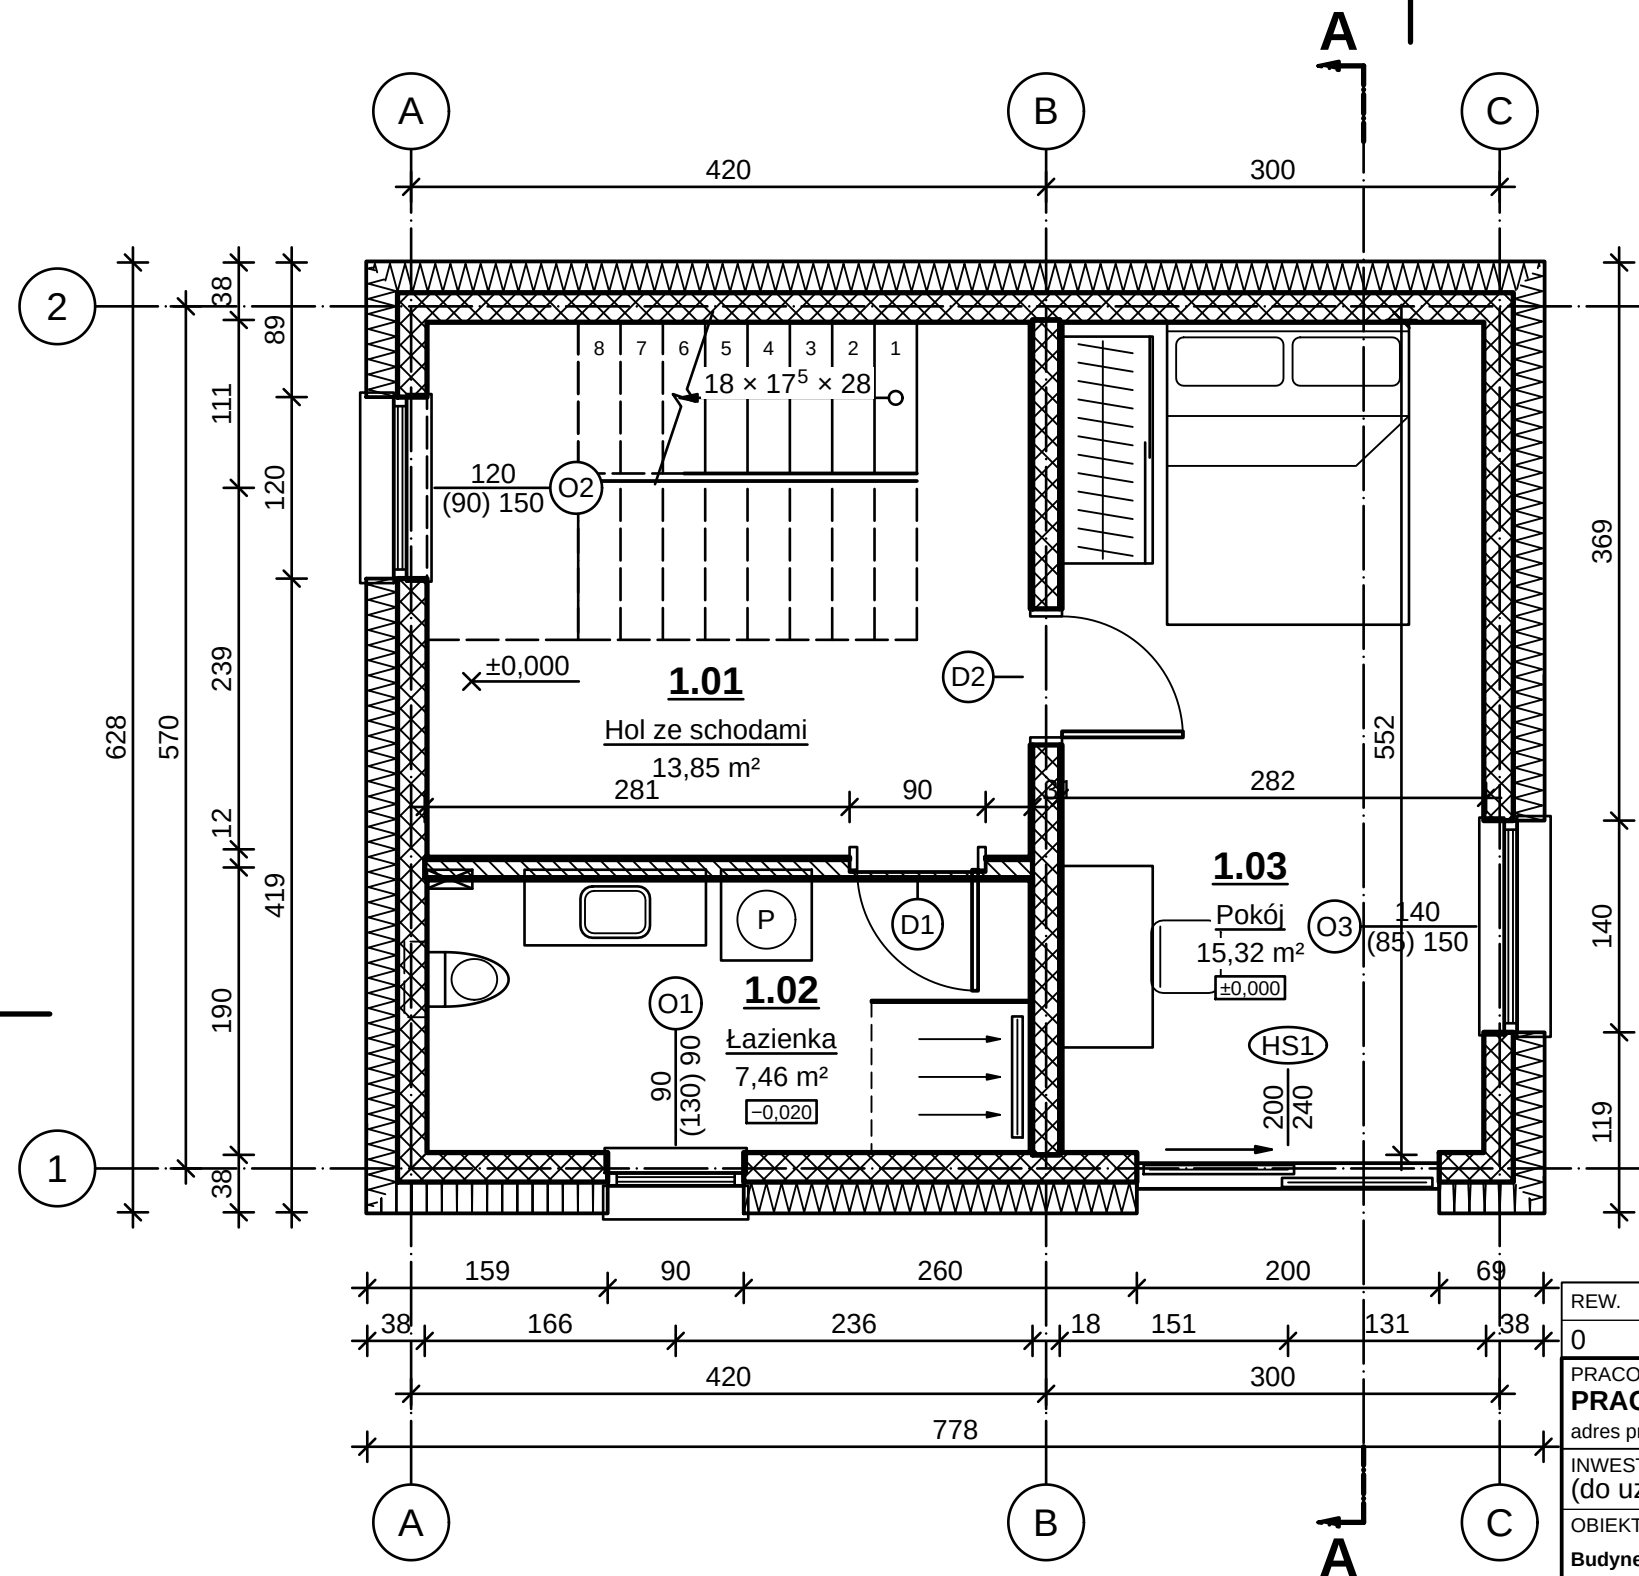

RZUT PARTERU — FRAGMENT 1:50

ZESTAWIENIE POMIESZCZEŃ

Nr	Nazwa pomieszczenia	Posadzka	Pow. [m²]
1.01	Hol ze schodami	gres	13,85
1.02	Łazienka	gres	7,46
1.03	Pokój	deska	15,32
RAZEM			36,62

ZESTAWIENIE OTWORÓW (w świetle muru)


Symbol	Szer. [cm]	Wys. [cm]	Parapet [cm]
O1	90	90	130
HS1	200	240	0
O2	120	150	90
O3	140	150	85
D1	90	205	—
D2	90	205	—

OZNACZENIA MATERIAŁÓW

	Mur z bloczków wapienno-piaskowych (silikatowych) — kratka ukośna 45°/135°		Izolacja termiczna twarda (EPS) — zygzak „VVV”
	Mur z cegieł i pustaków ceramicznych — 45° ciągłe		Tynk, zaprawa — kropki nieregularne

OBJAŚNIENIA I UWAGI

- Wymiary w cm (mm w indeksie górnym, np. 24⁵ = 24,5 cm), rzędne w m. ±0,000 = posadzka parteru = 101,650 m n.p.m. (PL-EVRF2007-NH).
- Otwory: licznik — szerokość, mianownik — wysokość w świetle muru, w nawiasie wysokość parapetu.
- Oznaczenia mur silikatowy i EPS/wełna — przyjęte (brak w PN-B-01030), objaśnione w legendzie.
- Rysunek testowy silnika — dane nie stanowią projektu.

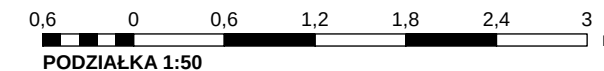

REW.		OPIS ZMIANY		DATA		
0		Wydanie do weryfikacji silnika rysunkowego			2026-09-25	
PRACOWNIA PROJEKTOWA PRACOWNIA PROJEKTOWA — nazwa do uzupełnienia adres pracowni do uzupełnienia				STADIUM PB	BRANŻA ARCHITEKTURA (AR)	
INWESTOR (do uzupełnienia)						
OBIEKT / NAZWA ZAMIERZENIA BUDOWLANEGO Budynek mieszkalny jednorodzinny „Dom LAMELA” — PRÓBA SILNIKA RYSUNKOWEGO (rysunek testowy)						
ADRES / LOKALIZACJA (NR DZIAŁKI, OBRĘB, JEDN. EWIDENCYJNA) dz. nr ewid. 123/4, obręb 0005 Przykładowo, jedn. ewid. Przykładowo (dane fikcyjne)					KAT. OBIEKTU I	
FUNKCJA	IMIĘ I NAZWISKO		SPECJALNOŚĆ, NR UPRAWNIEN		DATA	PODPIS
Projektant						
Projektant (wsp.)						
Sprawdzający						
Opracował						
TYTUŁ RYSUNKU RZUT PRÓBNY — FRAGMENT PARTERU						
SKALA 1:50	FORMAT A3	DATA WYDANIA 2026-09-25	RODZAJ DOK. rzut	NR RYSUNKU DEMO-01	ARKUSZ 1/3	REW. 0